

1

2

3

4

5

6

7

8

A

B

C

D

E

F

Ä-Buchst.
Rev. Ltr.

Datum
Date

Änd.Nr.
Rev.No.

Blattanzahl
No. of sheets

Änderung
Revision

Geänderte Seiten
Modified Pages

-

06.09.2011

77313

162

war kZ

1-162

a

13.11.2014

116665

162

Verkabelung geändert

1-4,16,23,30,37,44,51,56,61,66,71,76,81,112-114,134-137,144-149,151-156,158-161

b

15.01.2018

Freigegeben

162

Verkabelung geändert

18,25-26,32,39-40,46-47,53,58,63-64,68,73-74,78-79,83,90,97-98,114-115,126,132,136-137,148,155-156,160-161

c

26.02.2018

Freigegeben

162

Rahmentexte bericht.

1-162

Keine Änderung ohne Zustimmung der
Federführenden Konstruktion.
Any alterations are subject to the
approval of the design department.

© MTU Friedrichshafen GmbH
Schutzvermerk DIN 34 beachten !
Refer to protection notice DIN 34 !

CAD

Datum

Name

Bearb.

21.02.2018

SAUTER

Gepr.

21.02.2018

BOLL

Norm.

21.02.2018

SAUTER

Buchst.

Aenderung / Revision

Auftrags-Nr.

Datum/Date

Name

Abt. TEA

mtu

MTU Friedrichshafen GmbH

Benennung/Title

SCHEMA VERKABELUNG
ANLAGENAUTOMATION
WIRING DIAGRAM
PLANT AUTOMATION

NULLBLATT
ACTIVE SHEET RECORD

Auftrag/
Projekt

BLUE-VIS

Zeichnungs-Nr.
Drawing No.

BZ00E50000064

Blatt
Sheet

0

Referenz-Nr./Reference-No.

RUPLAN

1

2

3

4

5

6

7

8

DIN A3

A	Blatt Sheet	Benennungen Titles			Blatt Sheet	Benennungen Titles			
		1	2	3		4	5	6	7
B	1	INHALTSVERZEICHNIS TABLE OF CONTENTS			26	ZF GETRIEBE, OHNE WENDETEIL, TYP A(GR.1), WELLENDREHZAH ZF GEARBOX, WITHOUT REVERSING, TYPE A(GR.1), SHAFT SPEED			
	2	INHALTSVERZEICHNIS TABLE OF CONTENTS			27	ZF GETRIEBE, MIT WENDETEIL, TYP A(GR.2), HINWEISE ZF GEARBOX, WITH REVERSING, TYPE A(GR.2), INSTRUCTIONS			
C	3	INHALTSVERZEICHNIS TABLE OF CONTENTS			28	ZF GETRIEBE, MIT WENDETEIL, TYP A(GR.2), GRUNDUMFANG ZF GEARBOX, WITH REVERSING, TYPE A(GR.2), BASIC SCOPE			
	4	INHALTSVERZEICHNIS TABLE OF CONTENTS			29	ZF GETRIEBE, MIT WENDETEIL, TYP A(GR.2), GRUNDUMFANG ZF GEARBOX, WITH REVERSING, TYPE A(GR.2), BASIC SCOPE			
D	5	HINWEISE ALLGEMEIN INSTRUCTIONS GENERAL			30	ZF GETRIEBE, MIT WENDETEIL, TYP A(GR.2), ERWEIT. UMFANG ZF GEARBOX, WITH REVERSING, TYPE A(GR.2), EXTENTED SCOPE			
	6	ABGASKLAPPENSTEUERUNG: STROMVERSORGUNG 24VDC EXHAUST FLAP CONTROL: POWER SUPPLY 24VDC			31	ZF GETRIEBE, MIT WENDETEIL, TYP A(GR.2), ERWEIT. UMFANG ZF GEARBOX, WITH REVERSING, TYPE A(GR.2), EXTENTED SCOPE			
E	7	ABGASKLAPPENSTEUERUNG: ANSTEUERUNG EXHAUST FLAP CONTROL: FLAP CONTROL			32	ZF GETRIEBE, MIT WENDETEIL, TYP A(GR.2), ERWEIT. UMFANG ZF GEARBOX, WITH REVERSING, TYPE A(GR.2), EXTENTED SCOPE			
	8	ABGASKLAPPENSTEUERUNG: RÜCKMELDUNGEN EXHAUST FLAP CONTROL: FEEDBACKS			33	ZF GETRIEBE, MIT WENDETEIL, TYP A(GR.2), WELLENDREHZAH ZF GEARBOX, WITH REVERSING, TYPE A(GR.2), SHAFT SPEED			
F	9	ABGASKLAPPENSTEUERUNG: VARIANTE FCU AN GCU ANGESCHLOSSEN EXHAUST FLAP CONTROL: VERSION FCU CONNECTED TO GCU			34	ZF GETRIEBE, OHNE WENDETEIL, TYP A(GR.2), HINWEISE ZF GEARBOX, WITHOUT REVERSING, TYPE A(GR.2), INSTRUCTIONS			
	10	ABGASKLAPPENSTEUERUNG: VARIANTE FCU AN LOP ANGESCHLOSSEN EXHAUST FLAP CONTROL: VERSION FCU CONNECTED TO LOP			35	ZF GETRIEBE, OHNE WENDETEIL, TYP A(GR.2), GRUNDUMFANG ZF GEARBOX, WITHOUT REVERSING, TYPE A(GR.2), BASIC SCOPE			
G	11	ZF GETRIEBE, HINWEISE GETRIEBESCHNITTSTELLEN ZF GEARBOX, INSTRUCTIONS GEARBOX INTERFACES			36	ZF GETRIEBE, OHNE WENDETEIL, TYP A(GR.2), GRUNDUMFANG ZF GEARBOX, WITHOUT REVERSING, TYPE A(GR.2), BASIC SCOPE			
	12	ZF GETRIEBE, HINWEISE GETRIEBESCHNITTSTELLEN ZF GEARBOX, INSTRUCTIONS GEARBOX INTERFACES			37	ZF GETRIEBE, OHNE WENDETEIL, TYP A(GR.2), ERWEIT. UMFANG ZF GEARBOX, WITHOUT REVERSING, TYPE A(GR.2), EXTENTED SCOPE			
H	13	ZF GETRIEBE, MIT WENDETEIL, TYP A(GR.1), HINWEISE ZF GEARBOX, WITH REVERSING, TYPE A(GR.1), INSTRUCTIONS			38	ZF GETRIEBE, OHNE WENDETEIL, TYP A(GR.2), ERWEIT. UMFANG ZF GEARBOX, WITHOUT REVERSING, TYPE A(GR.2), EXTENTED SCOPE			
	14	ZF GETRIEBE, MIT WENDETEIL, TYP A(GR.1), GRUNDUMFANG ZF GEARBOX, WITH REVERSING, TYPE A(GR.1), BASIC SCOPE			39	ZF GETRIEBE, OHNE WENDETEIL, TYP A(GR.2), ERWEIT. UMFANG ZF GEARBOX, WITHOUT REVERSING, TYPE A(GR.2), EXTENTED SCOPE			
I	15	ZF GETRIEBE, MIT WENDETEIL, TYP A(GR.1), GRUNDUMFANG ZF GEARBOX, WITH REVERSING, TYPE A(GR.1), BASIC SCOPE			40	ZF GETRIEBE, OHNE WENDETEIL, TYP A(GR.2), WELLENDREHZAH ZF GEARBOX, WITHOUT REVERSING, TYPE A(GR.2), SHAFT SPEED			
	16	ZF GETRIEBE, MIT WENDETEIL, TYP A(GR.1), ERWEIT. UMFANG ZF GEARBOX, WITH REVERSING, TYPE A(GR.1), EXTENTED SCOPE			41	ZF GETRIEBE, OHNE WENDETEIL, TYP A(GR.3), HINWEISE ZF GEARBOX, WITHOUT REVERSING, TYPE A(GR.3), INSTRUCTIONS			
J	17	ZF GETRIEBE, MIT WENDETEIL, TYP A(GR.1), ERWEIT. UMFANG ZF GEARBOX, WITH REVERSING, TYPE A(GR.1), EXTENTED SCOPE			42	ZF GETRIEBE, OHNE WENDETEIL, TYP A(GR.3), GRUNDUMFANG ZF GEARBOX, WITHOUT REVERSING, TYPE A(GR.3), BASIC SCOPE			
	18	ZF GETRIEBE, MIT WENDETEIL, TYP A(GR.1), ERWEIT. UMFANG ZF GEARBOX, WITH REVERSING, TYPE A(GR.1), EXTENTED SCOPE			43	ZF GETRIEBE, OHNE WENDETEIL, TYP A(GR.3), GRUNDUMFANG ZF GEARBOX, WITHOUT REVERSING, TYPE A(GR.3), BASIC SCOPE			
K	19	ZF GETRIEBE, MIT WENDETEIL, TYP A(GR.1), WELLENDREHZAH ZF GEARBOX, WITH REVERSING, TYPE A(GR.1), SHAFT SPEED			44	ZF GETRIEBE, OHNE WENDETEIL, TYP A(GR.3), ERWEIT. UMFANG ZF GEARBOX, WITHOUT REVERSING, TYPE A(GR.3), EXTENTED SCOPE			
	20	ZF GETRIEBE, OHNE WENDETEIL, TYP A(GR.1), HINWEISE ZF GEARBOX, WITHOUT REVERSING, TYPE A(GR.1), INSTRUCTIONS			45	ZF GETRIEBE, OHNE WENDETEIL, TYP A(GR.3), ERWEIT. UMFANG ZF GEARBOX, WITHOUT REVERSING, TYPE A(GR.3), EXTENTED SCOPE			
L	21	ZF GETRIEBE, OHNE WENDETEIL, TYP A(GR.1), GRUNDUMFANG ZF GEARBOX, WITHOUT REVERSING, TYPE A(GR.1), BASIC SCOPE			46	ZF GETRIEBE, OHNE WENDETEIL, TYP A(GR.3), ERWEIT. UMFANG ZF GEARBOX, WITHOUT REVERSING, TYPE A(GR.3), EXTENTED SCOPE			
	22	ZF GETRIEBE, OHNE WENDETEIL, TYP A(GR.1), GRUNDUMFANG ZF GEARBOX, WITHOUT REVERSING, TYPE A(GR.1), BASIC SCOPE			47	ZF GETRIEBE, OHNE WENDETEIL, TYP A(GR.3), WELLENDREHZAH ZF GEARBOX, WITHOUT REVERSING, TYPE A(GR.3), SHAFT SPEED			
M	23	ZF GETRIEBE, OHNE WENDETEIL, TYP A(GR.1), ERWEIT. UMFANG ZF GEARBOX, WITHOUT REVERSING, TYPE A(GR.1), EXTENTED SCOPE			48	ZF GETRIEBE, MIT WENDETEIL, TYP A(GR.4), HINWEISE ZF GEARBOX, WITH REVERSING, TYPE A(GR.4), INSTRUCTIONS			
	24	ZF GETRIEBE, OHNE WENDETEIL, TYP A(GR.1), ERWEIT. UMFANG ZF GEARBOX, WITHOUT REVERSING, TYPE A(GR.1), EXTENTED SCOPE			49	ZF GETRIEBE, MIT WENDETEIL, TYP A(GR.4), GRUNDUMFANG ZF GEARBOX, WITH REVERSING, TYPE A(GR.4), BASIC SCOPE			
N	25	ZF GETRIEBE, OHNE WENDETEIL, TYP A(GR.1), ERWEIT. UMFANG ZF GEARBOX, WITHOUT REVERSING, TYPE A(GR.1), EXTENTED SCOPE			50	ZF GETRIEBE, MIT WENDETEIL, TYP A(GR.4), GRUNDUMFANG ZF GEARBOX, WITH REVERSING, TYPE A(GR.4), BASIC SCOPE			
© MTU Friedrichshafen GmbH Schutzvermerk DIN 34 beachten! Refer to protection notice DIN 34!									
Keine Änderung ohne Zustimmung der federführenden Konstruktion. Any alterations are subject to the approval of the design department.									
013R001F									
RUPLAN					DIN A3				

EMPFOHLENE SCHIFFSKABEL

=21.X	PLANT	ENGINE PLANT
X		ENGINE X, ENGINE ROOM
=31.X	PLANT	MAIN POWER SUPPLY SYSTEM
X		ENGINE X
+A001	LOCATION	LOCAL OPERATING PANEL LOP11
+A002	LOCATION	GEAR CONTROL UNIT GCU3 OR GCU6
+A005	LOCATION	ENGINE INTERFACE MODULE EIM
+A006	LOCATION	PRIMING PUMP CONTROL PPC
+A008	LOCATION	EXHAUST FLAP CONTROL FCU2
+A012	LOCATION	SHAFT MONITORING UNIT SMU1
+A020	LOCATION	PROPULSION CONTROL AND MONITORING PCMU
+A025	LOCATION	TROLLING CONTROL SYSTEM (YARD)
+A029	LOCATION	TROLLING DEVICE: ZF AUTOTROLL (3 VERSIONS) 1. ZF AUTOTROLL MTCU/EST-159 ... (IN CONJUNCTION WITH ... SUPERSHIFT-E ACTUATION) 2. ZF AUTOTROLL MTCU/EST-59 3. ZF AUTOTROLL TWIN DISC E-TROLL OR E-TROLL ECO50 REINTJES G-ADS
+G002	LOCATION	MAIN AND EMERG. POWER SUPPLY 24VDC (YARD)
+G006	LOCATION	POWER SUPPLY AC (YARD)
+X020	LOCATION	GEARBOX TERMINAL BOX GTB
-M002	DEVICE	PRIMING PUMP
-G002	DEVICE	MAIN POWER SUPPLY 24VDC (YARD)
-F007	DEVICE	FUSE (YARD)
-F015	DEVICE	FUSE (YARD)
-F016	DEVICE	FUSE (YARD)
-X015	DEVICE	GEARBOX PLUG CONNECTOR GPC
-X020	DEVICE	GEARBOX PLUG CONNECTOR GPC
-X027	DEVICE	GEARBOX PLUG CONNECTOR GPC
-X028	DEVICE	GEARBOX PLUG CONNECTOR GPC
-X055	DEVICE	GEARBOX PLUG CONNECTOR GPC

RECOMMENDED SHIP CABLES



ADERKENNZEICHNUNG VON SCHIFFSKABEL

WIRE IDENTIFICATION OF SHIP'S CABLES

THE INDIVIDUAL WIRES OF THE SHIP'S CABLES SHOWN ARE CONSECUTIVELY NUMBERED FROM 1 TO n. IF SHIP'S CABLES WITH DIFFERING WIRE IDENTIFICATIONS ARE USED (E.G. COLORED MARKINGS), THE WIRES MUST BE CONNECTED ANALOGOUSLY.

THE INTERFACES AT THE MONITORING
AND CONTROL SYSTEMS (LOP, LOS, PIM4, ...) ARE SHOWN BY SYMBOLS.


EXAMPLE:

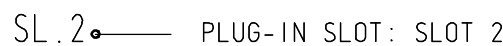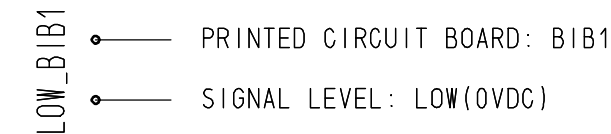

RUPLAN	1	2	3	4	5	6	7	8	DIN A3
--------	---	---	---	---	---	---	---	---	--------

Keine Änderung ohne Zustimmung der
federführenden Konstruktion.
Any alterations are subject to the
approval of the design department.

© MTU Friedrichshafen GmbH
Schutzvermerk DIN 34 beachten !
Refer to protection notice DIN 34 !

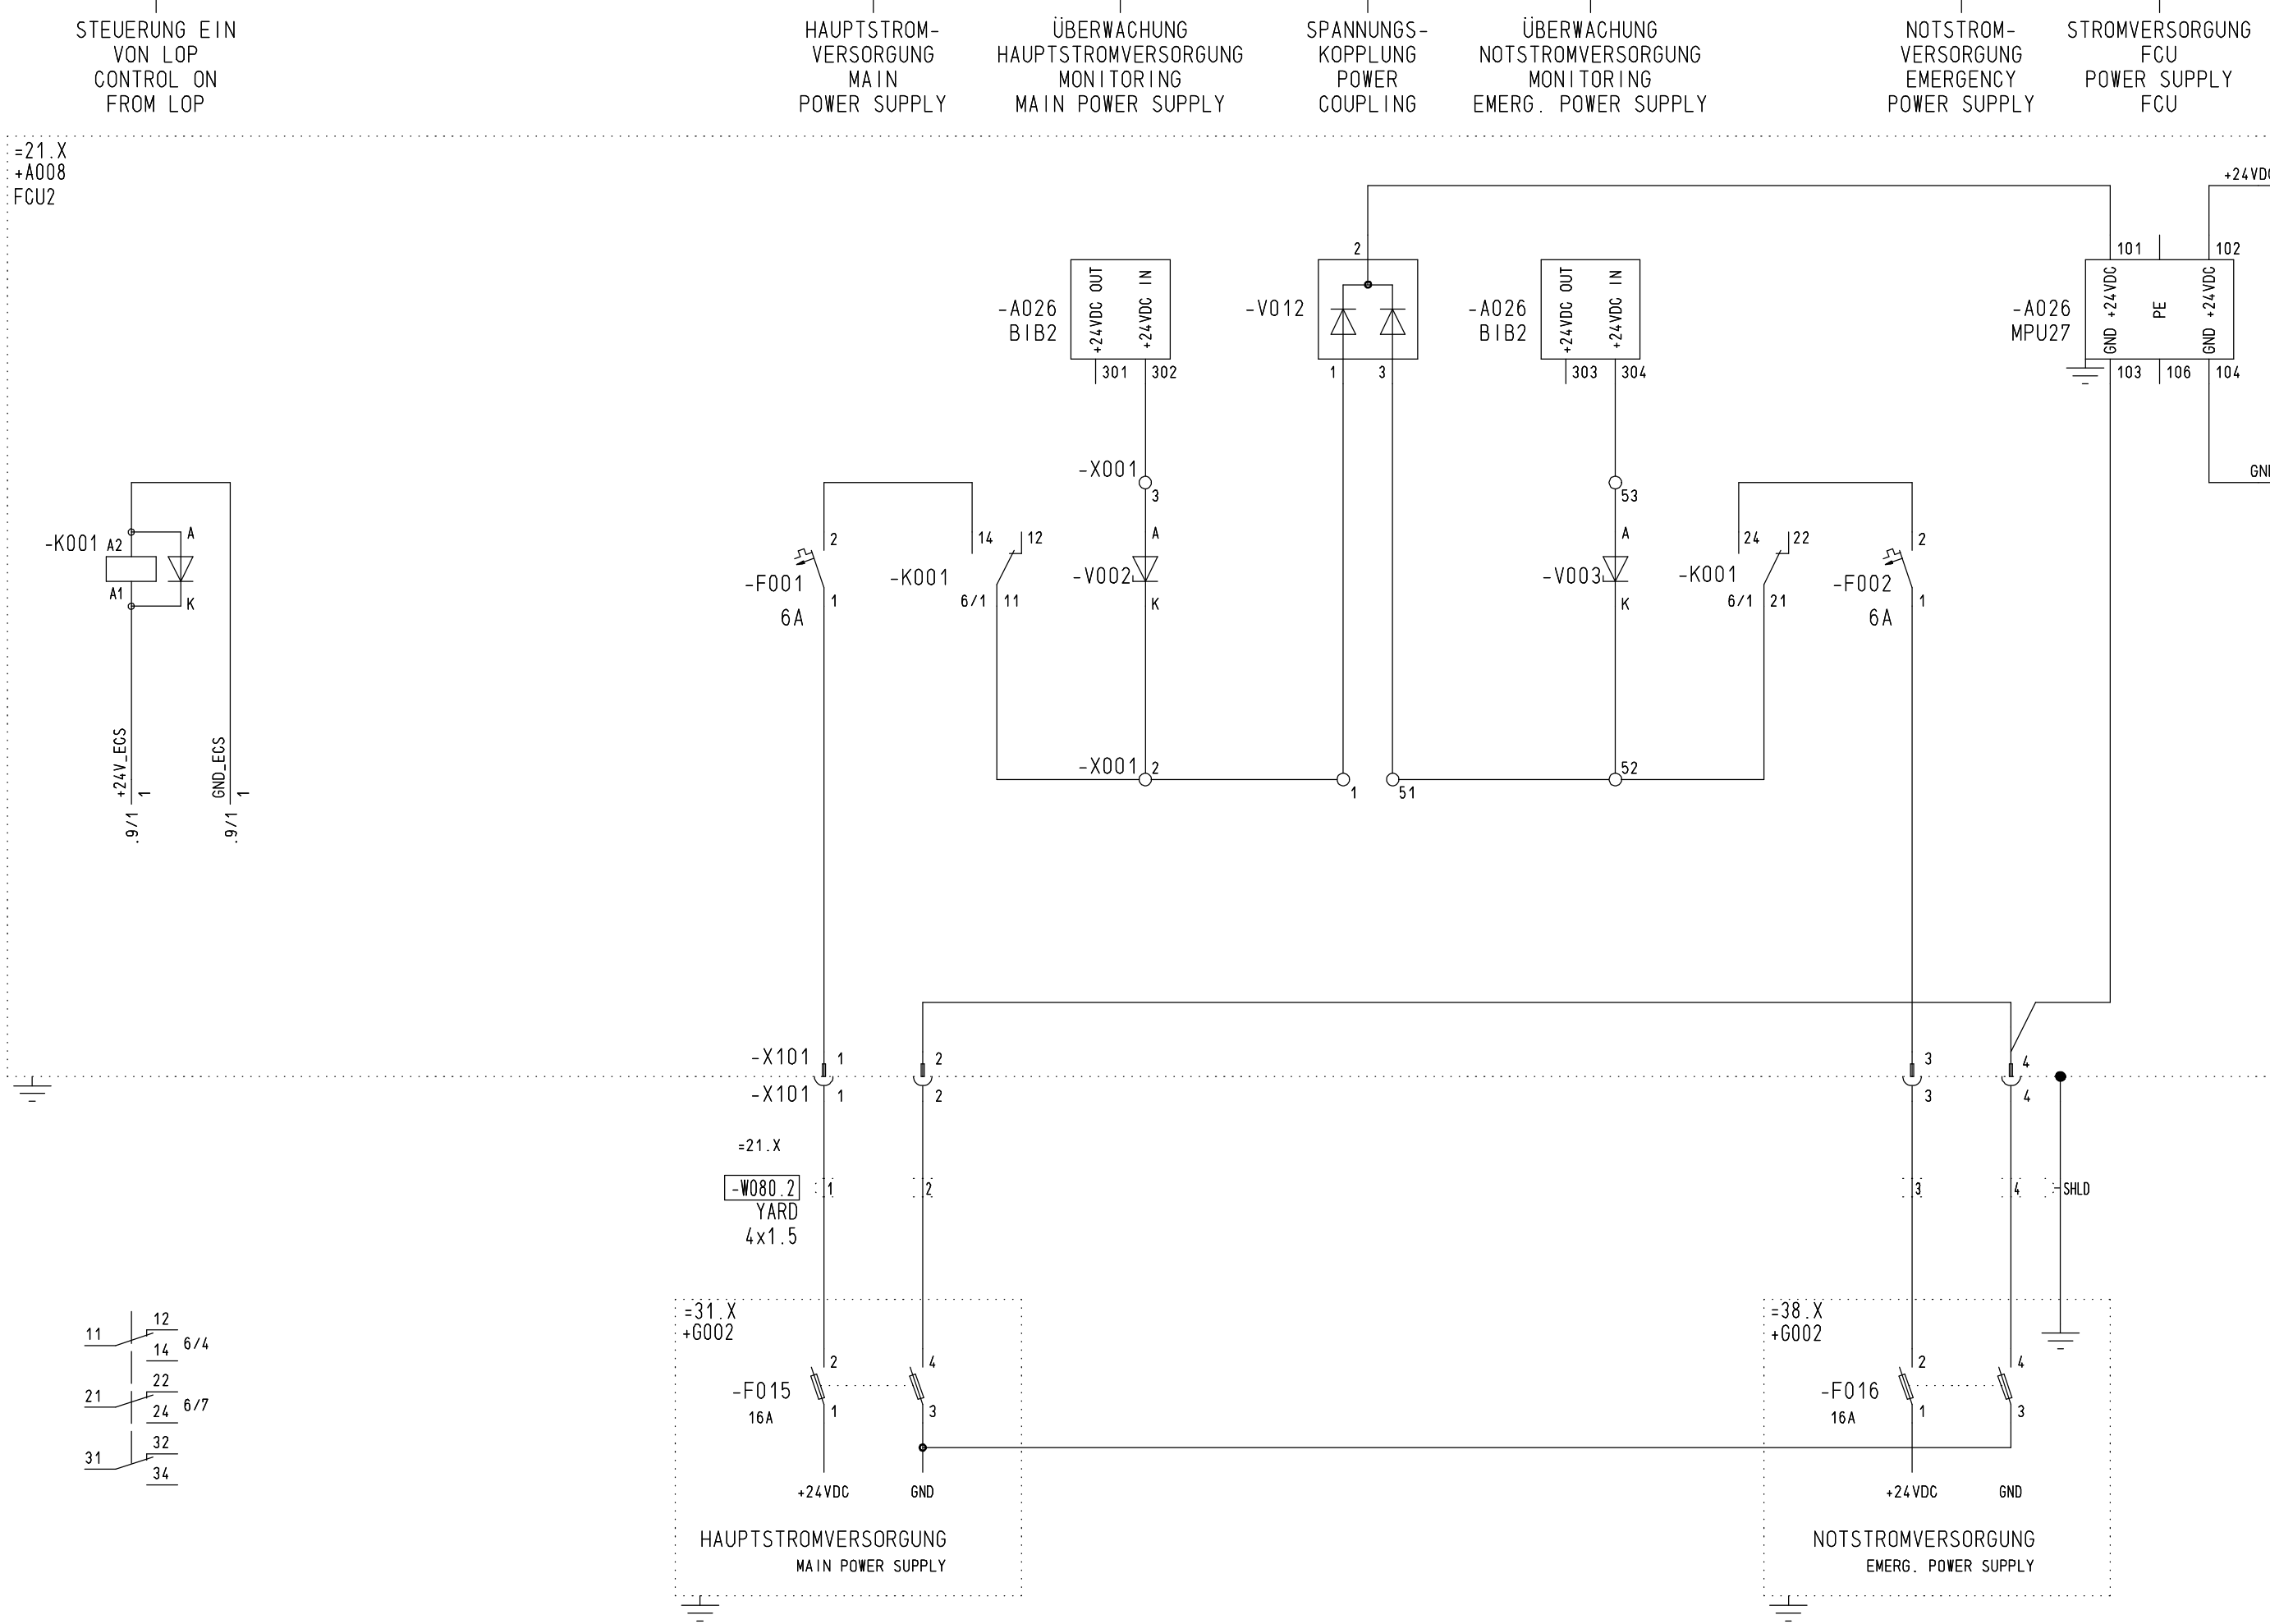

					CAD	Datum	Name	 MTU Friedrichshafen GmbH	Benennung/Title SCHEMA VERKABELUNG ANLAGENAUTOMATION WIRING DIAGRAM PLANT AUTOMATION	ABGASKLAPPENSTEUERUNG: STROMVERSORGUNG 24VDC EXHAUST FLAP CONTROL: POWER SUPPLY 24VDC					
					Bearb.	21.02.2018	SAUTER								
					Gepr.	21.02.2018	BOLL								
c	Rahmentexte bericht.	Freigegeb.	26.02.2018	Boll	Norm.	21.02.2018	SAUTER								
Buchst.	Aenderung / Revision	Auftrags-Nr.	Datum/Date	Name	Abt. TEA					Auftrag/ Projekt	BLUE-VIS	Zeichnungs-Nr. Drawing No.	BZ00E50000064	Blatt Sheet	6
										Referenz-Nr./Reference-No.		-----			

ABGASKLAPPE UNTER WASSER
SCHLIESSEN
EXHAUST FLAP UNDER WATER
CLOSE

-A026
BOB1

213	212	211
-----	-----	-----

61

=21.X
-W081.4
YARD
2x1.5

-W081.4
YARD
2x1.5

-Y071.2

-Y071.2

24VDC/max.2A


MTU Friedrichshafen GmbH


Referenz-Nr./Reference-No.	-----	-----
----------------------------	-------	-------

DIN A3

MTU Friedrichshafen GmbH
Schutzvermerk DIN 34 beachten !
Refer to protection notice DIN 34 !

RUPLAN

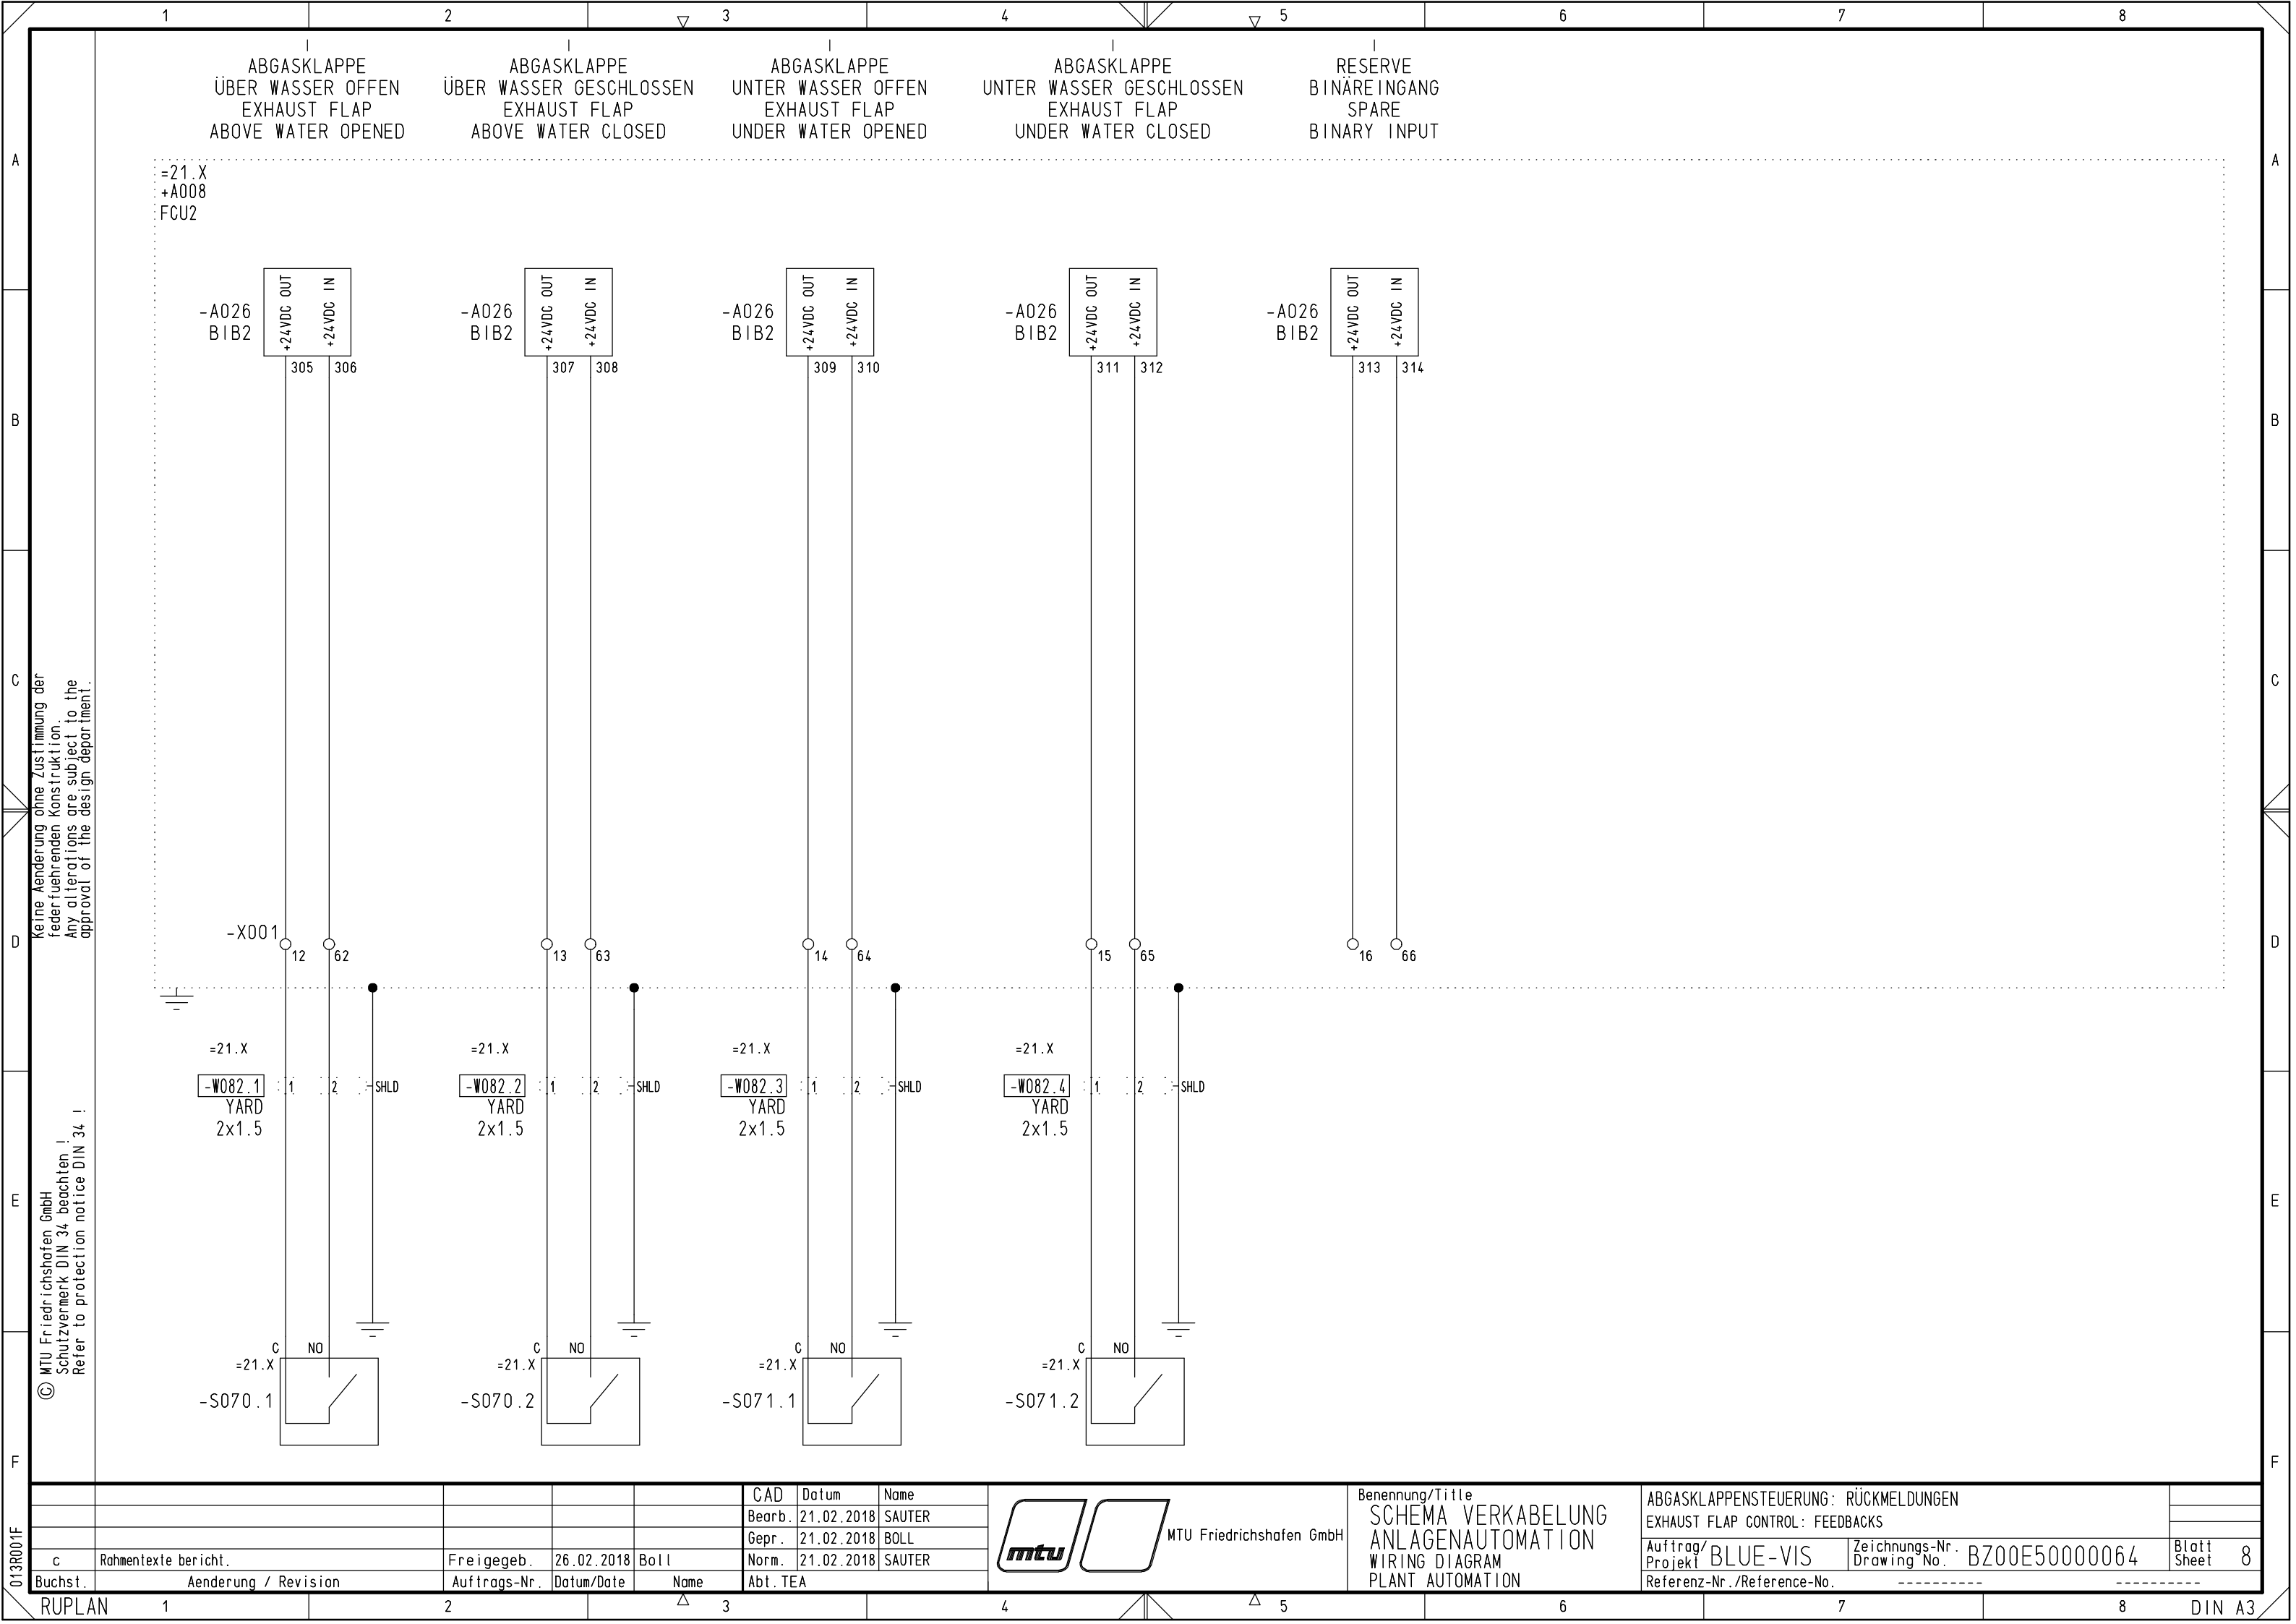

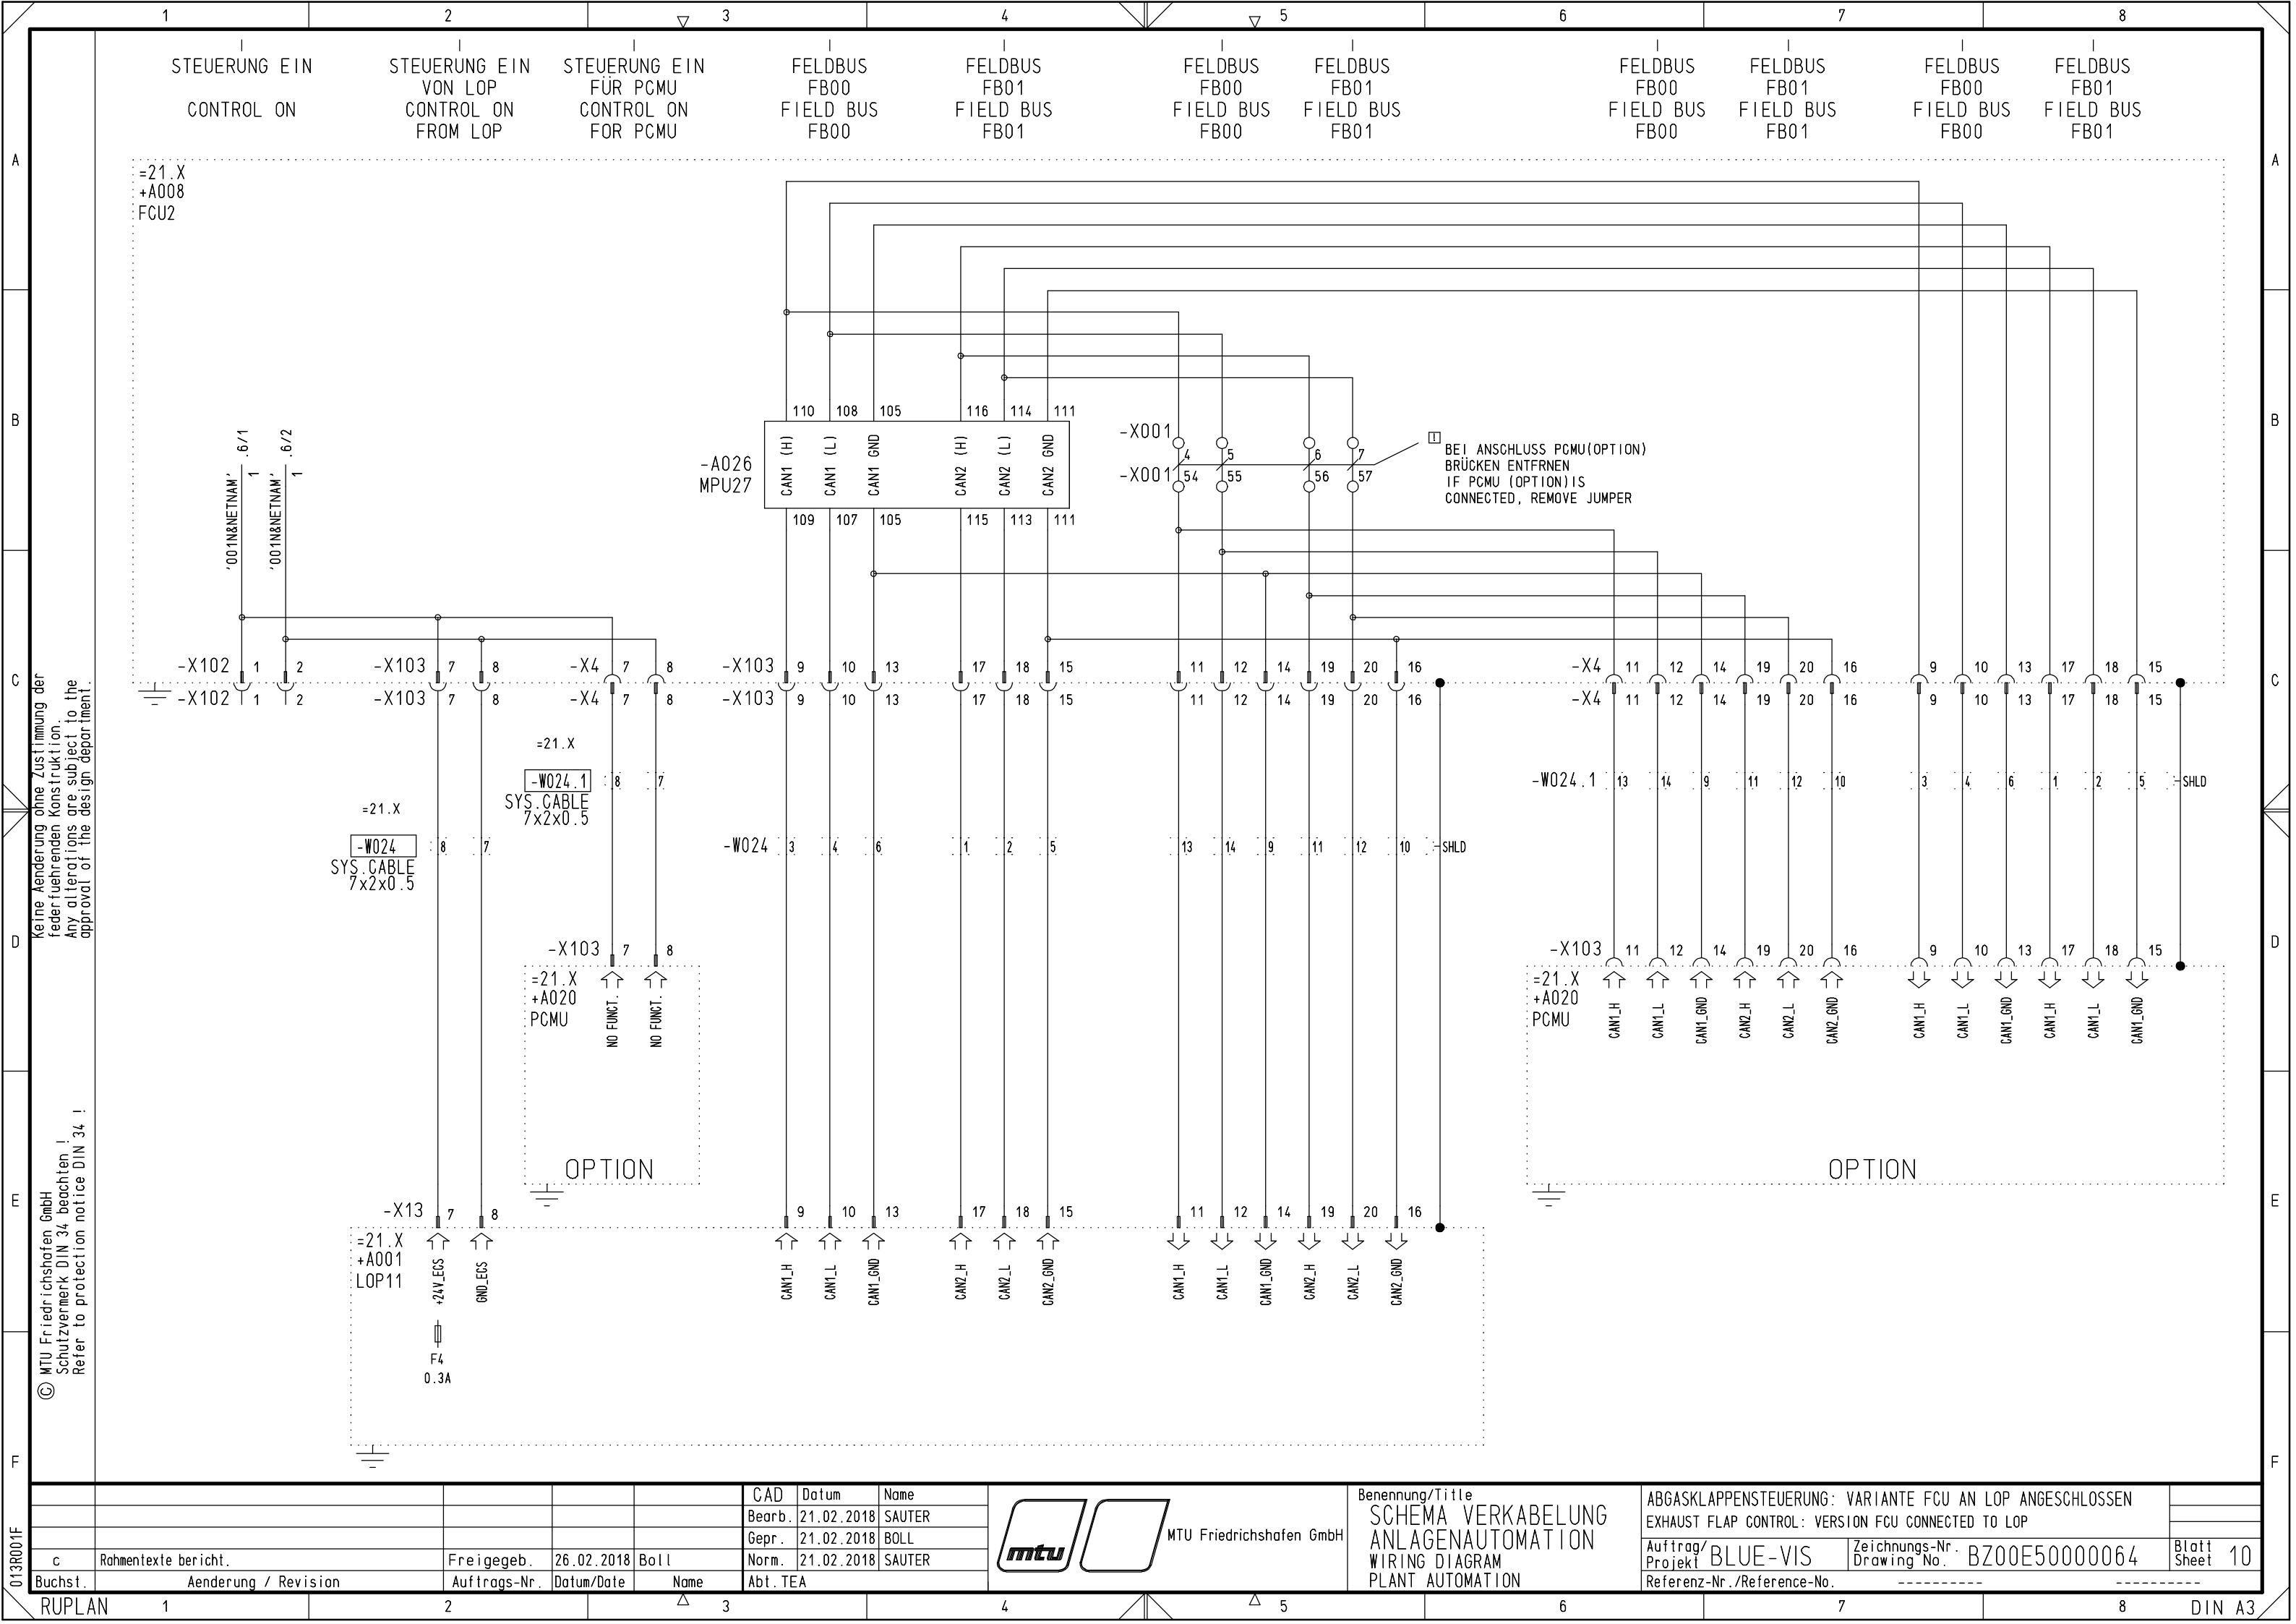

Keine Änderung ohne Zustimmung der
federführenden Konstruktion.
Any alterations are subject to the
approval of the design department.

© MTU Friedrichshafen GmbH
Schutzvermerk DIN 34 beachten !
Refer to protection notice DIN 34 !

					CAD	Datum	Name
					Bearb.	21.02.2018	SAUTER
					Gepr.	21.02.2018	BOLL
					Norm.	21.02.2018	SAUTER
c	Rahmentexte bericht.	Freigegeb.	26.02.2018	Boll	Abt. TEA		
Buchst.	Aenderung / Revision	Auftrags-Nr.	Datum/Date	Name			



Benennung/Title
SCHEMA VERKABELUNG
ANLAGENAUTOMATION
WIRING DIAGRAM
PLANT AUTOMATION

ABGASKLAPPENSTEUERUNG: VARIANTE FCU AN LOP ANGESCHLOSSEN EXHAUST FLAP CONTROL: VERSION FCU CONNECTED TO LOP			
Auftrag/ Projekt	BLUE-VIS	Zeichnungs-Nr. Drawing No.	BZ00E50000064
Referenz-Nr./Reference-No.	-----		
Blatt Sheet	10		


THE WIRING OF THE GEARBOXE IS SHOWN FOR DIFFERENT
INTERFACES(CONNECTING VARIATIONS).
SEE GEARBOX FOR VALID VERSION.


				CAD	Datum	Name	 MTU Friedrichshafen GmbH	Benennung/Title SCHEMA VERKABELUNG ANLAGENAUTOMATION WIRING DIAGRAM PLANT AUTOMATION	ZF GETRIEBE, HINWEISE GETRIEBESCHNITTSTELLEN				
				Bearb.	21.02.2018	SAUTER			ZF GEARBOX, INSTRUCTIONS GEARBOX INTERFACES				
				Gepr.	21.02.2018	BOLL							
				Norm.	21.02.2018	SAUTER							
entexte bericht.	Freigegeb.	26.02.2018	Boll						Auftrag/ Projekti	BLUE-VIS	Zeichnungs-Nr. Drawing No.	BZ00E50000064	Blatt Sheet
Änderung / Revision	Auftrags-Nr.	Datum/Date	Name	Abt. TEA					Referenz-Nr./Reference-No. -----				

THE WIRING OF THE GEARBOXE IS SHOWN FOR DIFFERENT
INTERFACES(CONNECTING VARIATIONS).
SEE GEARBOX FOR VALID VERSION.

				CAD	Datum	Name	 MTU Friedrichshafen GmbH	Benennung/Title SCHEMA VERKABELUNG ANLAGENAUTOMATION WIRING DIAGRAM PLANT AUTOMATION	ZF GETRIEBE, HINWEISE GETRIEBESCHNITTSTELLEN			
				Bearb.	21.02.2018	SAUTER			ZF GEARBOX, INSTRUCTIONS GEARBOX INTERFACES			
				Gepr.	21.02.2018	BOLL			Auftrag/ Projekt		Zeichnungs-Nr. Drawing No.	Blatt Sheet
entexte bericht.	Freigegeb.	26.02.2018	Boll	Norm.	21.02.2018	SAUTER			Referenz-Nr./Reference-No.		-----	-----
Änderung / Revision	Auftrags-Nr.	Datum/Date	Name	Abt. TEA								

[illegible]

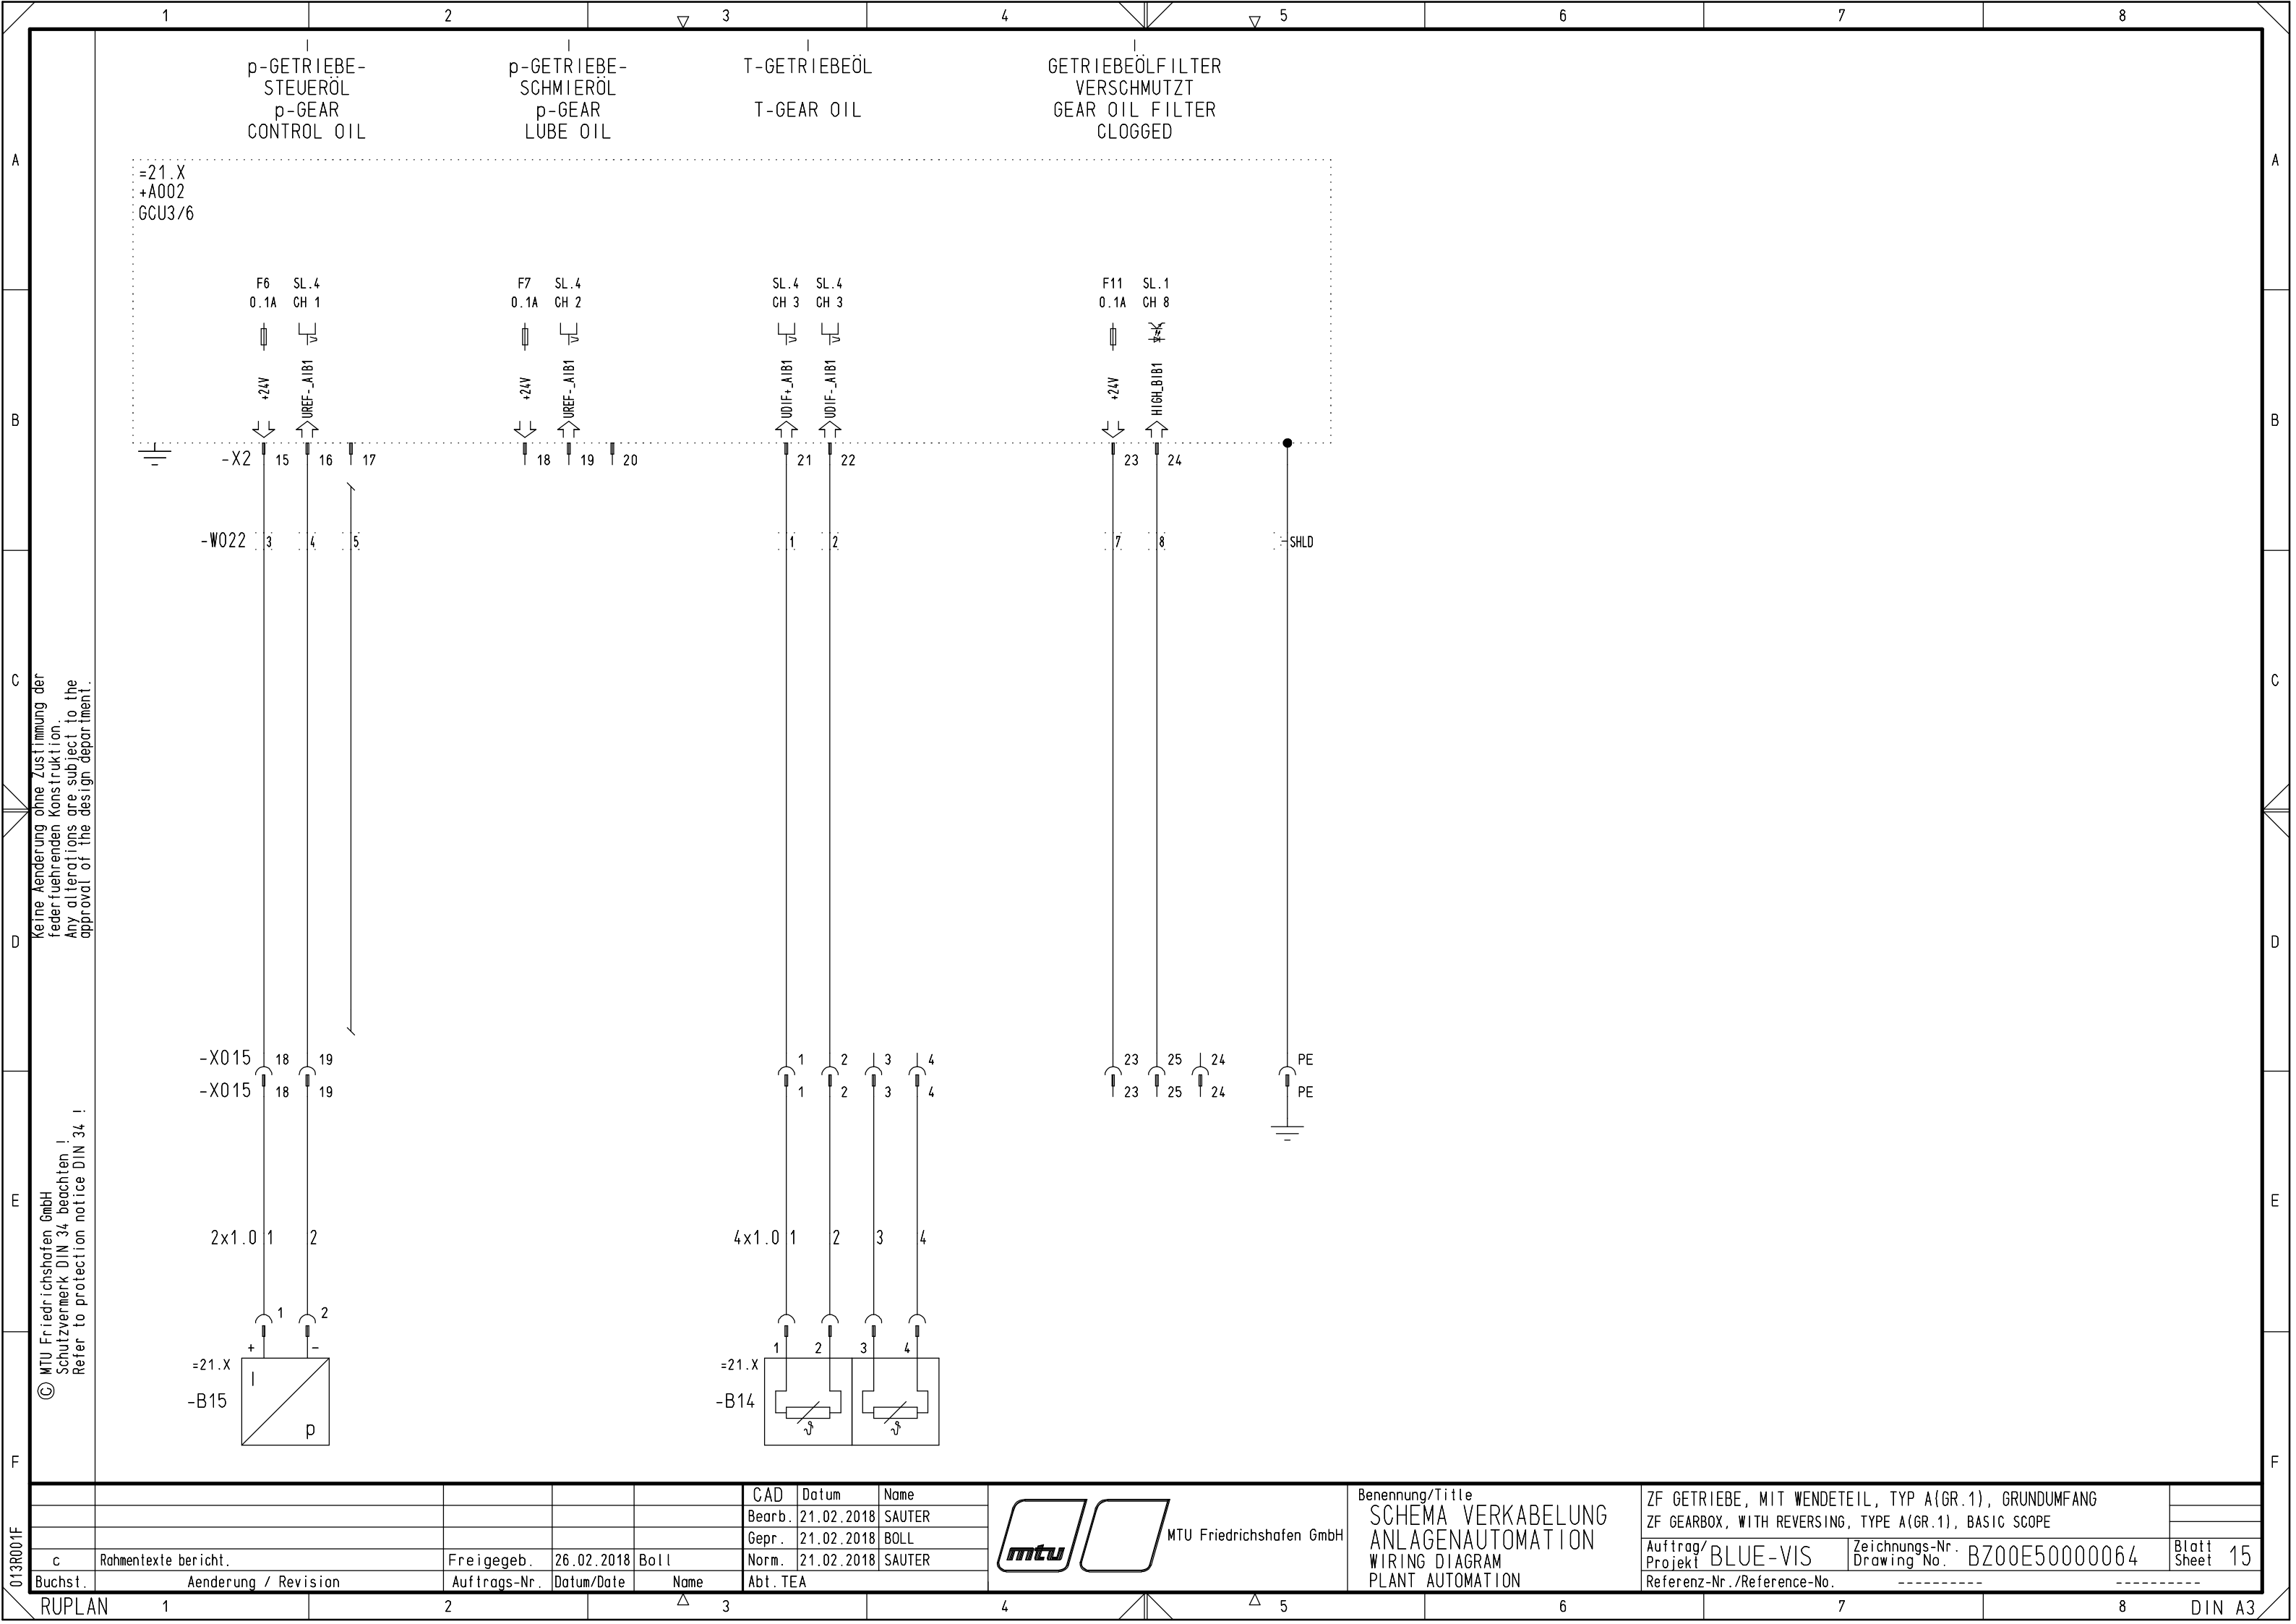

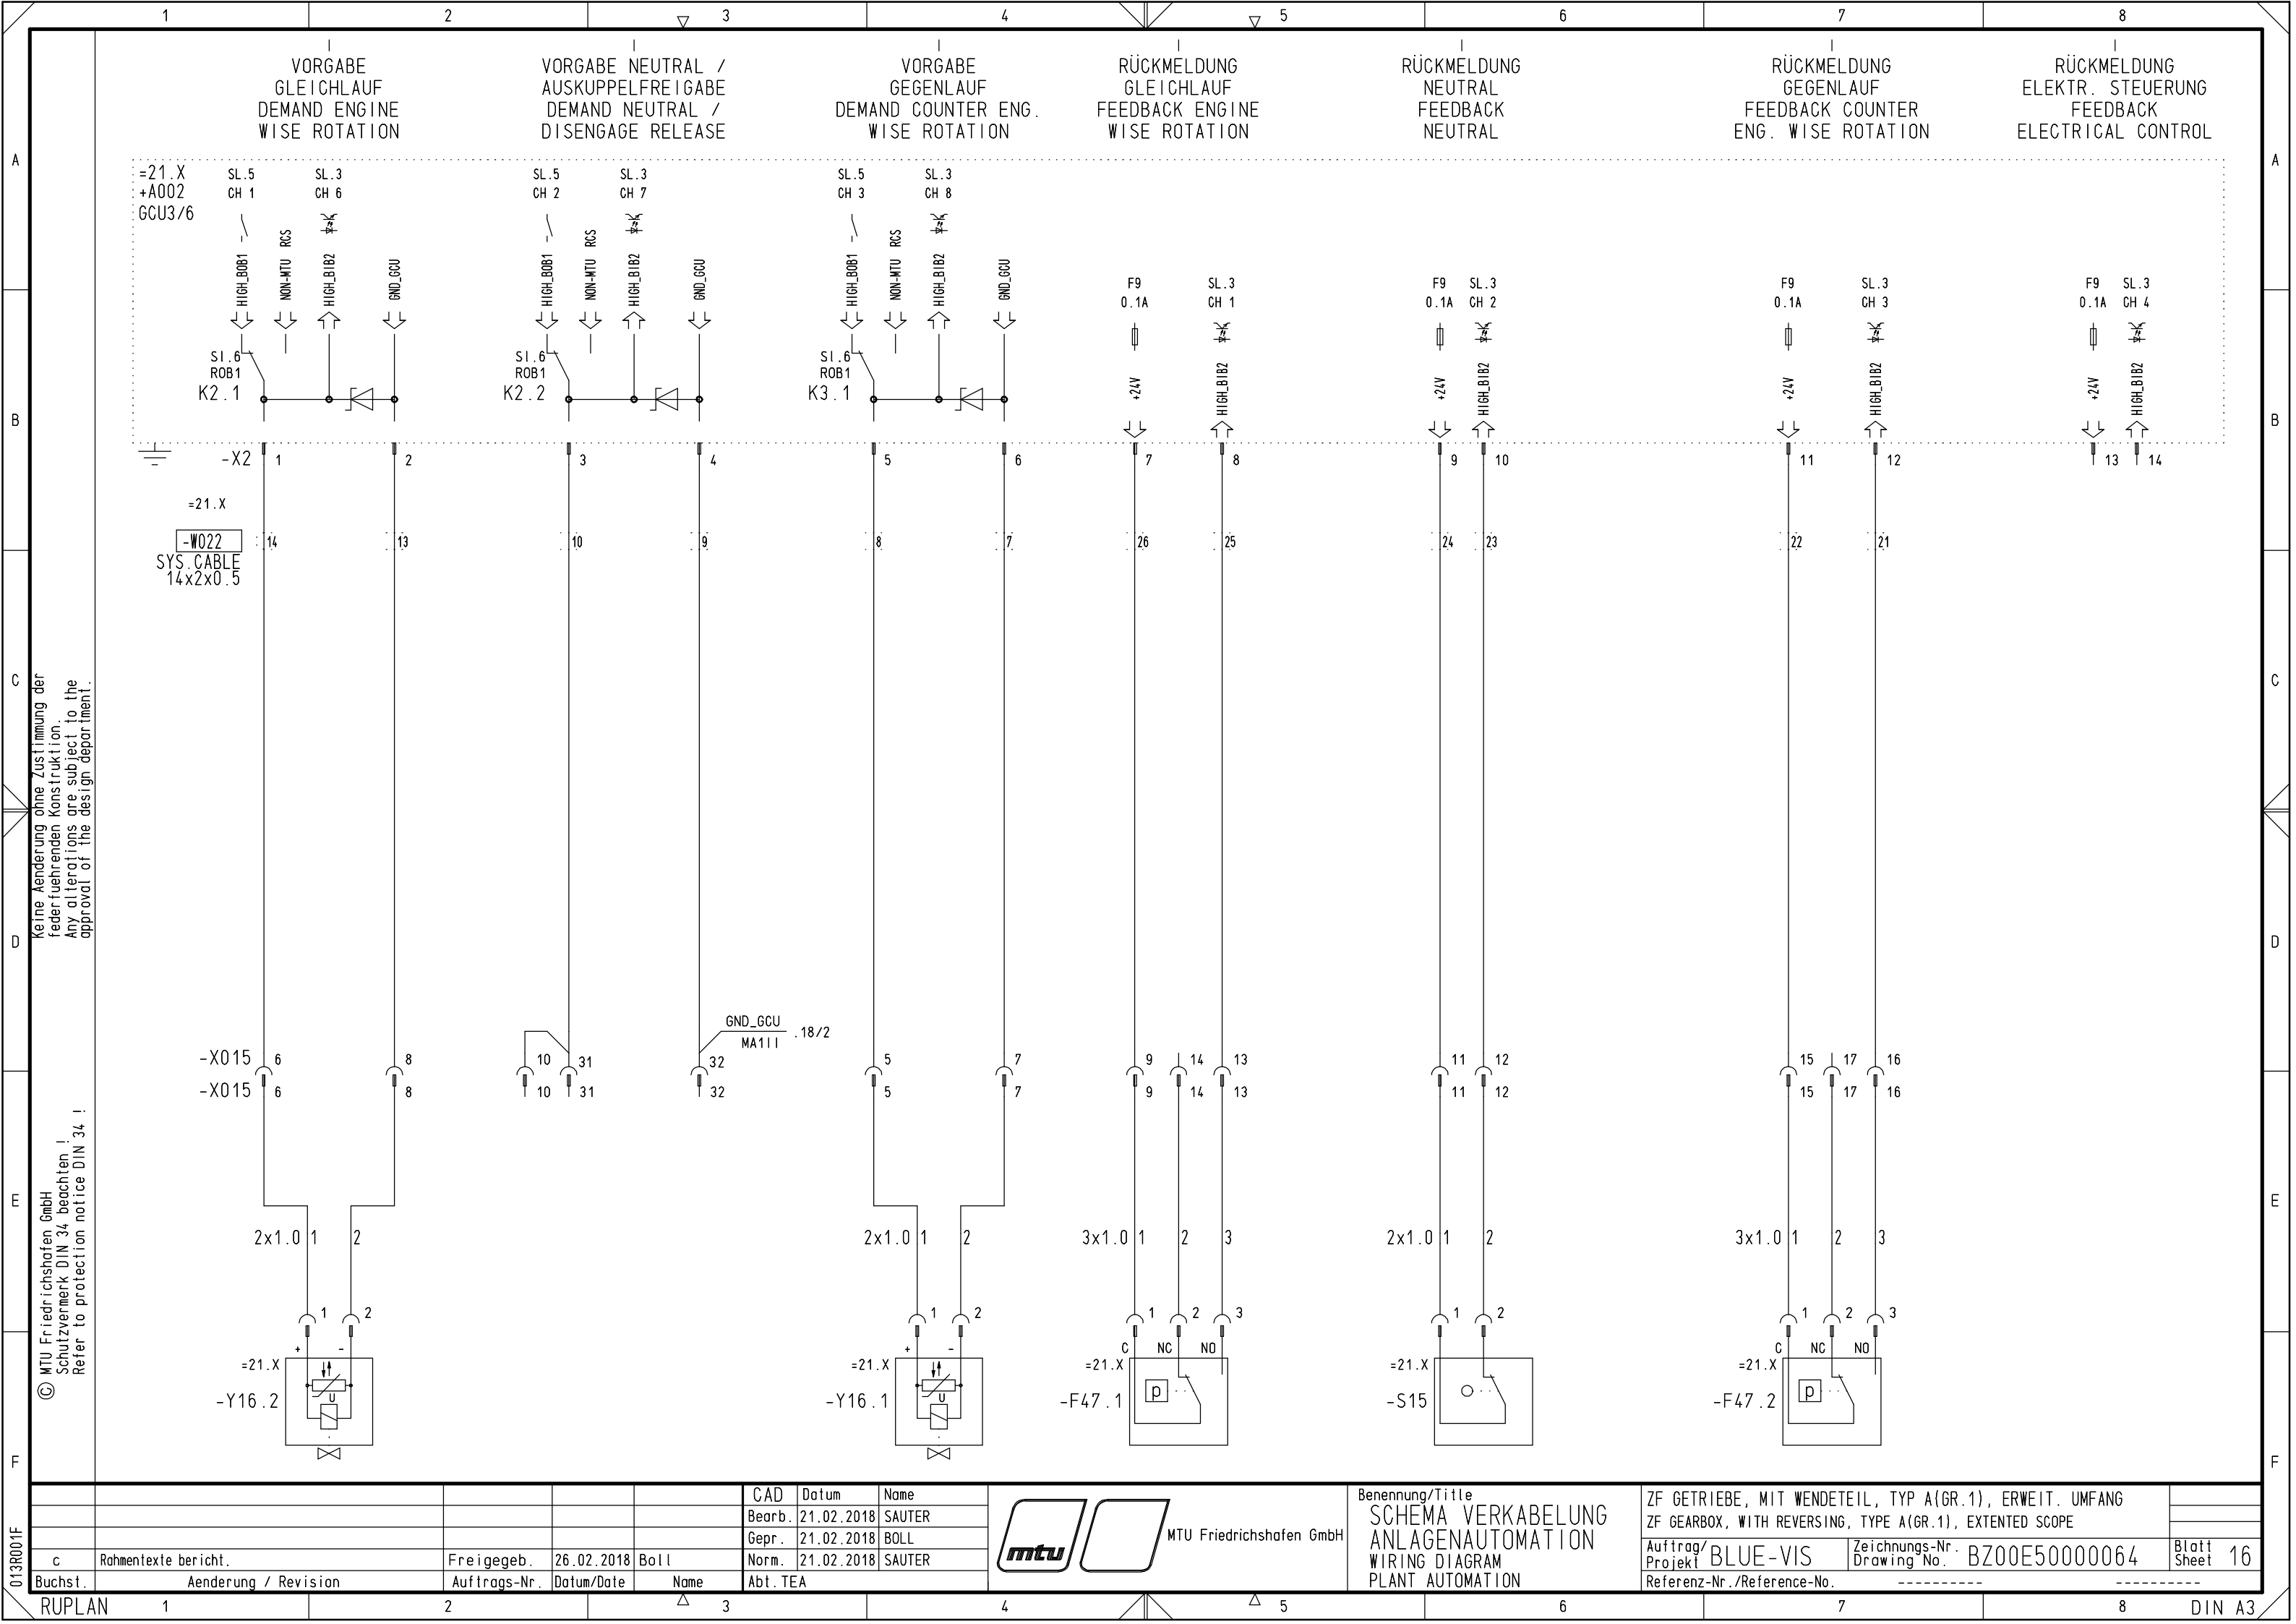

Keine Änderung ohne Zustimmung der
federführenden Konstruktion.
Any alterations are subject to the
approval of the design department.


© MTU Friedrichshafen GmbH
Schutzvermerk DIN 34 beachten!
Refer to protection notice DIN 34!


					CAD	Datum	Name
					Bearb.	21.02.2018	SAUTER
					Gepr.	21.02.2018	BOLL
					Norm.	21.02.2018	SAUTER
c	Rahmentexte bericht.	Freigegeb.	26.02.2018	Boll	Abt. TEA		
Buchst.	Aenderung / Revision	Auftrags-Nr.	Datum/Date	Name			




Benennung/Title
SCHEMA VERKABELUNG
ANLAGENAUTOMATION
WIRING DIAGRAM
PLANT AUTOMATION


ZF GETRIEBE, MIT WENDETEIL, TYP A(GR.1), ERWEIT. UMFANG ZF GEARBOX, WITH REVERSING, TYPE A(GR.1), EXTENDED SCOPE		
Auftrag/ Projekt	BLUE-VIS	Zeichnungs-Nr. Drawing No. BZ00E50000064
Referenz-Nr./Reference-No.		Blatt Sheet 16

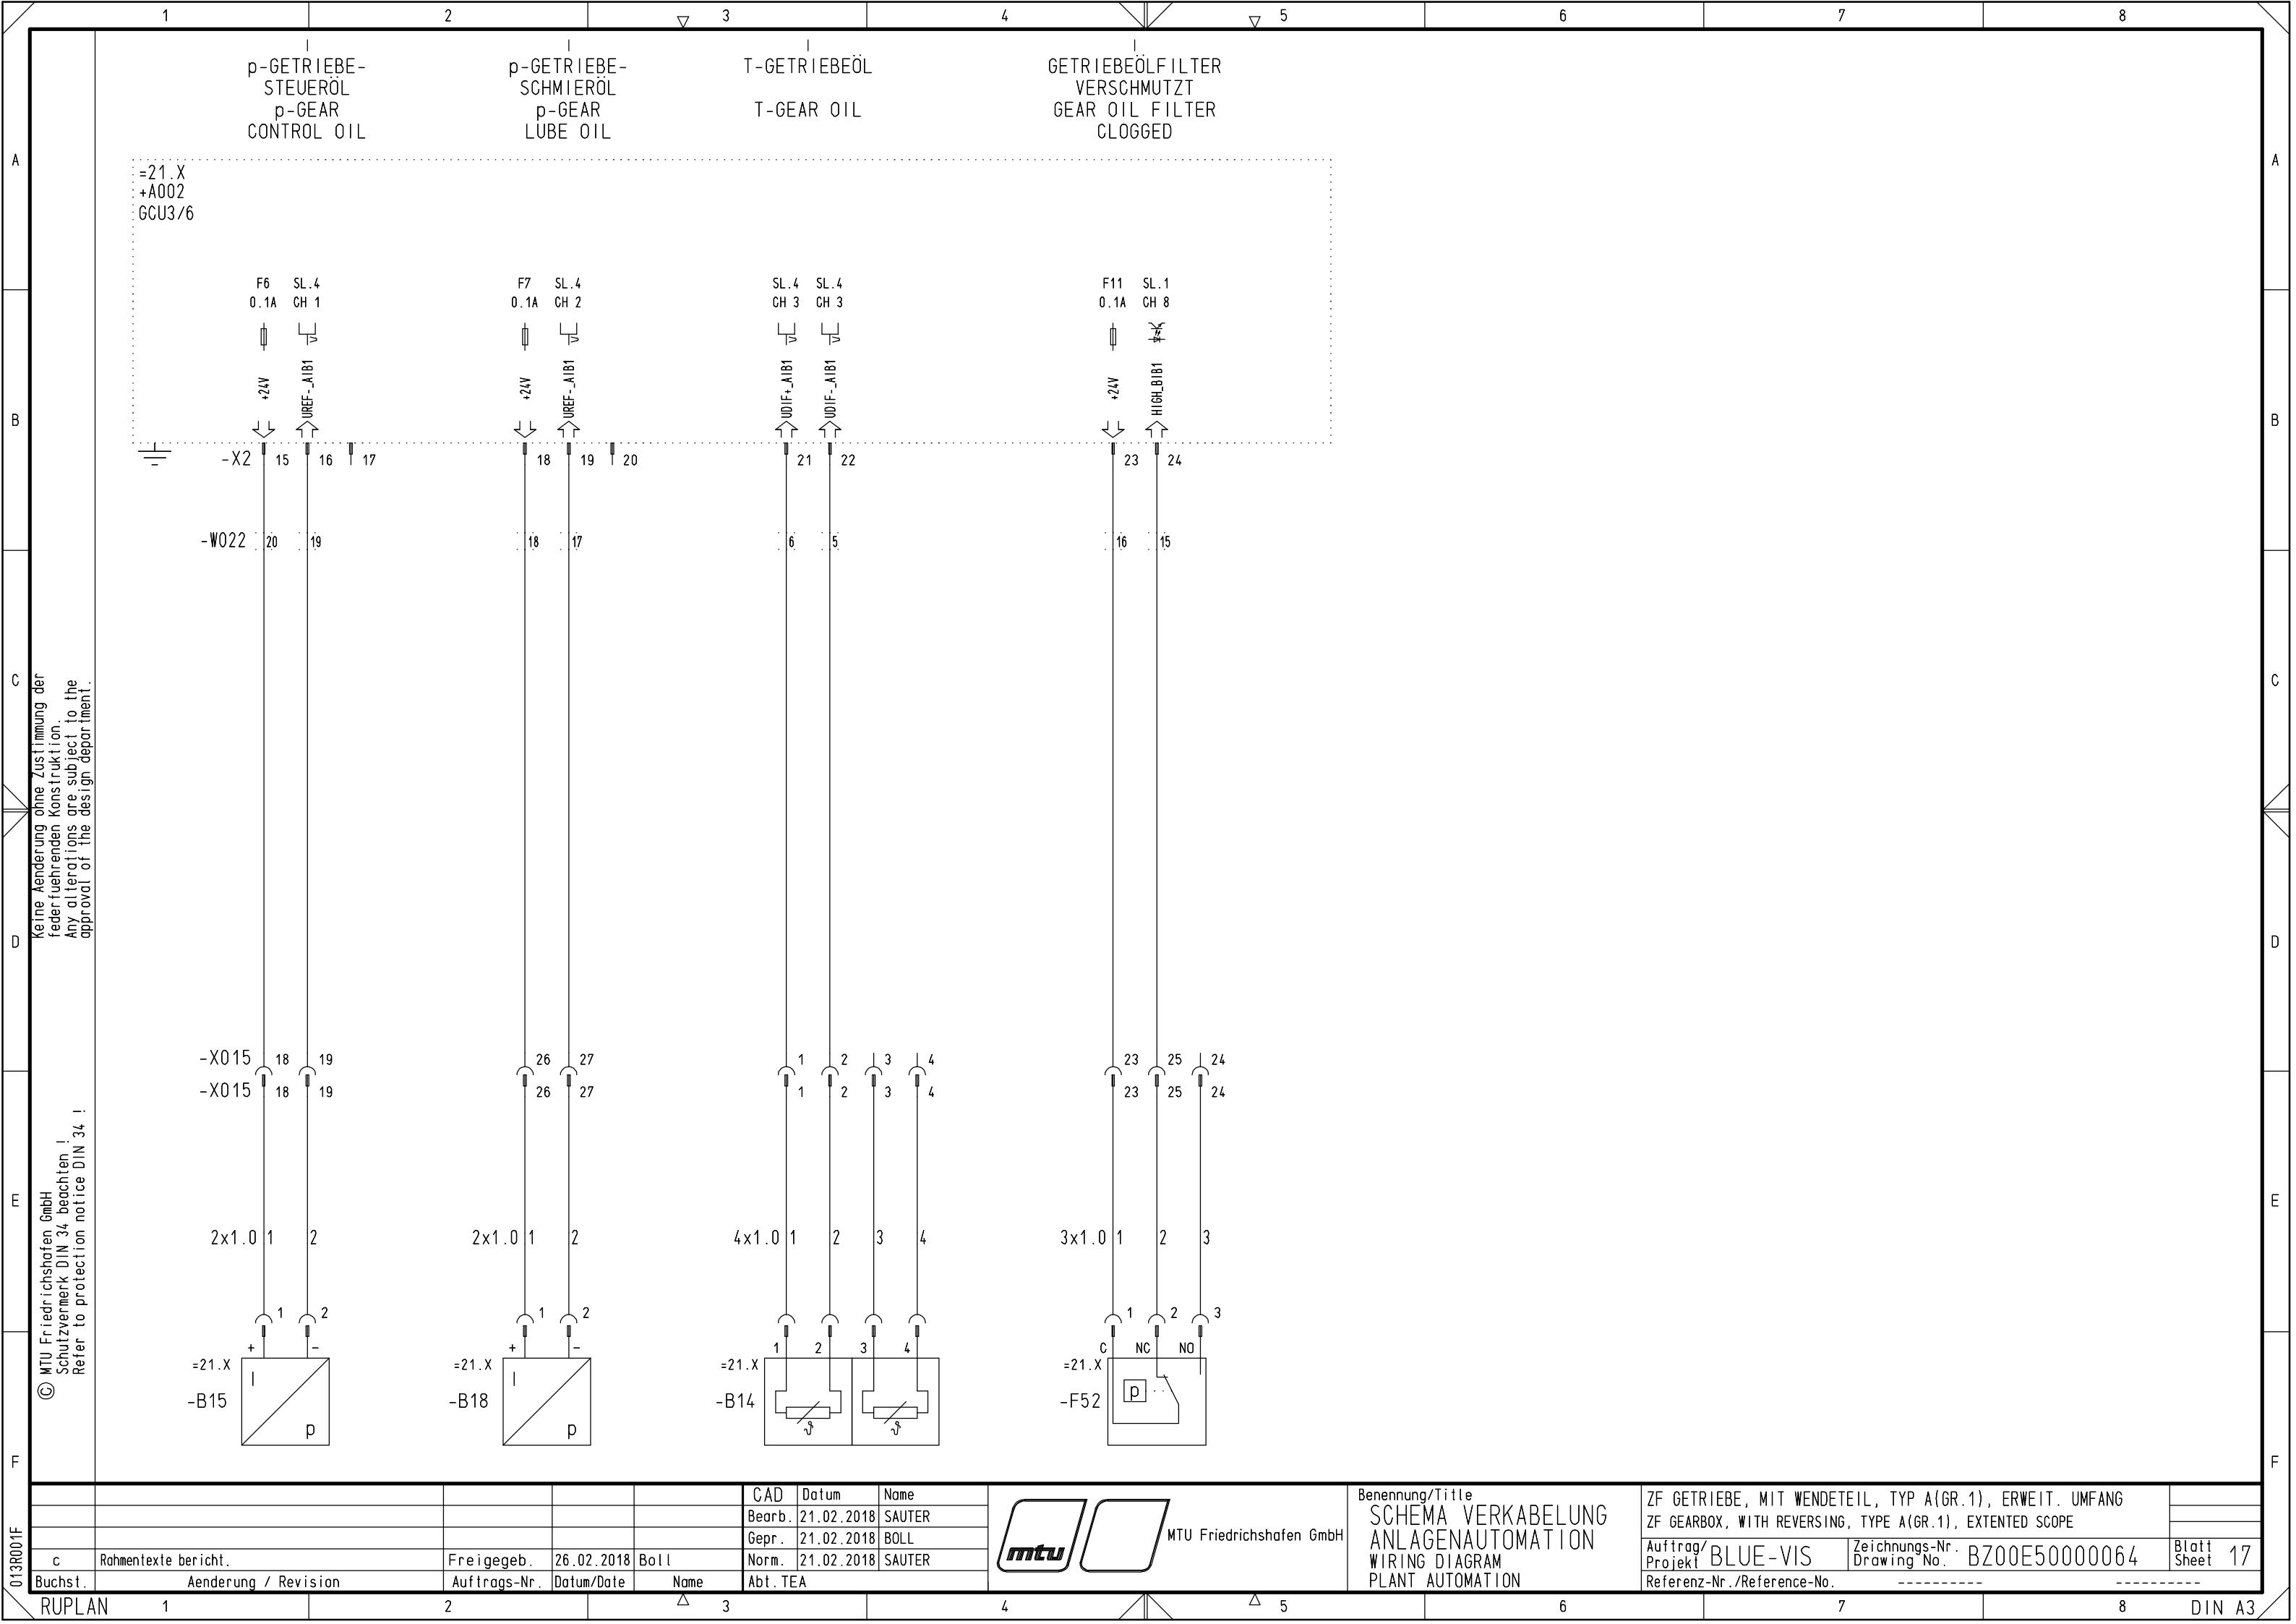

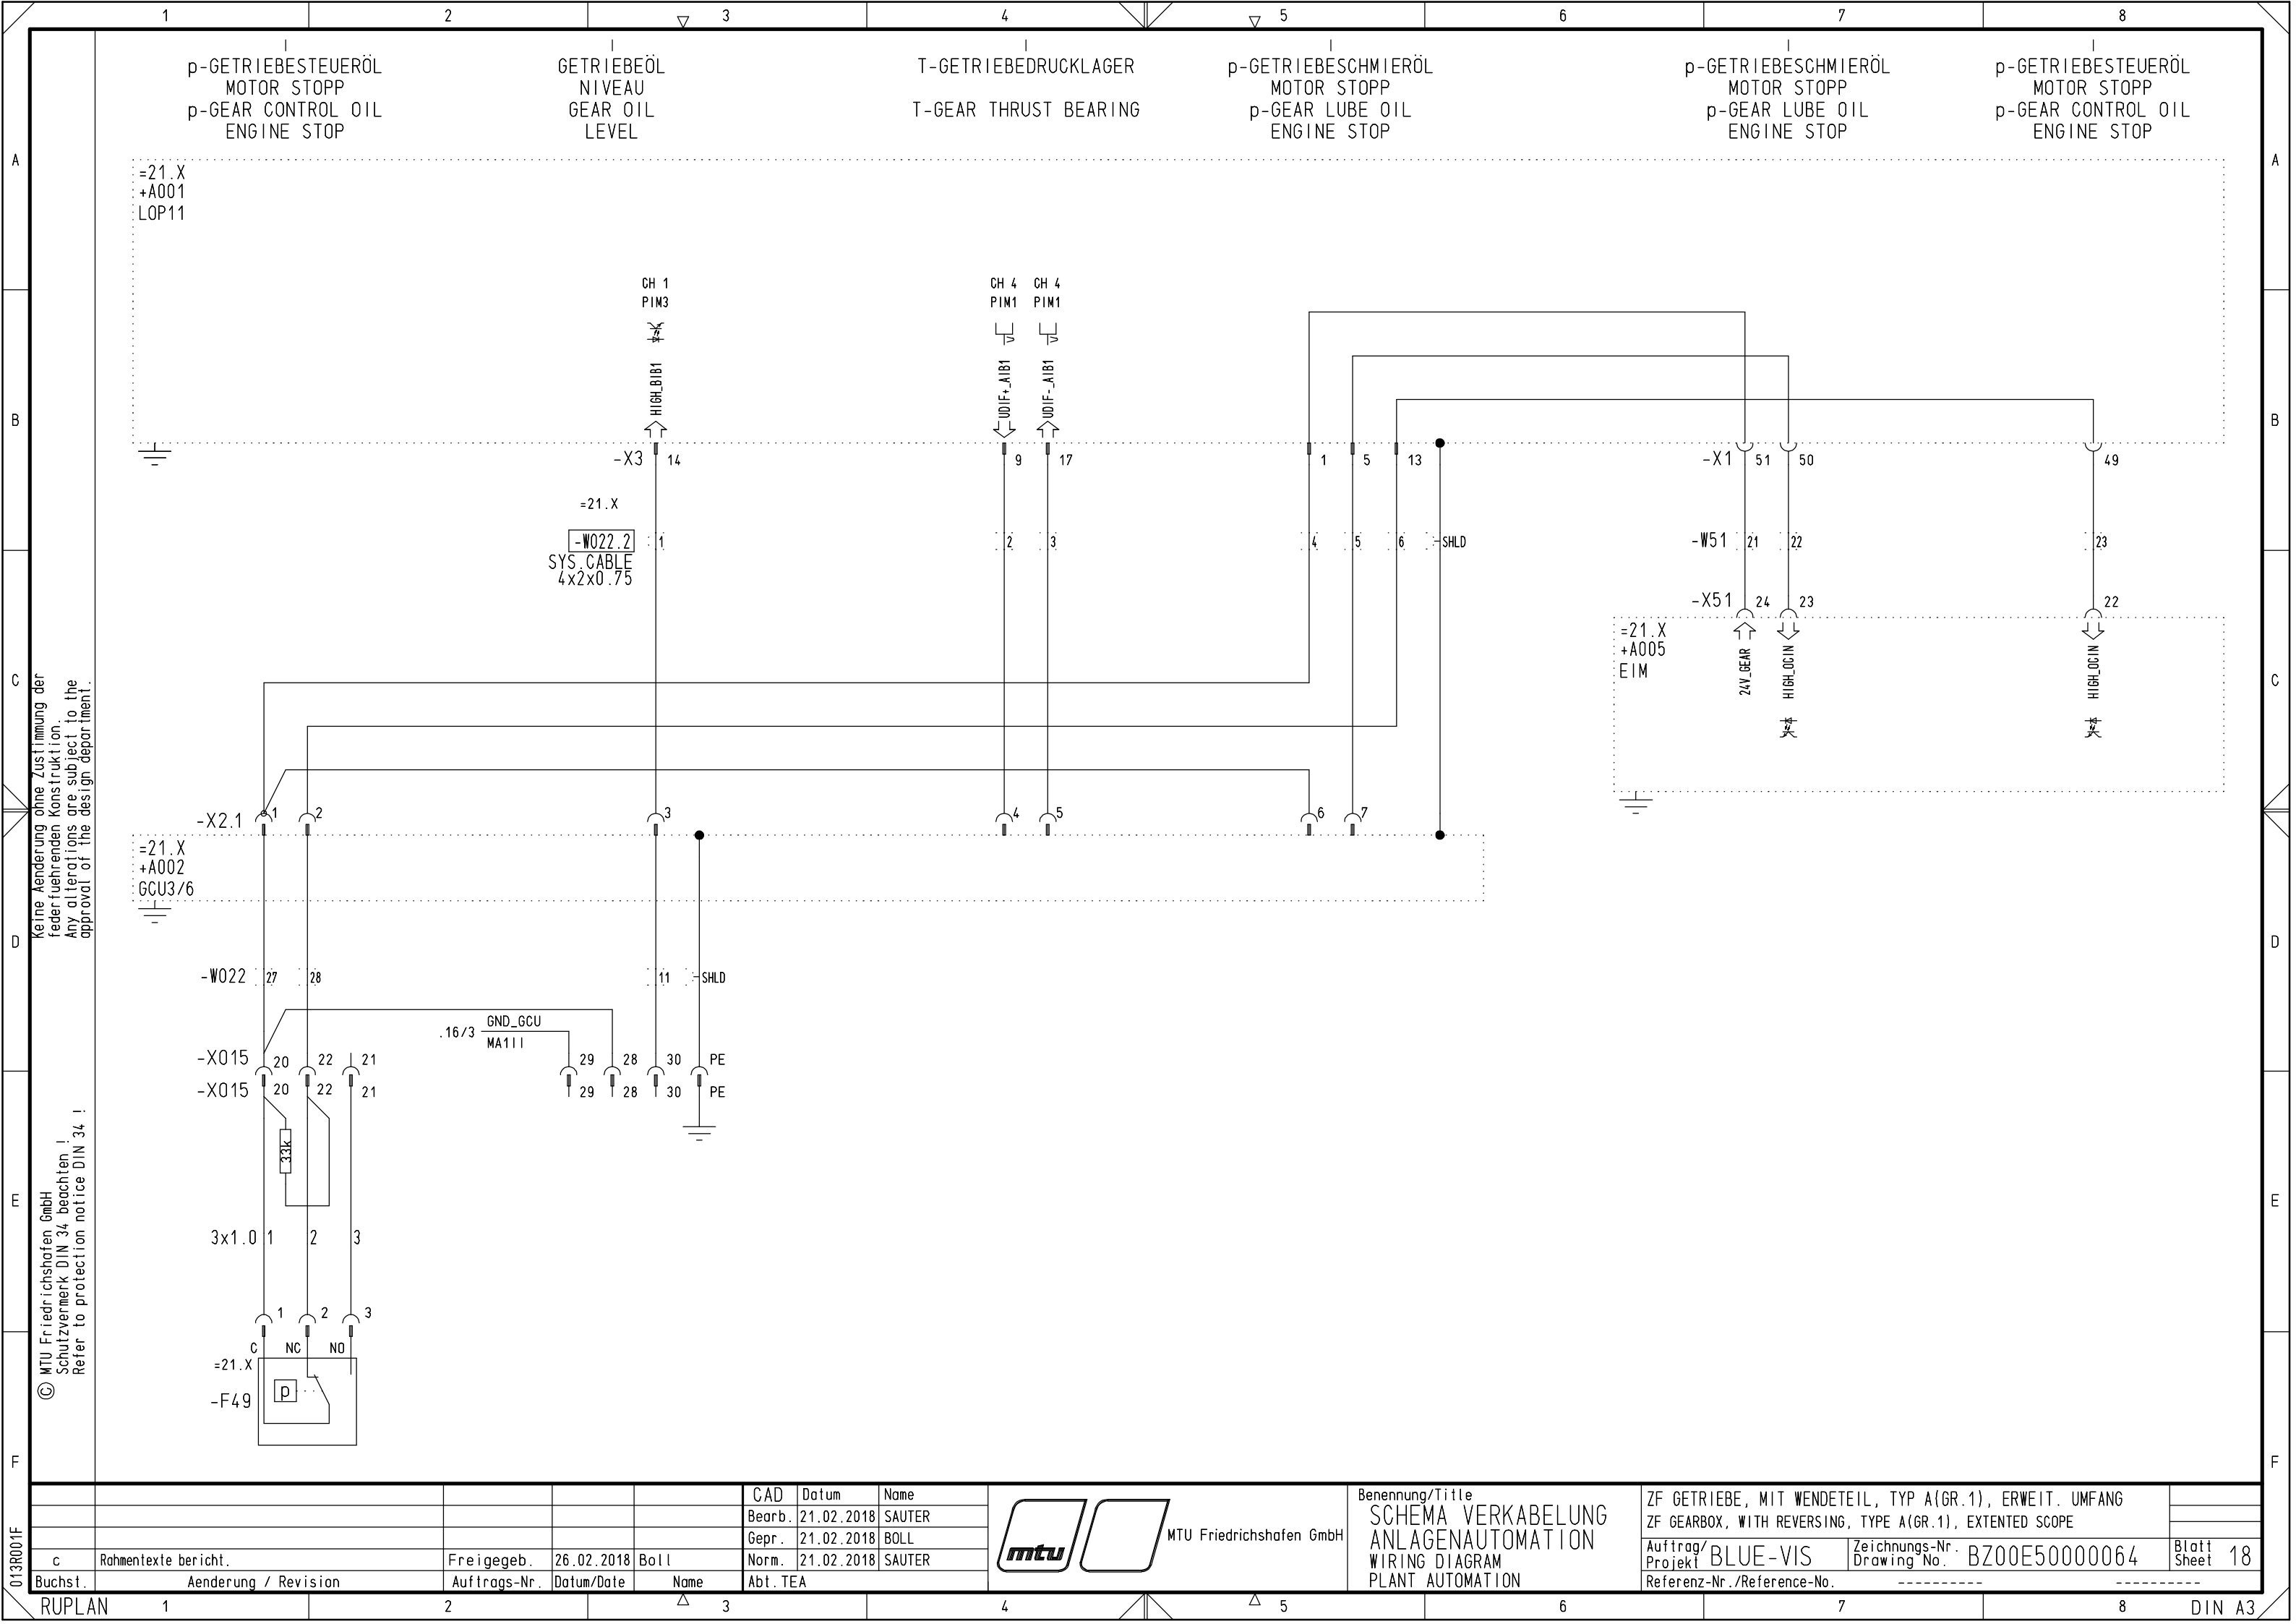

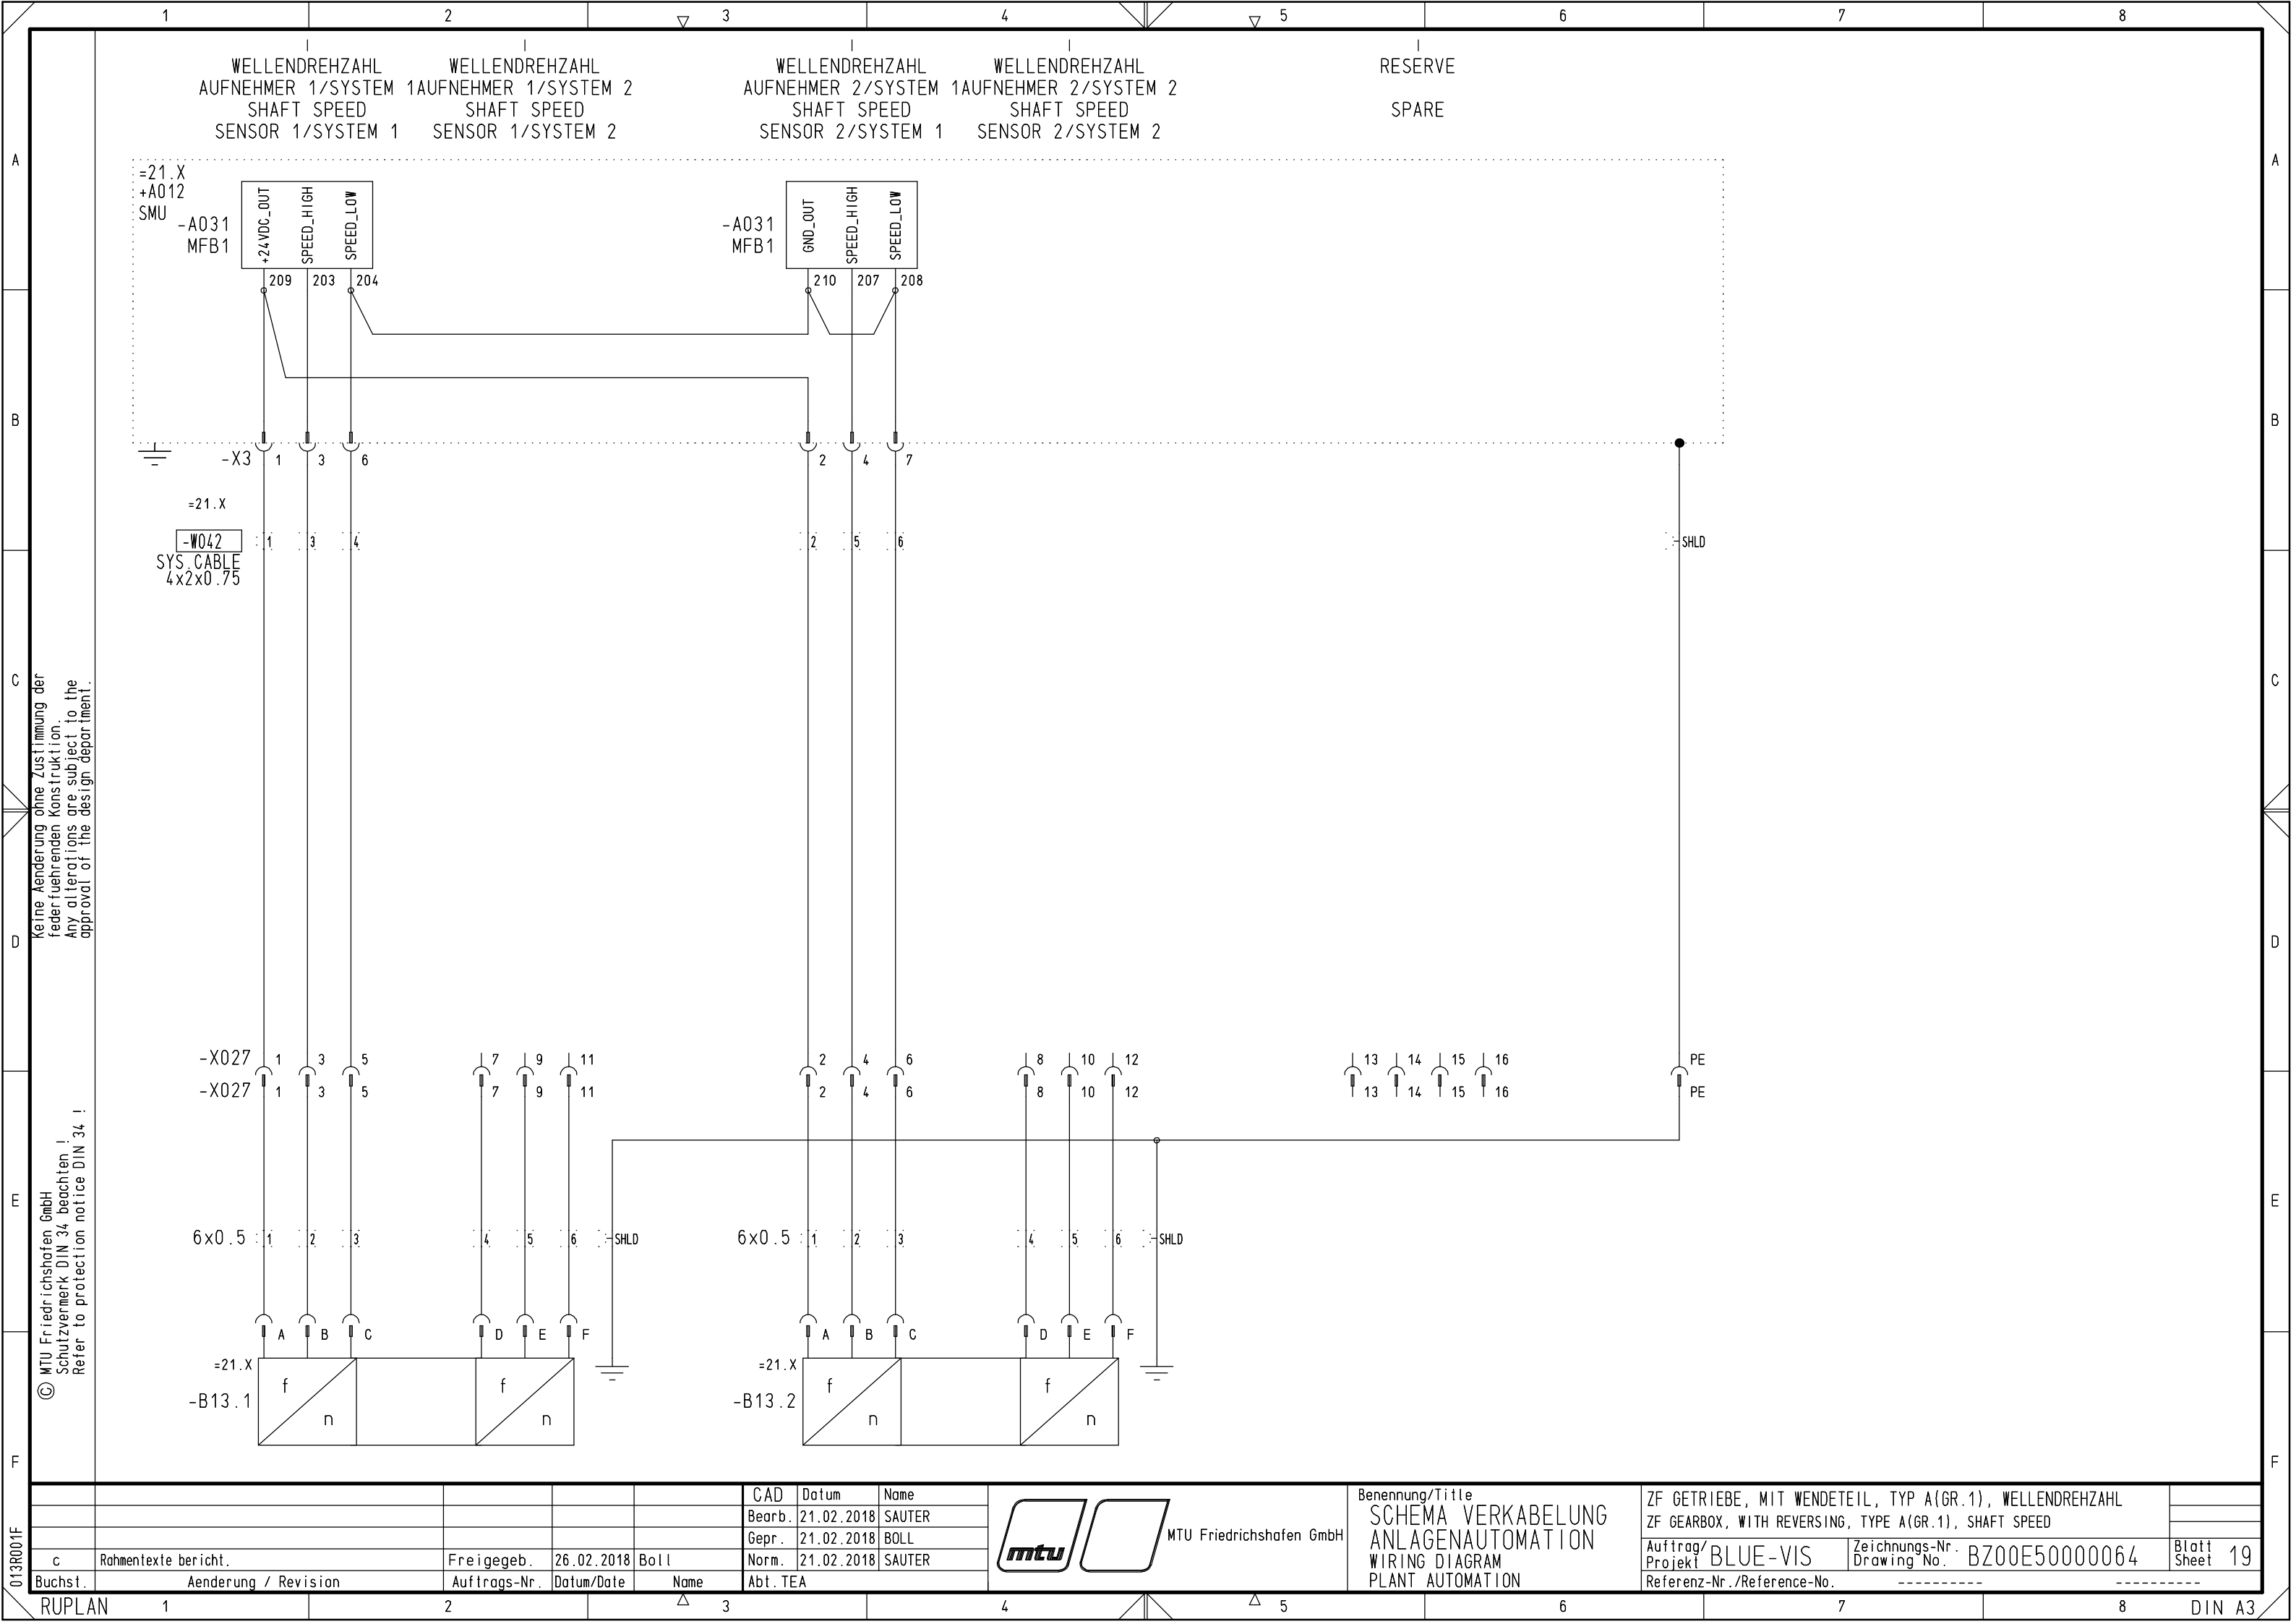

[illegible]

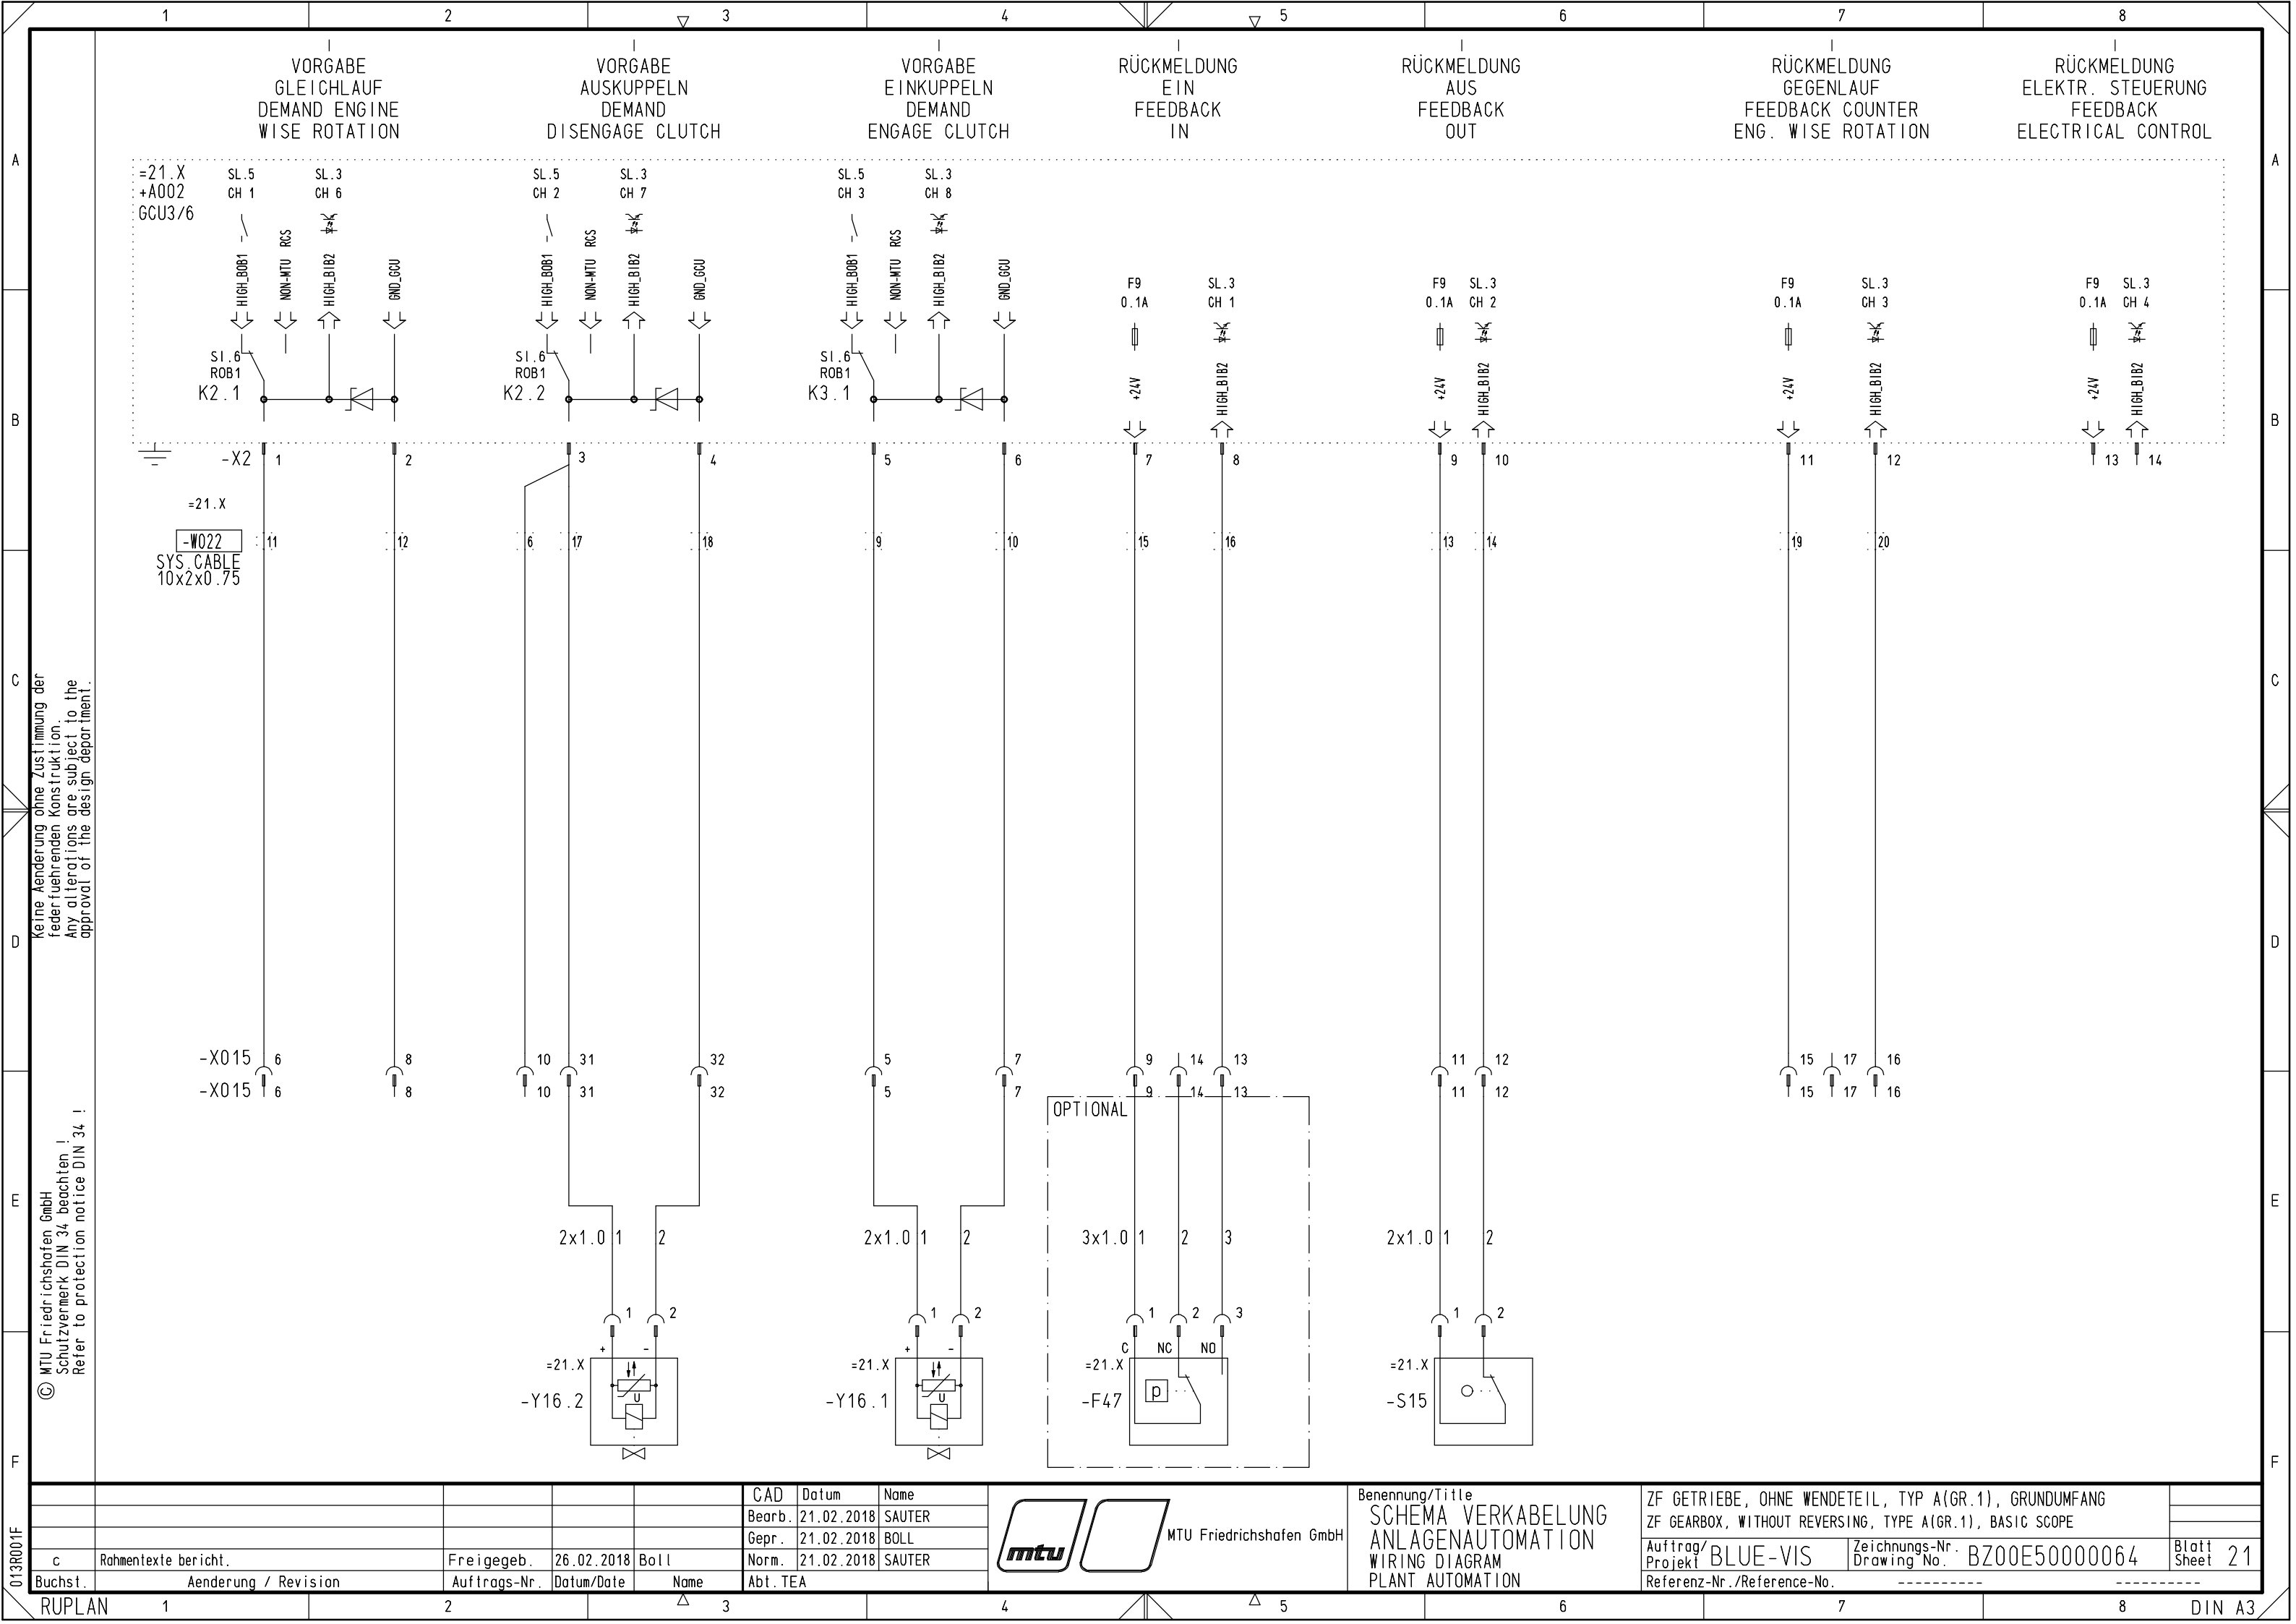

Keine Änderung ohne Zustimmung der
federführenden Konstruktion.
Any alterations are subject to the
approval of the design department.

© MTU Friedrichshafen GmbH
Schutzmerk DIN 34 beachten !
Refer to protection notice DIN 34 !


					CAD	Datum	Name
					Bearb.	21.02.2018	SAUTER
					Gepr.	21.02.2018	BOLL
					Norm.	21.02.2018	SAUTER
c	Rahmentexte bericht.	Freigegeb.	26.02.2018	Boll	Abt. TEA		
Buchst.	Aenderung / Revision	Auftrags-Nr.	Datum/Date	Name			




Benennung/Title SCHEMA VERKABELUNG ANLAGENAUTOMATION WIRING DIAGRAM PLANT AUTOMATION		ZF GETRIEBE, OHNE WENDETEIL, TYP A(GR.1), GRUNDUMFANG ZF GEARBOX, WITHOUT REVERSING, TYPE A(GR.1), BASIC SCOPE		
Auftrag/ Projekt	BLUE-VIS	Zeichnungs-Nr. Drawing No.	BZ00E50000064	Blatt Sheet
Referenz-Nr./Reference-No.		-----		

Keine Änderung ohne Zustimmung der
federführenden Konstruktion.
Any alterations are subject to the
approval of the design department.

© MTU Friedrichshafen GmbH
Schutzvermerk DIN 34 beachten !
Refer to protection notice DIN 34 !

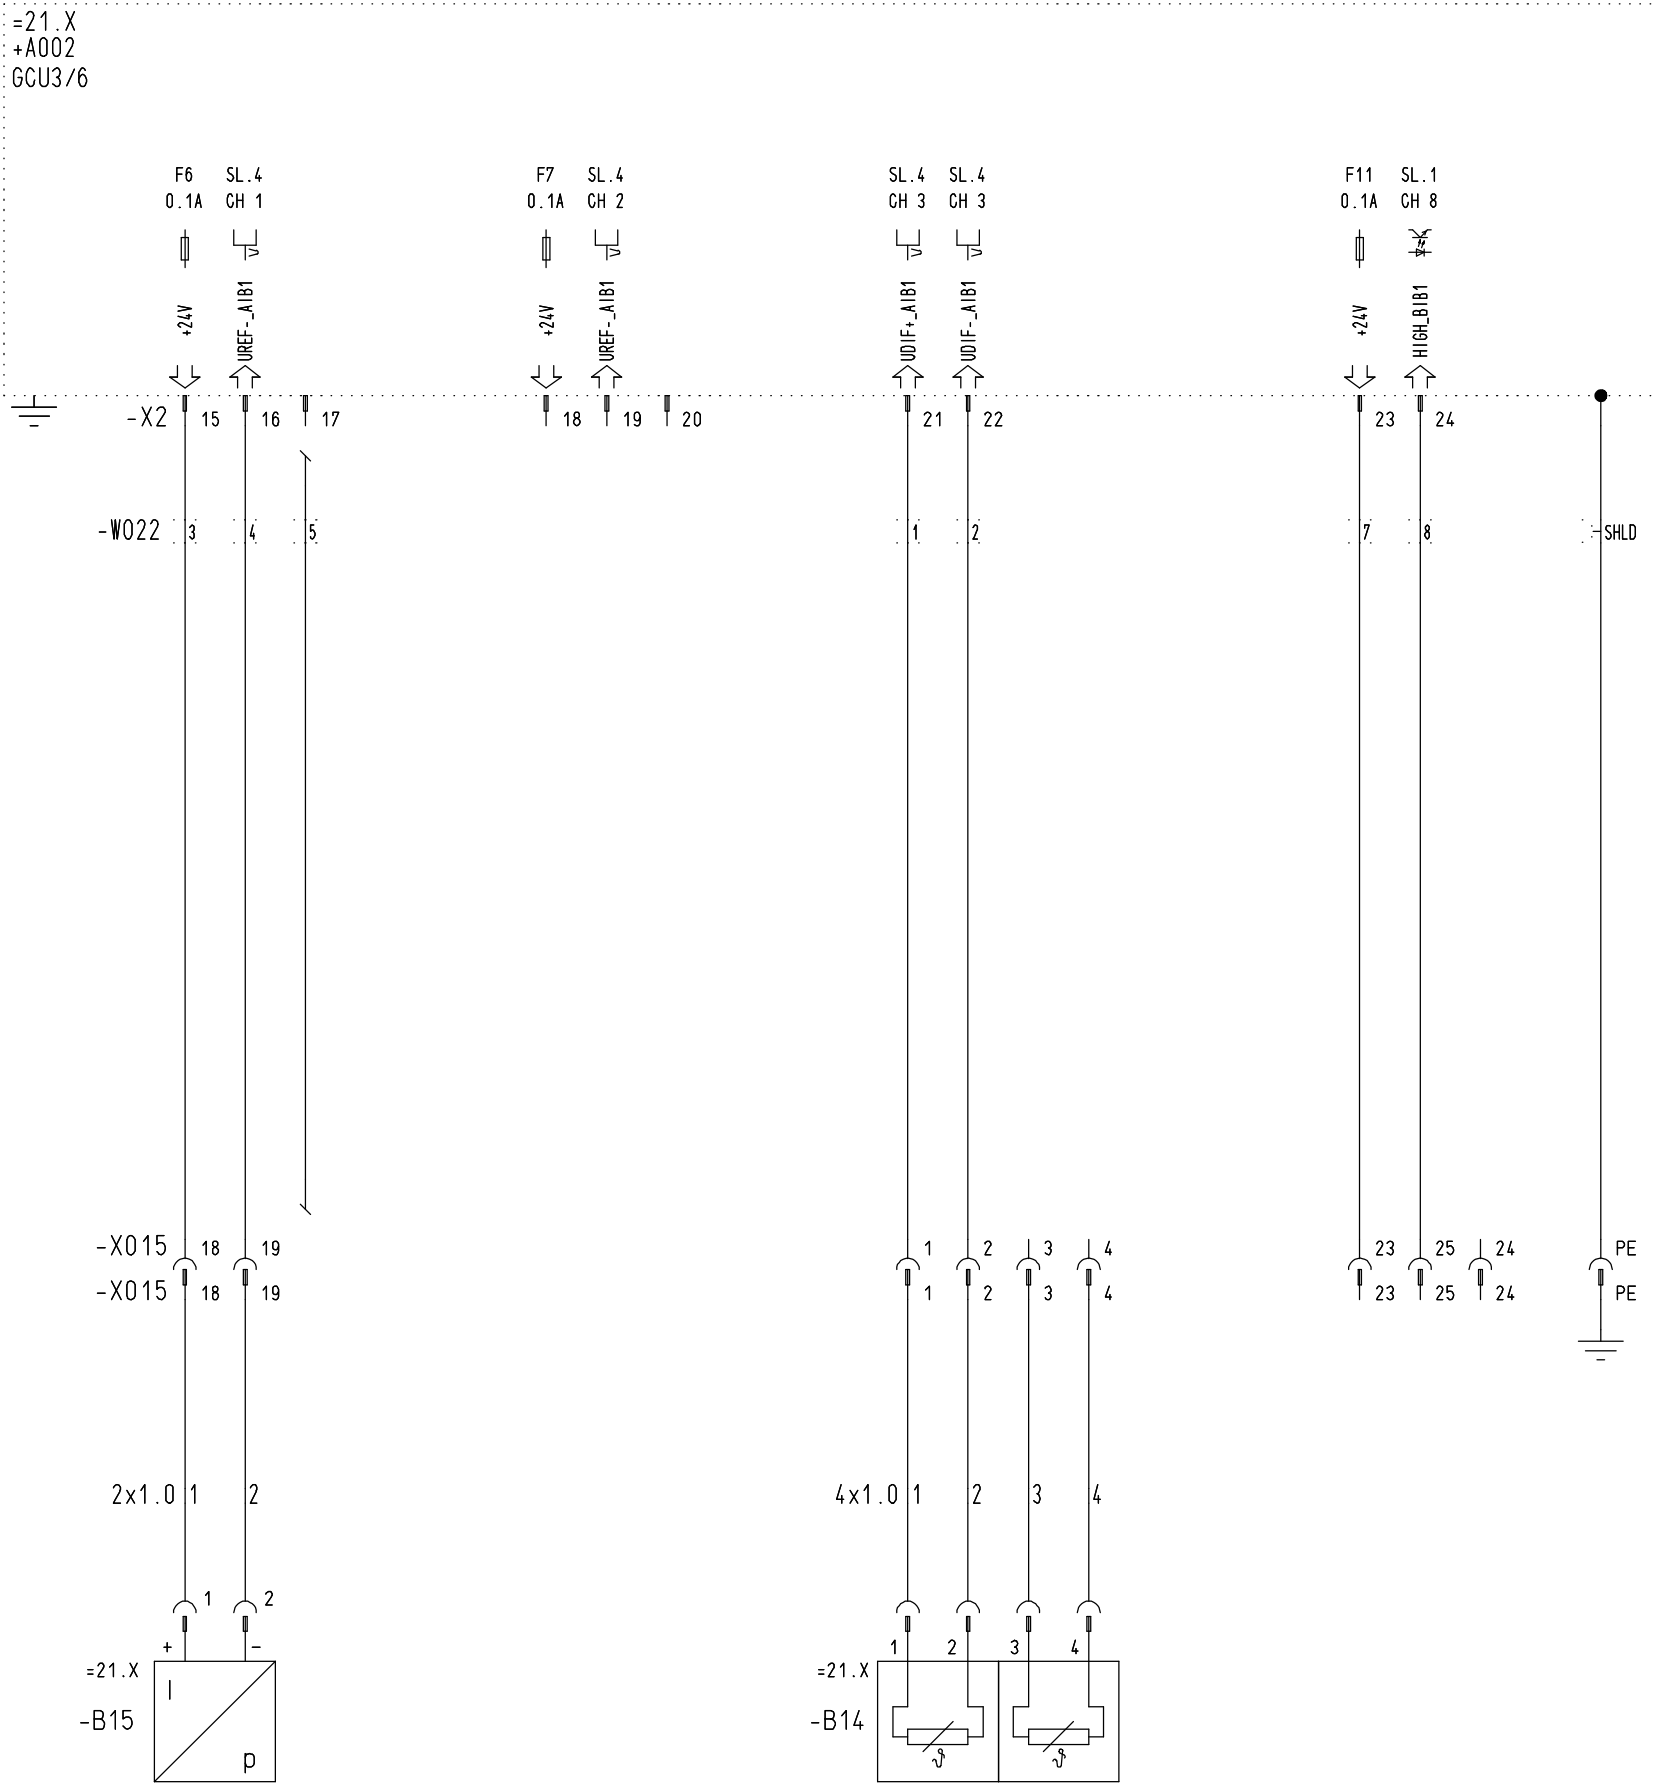


					CAD	Datum	Name	mtu MTU Friedrichshafen GmbH		Benennung/Title SCHEMA VERKABELUNG ANLAGENAUTOMATION WIRING DIAGRAM PLANT AUTOMATION		ZF GETRIEBE, OHNE WENDETEIL, TYP A(GR.1), GRUNDUMFANG ZF GEARBOX, WITHOUT REVERSING, TYPE A(GR.1), BASIC SCOPE		Blatt Sheet 22
					Bearb.	21.02.2018	SAUTER							
					Gepr.	21.02.2018	BOLL							
					Norm.	21.02.2018	SAUTER							
Buchst.	Aenderung / Revision	Auftrags-Nr.	Datum/Date	Name	Abt. TEA							Auftrag/ Projekt	Zeichnungs-Nr. Drawing No.	Referenz-Nr./Reference-No.
c	Rahmentexte bericht.	Freigegeb.	26.02.2018	Boll								BLUE-VIS	BZ00E50000064	
RUPLAN														

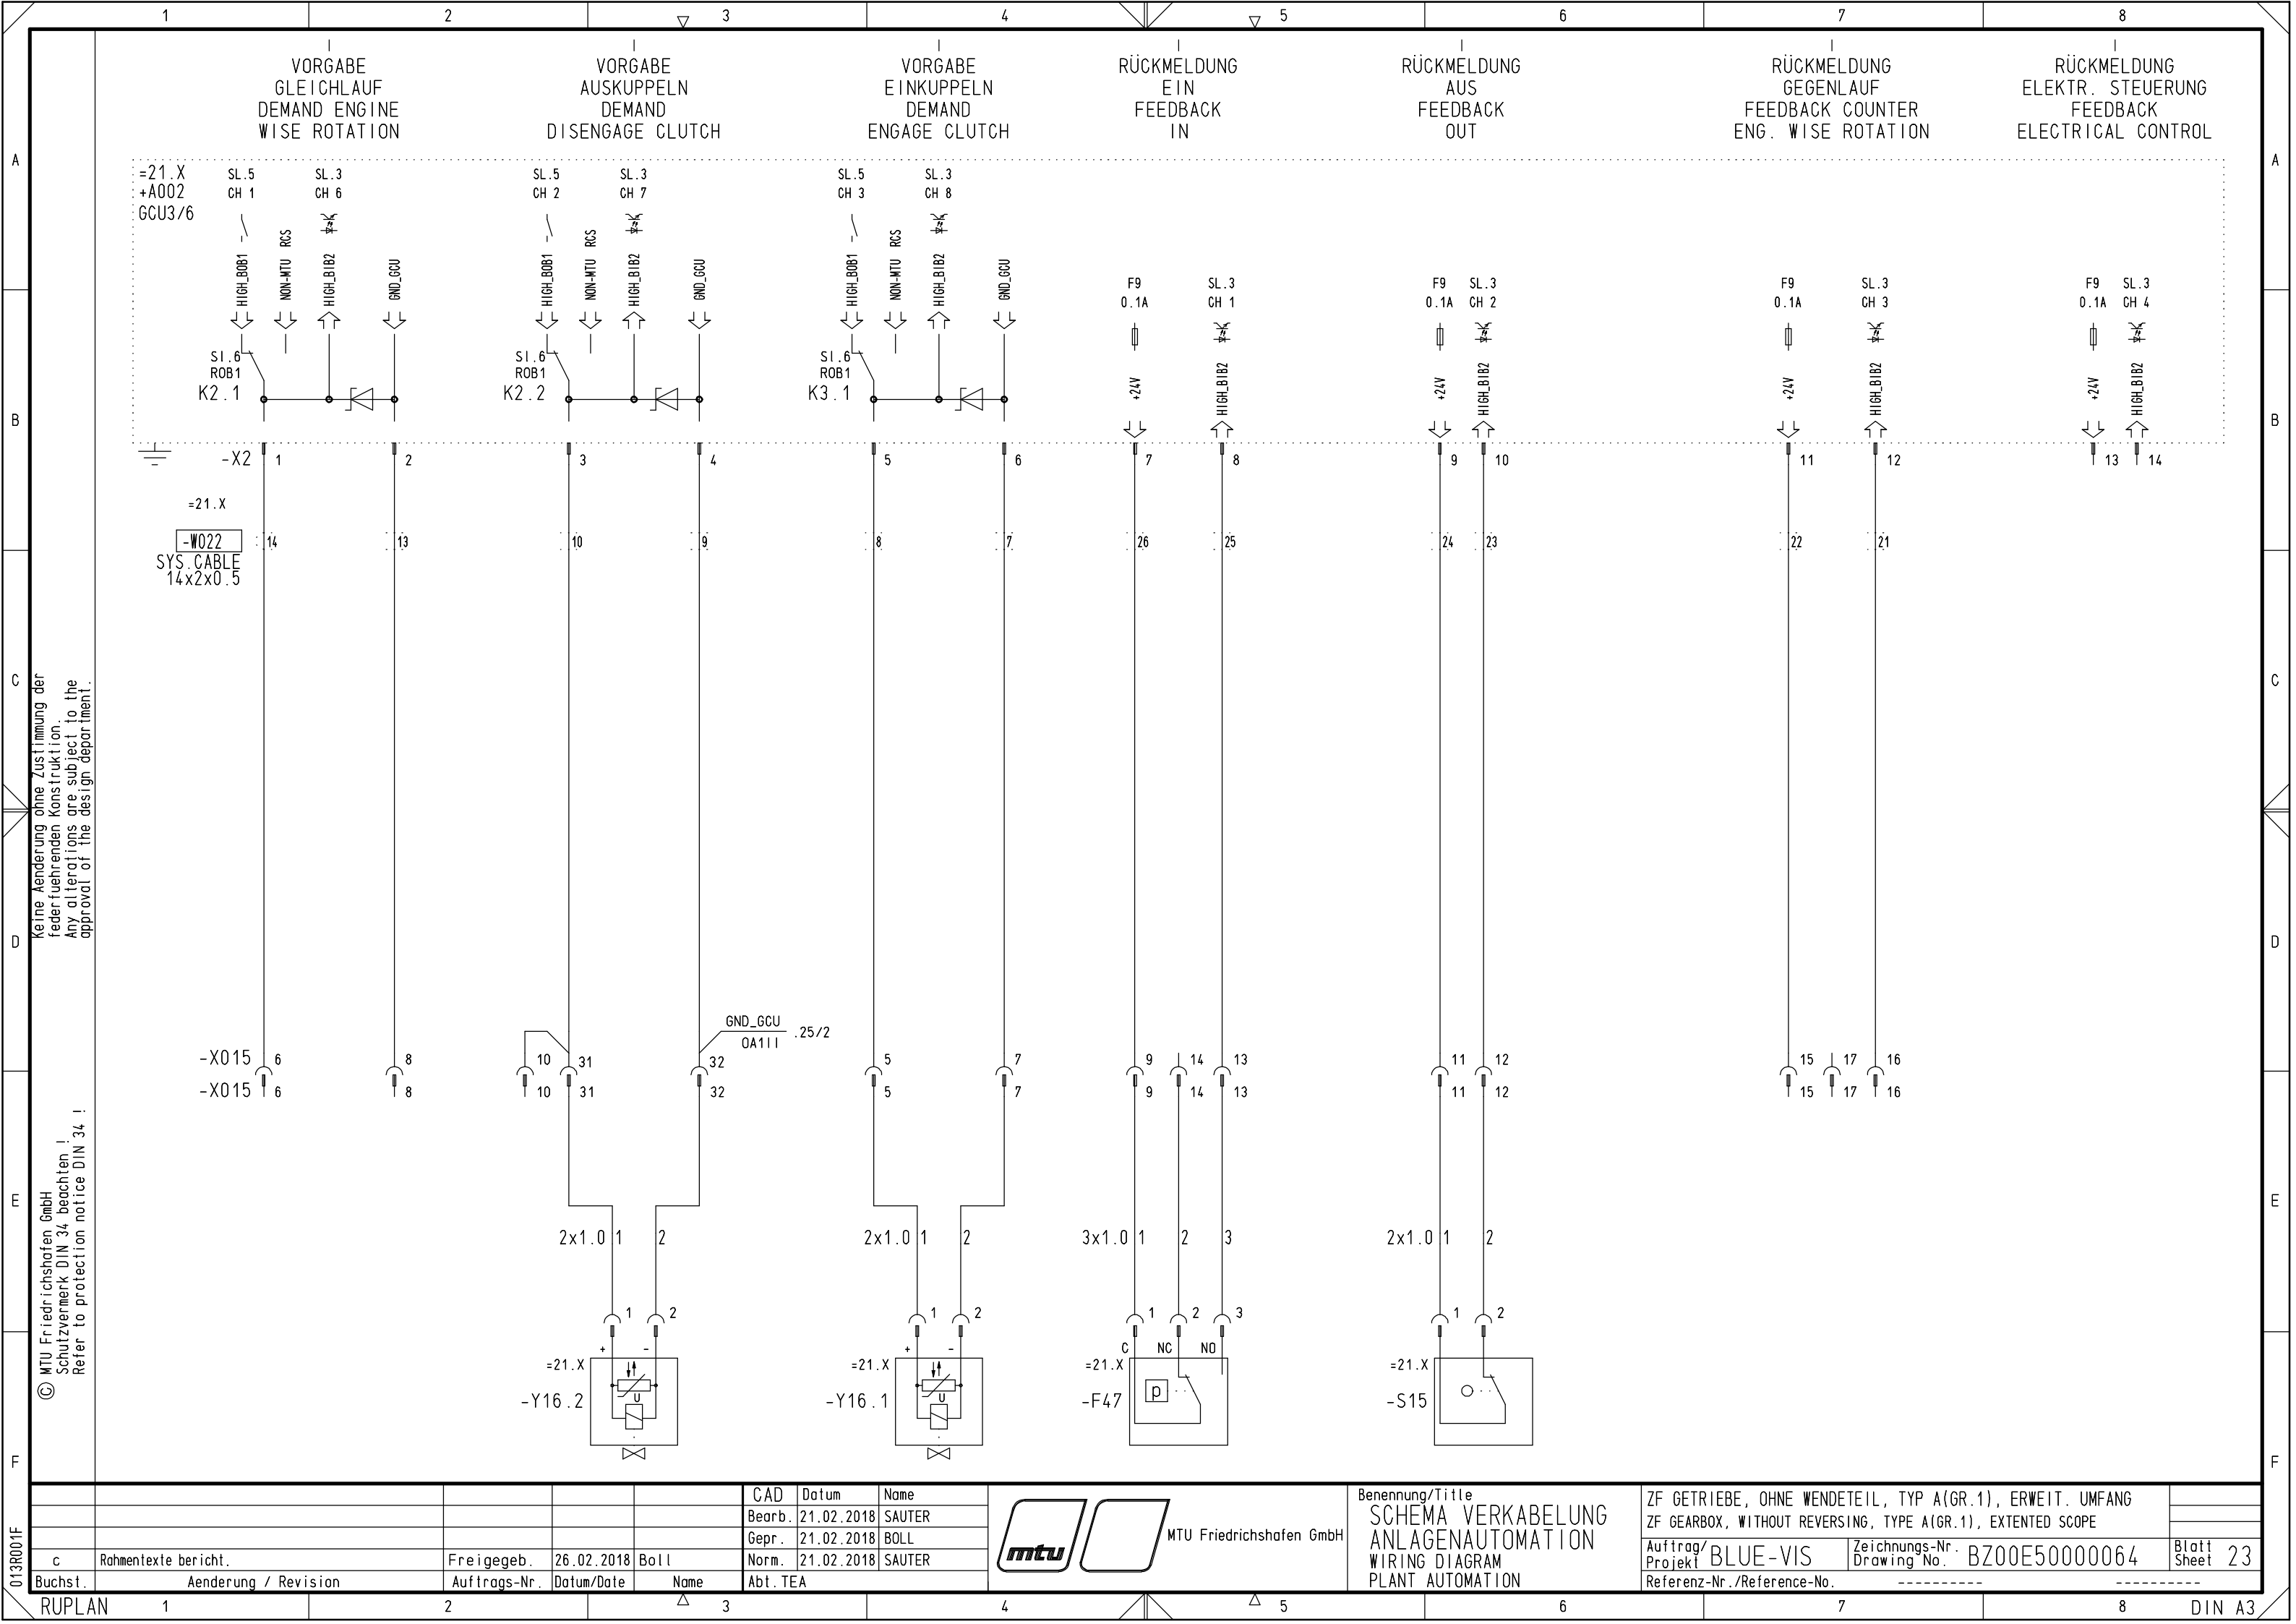



Keine Änderung ohne Zustimmung der
federführenden Konstruktion.
Any alterations are subject to the
approval of the design department.

© MTU Friedrichshafen GmbH
Schutzvermerk DIN 34 beachten !
Refer to protection notice DIN 34 !

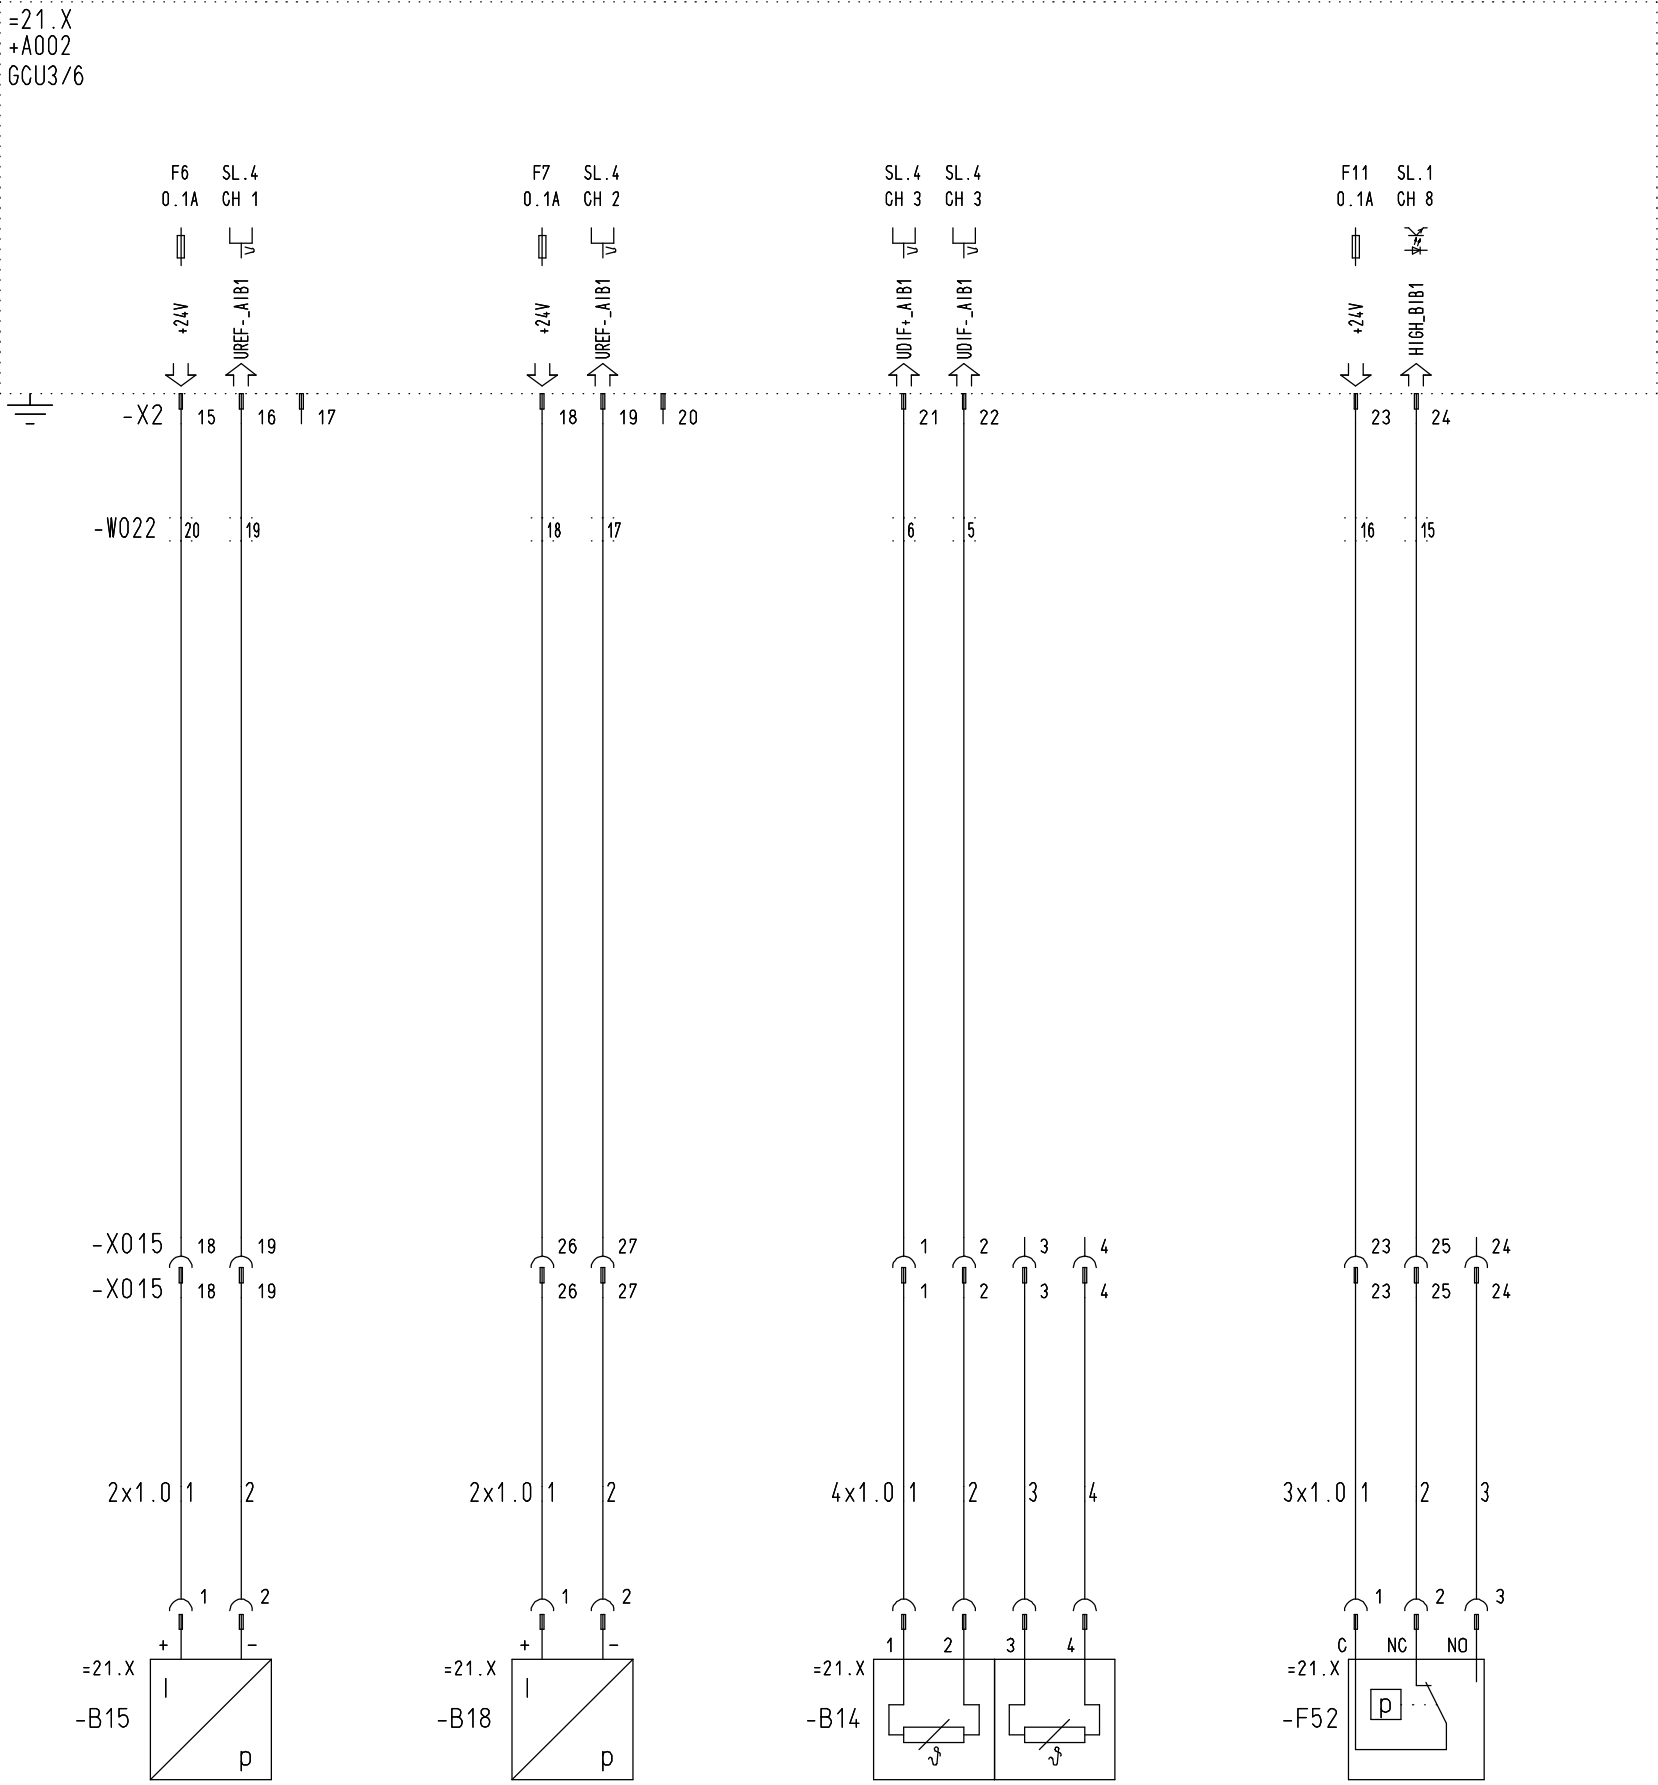

						CAD	Datum	Name	 MTU Friedrichshafen GmbH	Benennung/Title SCHEMA VERKABELUNG ANLAGENAUTOMATION WIRING DIAGRAM PLANT AUTOMATION	ZF GETRIEBE, OHNE WENDETEIL, TYP A(GR.1), ERWEIT. UMFANG			Blatt Sheet 24	
						Bearb.	21.02.2018	SAUTER			ZF GEARBOX, WITHOUT REVERSING, TYPE A(GR.1), EXTENDED SCOPE				
						Gepr.	21.02.2018	BOLL							
						Norm.	21.02.2018	SAUTER							
c	Rahmentexte bericht.		Freigegeb.	26.02.2018	Boll						Auftrag/ Projekt	BLUE-VIS	Zeichnungs-Nr. Drawing No.	BZ00E50000064	
Buchst.	Änderung / Revision		Auftrags-Nr.	Datum/Date	Name	Abt. TEA					Referenz-Nr./Reference-No.		-----		

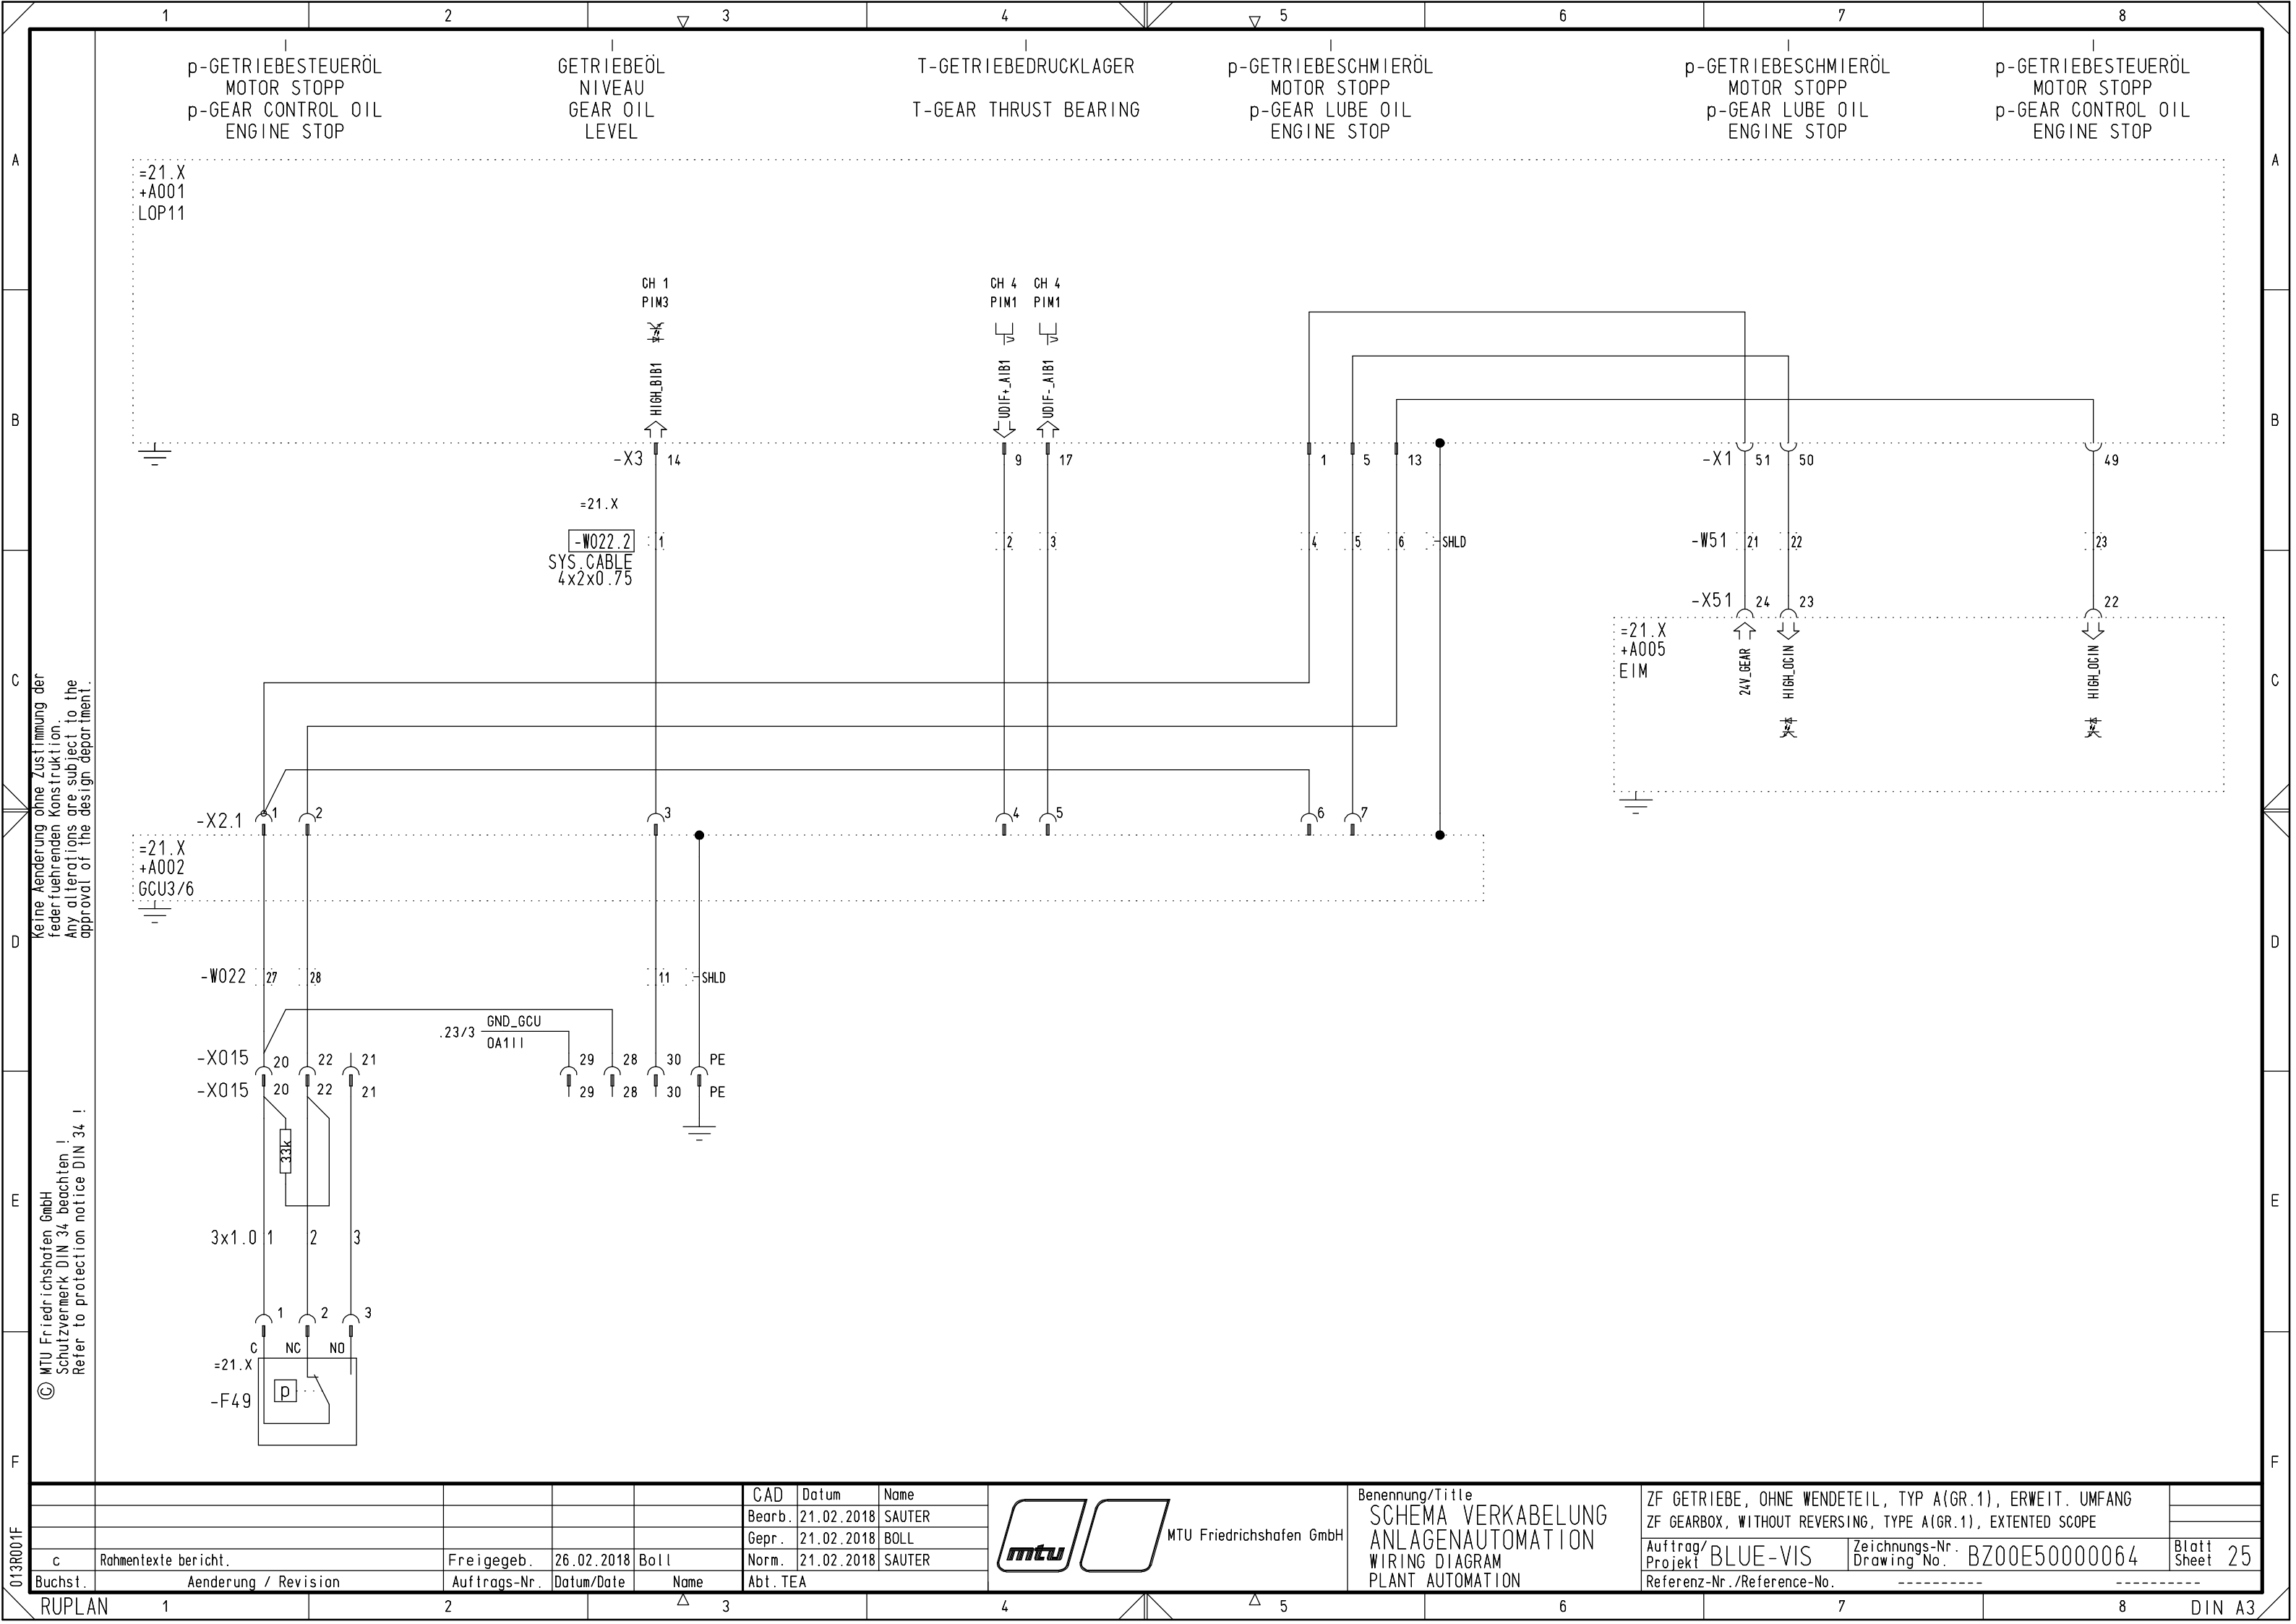


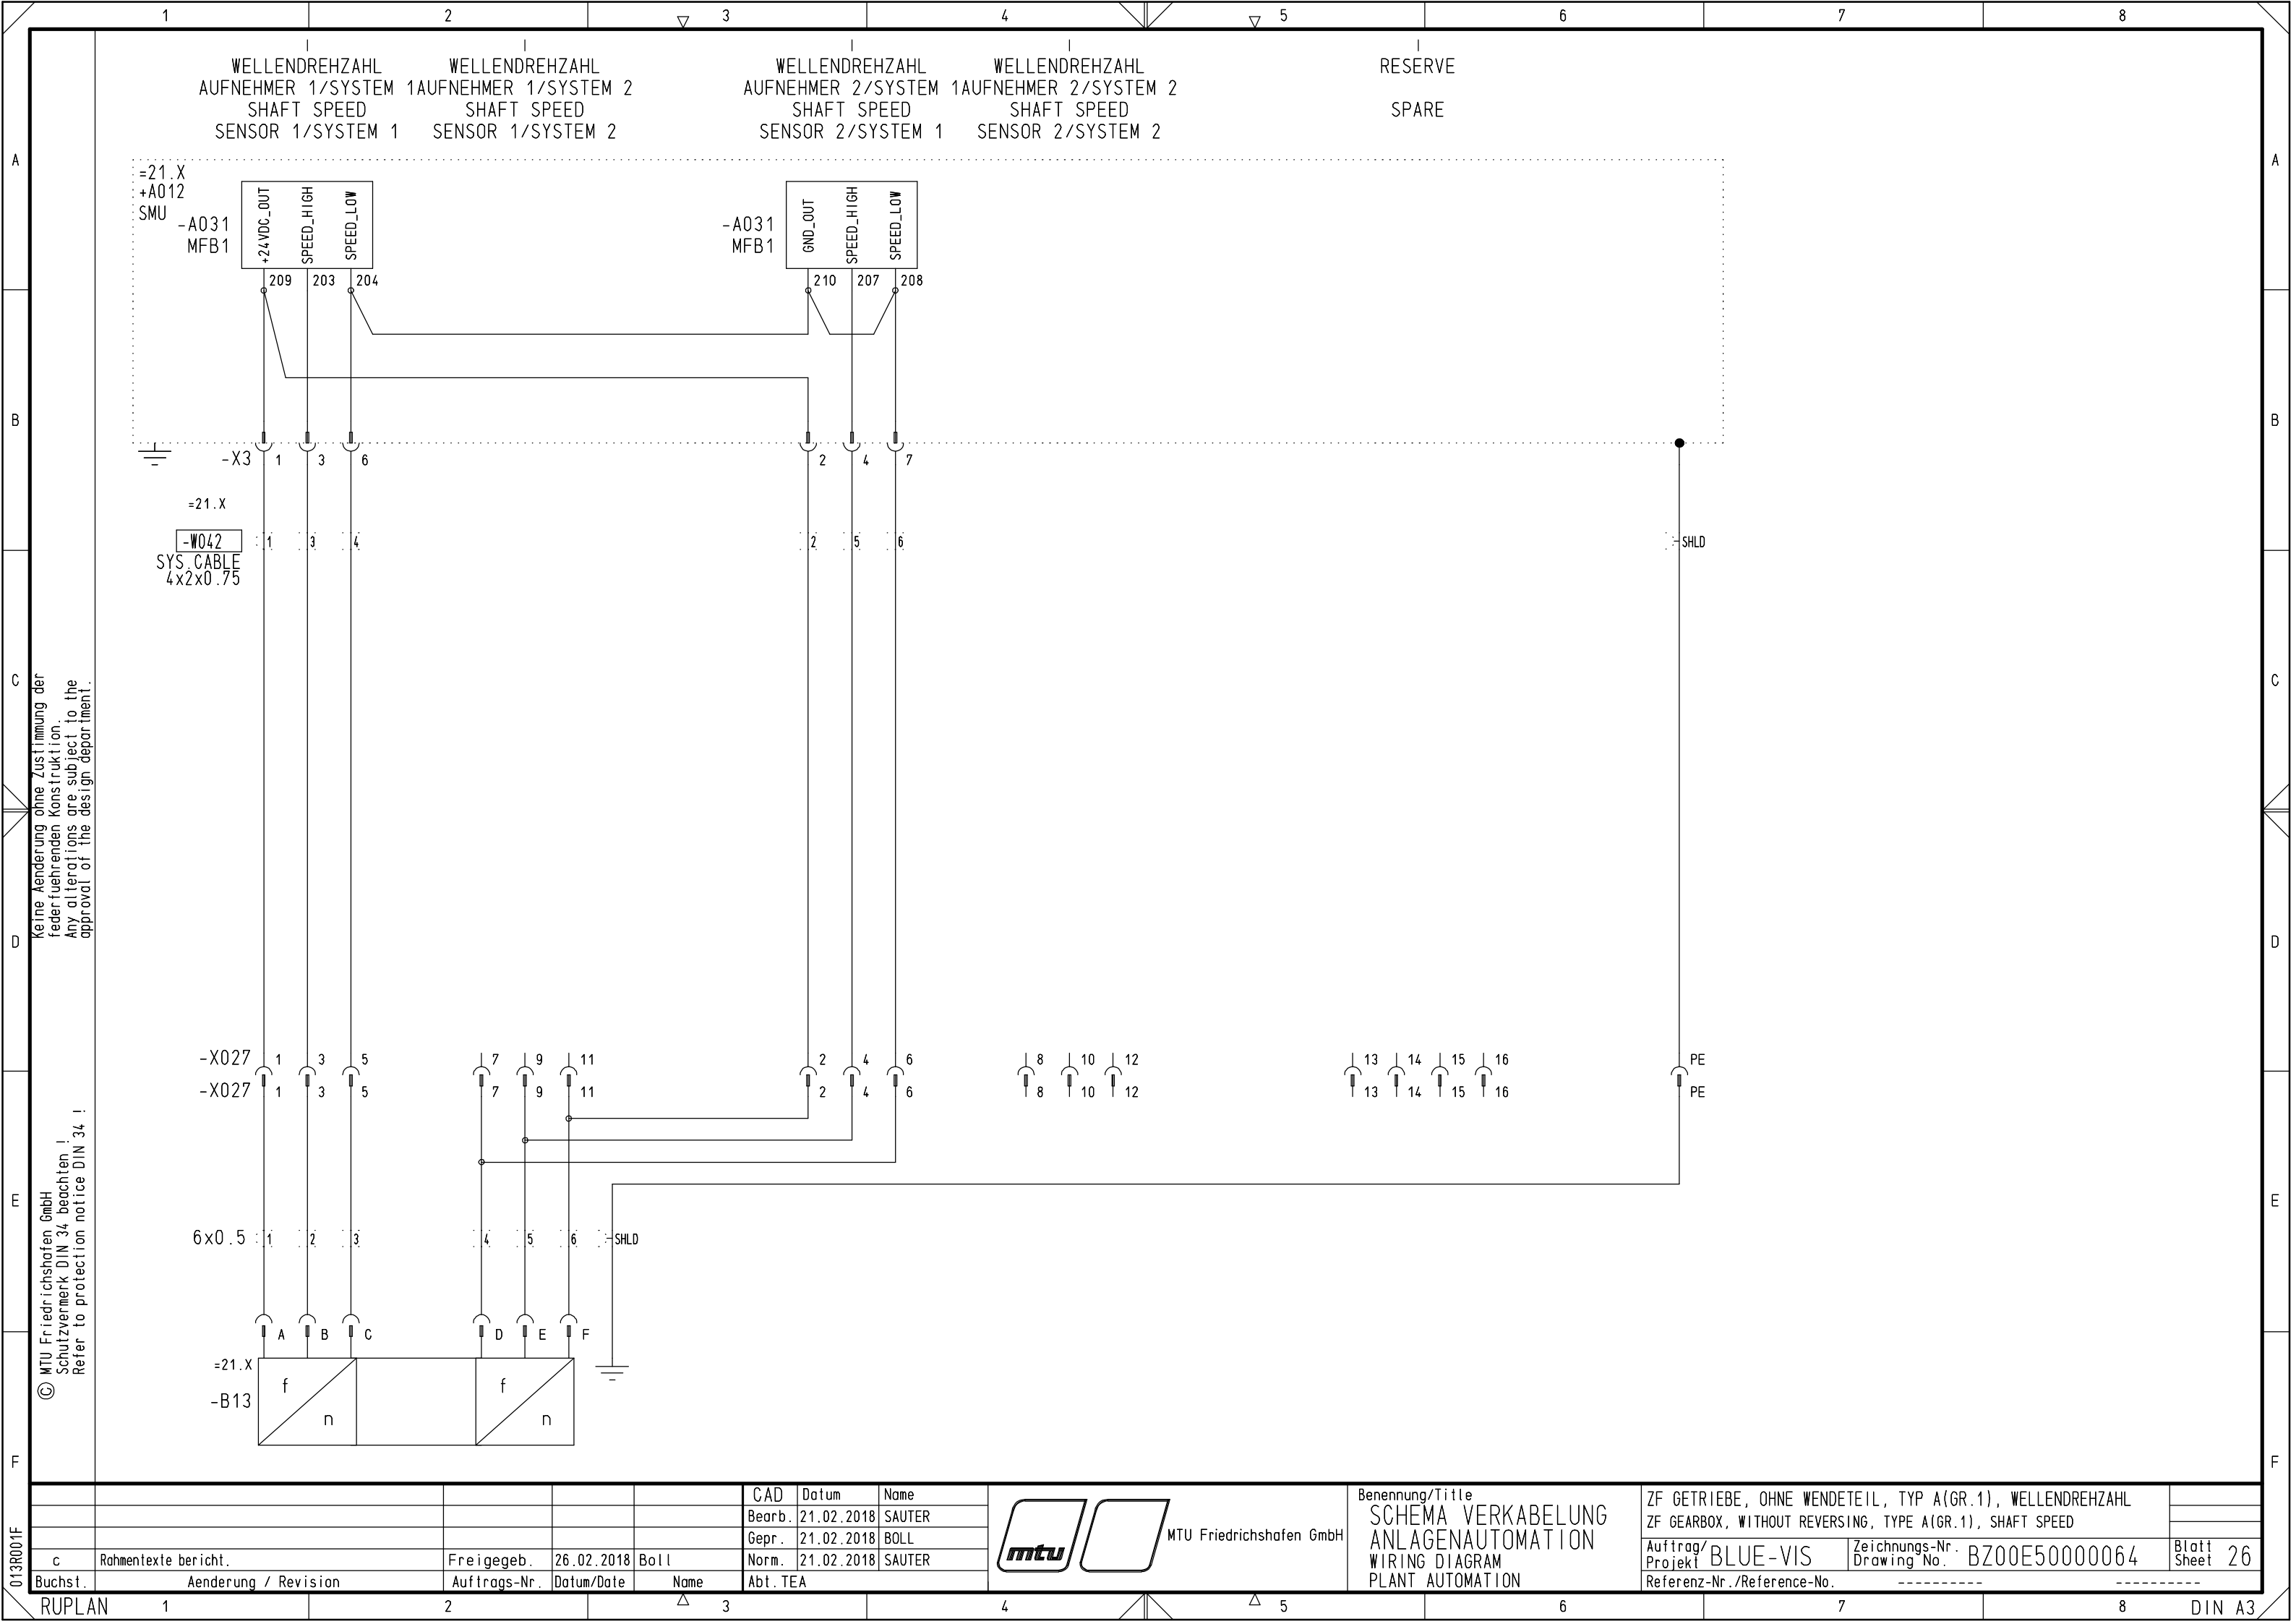

[illegible]

Keine Änderung ohne Zustimmung der
federführenden Konstruktion.
Any alterations are subject to the
approval of the design department.

© MTU Friedrichshafen GmbH
Schutzvermerk DIN 34 beachten !
Refer to protection notice DIN 34 !

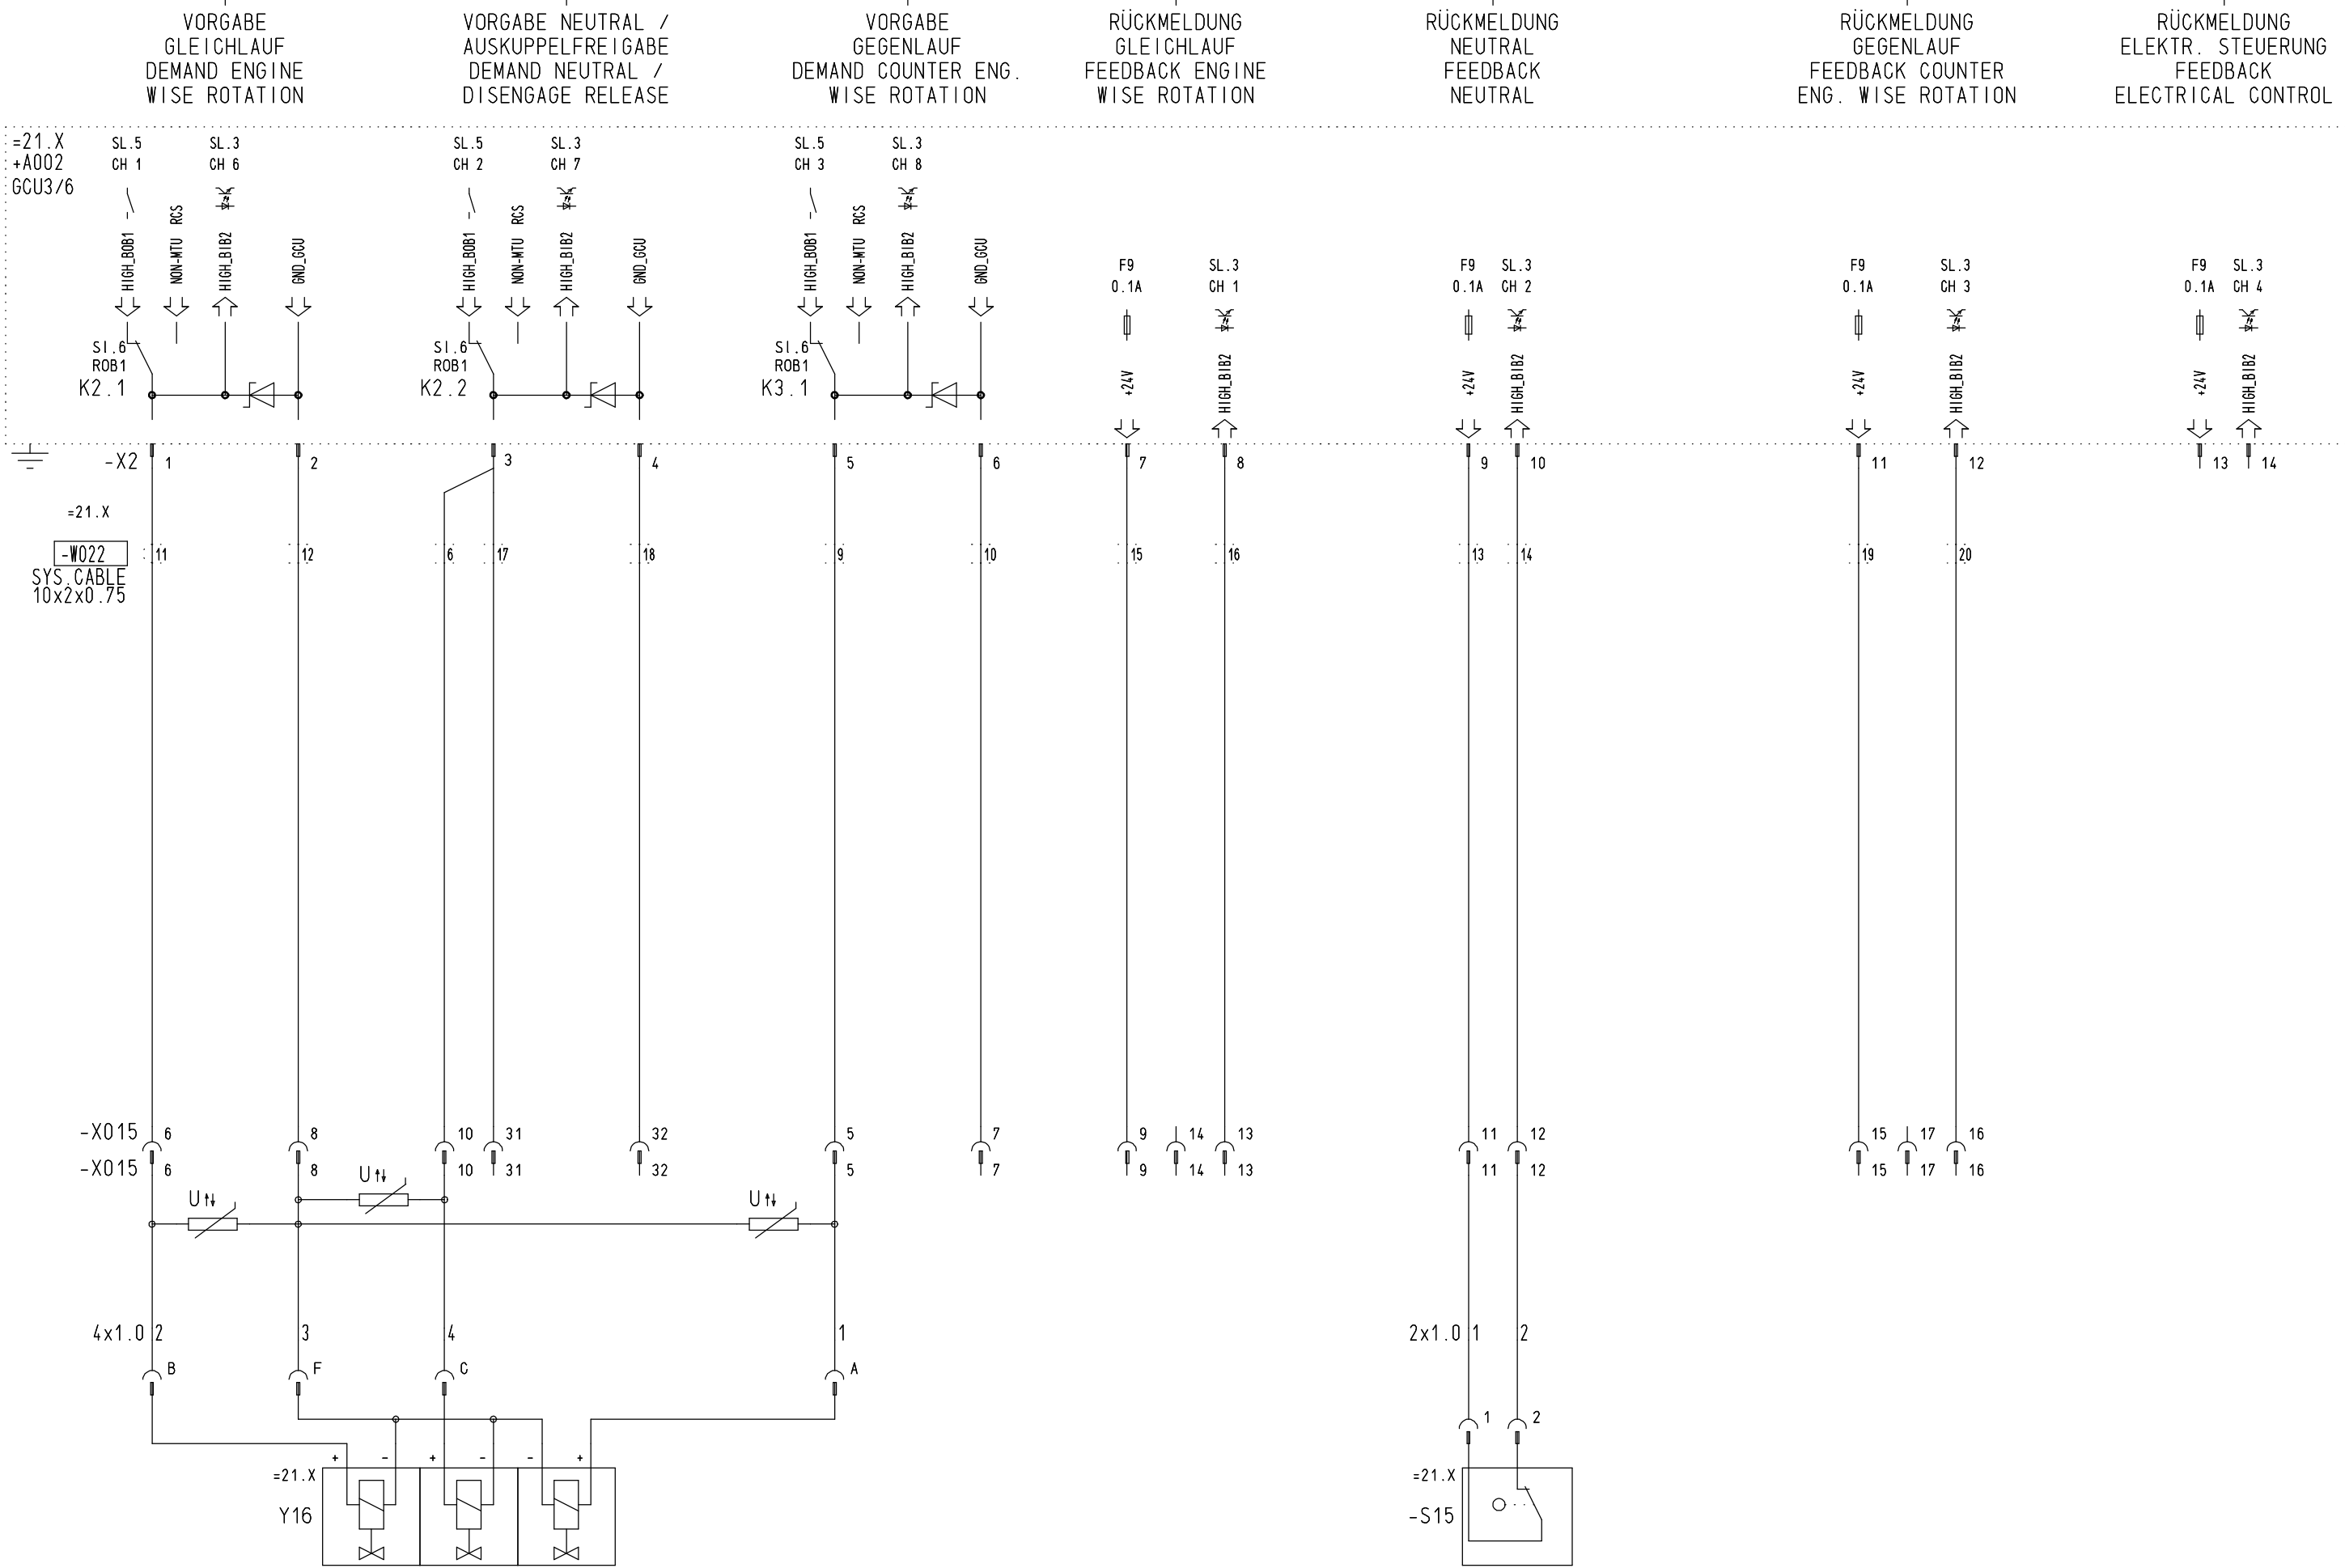


					CAD	Datum	Name
					Bearb.	21.02.2018	SAUTER
					Gedr.	21.02.2018	BOLL
					Norm.	21.02.2018	SAUTER
c	Rahmentexte bericht.	Freigegeb.	26.02.2018	Boll	Abt. TEA		
Buchst.	Aenderung / Revision	Auftrags-Nr.	Datum/Date	Name			



MTU Friedrichshafen GmbH

Benennung/Title
SCHEMA VERKABELUNG
ANLAGENAUTOMATION
WIRING DIAGRAM
PLANT AUTOMATION

ZF GETRIEBE, MIT WENDETEIL, TYP A(GR.2), GRUNDUMFANG ZF GEARBOX, WITH REVERSING, TYPE A(GR.2), BASIC SCOPE			
Auftrag/ Projekt	BLUE-VIS	Zeichnungs-Nr. Drawing No.	BZ00E50000064
Referenz-Nr./Reference-No.		-----	
			Blatt Sheet 28

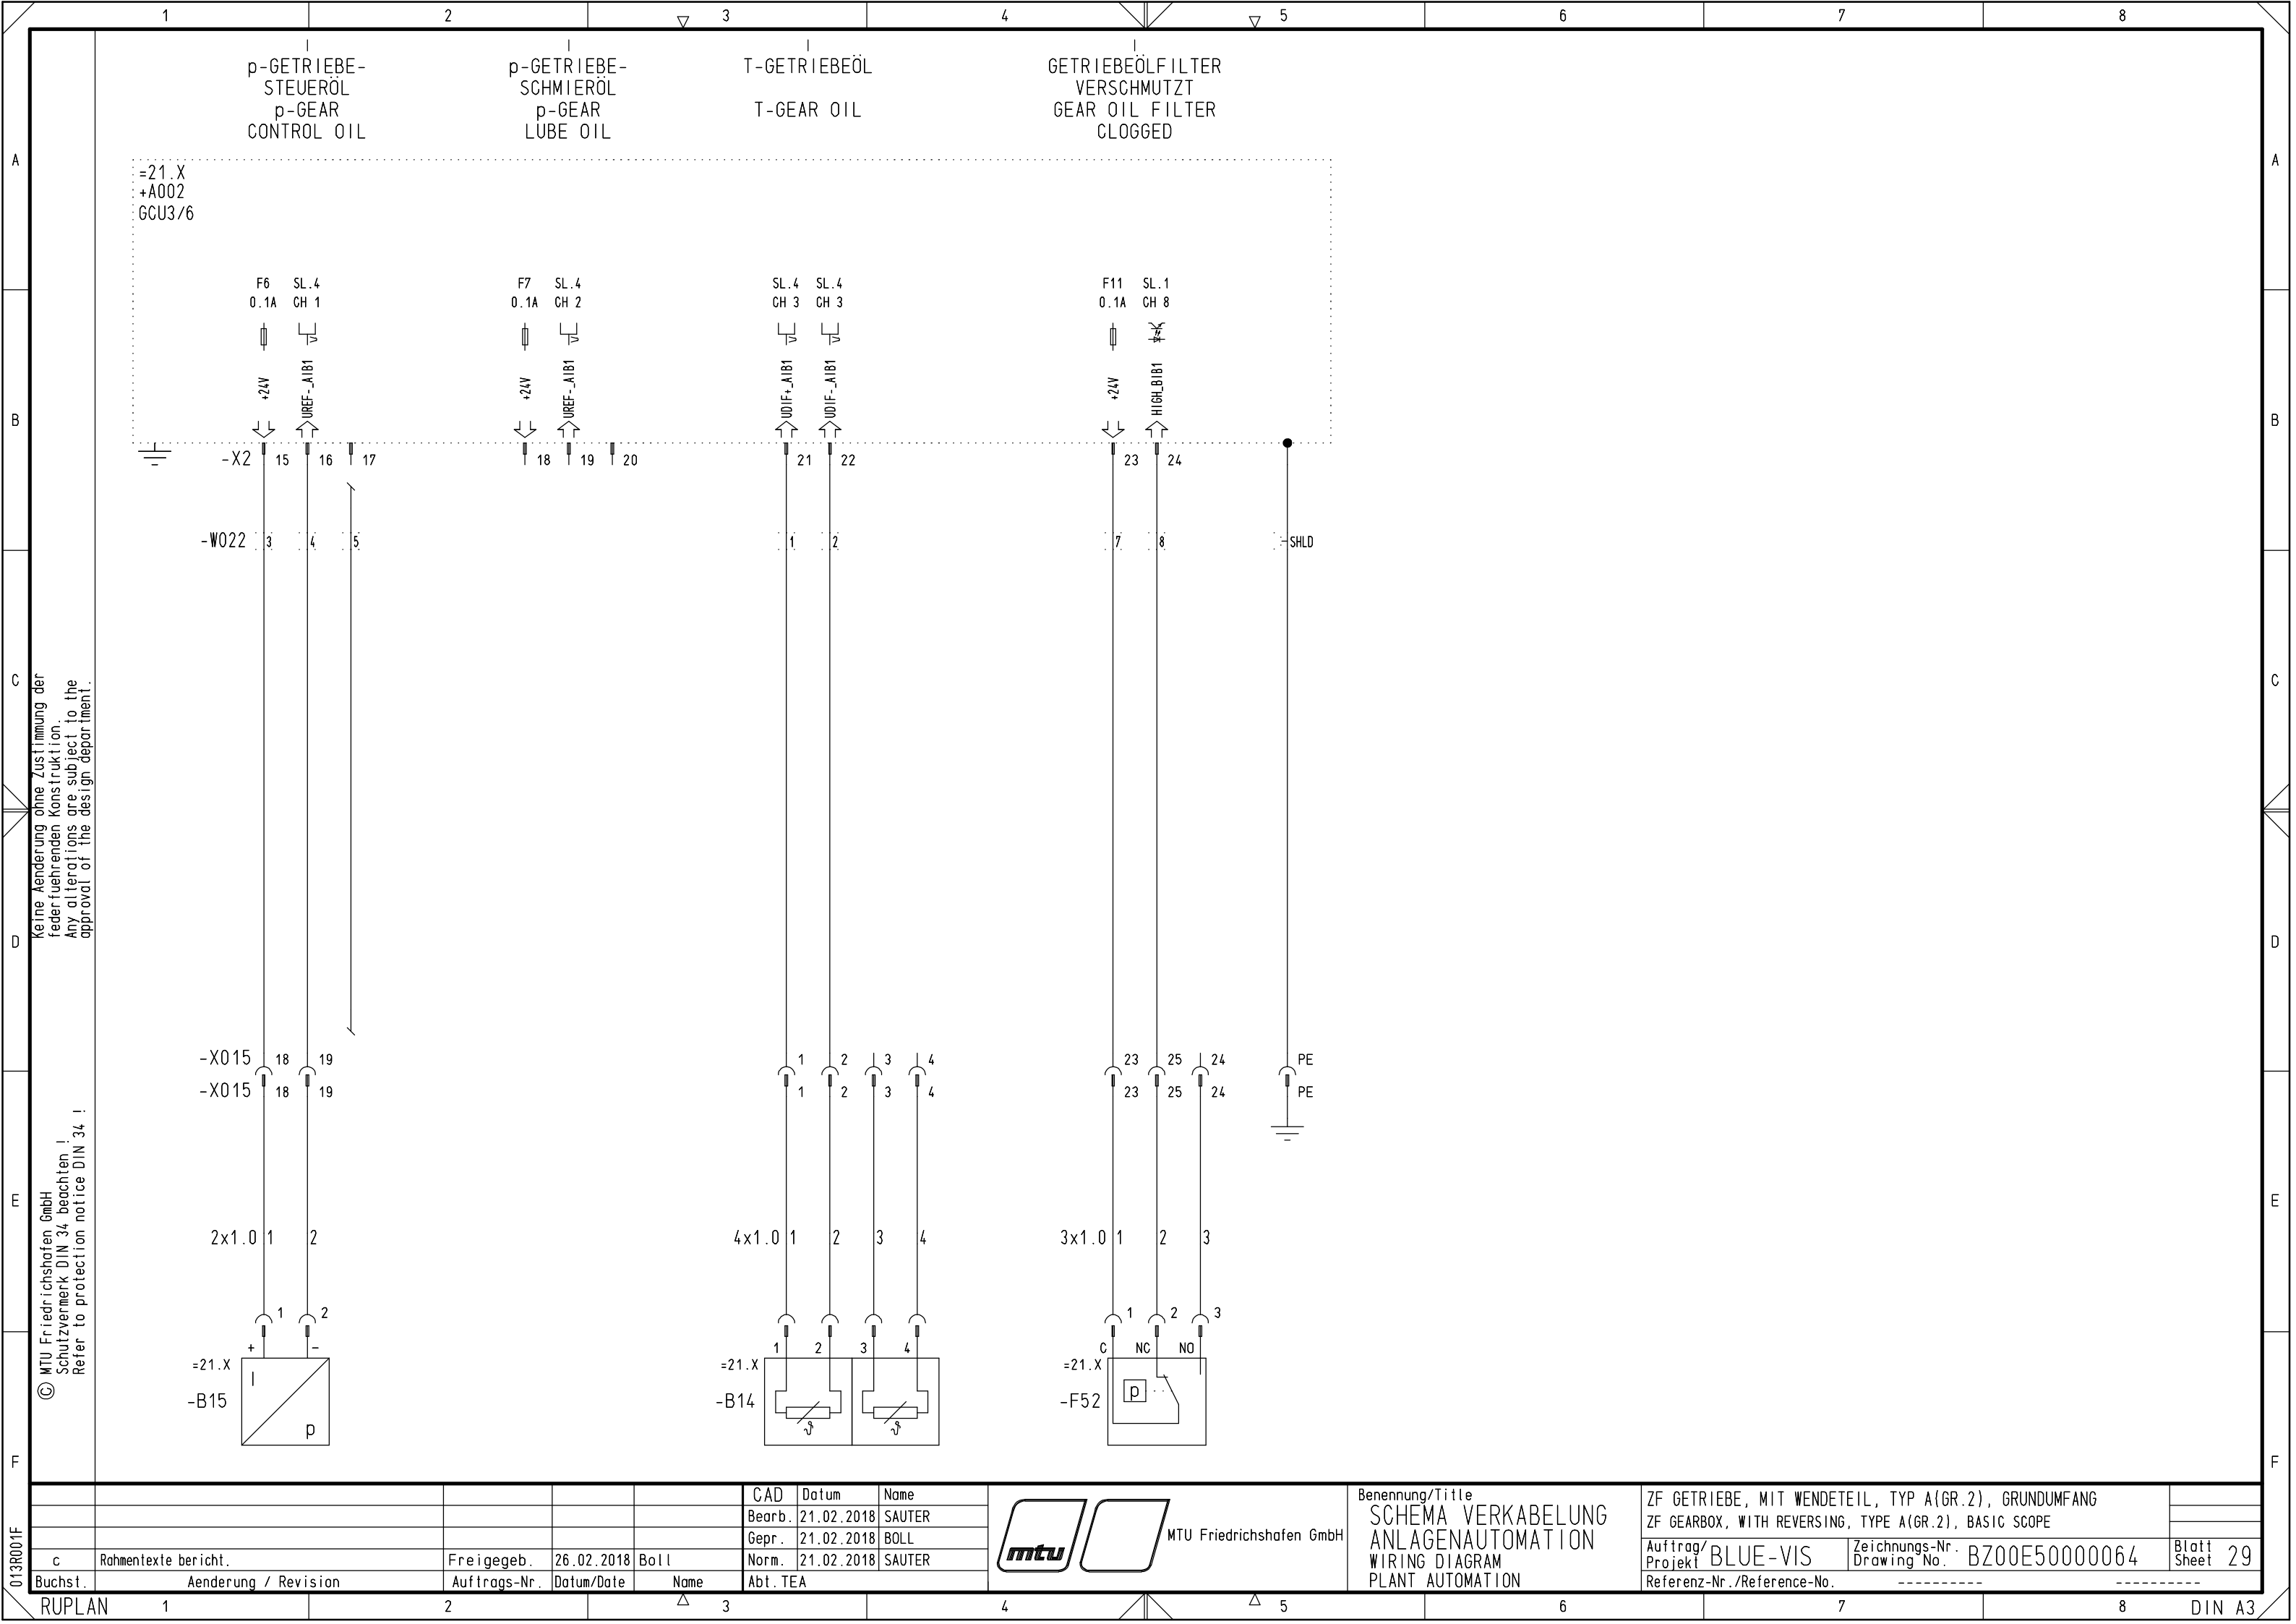

Keine Änderung ohne Zustimmung der
federführenden Konstruktion.
Any alterations are subject to the
approval of the design department.

© MTU Friedrichshafen GmbH
Schutzvermerk DIN 34 beachten !
Refer to protection notice DIN 34 !

013R001F
c
Buchst.
Rahmentexte bericht.
Änderung / Revision

Freigegeb.
26.02.2018
Boll
Auftrags-Nr.
Datum/Date
Name

CAD
Datum
Name
Bearb.
21.02.2018
SAUTER
Gepr.
21.02.2018
BOLL
Norm.
21.02.2018
SAUTER
Abt. TEA





MTU Friedrichshafen GmbH


Benennung/Title
SCHEMA VERKABELUNG
ANLAGENAUTOMATION
WIRING DIAGRAM
PLANT AUTOMATION

ZF GETRIEBE, MIT WENDETEIL, TYP A(GR.2), ERWEIT. UMFANG
ZF GEARBOX, WITH REVERSING, TYPE A(GR.2), EXTENDED SCOPE
Auftrag/
Projekt
BLUE-VIS
Zeichnungs-Nr.
Drawing No.
BZ00E50000064
Referenz-Nr./Reference-No.

Blatt
Sheet
30

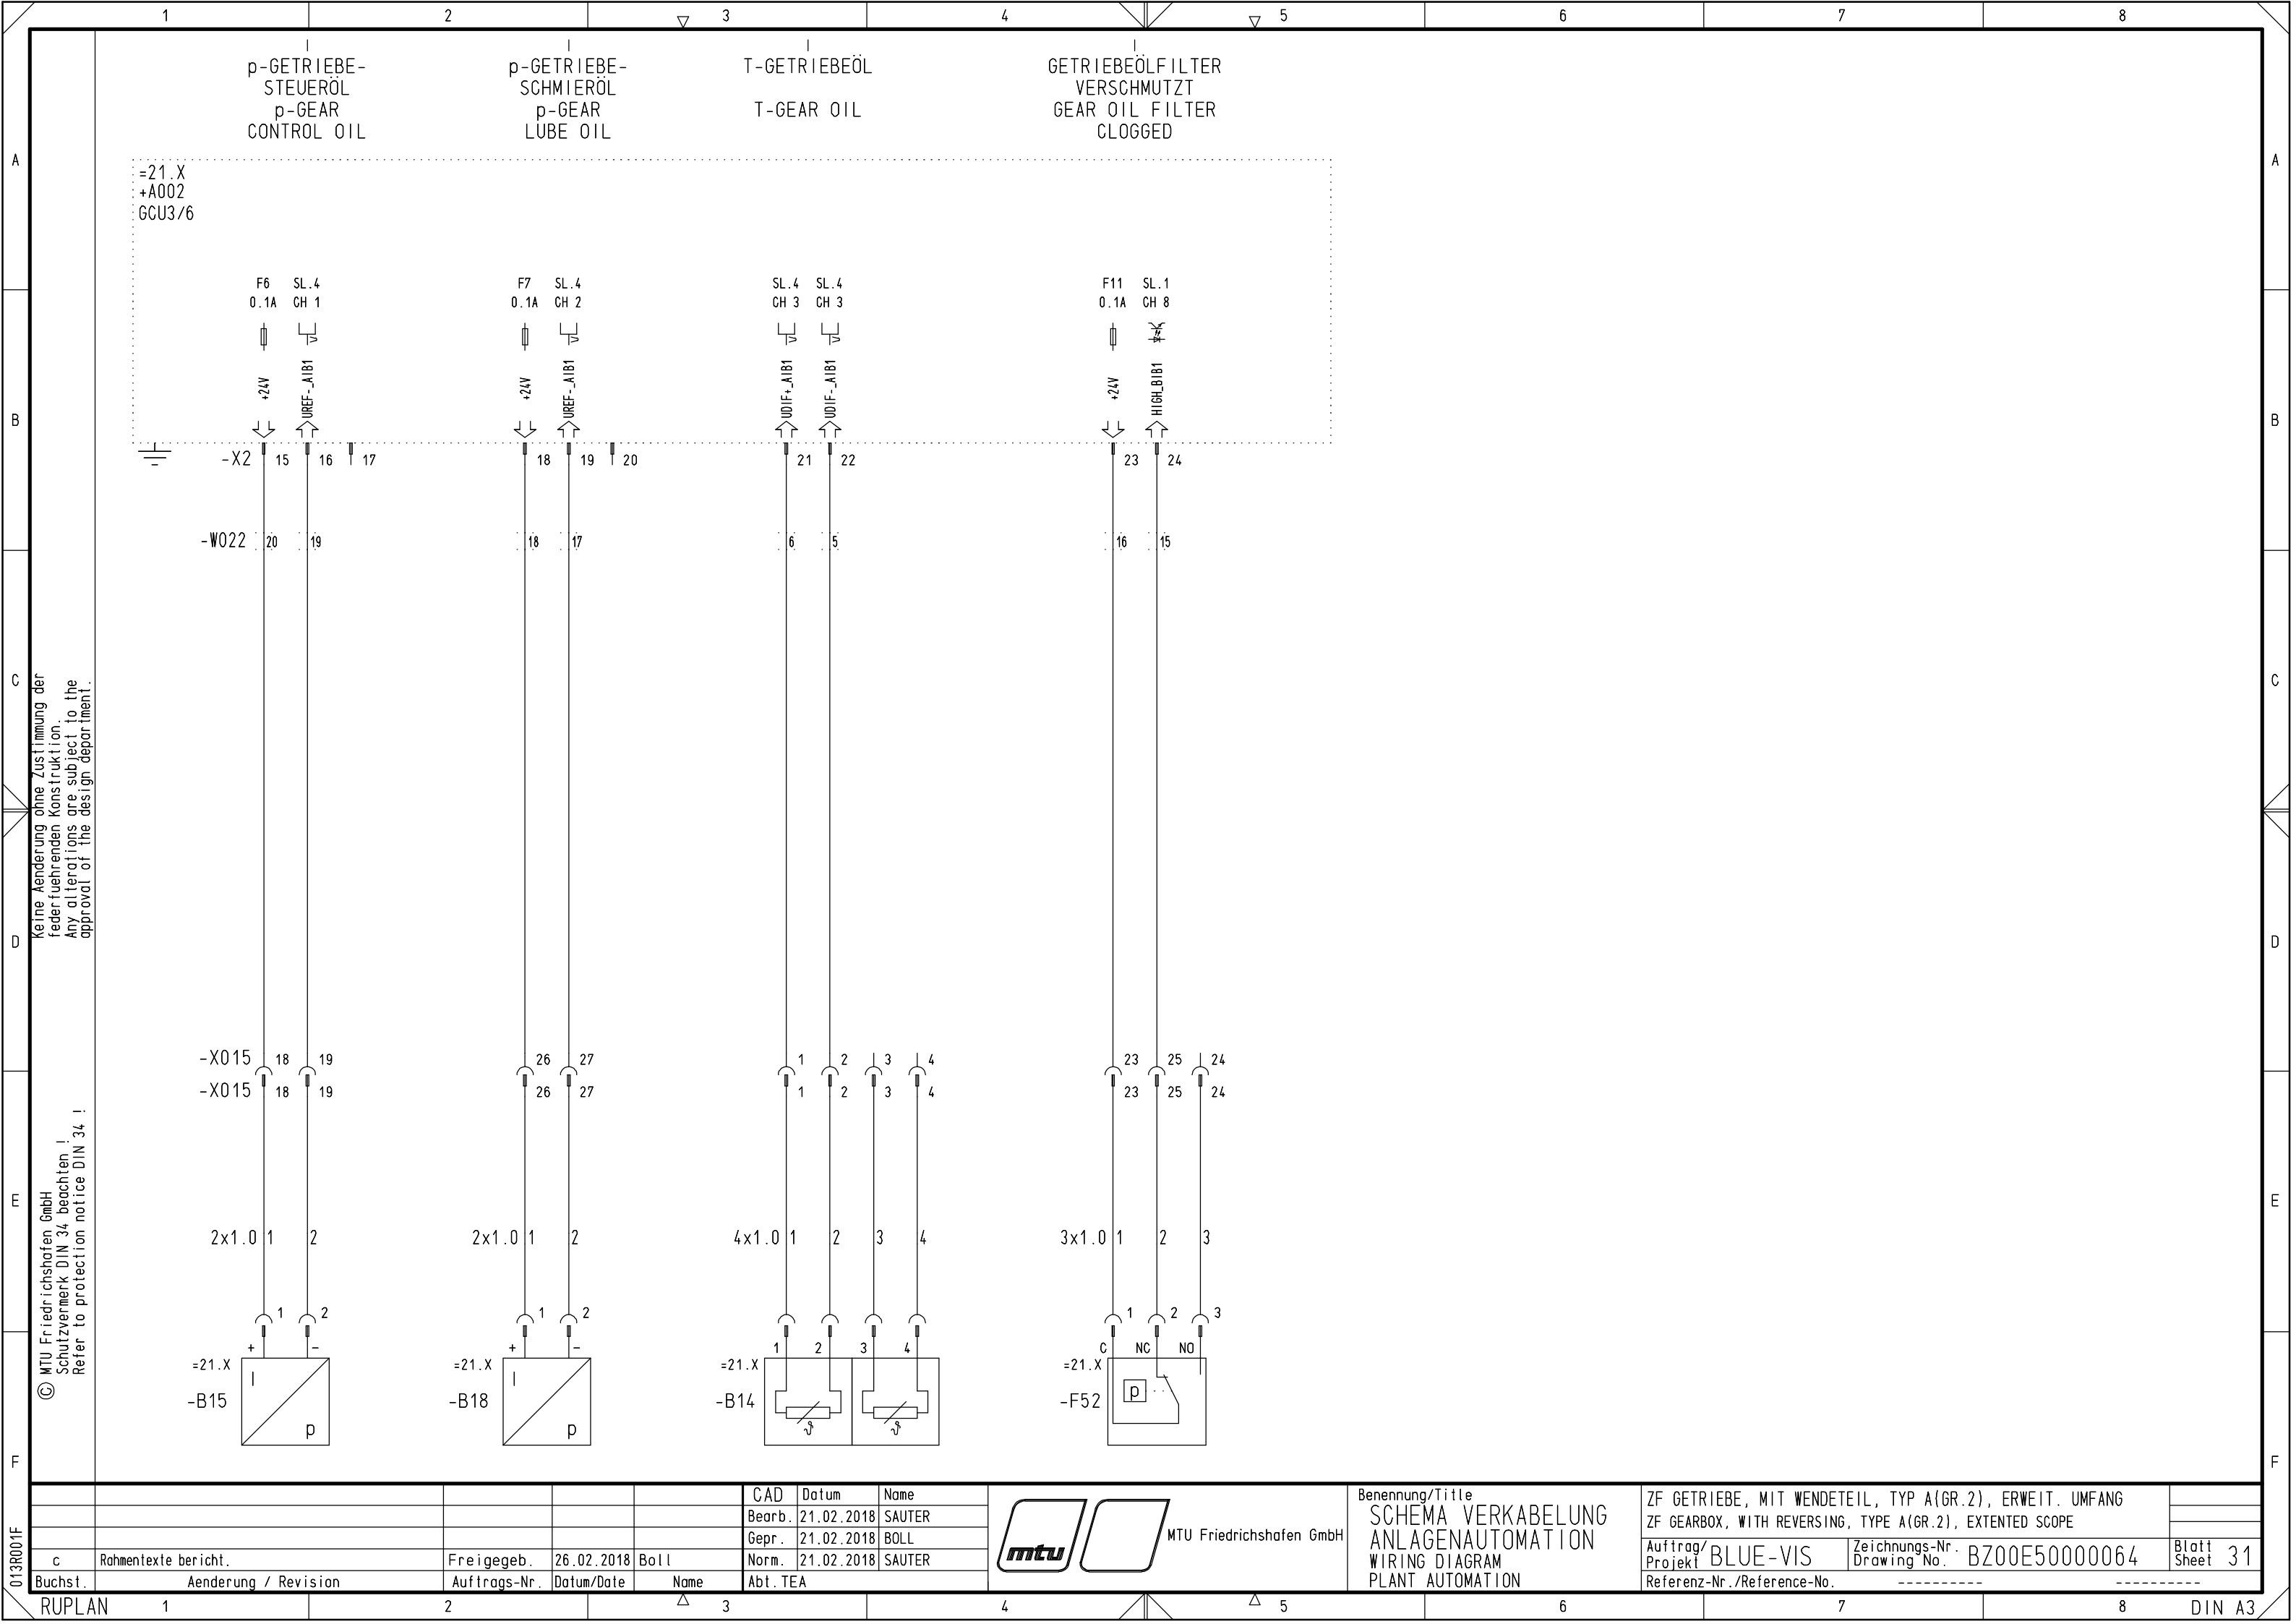

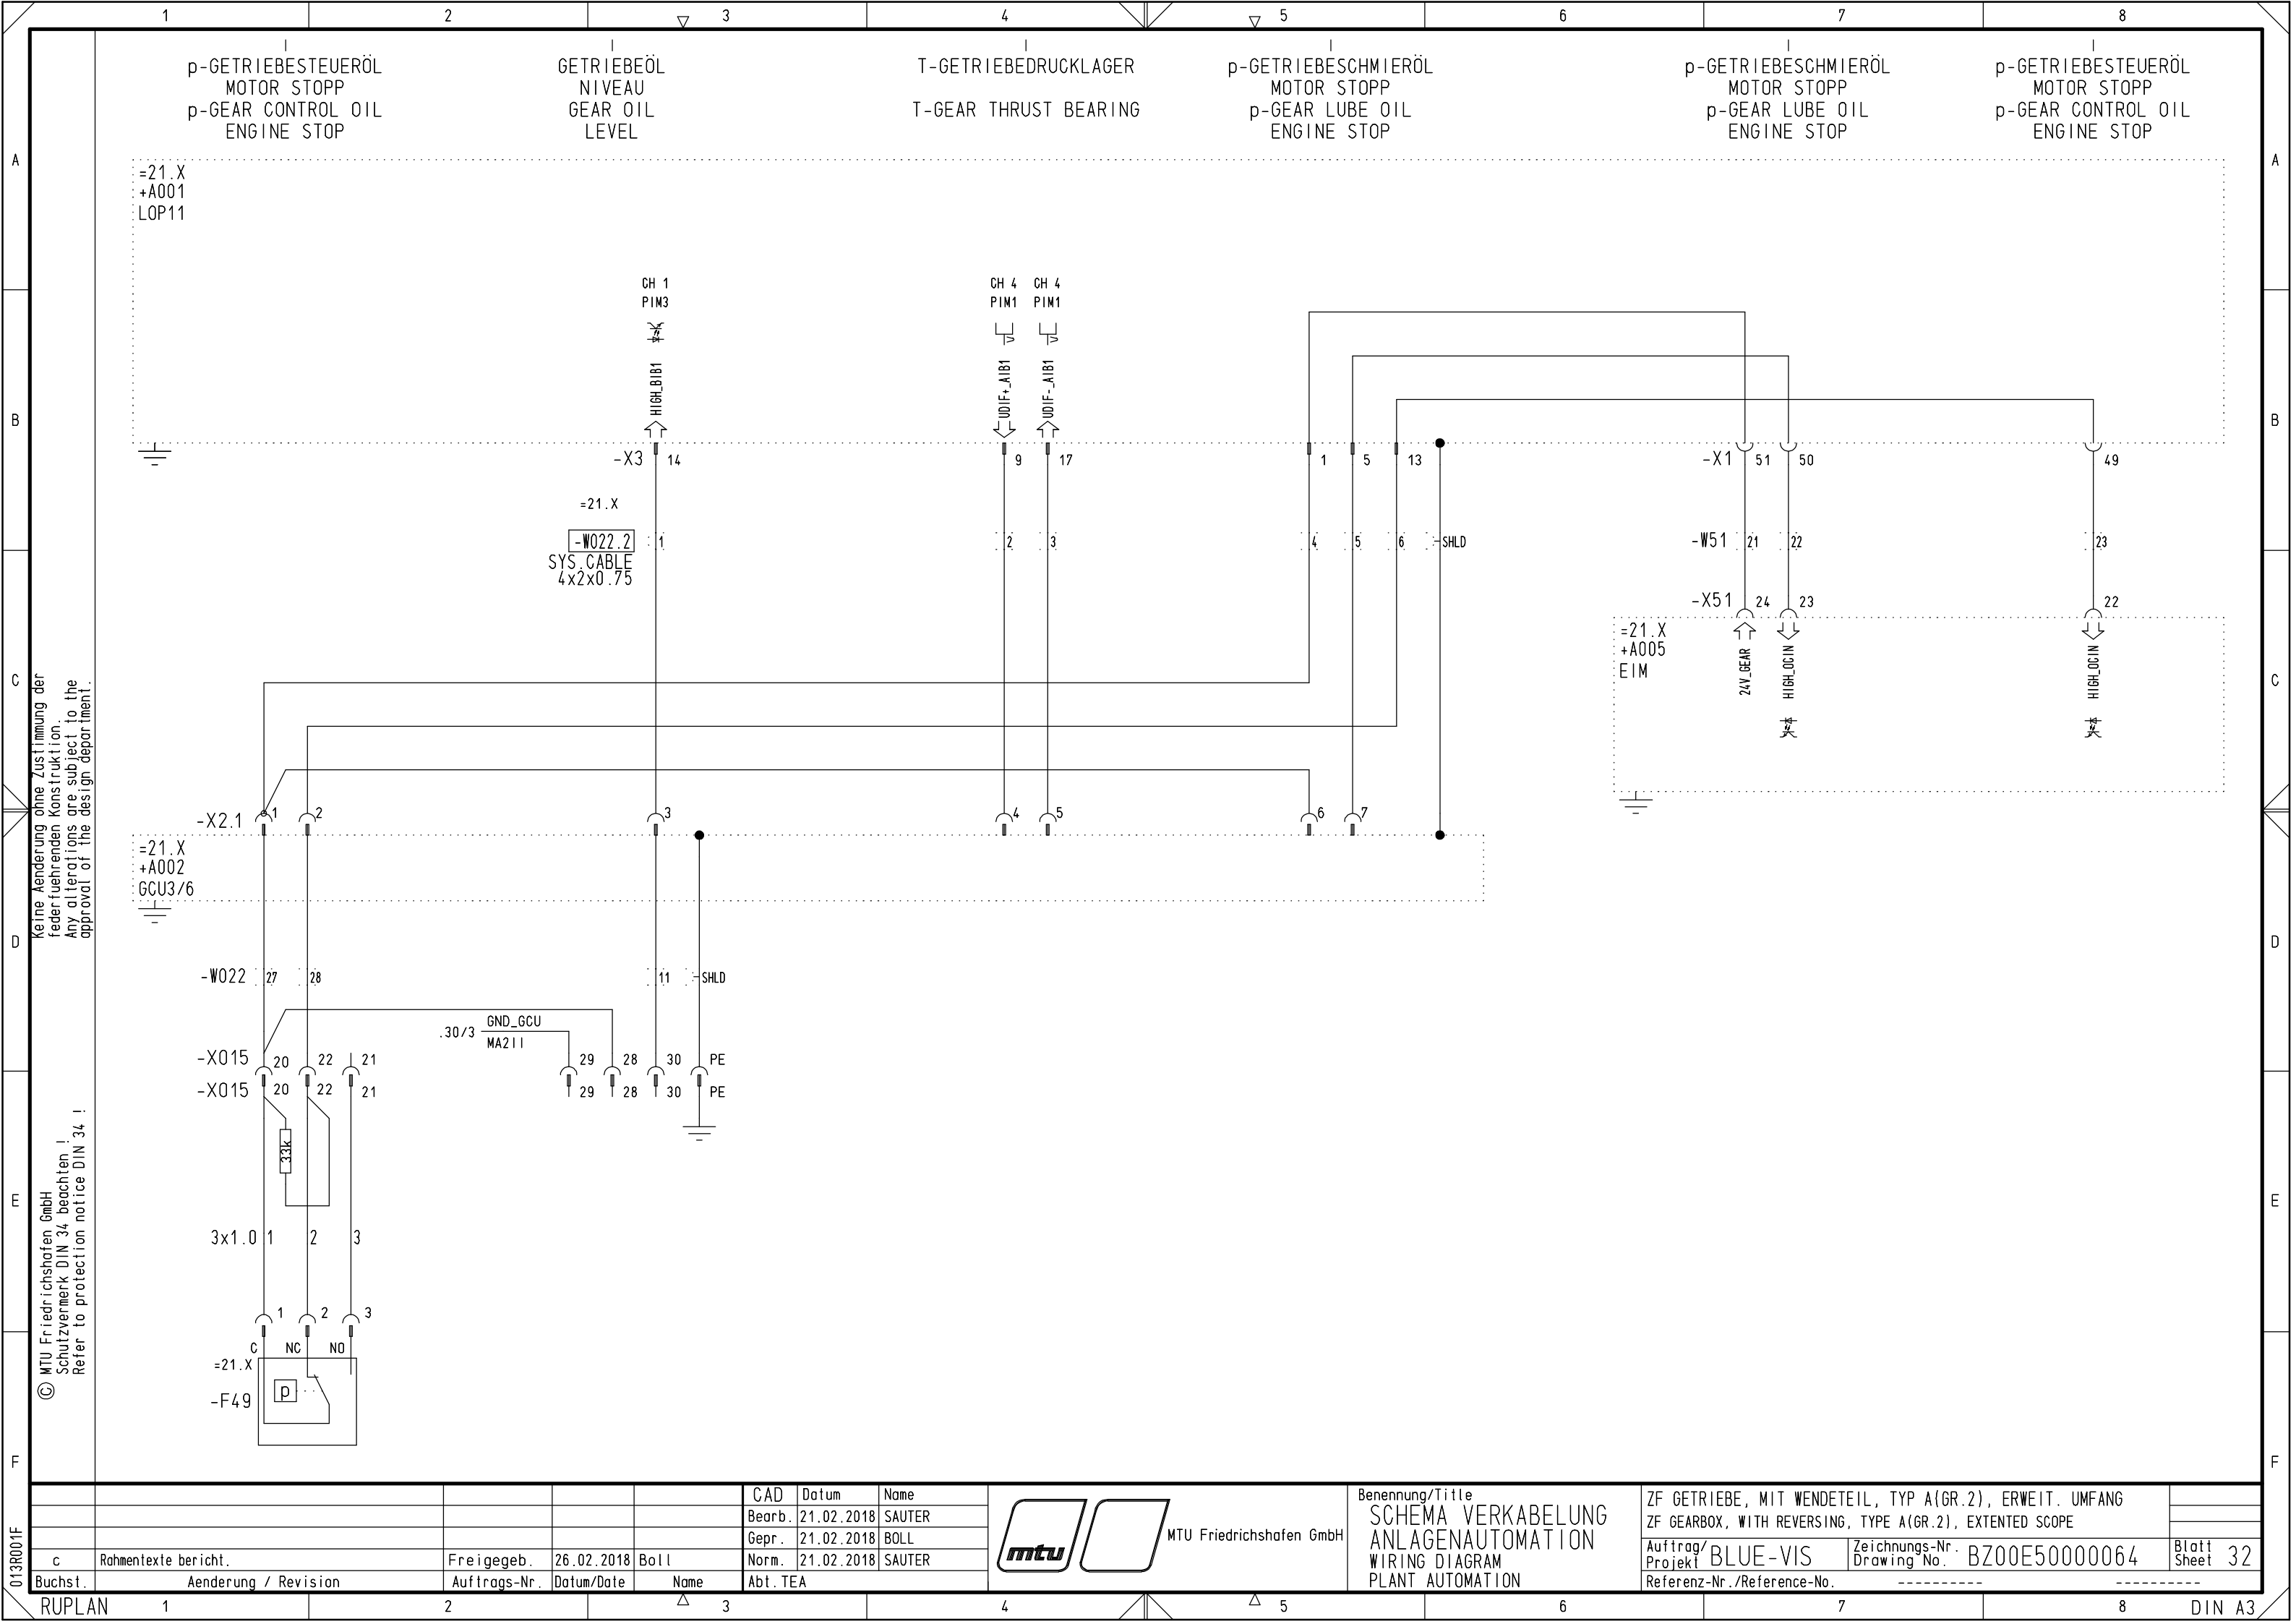

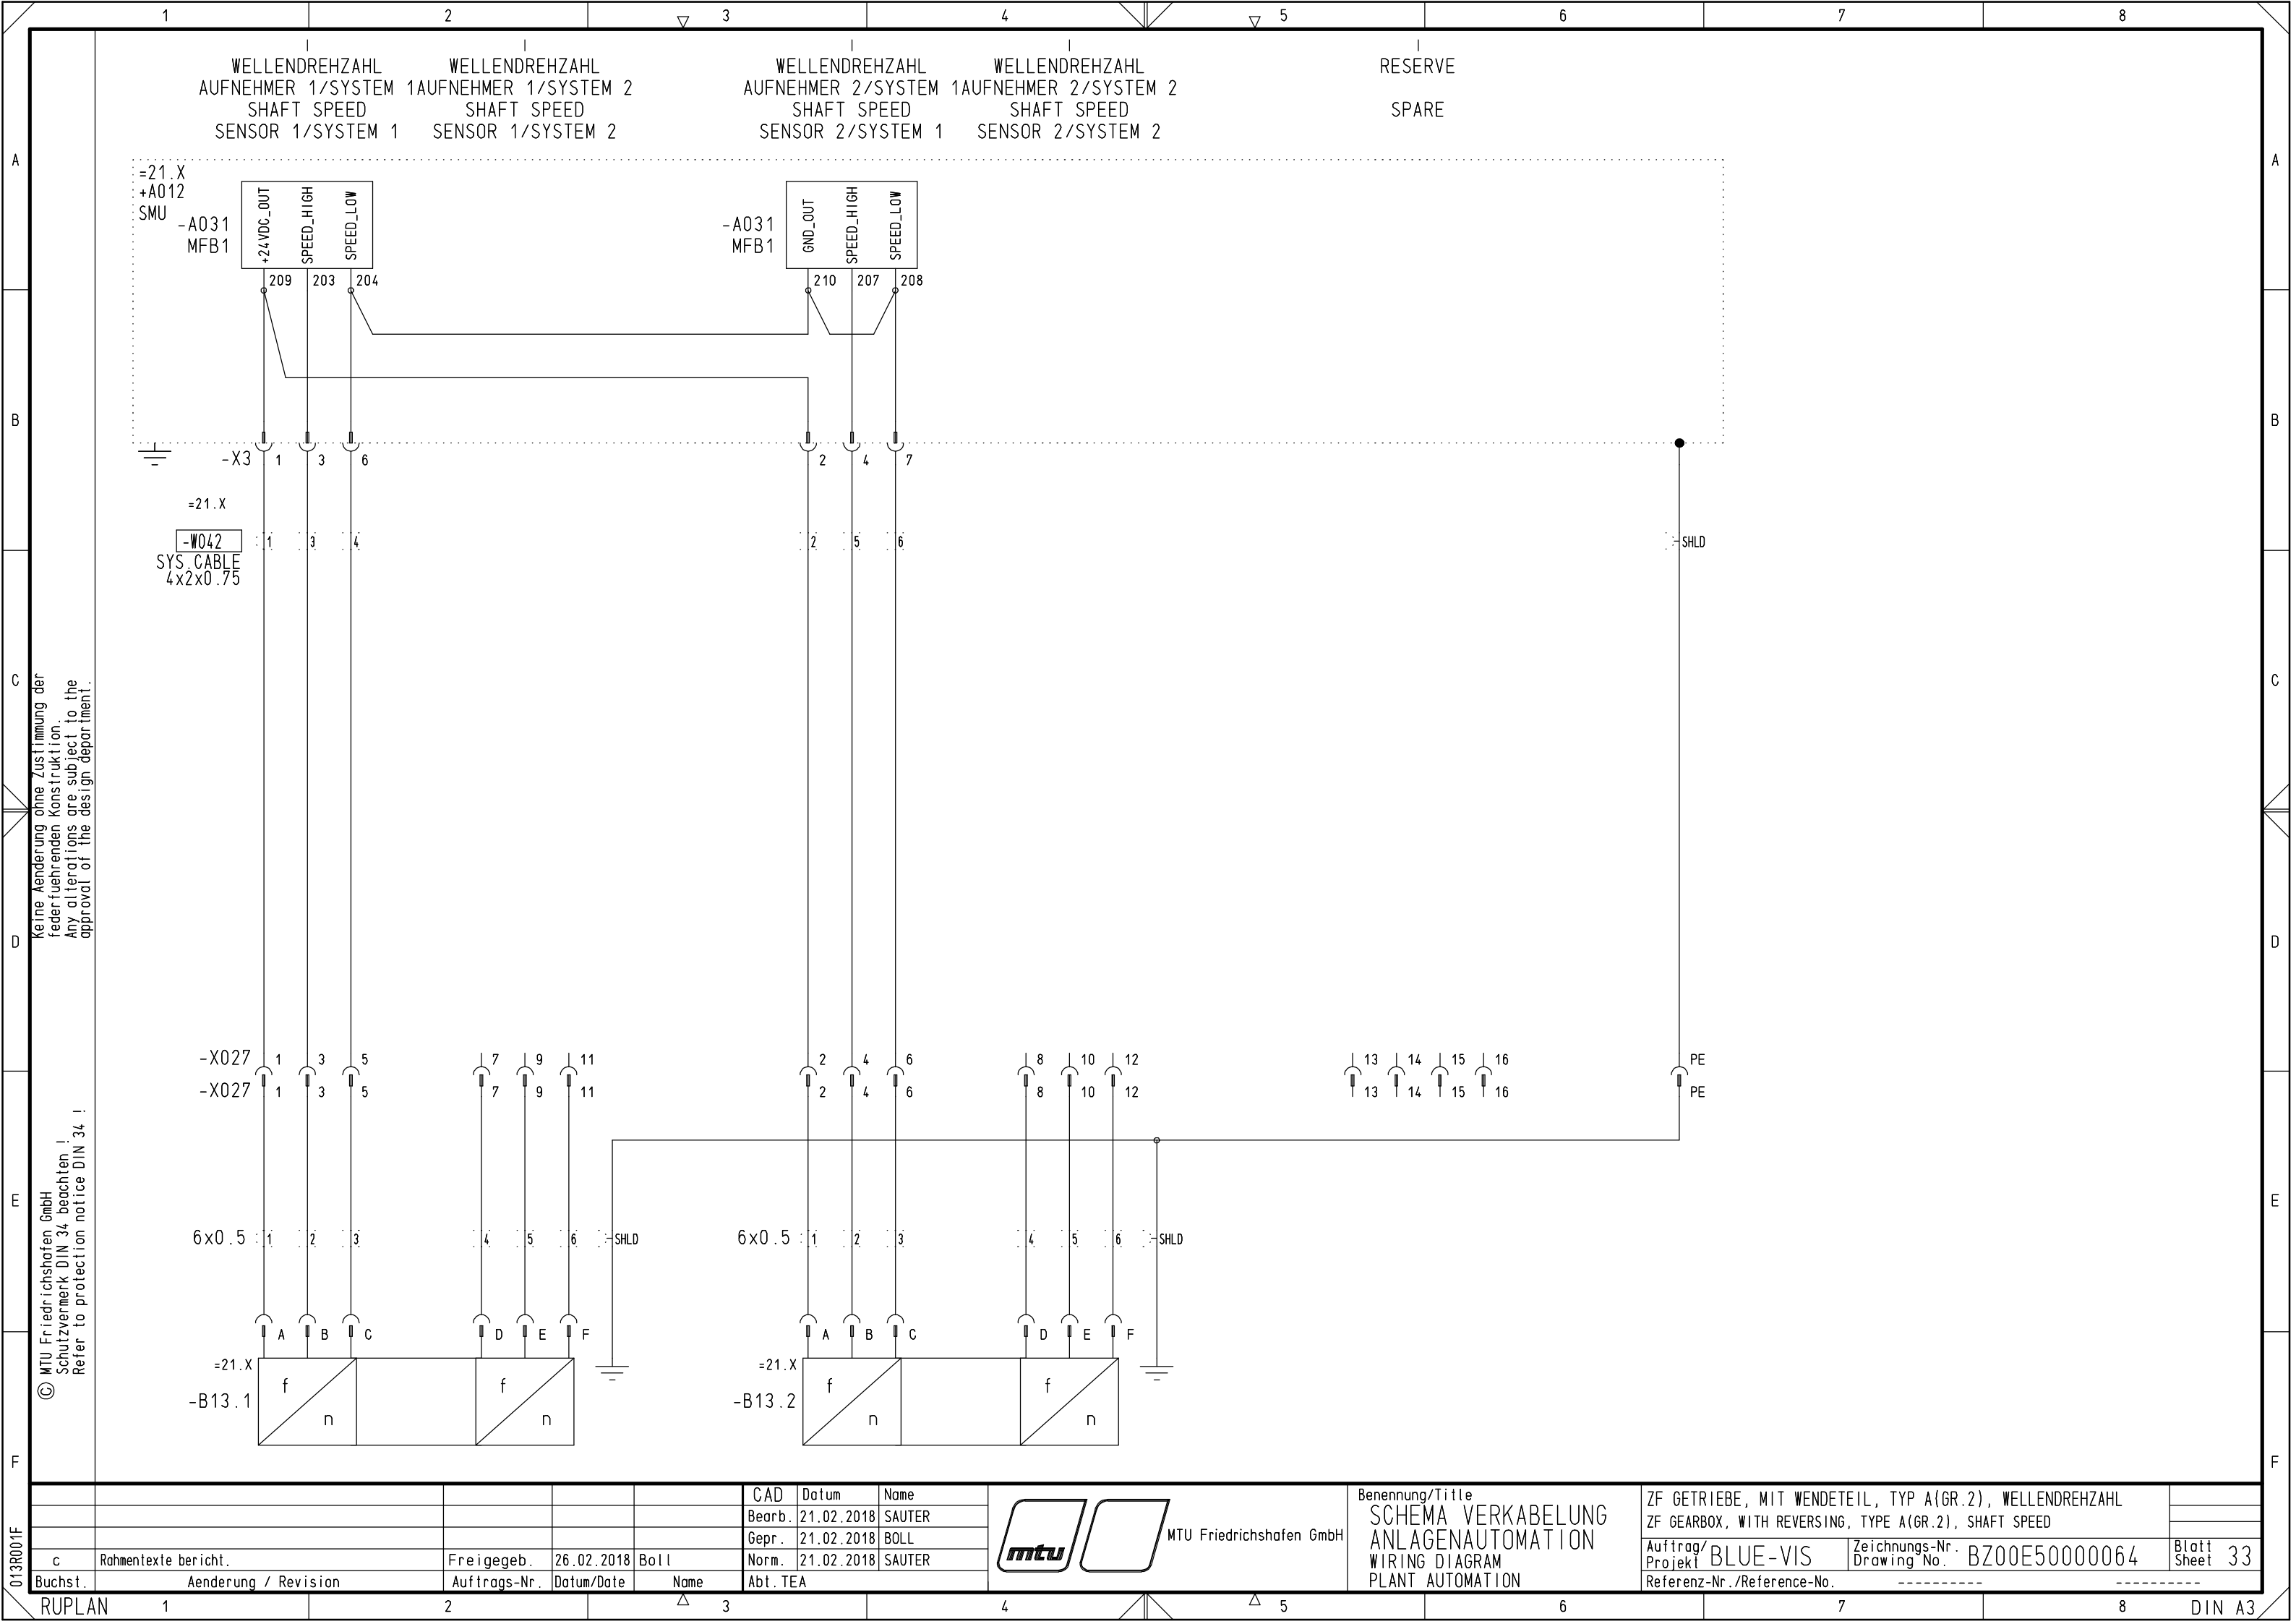

[illegible]

Keine Änderung ohne Zustimmung der
federführenden Konstruktion.
Any alterations are subject to the
approval of the design department.

© MTU Friedrichshafen GmbH
Schutzvermerk DIN 34 beachten !
Refer to protection notice DIN 34 !


					CAD	Datum	Name
					Bearb.	21.02.2018	SAUTER
					Gepr.	21.02.2018	BOLL
					Norm.	21.02.2018	SAUTER
c	Rahmentexte bericht.	Freigegeb.	26.02.2018	Boll	Abt. TEA		
Buchst.	Aenderung / Revision	Auftrags-Nr.	Datum/Date	Name			





MTU Friedrichshafen GmbH

Benennung/Title
SCHEMA VERKABELUNG
ANLAGENAUTOMATION
WIRING DIAGRAM
PLANT AUTOMATION

ZF GETRIEBE, OHNE WENDETEIL, TYP A(GR.2), GRUNDUMFANG ZF GEARBOX, WITHOUT REVERSING, TYPE A(GR.2), BASIC SCOPE			
Auftrag/ Projekt	BLUE-VIS	Zeichnungs-Nr. Drawing No.	BZ00E50000064
Referenz-Nr./Reference-No.		-----	
			Blatt Sheet 35

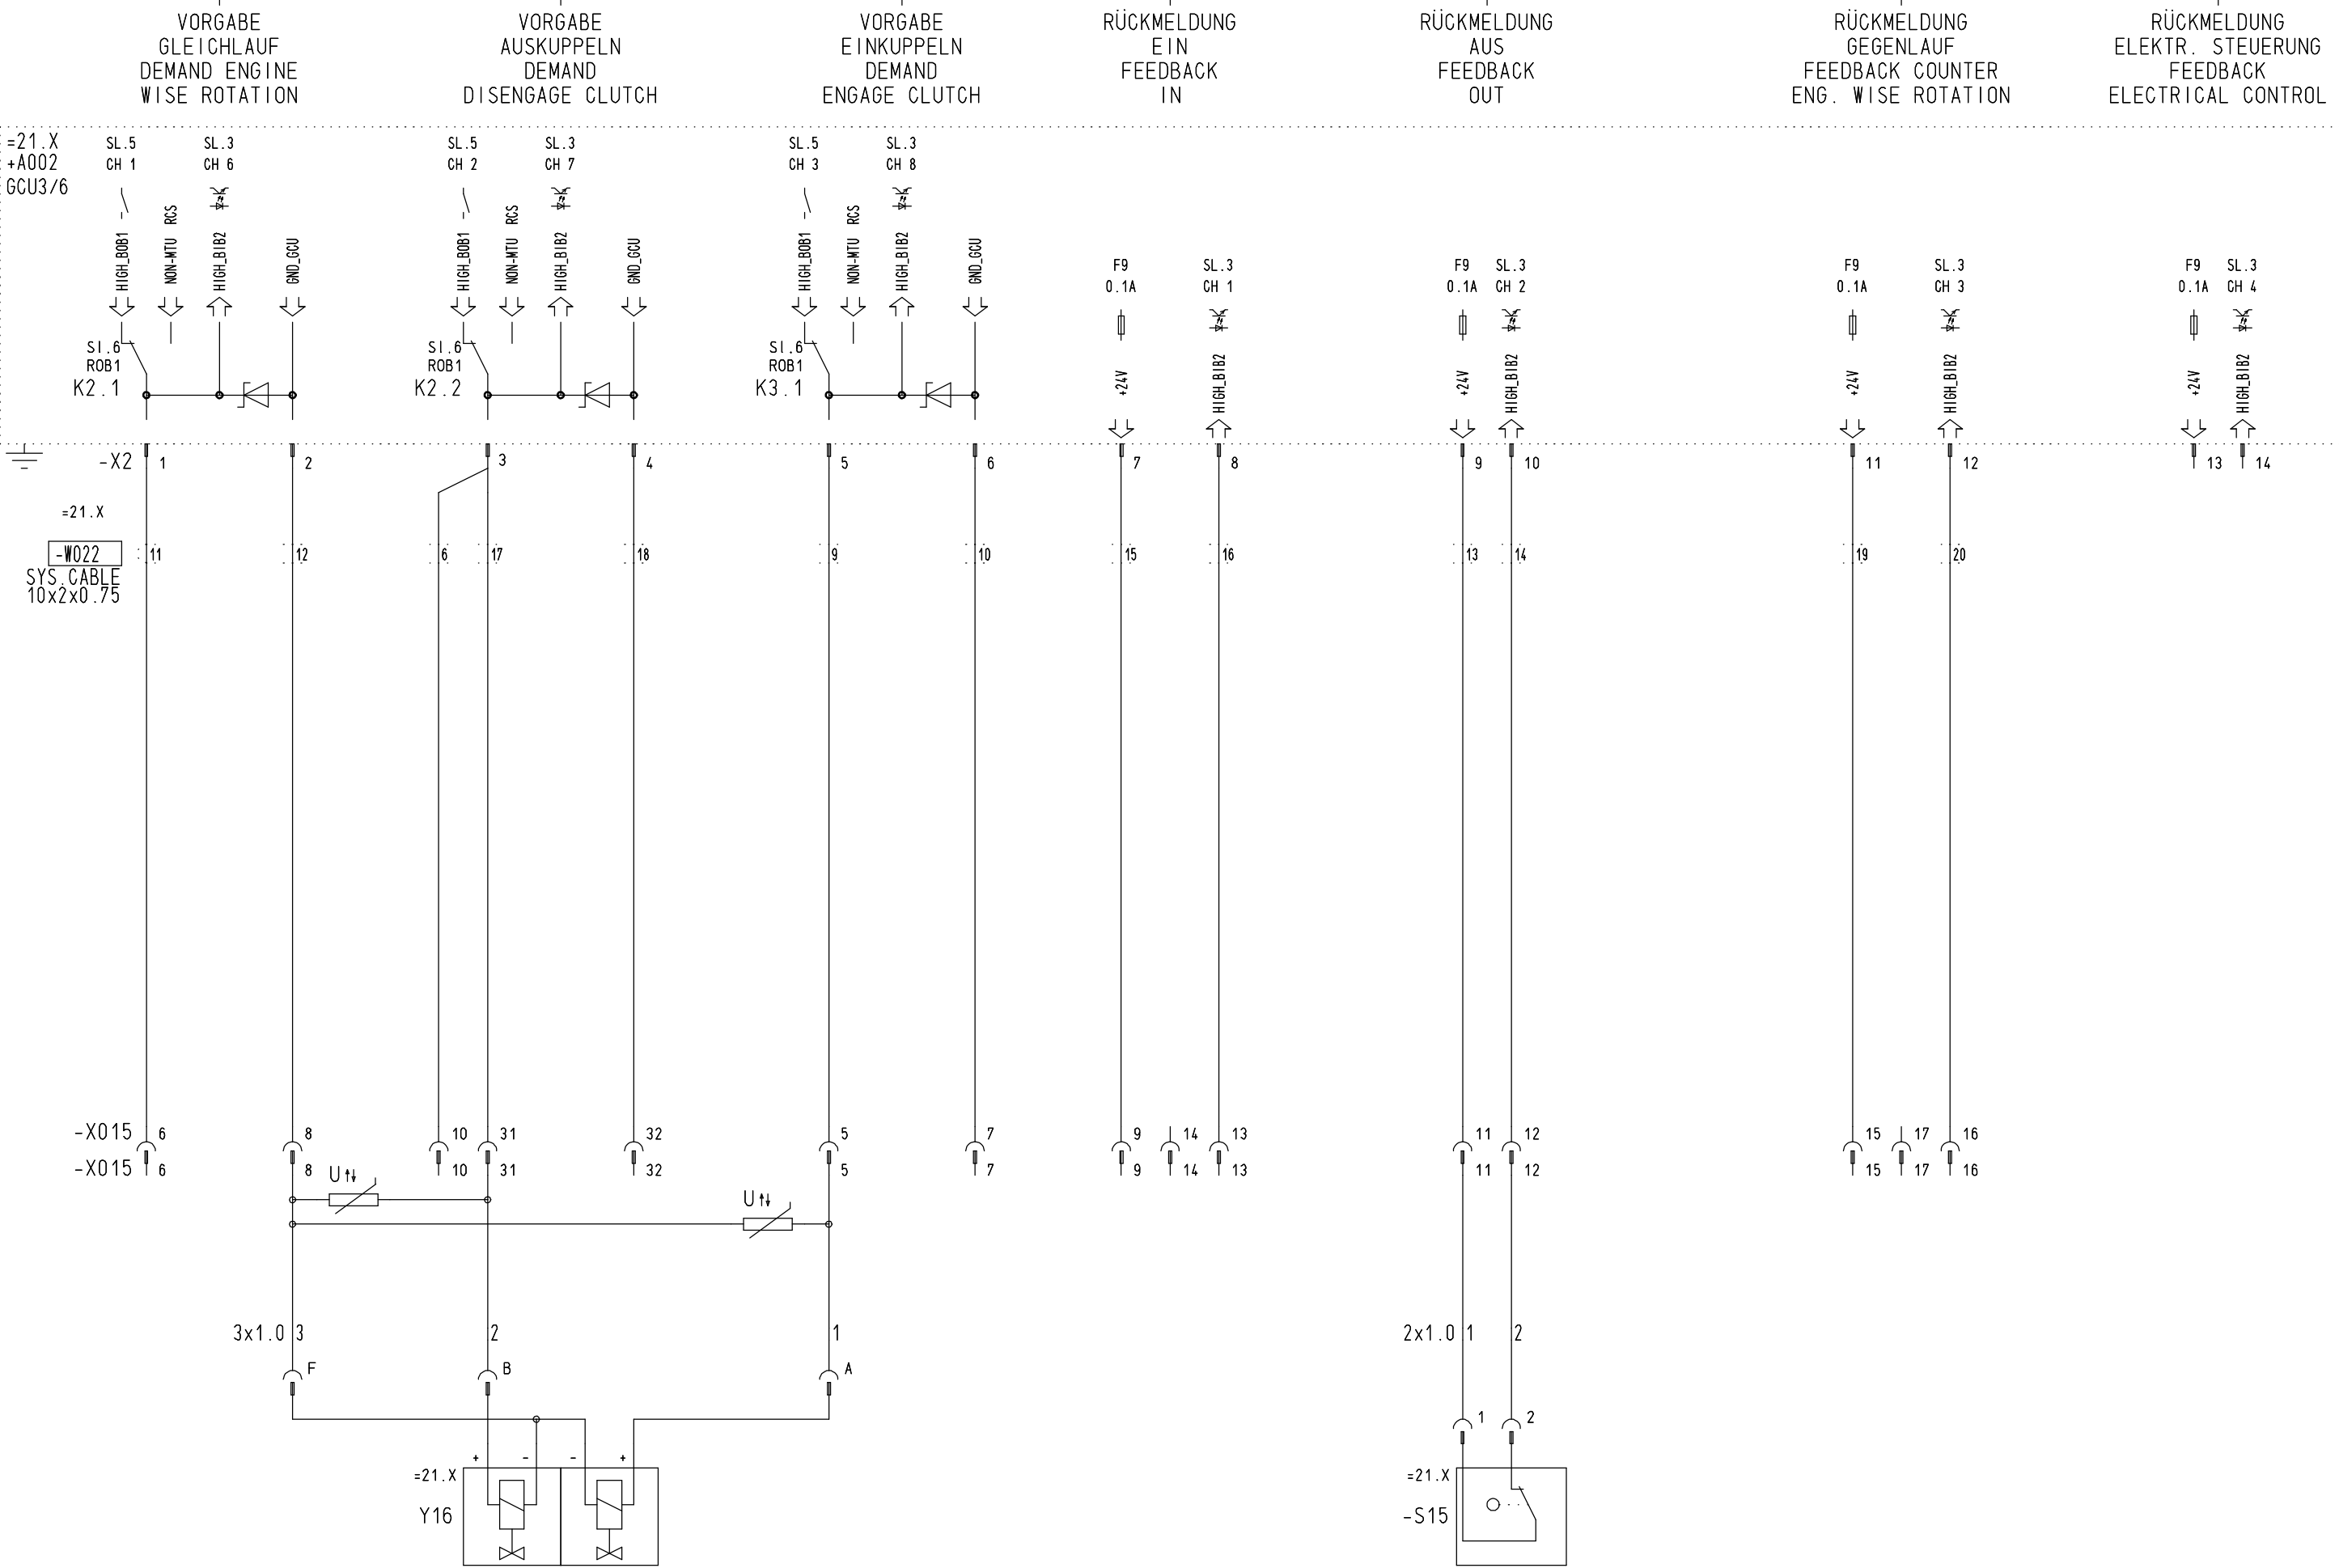


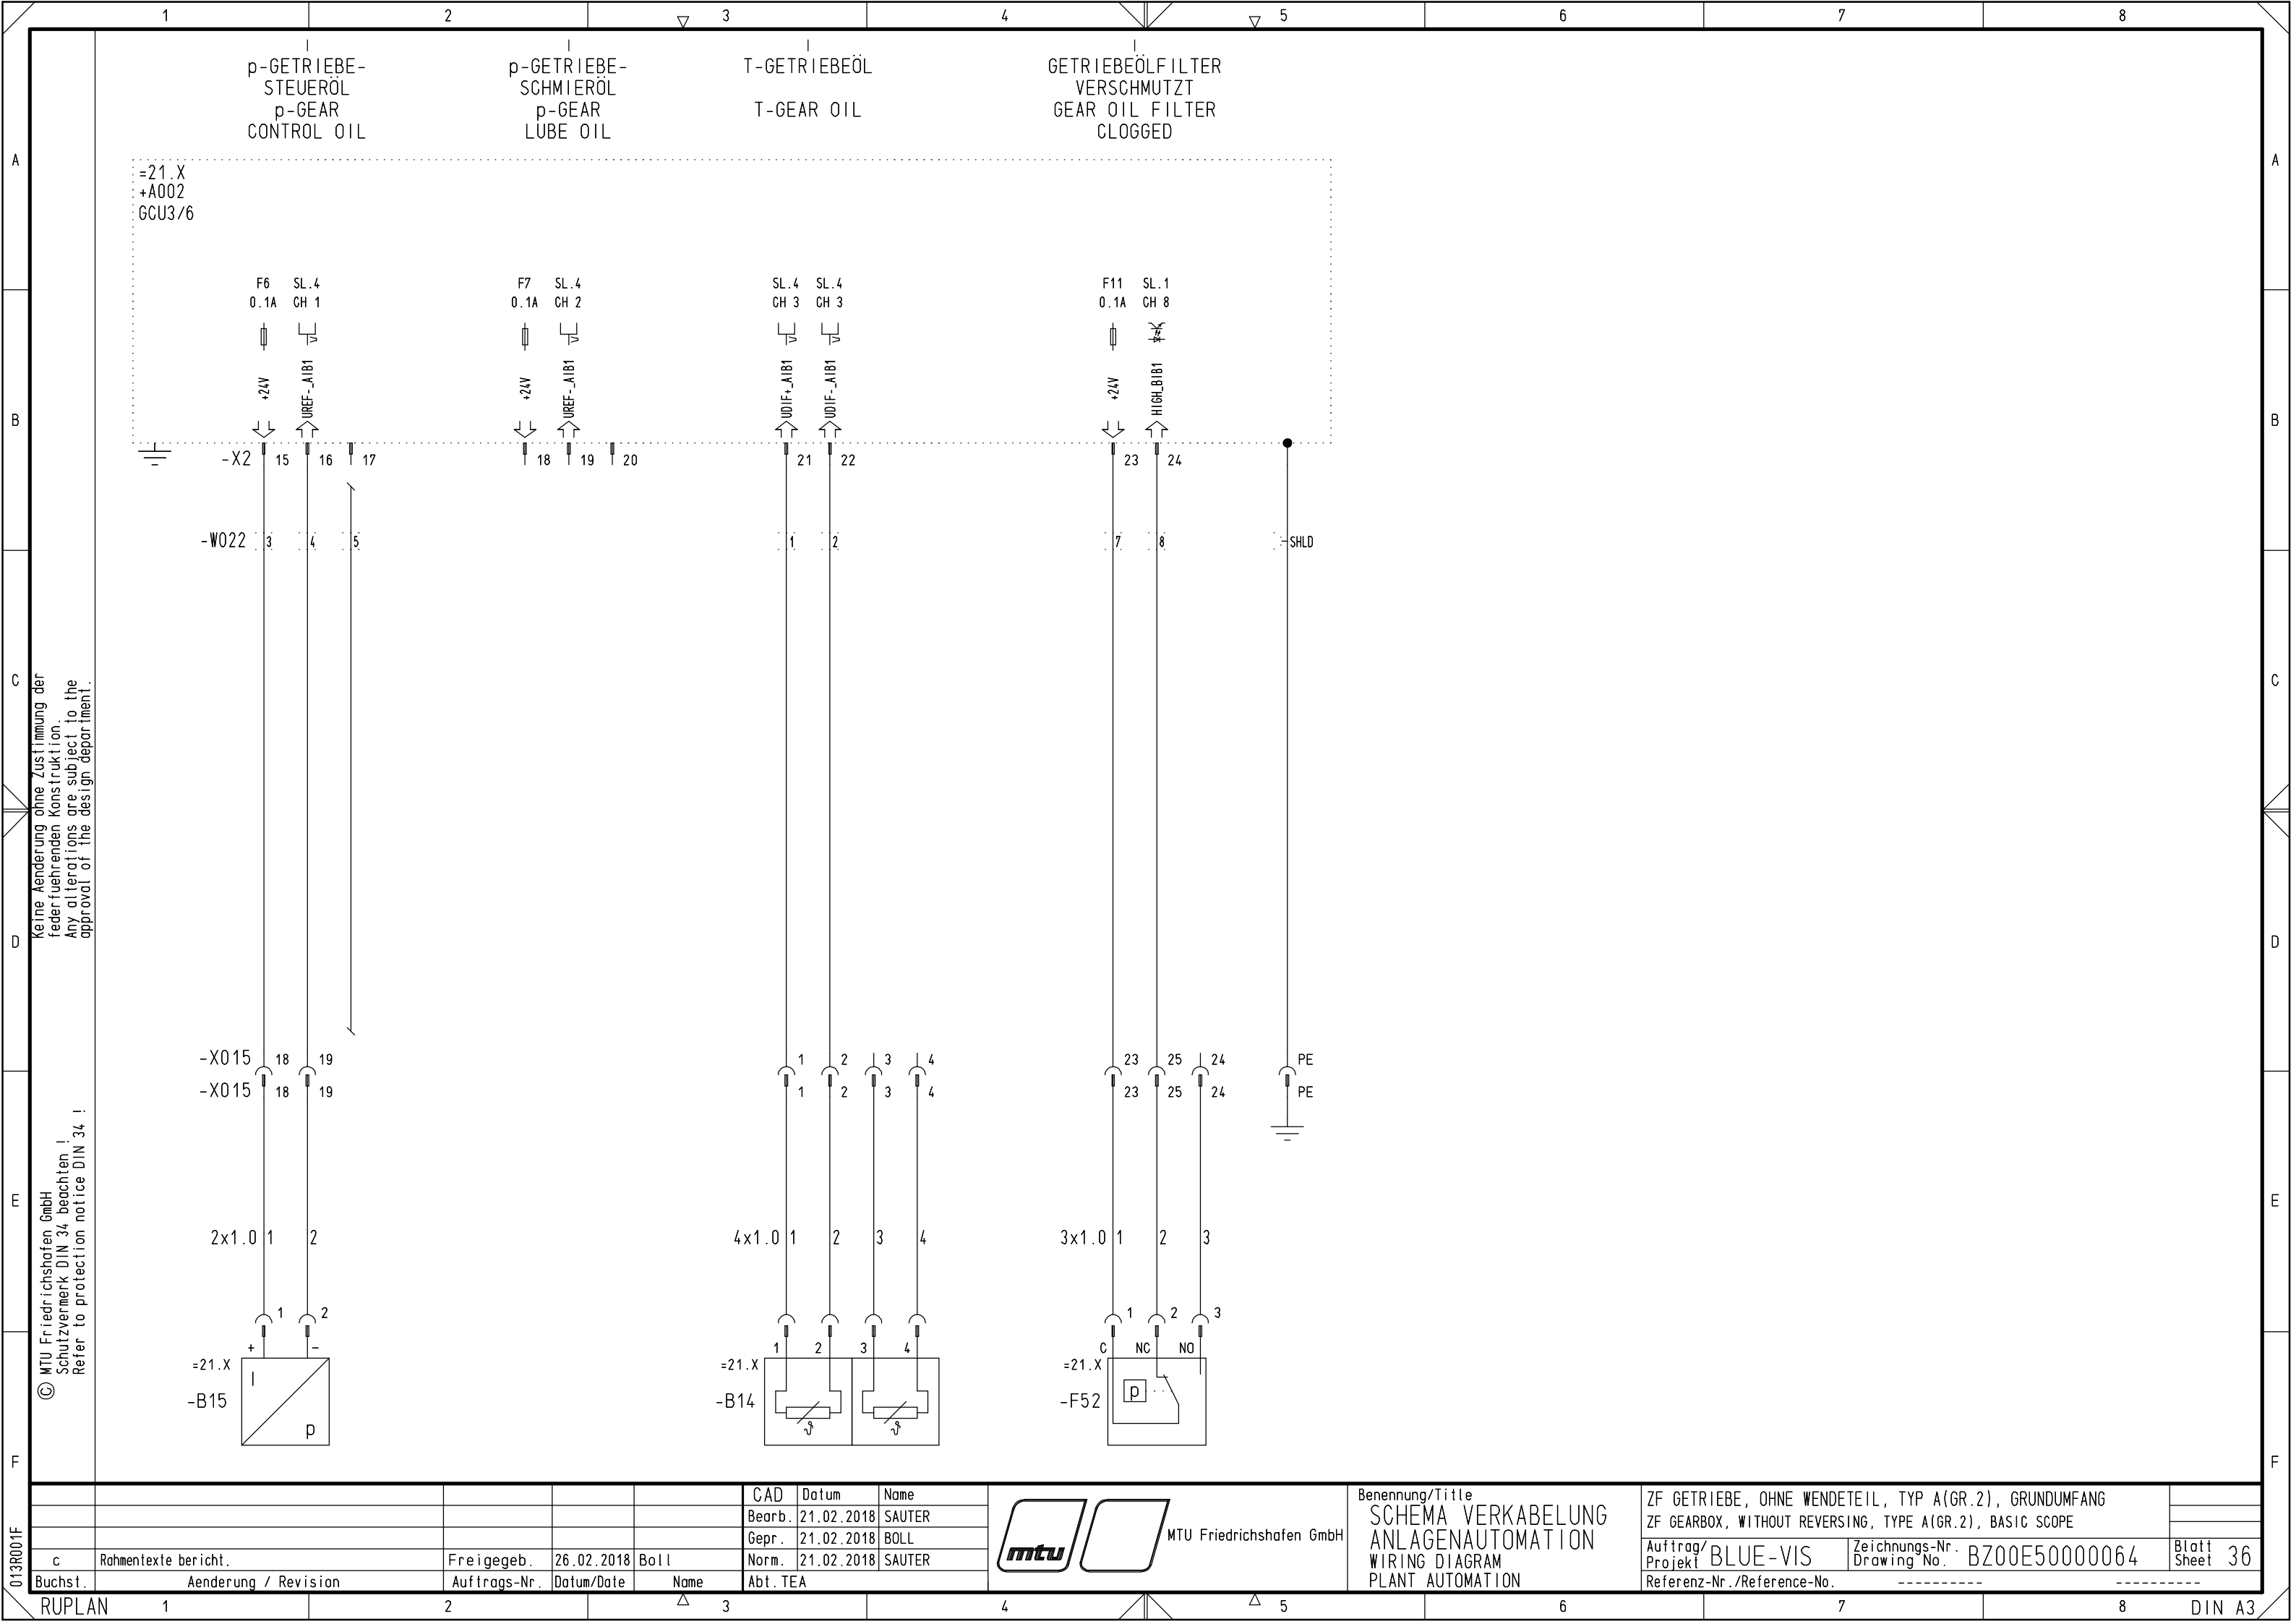

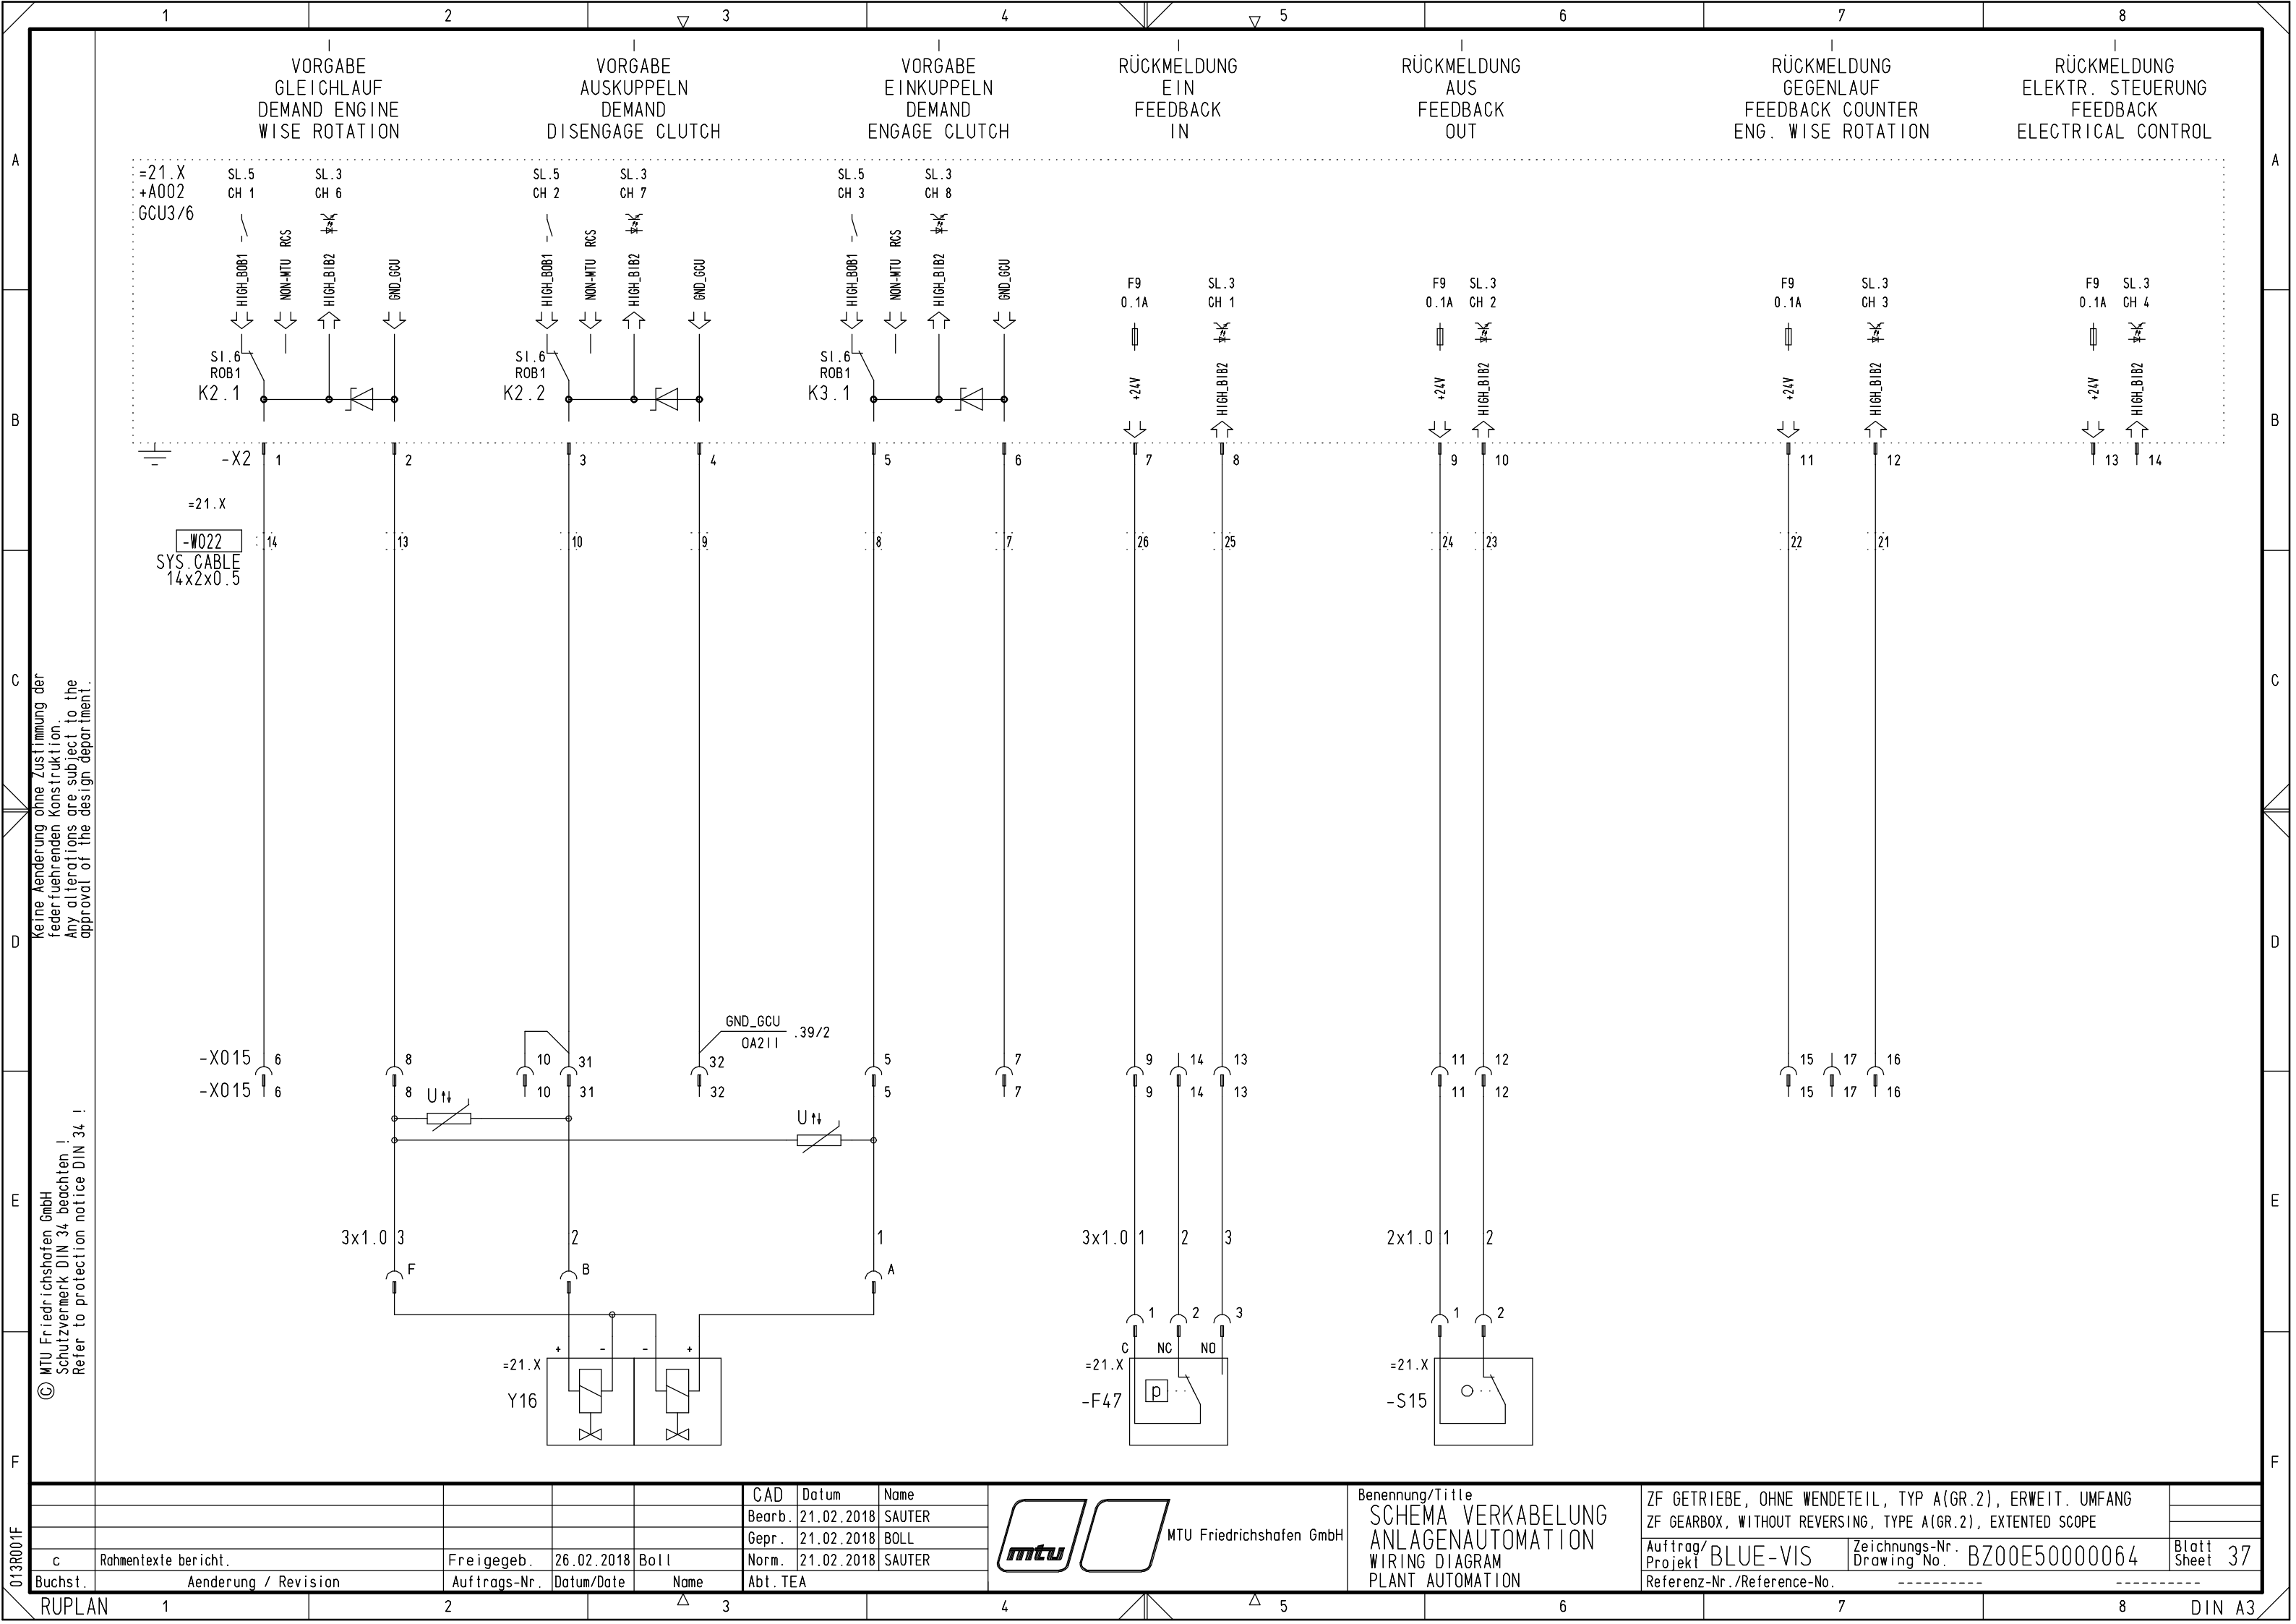


Keine Änderung ohne Zustimmung der
federführenden Konstruktion.
Any alterations are subject to the
approval of the design department.

© MTU Friedrichshafen GmbH
Schutzvermerk DIN 34 beachten !
Refer to protection notice DIN 34 !

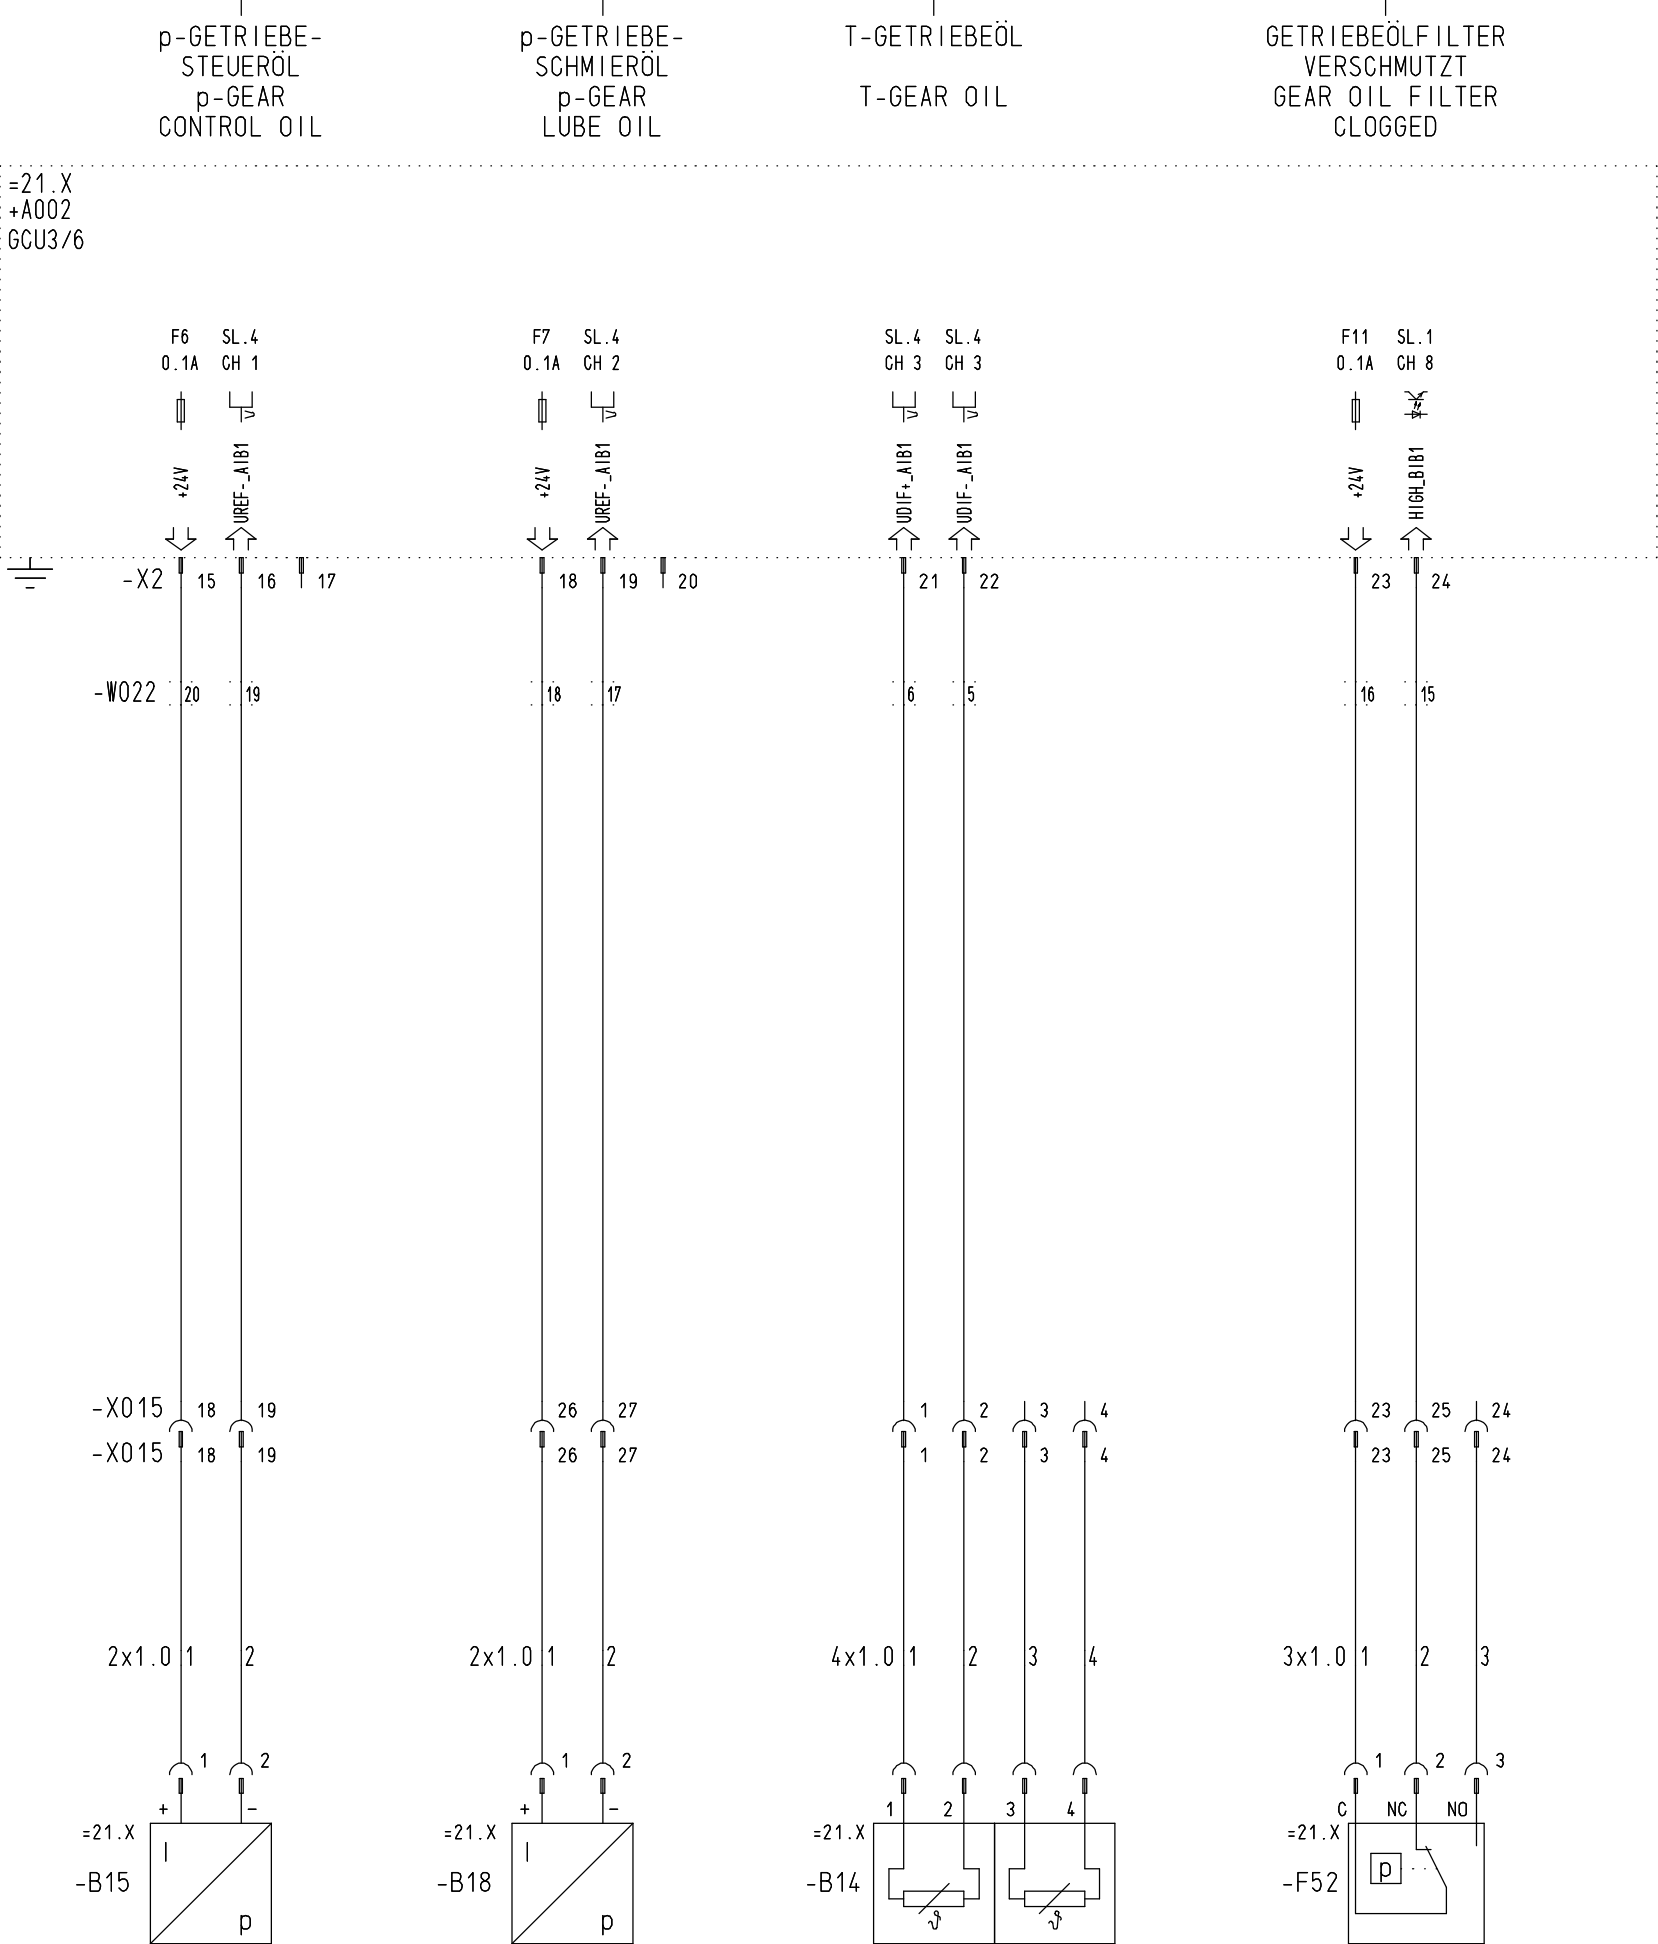

					CAD	Datum	Name	 MTU Friedrichshafen GmbH	Benennung/Title SCHEMA VERKABELUNG ANLAGENAUTOMATION WIRING DIAGRAM PLANT AUTOMATION	ZF GETRIEBE, OHNE WENDETEIL, TYP A(GR.2), ERWEIT. UMFANG ZF GEARBOX, WITHOUT REVERSING, TYPE A(GR.2), EXTENDED SCOPE					
					Bearb.	21.02.2018	SAUTER								
					Gepr.	21.02.2018	BOLL								
					Norm.	21.02.2018	SAUTER								
c	Rahmentexte bericht.		Freigegeb.	26.02.2018	Boll					Auftrag/ Projekt	BLUE-VIS	Zeichnungs-Nr. Drawing No.	BZ00E50000064	Blatt Sheet	38
Buchst.	Aenderung / Revision		Auftrags-Nr.	Datum/Date	Name	Abt. TEA				Referenz-Nr./Reference-No.		-----			

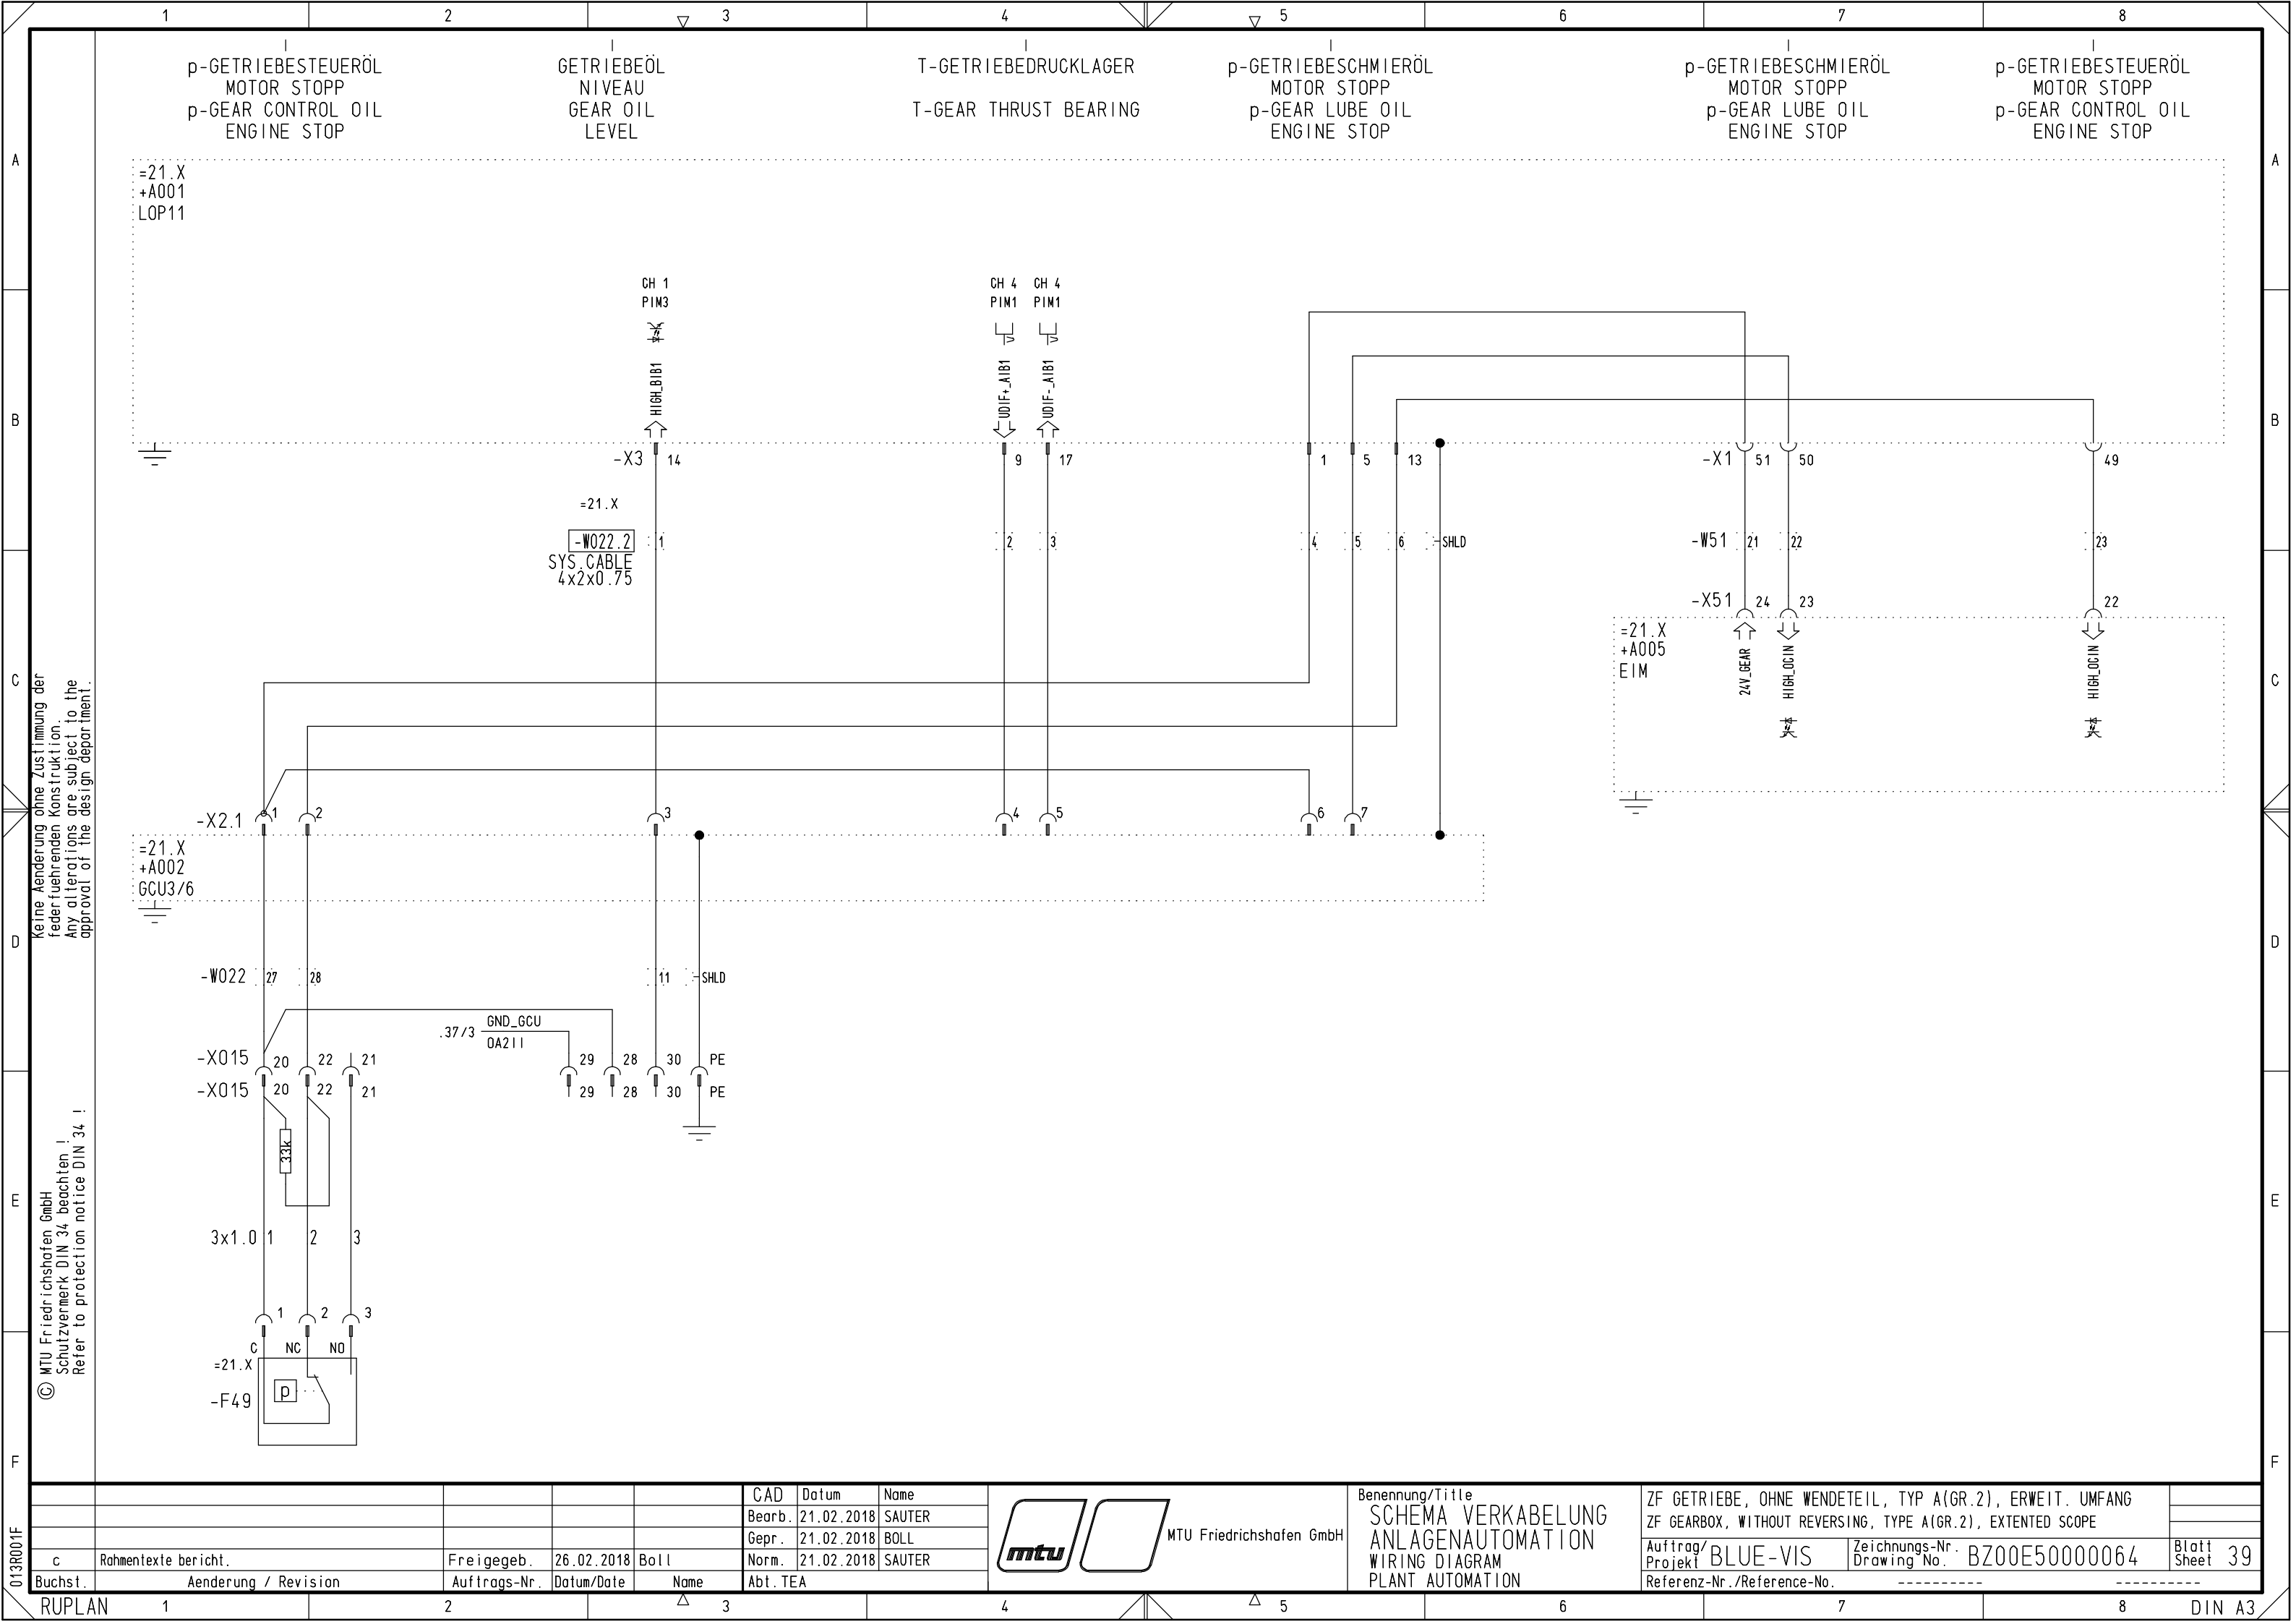


Keine Änderung ohne Zustimmung der
federführenden Konstruktion.
Any alterations are subject to the
approval of the design department.

© MTU Friedrichshafen GmbH
Schutzmerk DIN 34 beachten!
Refer to protection notice DIN 34!

					CAD	Datum	Name
					Bearb.	21.02.2018	SAUTER
					Gepr.	21.02.2018	BOLL
					Norm.	21.02.2018	SAUTER
c	Rahmentexte bericht.	Freigegeb.	26.02.2018	Boll	Abt. TEA		
Buchst.	Aenderung / Revision	Auftrags-Nr.	Datum/Date	Name			



Benennung/Title SCHEMA VERKABELUNG ANLAGENAUTOMATION WIRING DIAGRAM PLANT AUTOMATION		ZF GETRIEBE, OHNE WENDETEIL, TYP A(GR.2), ERWEIT. UMFANG ZF GEARBOX, WITHOUT REVERSING, TYPE A(GR.2), EXTENDED SCOPE		Auftrag/Projekt BLUE-VIS		Zeichnungs-Nr. Drawing No. BZ00E50000064		Blatt Sheet 39	
Referenz-Nr./Reference-No.									

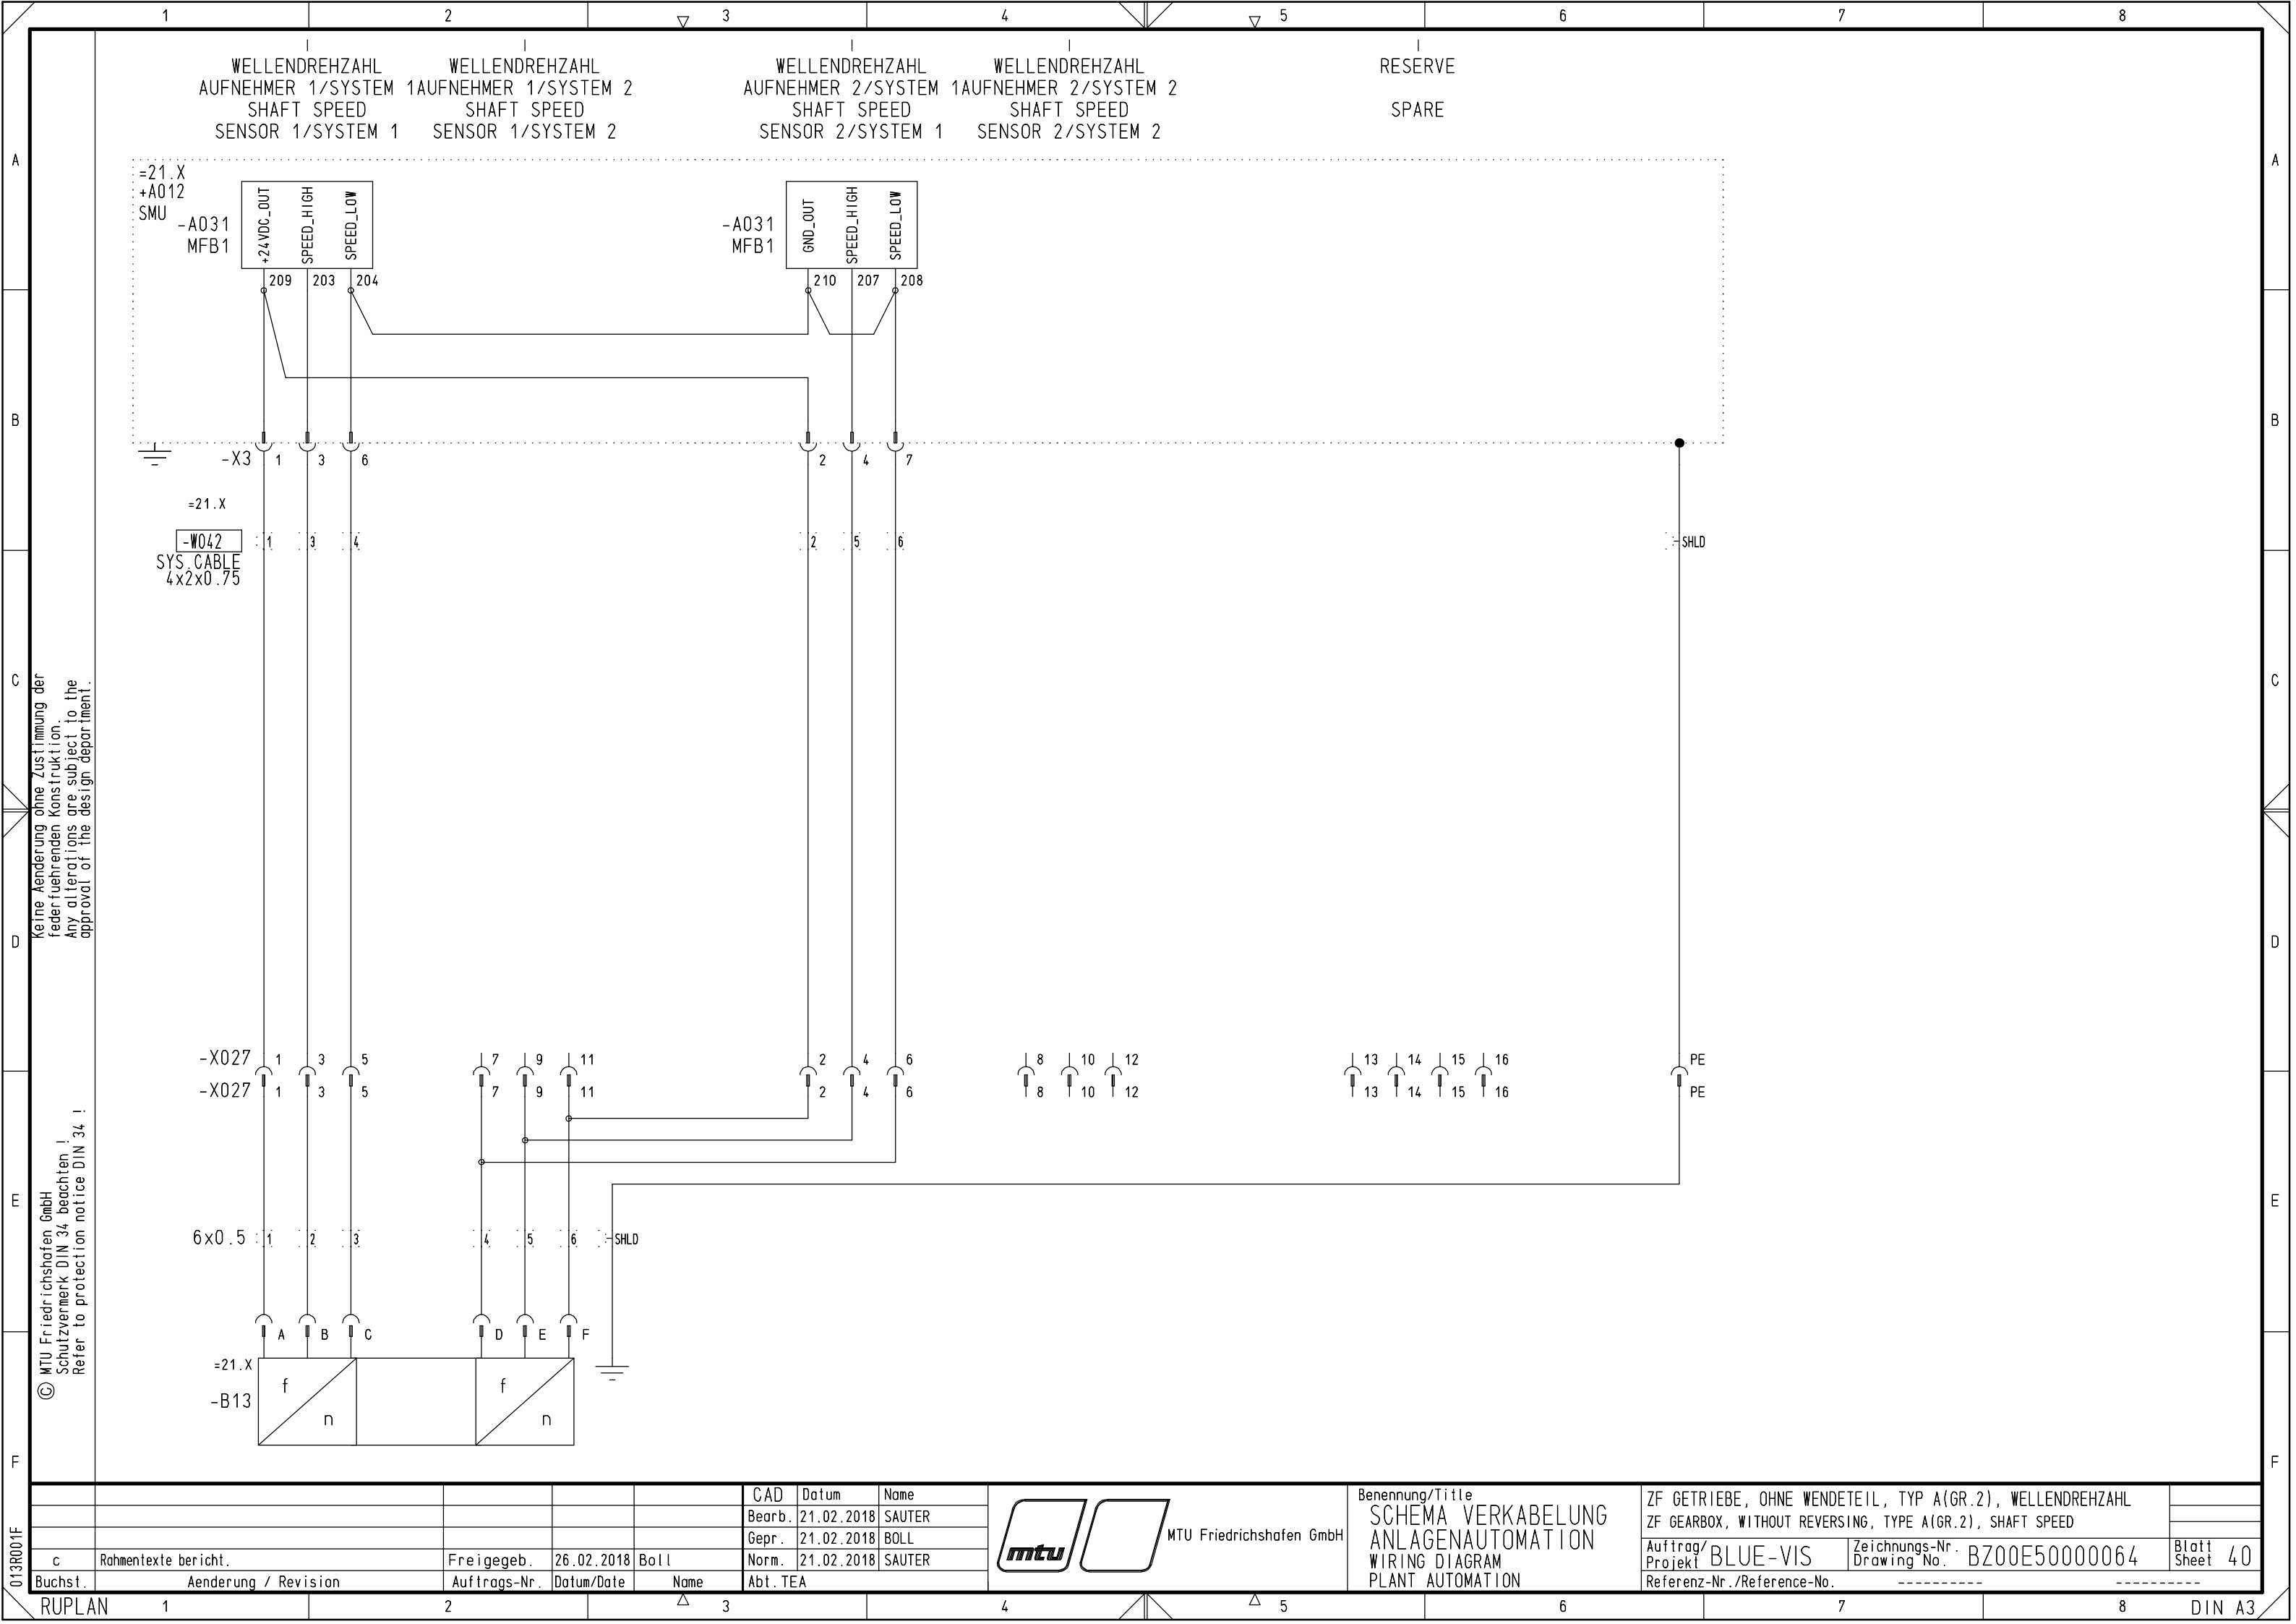

	1	2	3	4	5	6	7	8		
A										
B										
C										
D										
E										
F										
013R001F										
	c	Rahmentexte bericht.	Freigegeb.	26.02.2018	Boll					
	Buchst.	Aenderung / Revision	Auftrags-Nr.	Datum/Date	Name	Abt. TEA				
RUPLAN		1	2	3	4	5	6	7	8	DIN A3

GÜLTIG FÜR:
VALID FOR:

ZF 7550 NR2

ZF 7550 NR2H

ZF 7550 NR2B

ZF 7600 NR2

ZF 7600 NR2H

ZF 7600 NR2B

ZF 7650 NR2

ZF 7650 NR2H

ZF 7650 NR2B

GÜLTIG FÜR:
VALID FOR:

ZF 9000 NR2

ZF 9000 NR2H

ZF 9000 NR2B

ZF 9050 NR2

ZF 9050 NR2H

ZF 9050 NR2B

ZF 9060 NR2

ZF 9060 NR2H

ZF 9060 NR2B

MTU Friedrichshafen GmbH

Benennung/Title

SCHEMA VERKABELUNG
ANLAGENAUTOMATION
WIRING DIAGRAM
PLANT AUTOMATION

ZF GETRIEBE, OHNE WENDETEIL, TYP A(GR.3), HINWEISE
ZF GEARBOX, WITHOUT REVERSING, TYPE A(GR.3), INSTRUCTIONS

Auftrag/
Projekt

BLUE-VIS

Zeichnungs-Nr.
Drawing No.

BZ00E50000064


Blatt
Sheet

41

Referenz-Nr./Reference-No.


Keine Aenderung ohne Zustimmung der
federführenden Konstruktion.
Any alterations are subject to the
approval of the design department.

© MTU Friedrichshafen GmbH
Schutzvermerk DIN 34 beachten !
Refer to protection notice DIN 34 !

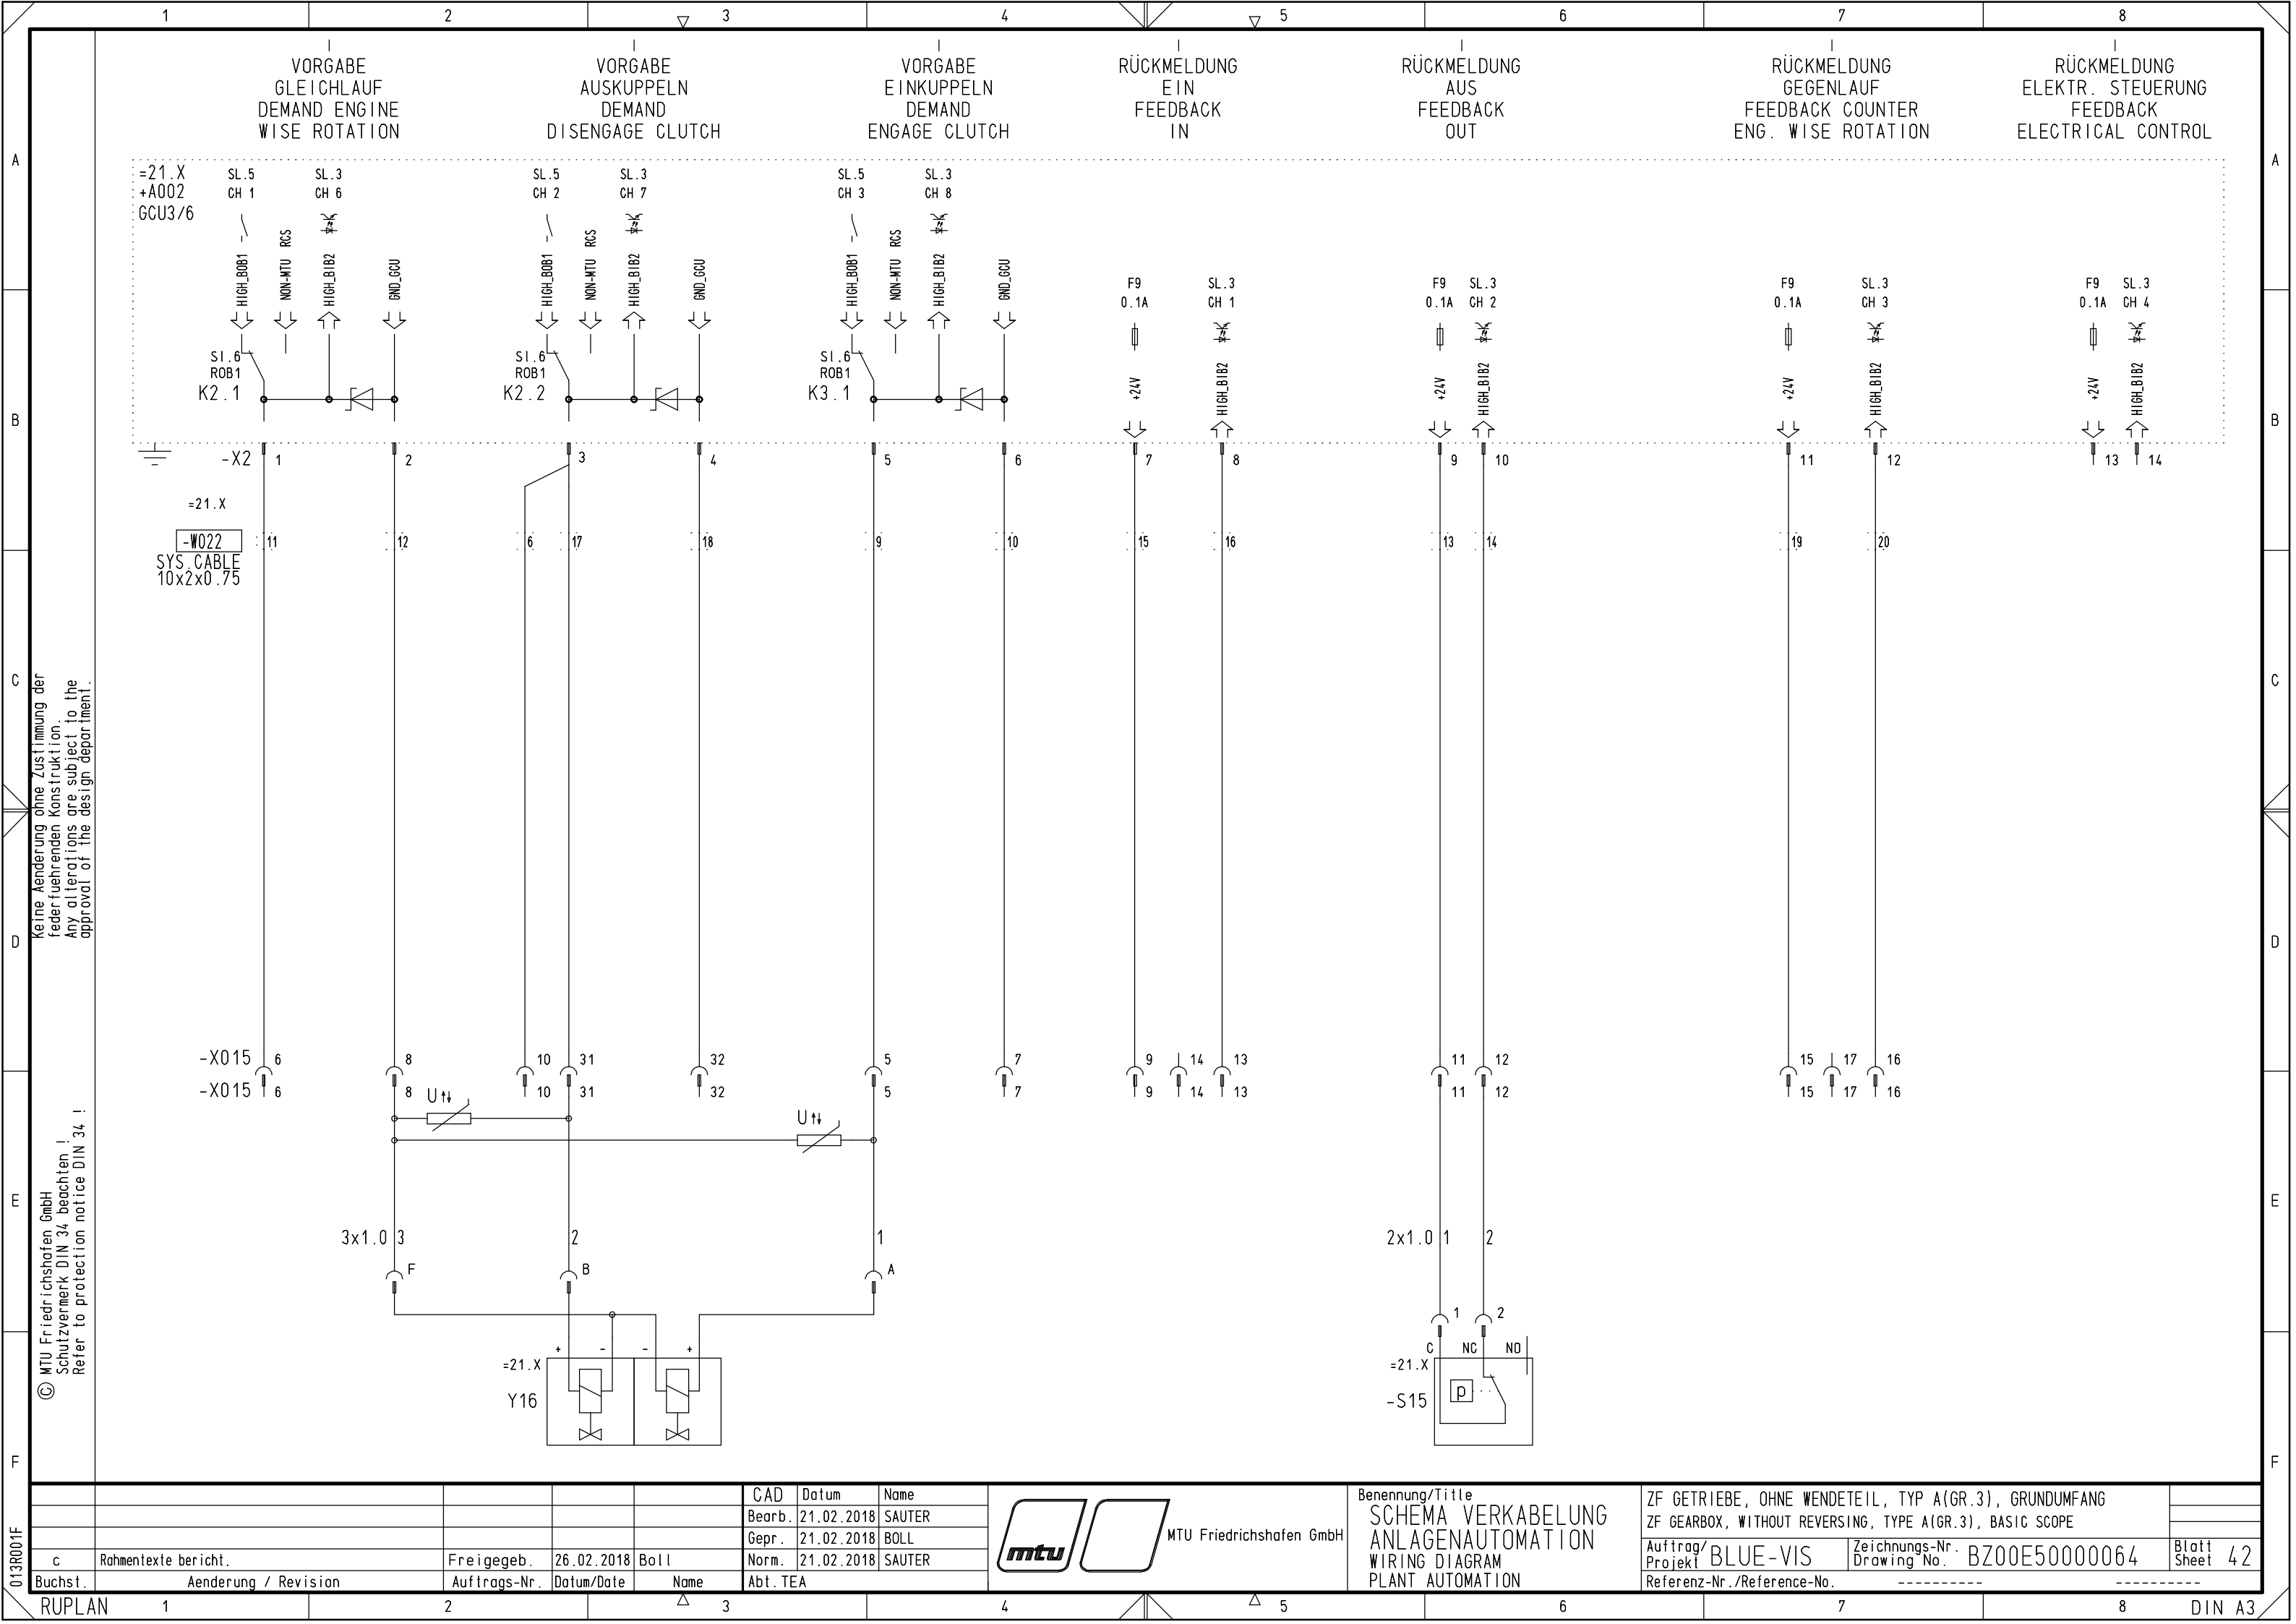

Keine Änderung ohne Zustimmung der
federführenden Konstruktion.
Any alterations are subject to the
approval of the design department.

© MTU Friedrichshafen GmbH
Schutzvermerk DIN 34 beachten !
Refer to protection notice DIN 34 !

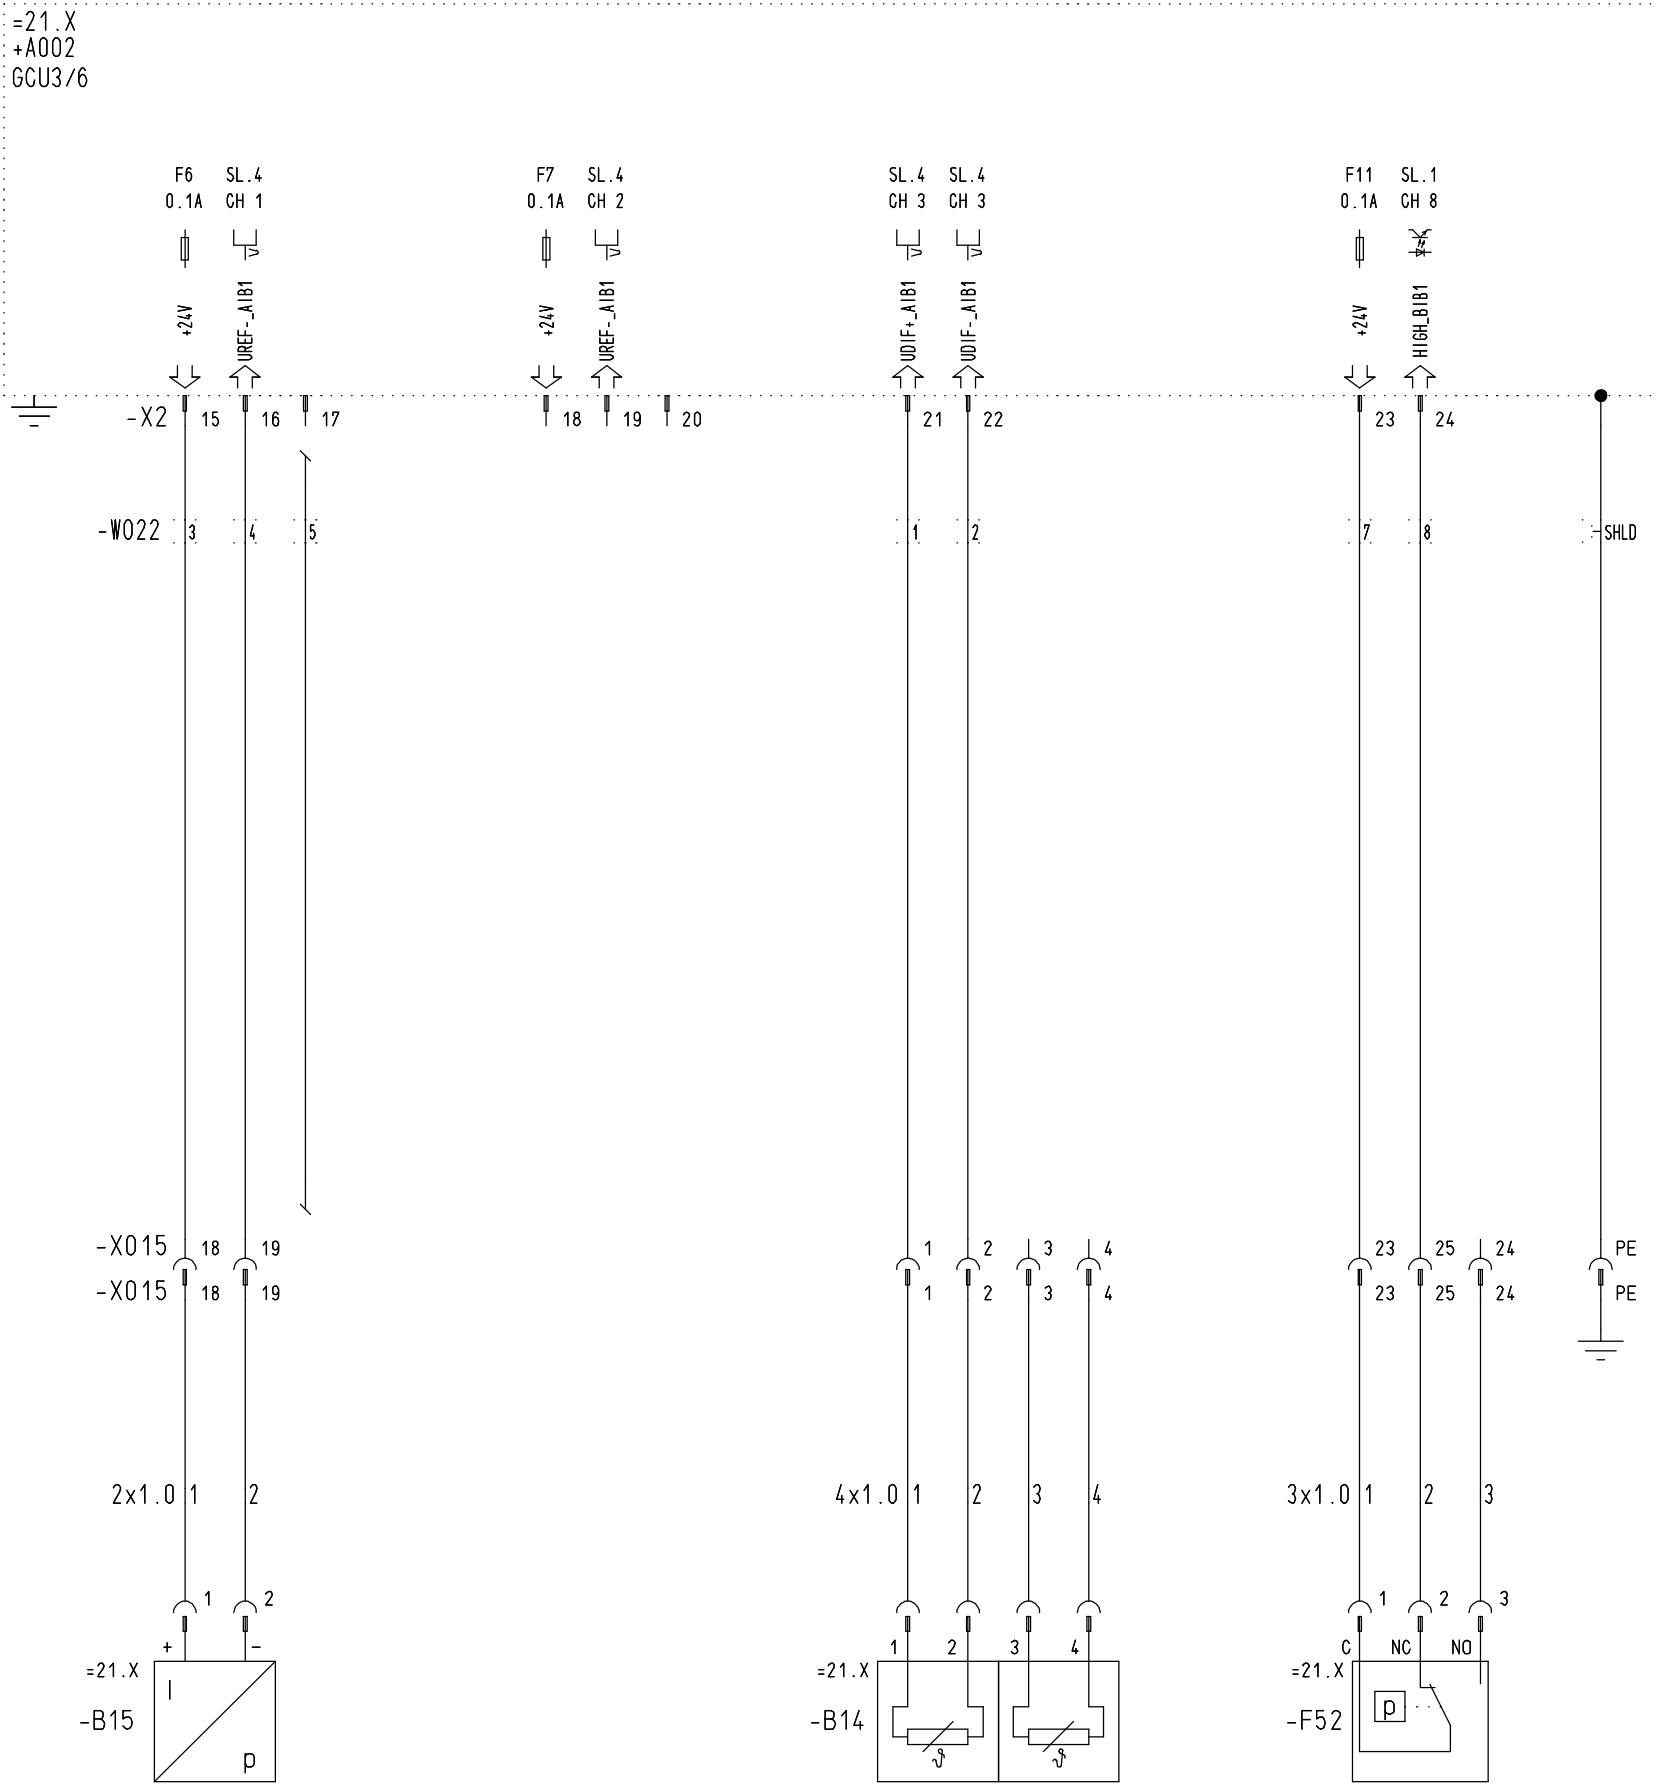


Buchst.	Rahmentexte bericht.	Freigegeb.	Datum/Date	Name	CAD	Datum	Name
					Bearb.	21.02.2018	SAUTER
					Gepr.	21.02.2018	BOLL
					Norm.	21.02.2018	SAUTER
c	Änderung / Revision	Auftrags-Nr.	Datum/Date	Name	Abt. TEA		




MTU Friedrichshafen GmbH


Benennung/Title
SCHEMA VERKABELUNG
ANLAGENAUTOMATION
WIRING DIAGRAM
PLANT AUTOMATION


ZF GETRIEBE, OHNE WENDETEIL, TYP A(GR.3), GRUNDUMFANG ZF GEARBOX, WITHOUT REVERSING, TYPE A(GR.3), BASIC SCOPE			Blatt Sheet 43
Auftrag/ Projekt BLUE-VIS	Zeichnungs-Nr. Drawing No. BZ00E50000064	Referenz-Nr./Reference-No.	

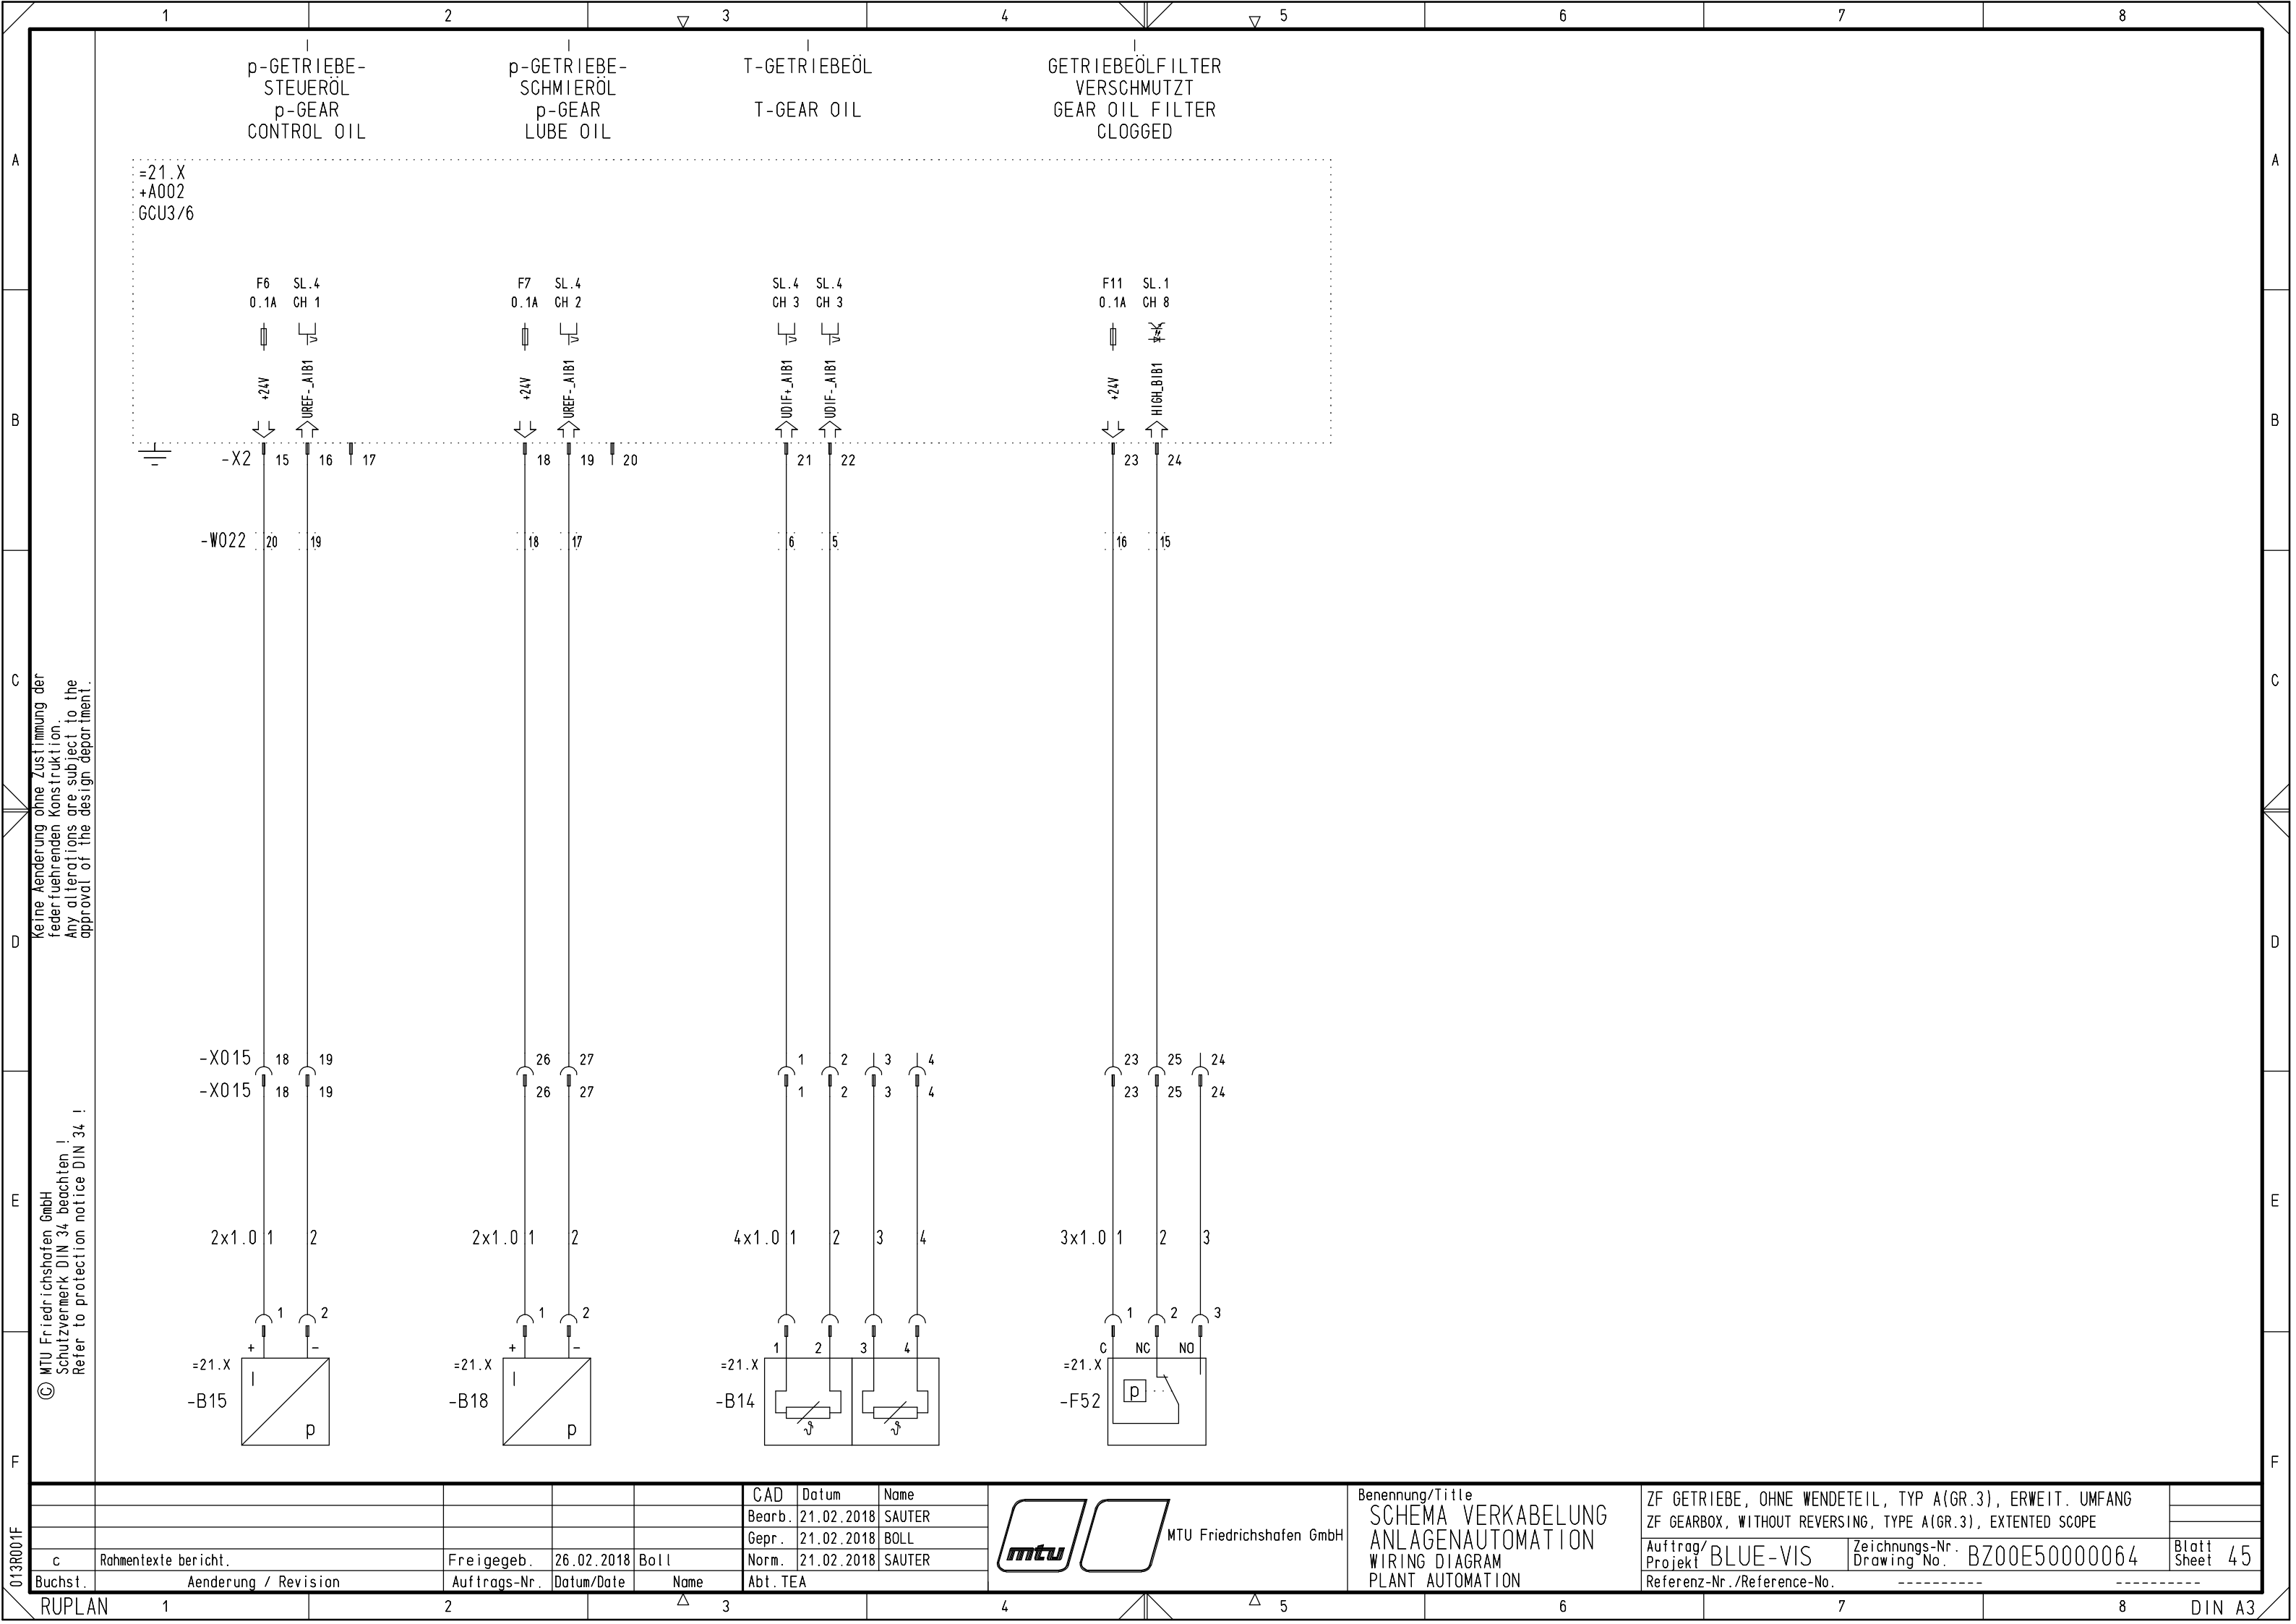

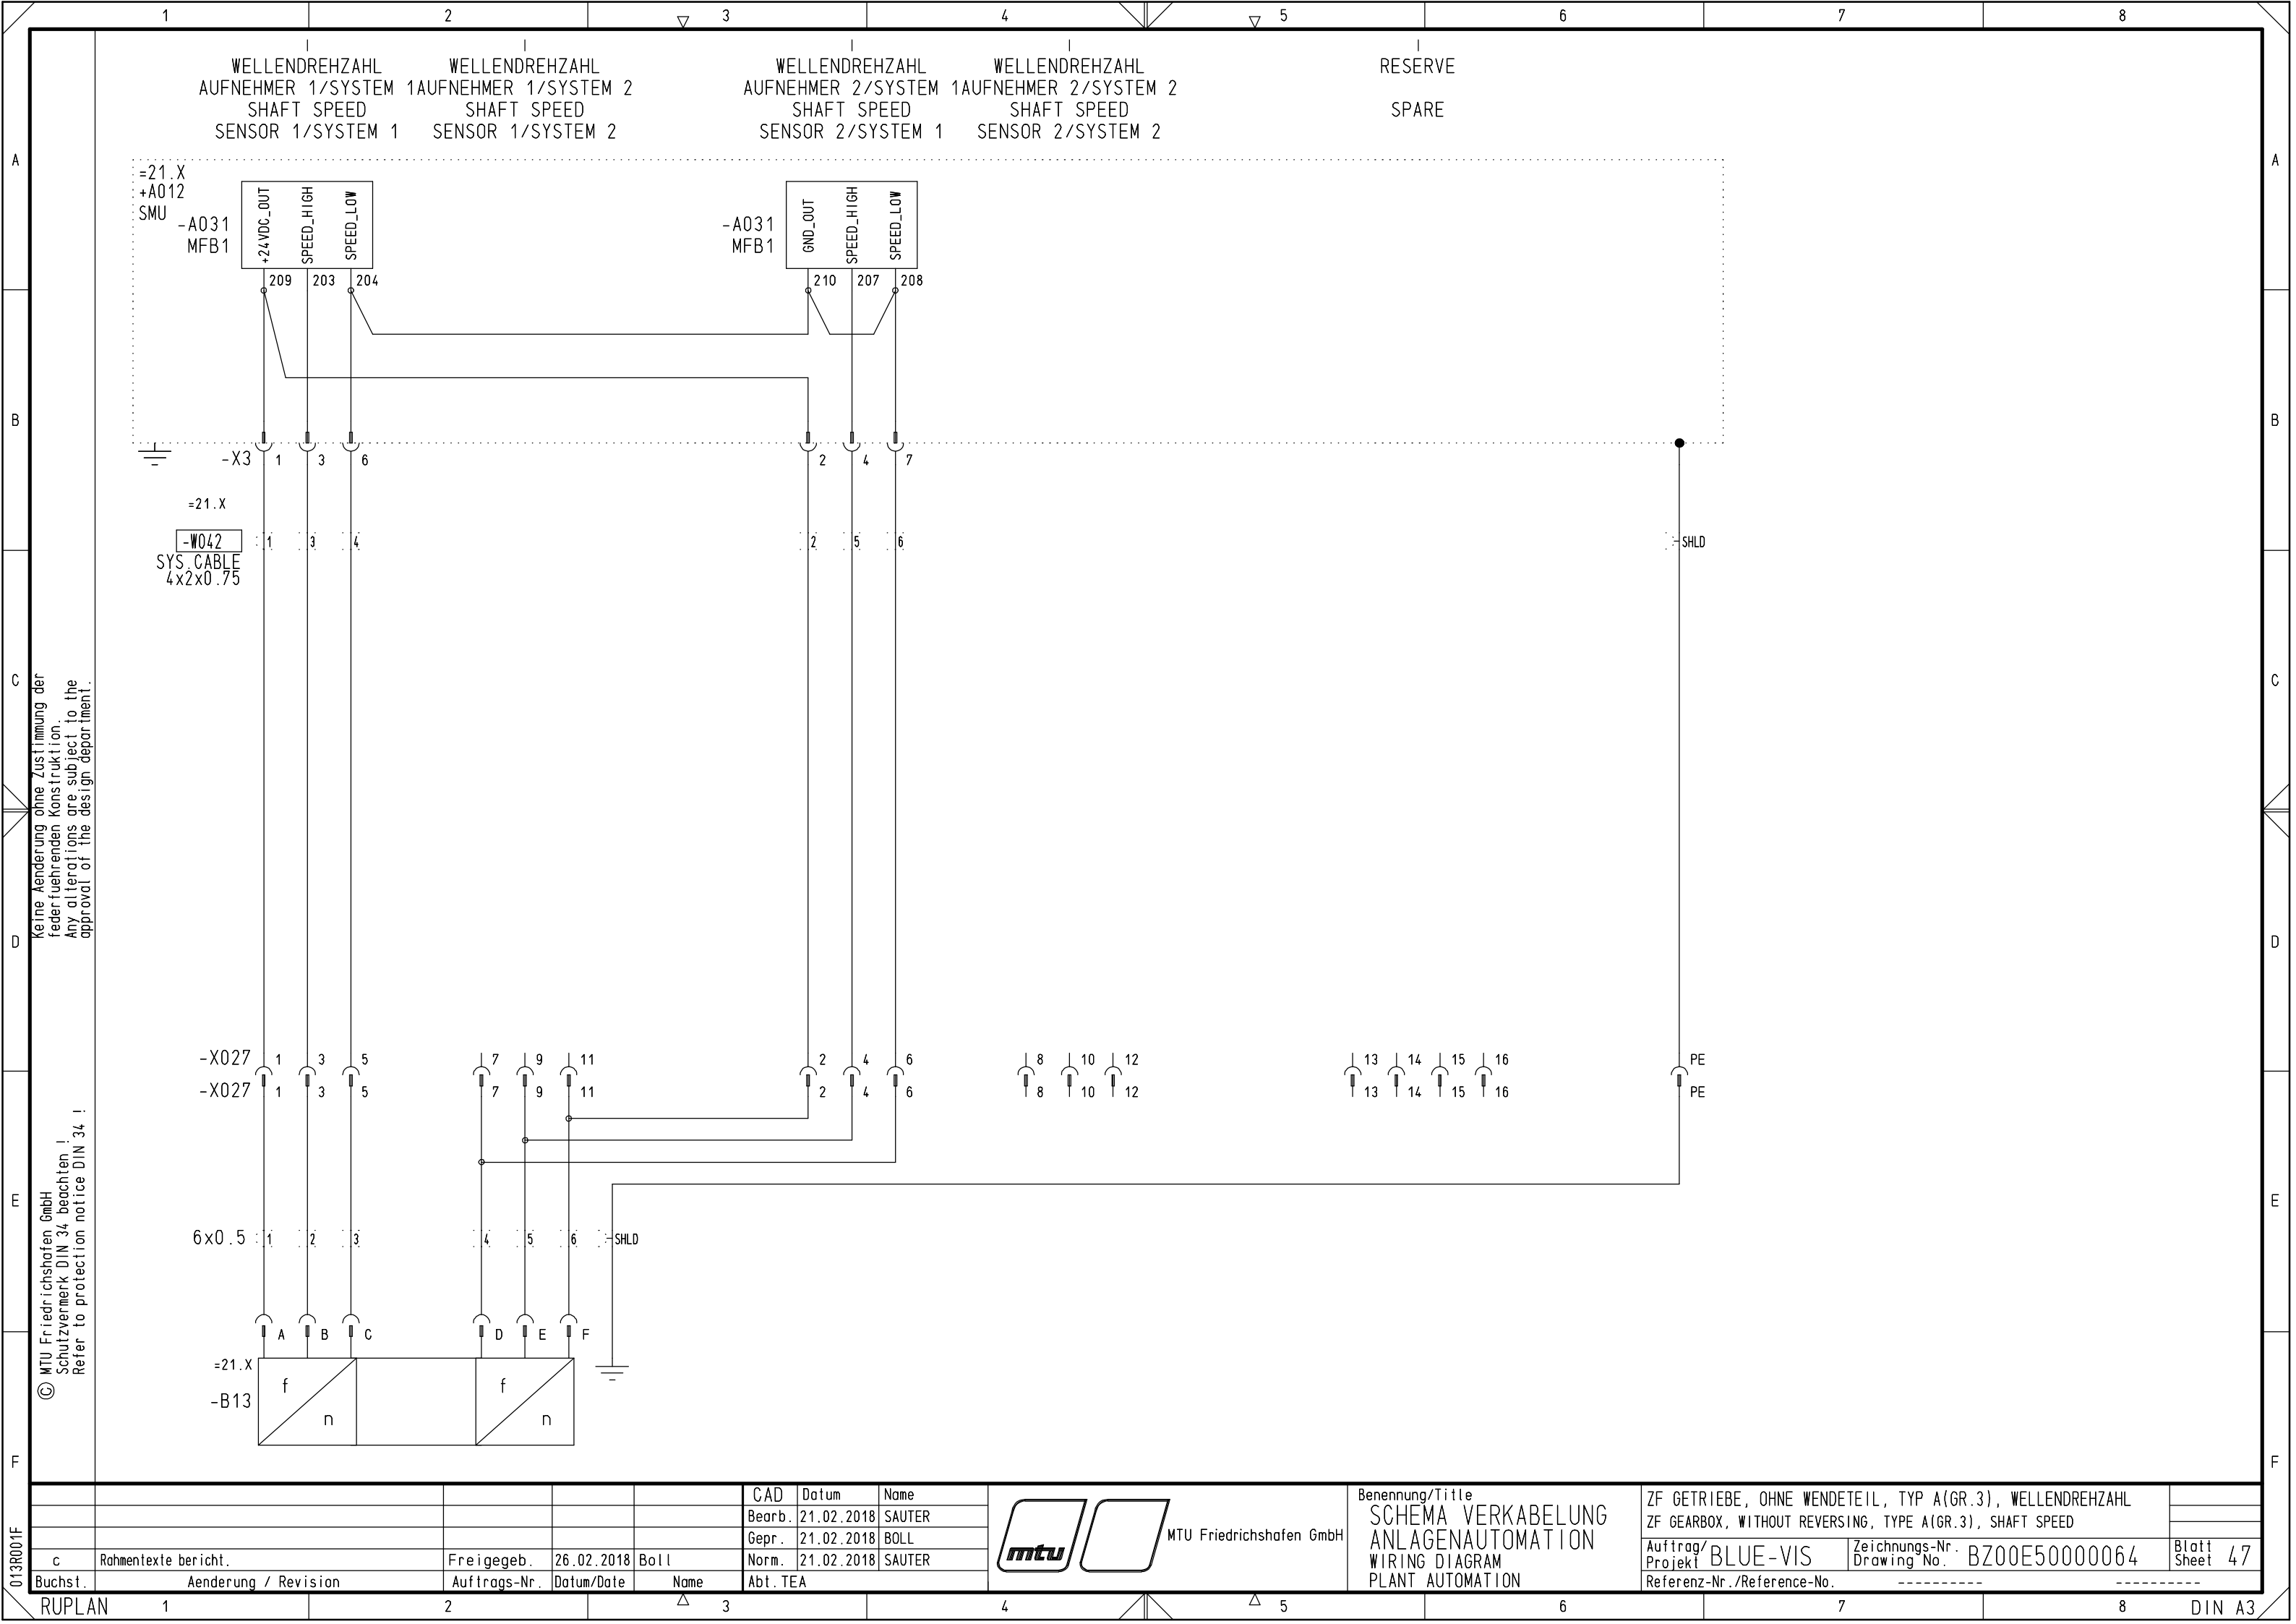

[illegible]

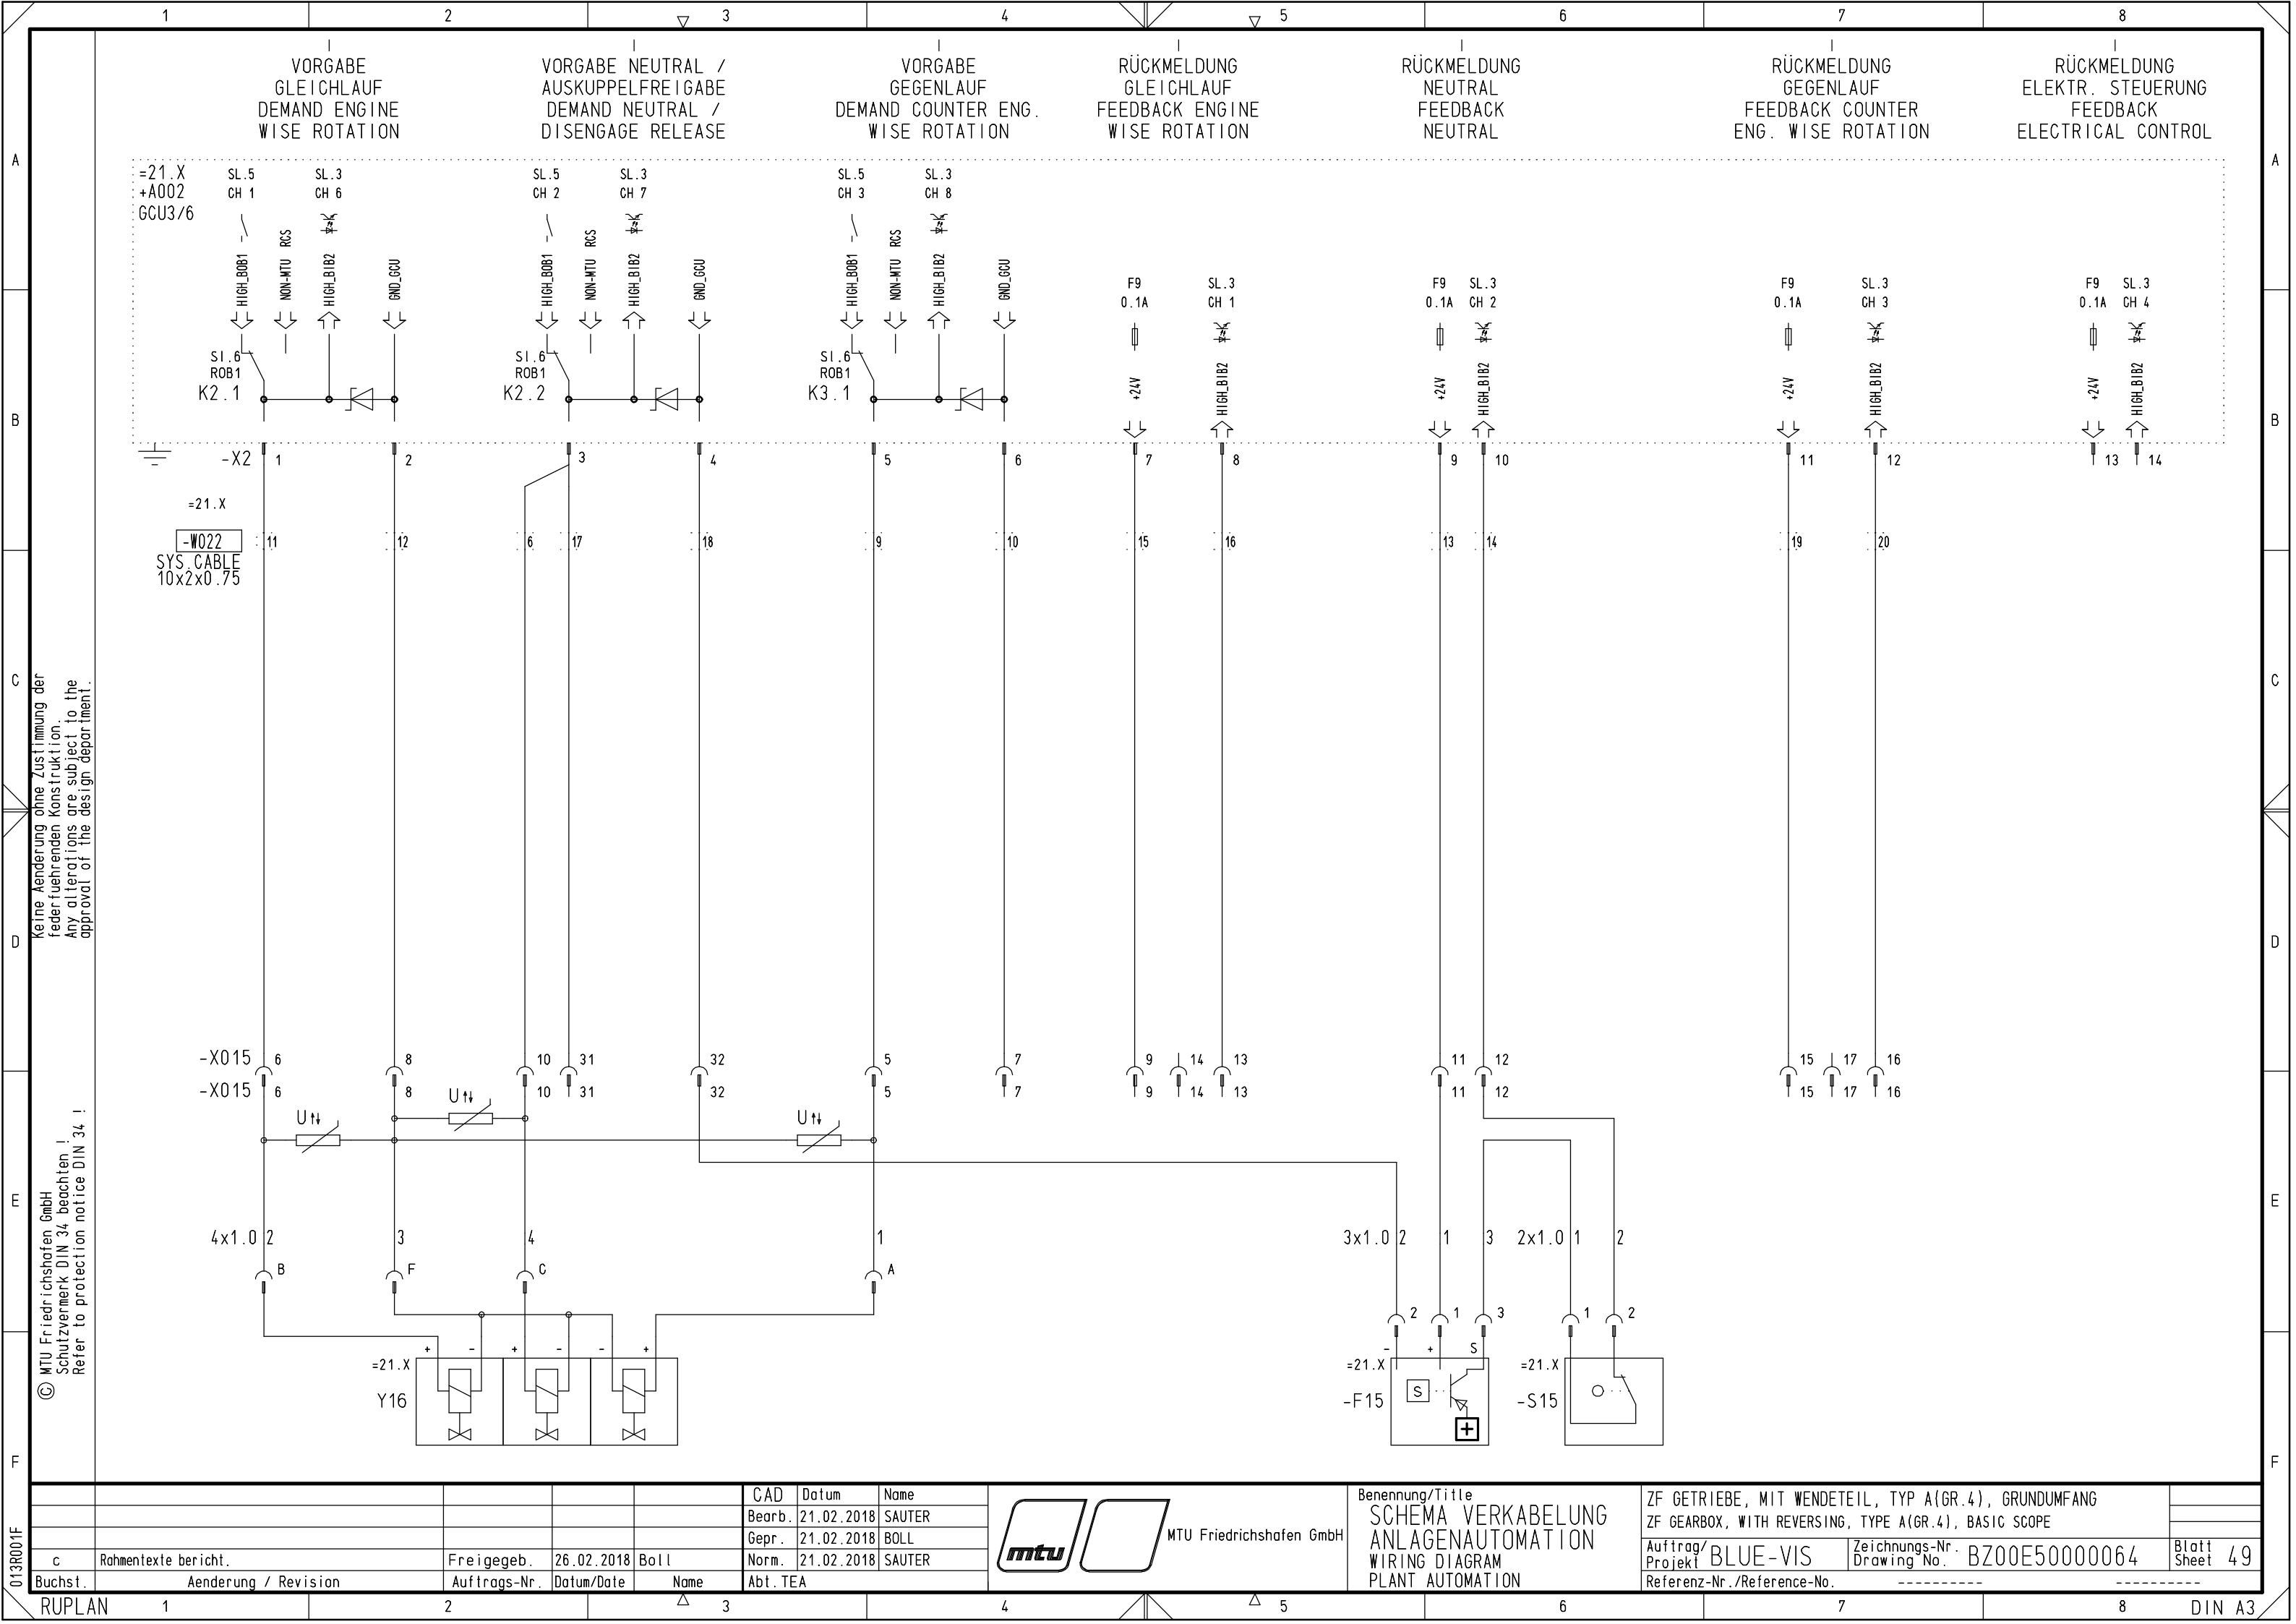

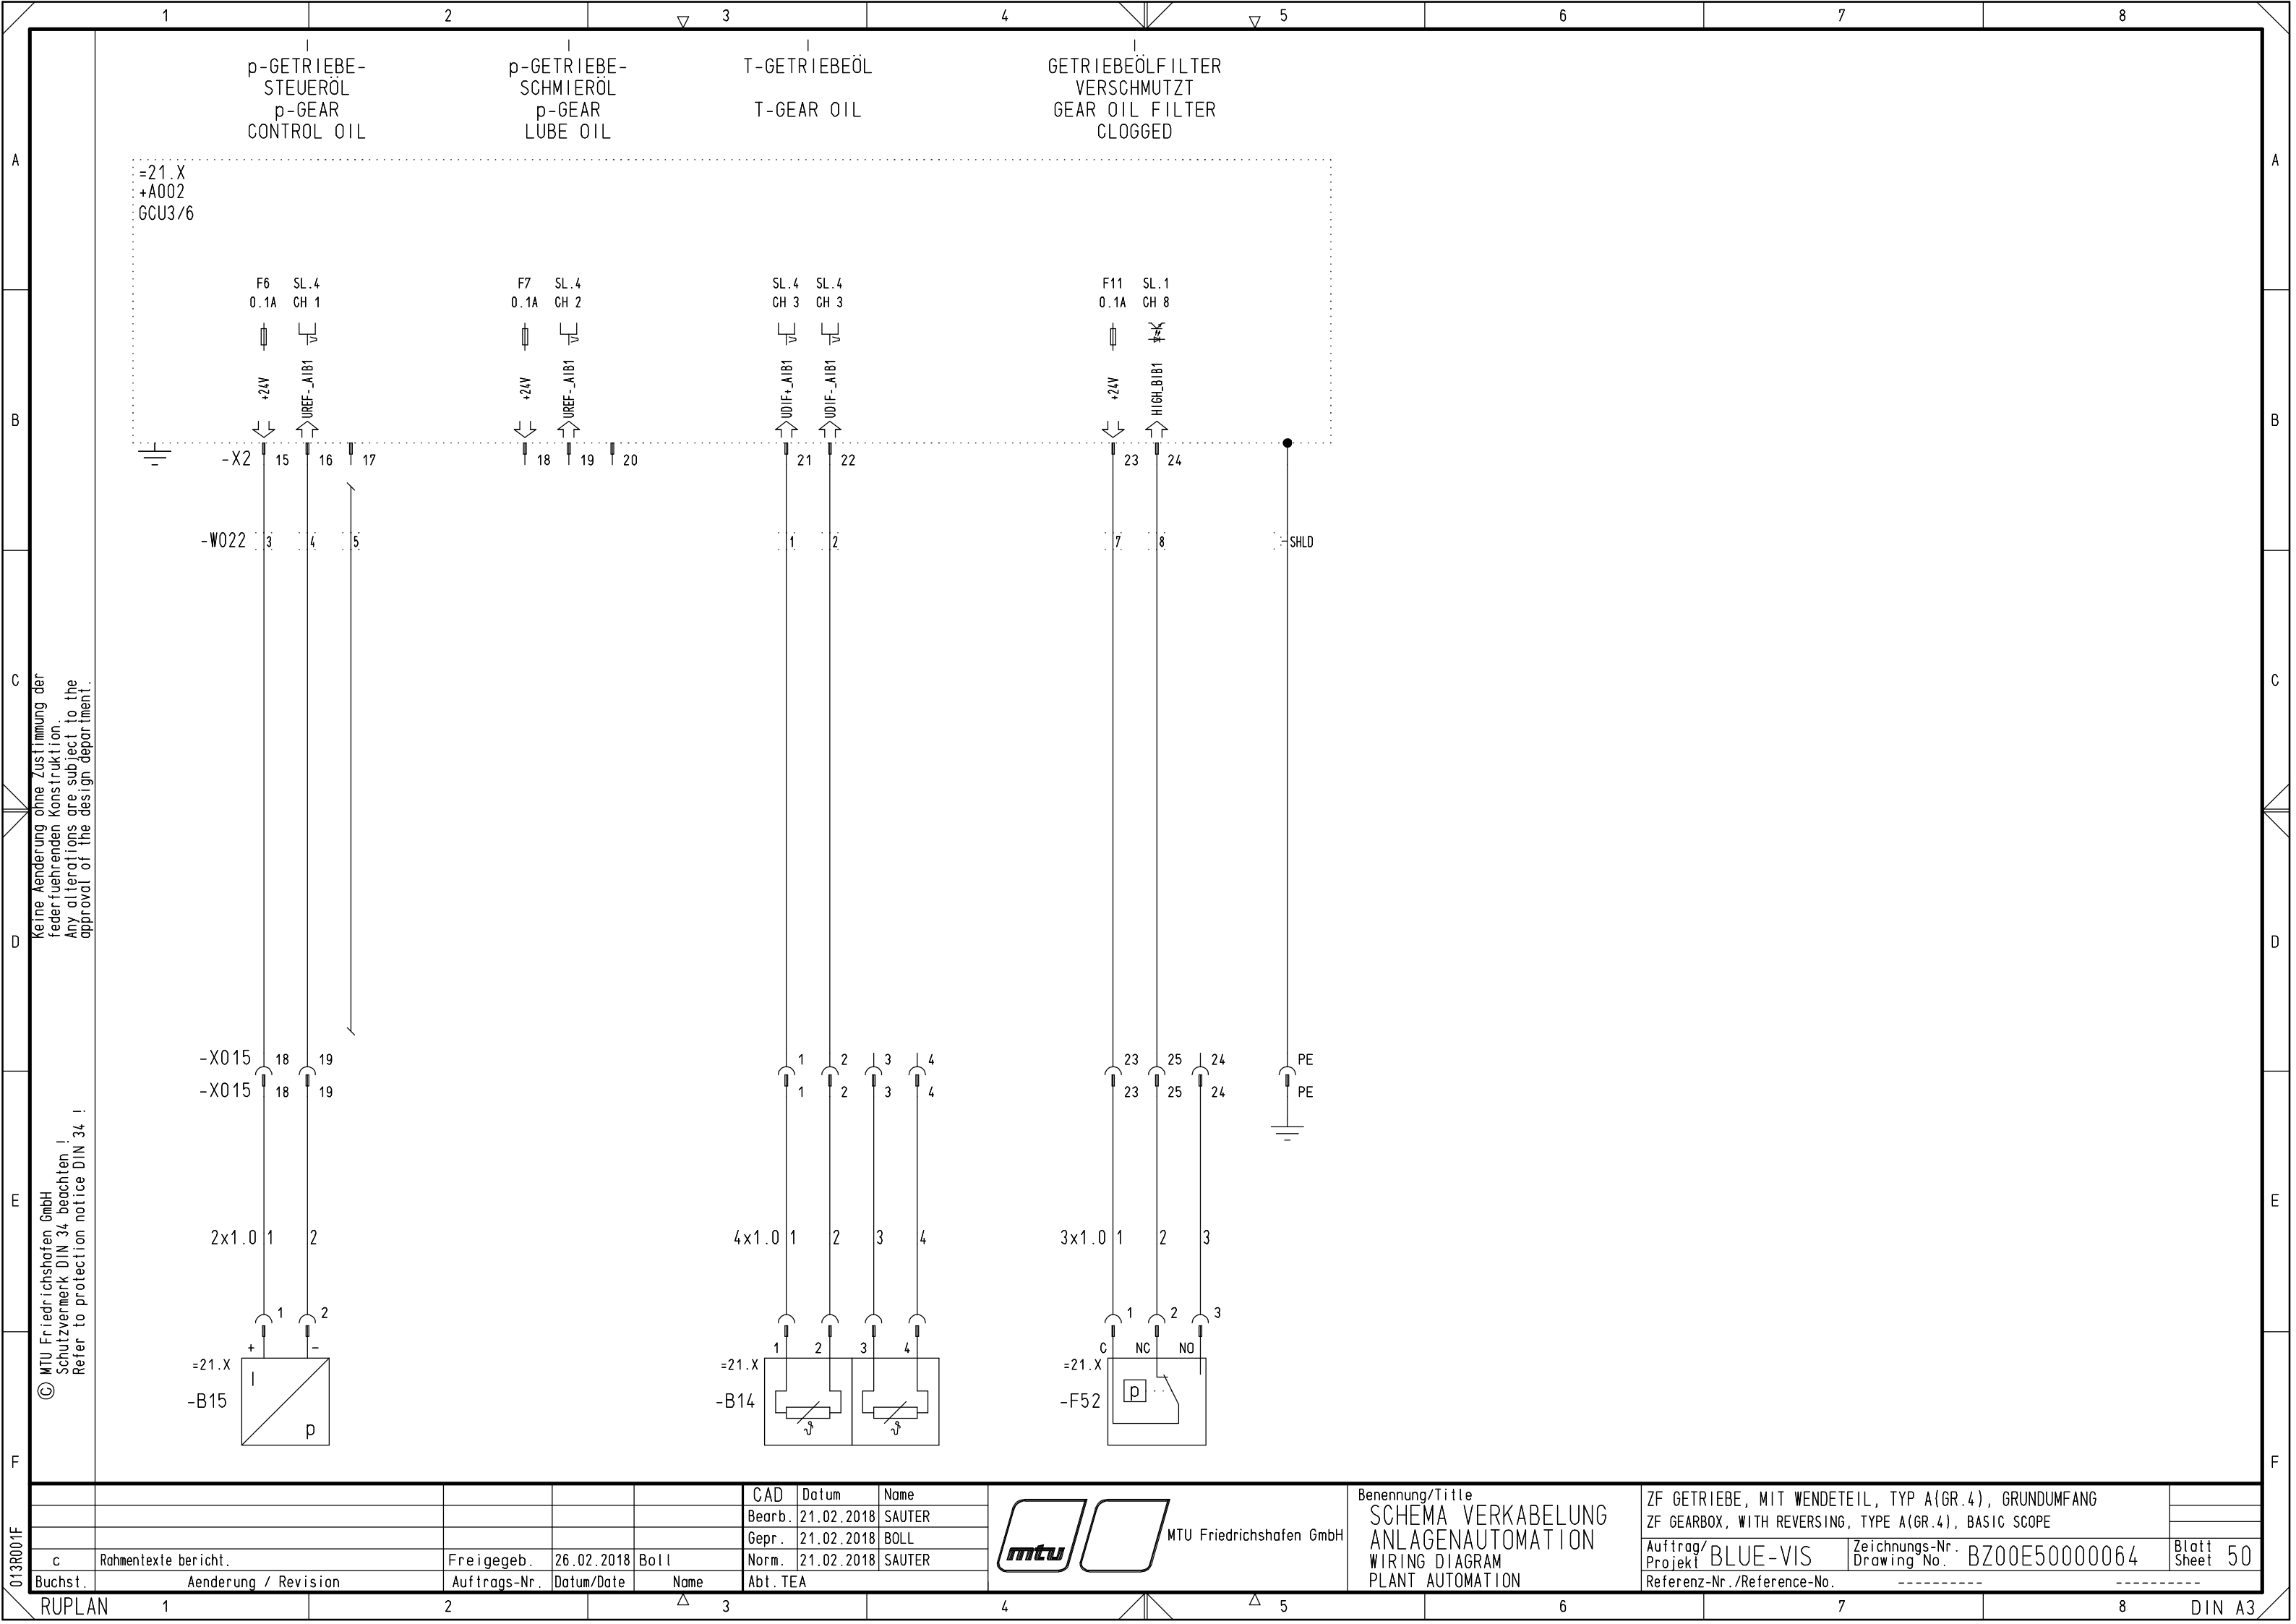


Keine Änderung ohne Zustimmung der
federführenden Konstruktion.
Any alterations are subject to the
approval of the design department.

© MTU Friedrichshafen GmbH
Schutzvermerk DIN 34 beachten !
Refer to protection notice DIN 34 !

013R001F

RUPLAN

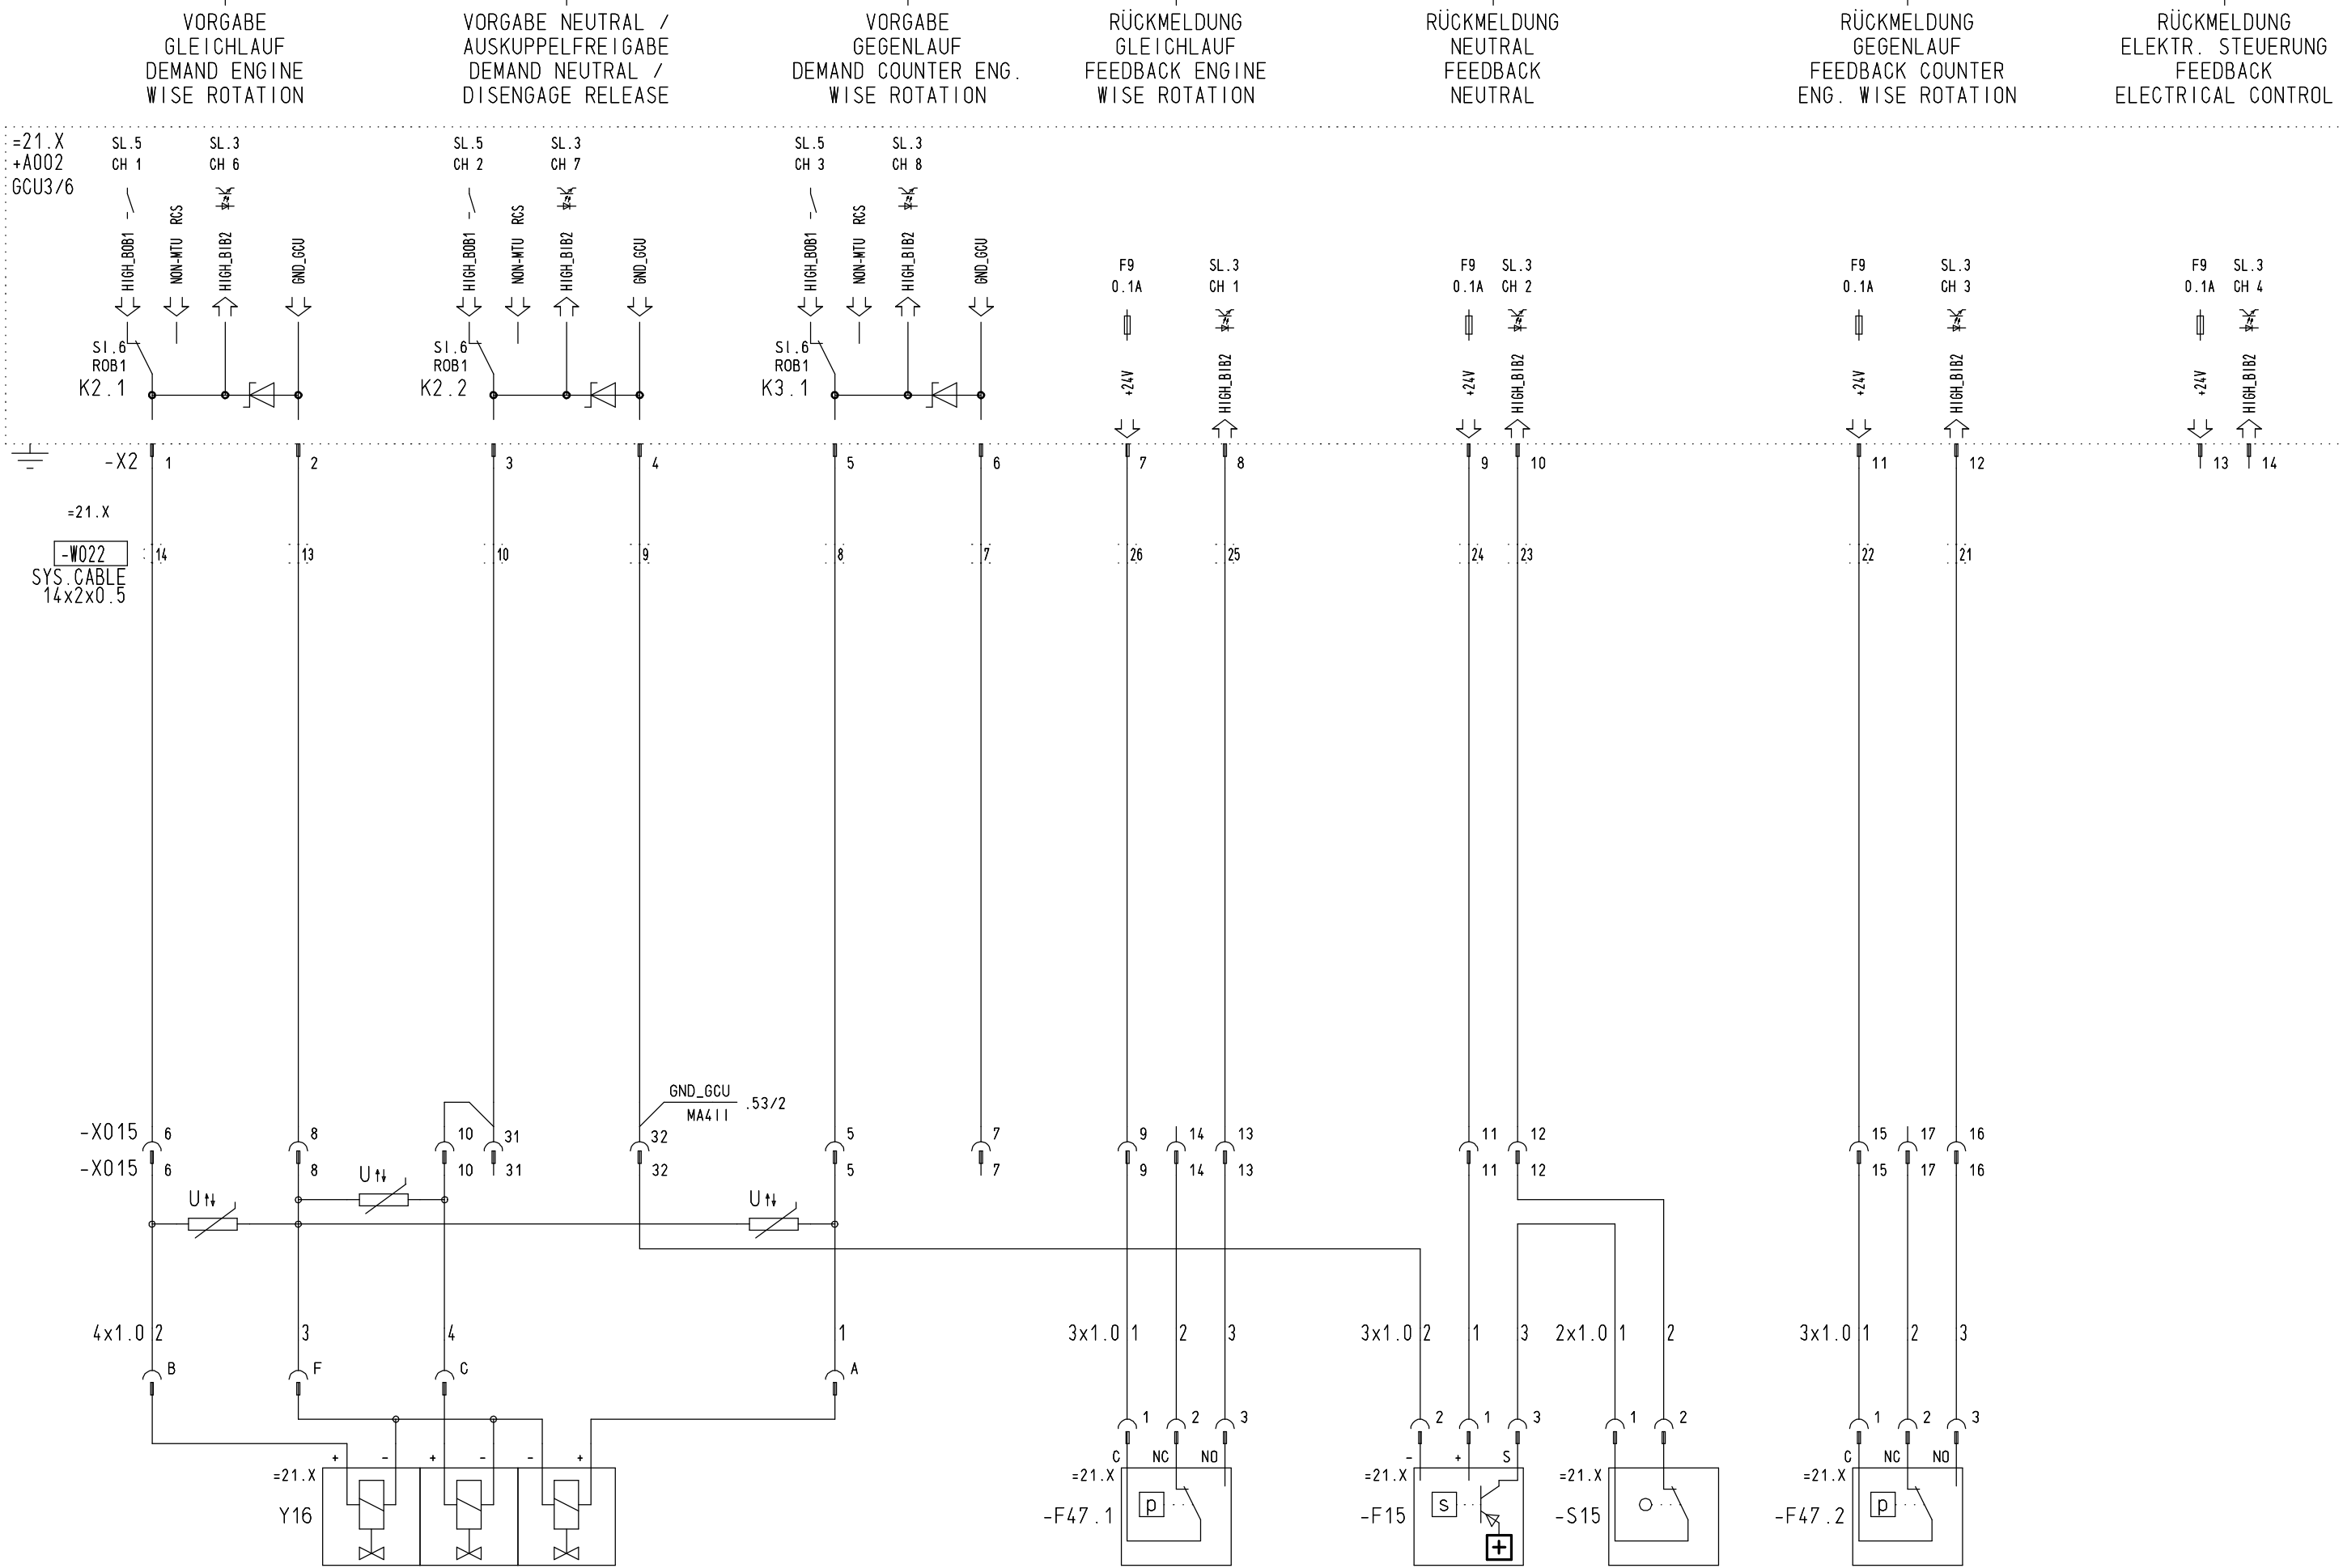

					CAD	Datum	Name
					Bearb.	21.02.2018	SAUTER
					Gedr.	21.02.2018	BOLL
					Norm.	21.02.2018	SAUTER
c	Rahmentexte bericht.	Freigegeb.	26.02.2018	Boll	Abt. TEA		
Buchst.	Änderung / Revision	Auftrags-Nr.	Datum/Date	Name			



MTU Friedrichshafen GmbH


Benennung/Title
SCHEMA VERKABELUNG
ANLAGENAUTOMATION
WIRING DIAGRAM
PLANT AUTOMATION


ZF GETRIEBE, MIT WENDETEIL, TYP A (GR.4), ERWEIT. UMFANG
ZF GEARBOX, WITH REVERSING, TYPE A (GR.4), EXTENDED SCOPE


Auftrag/Projekt
BLUE-VIS
Zeichnungs-Nr.
Drawing No. BZ00E50000064
Referenz-Nr./Reference-No. -----

Blatt
Sheet 51


DIN A3

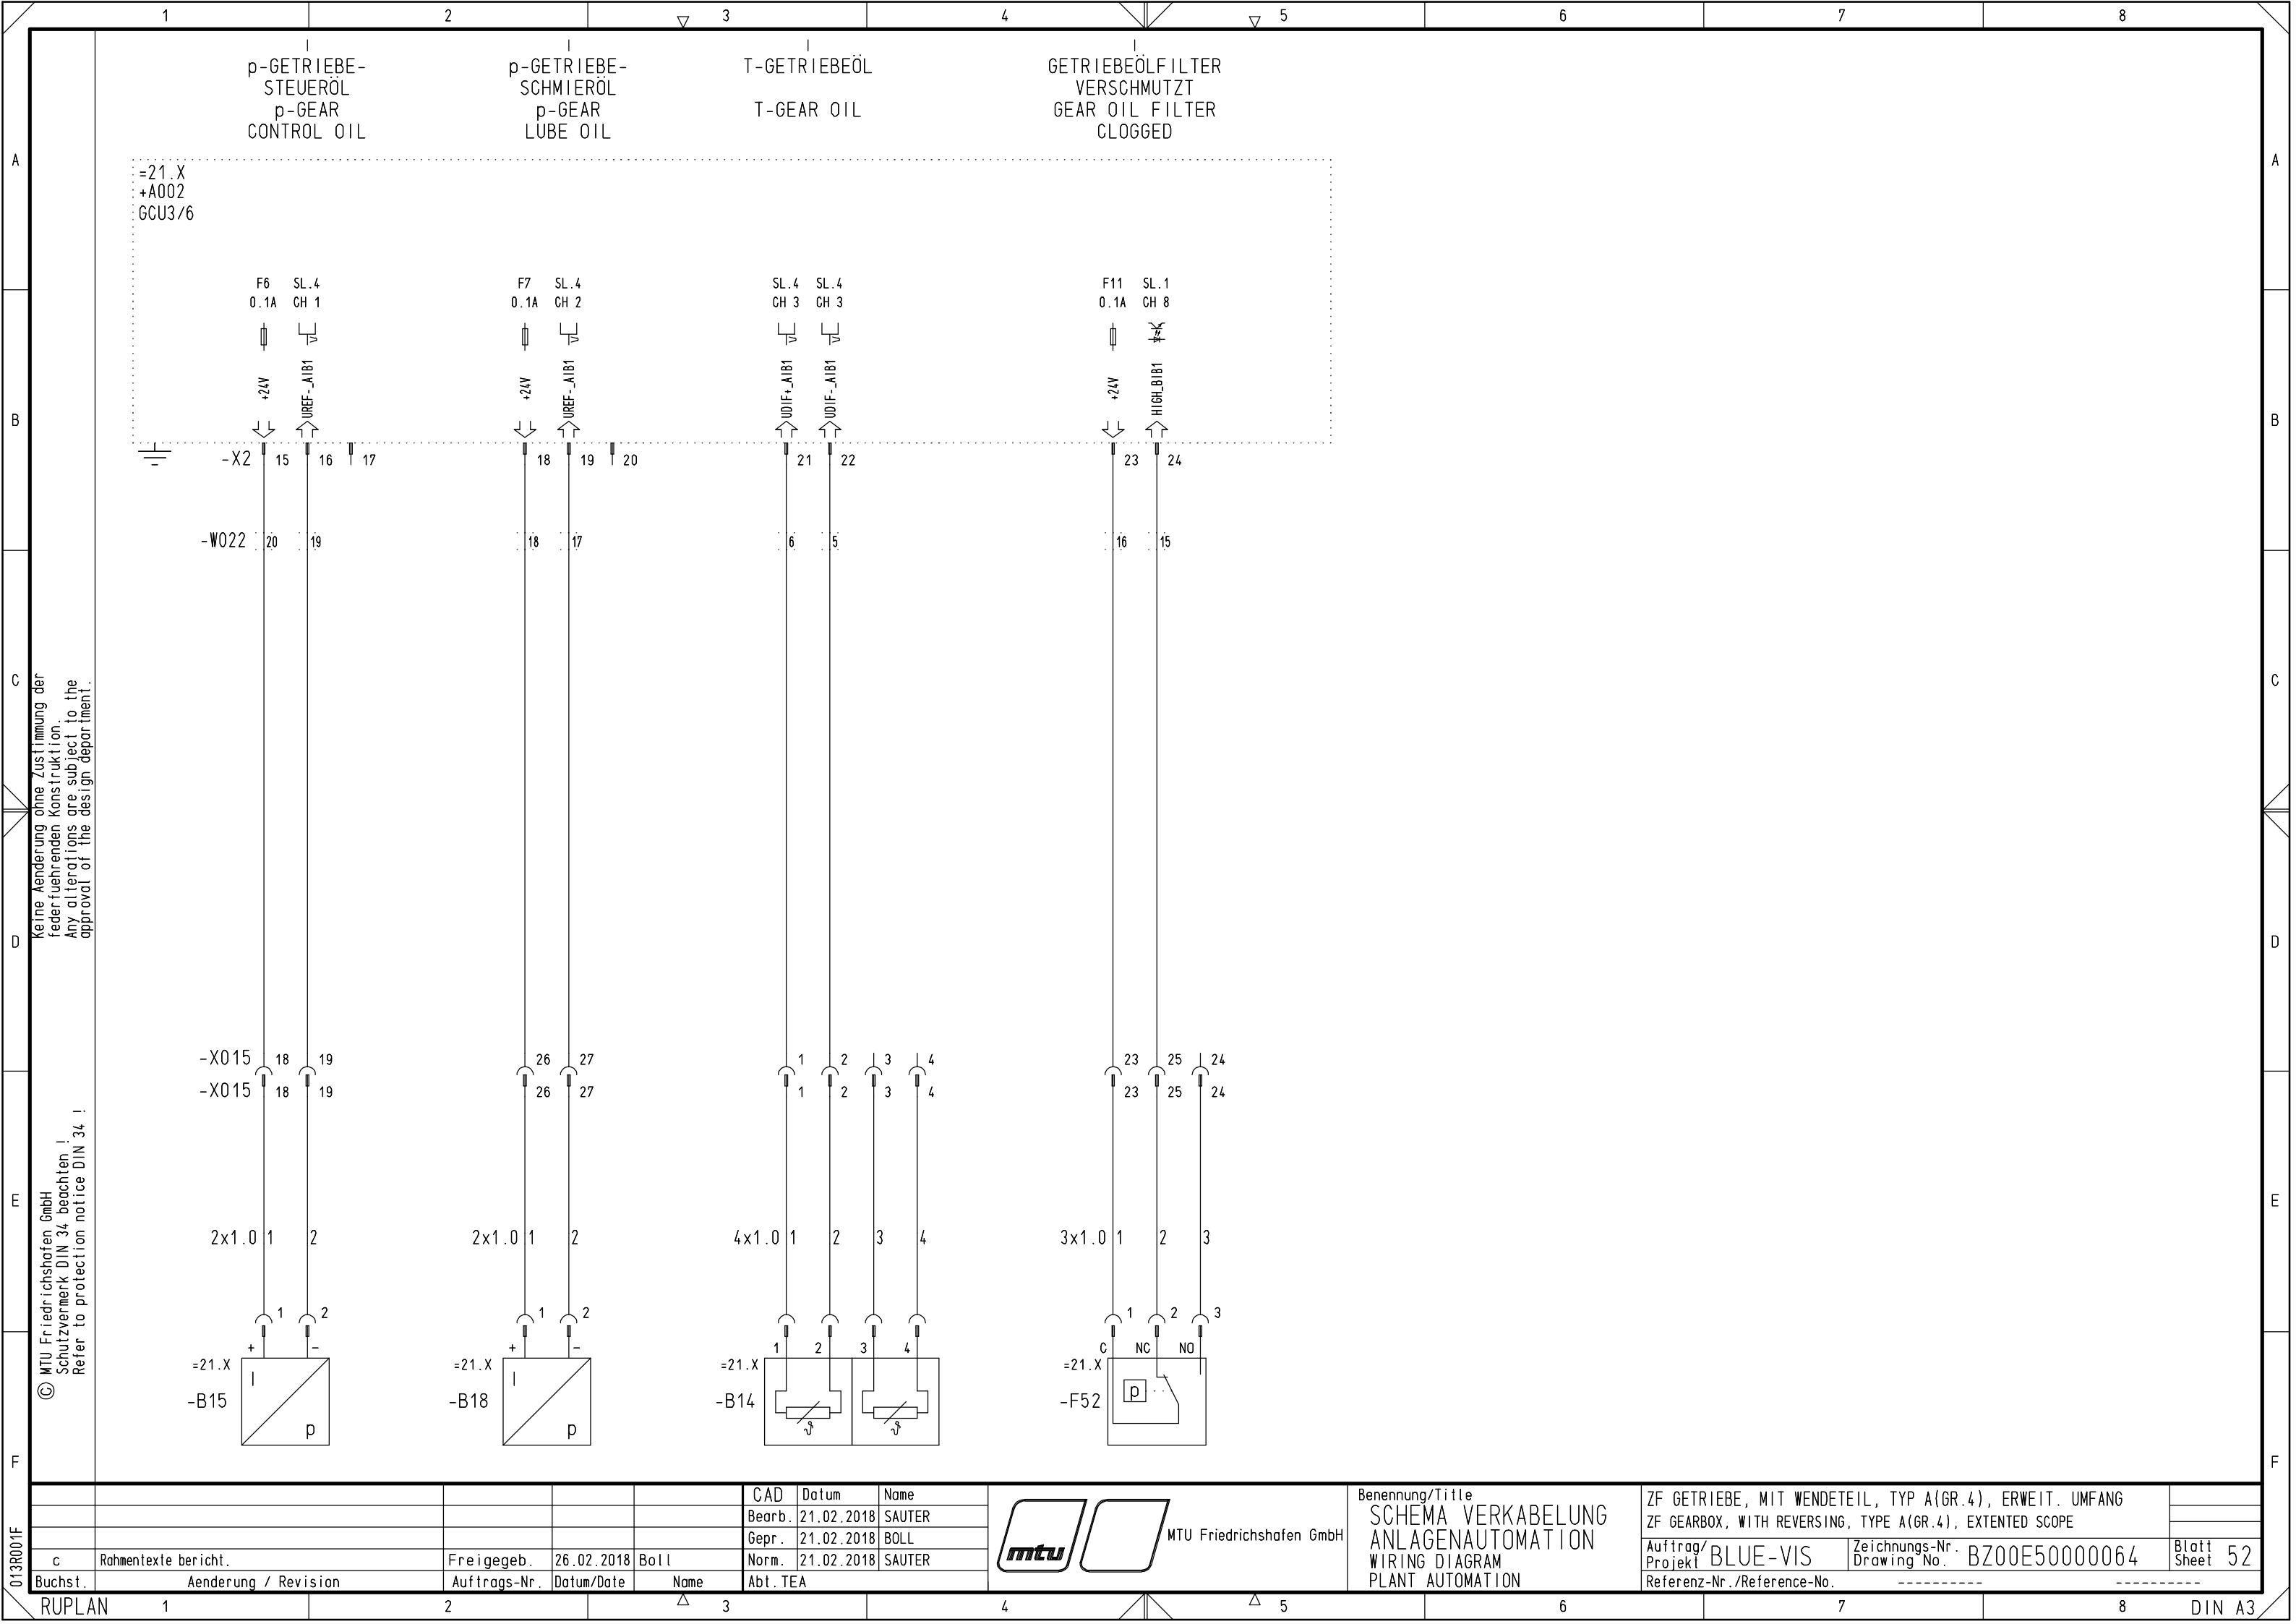


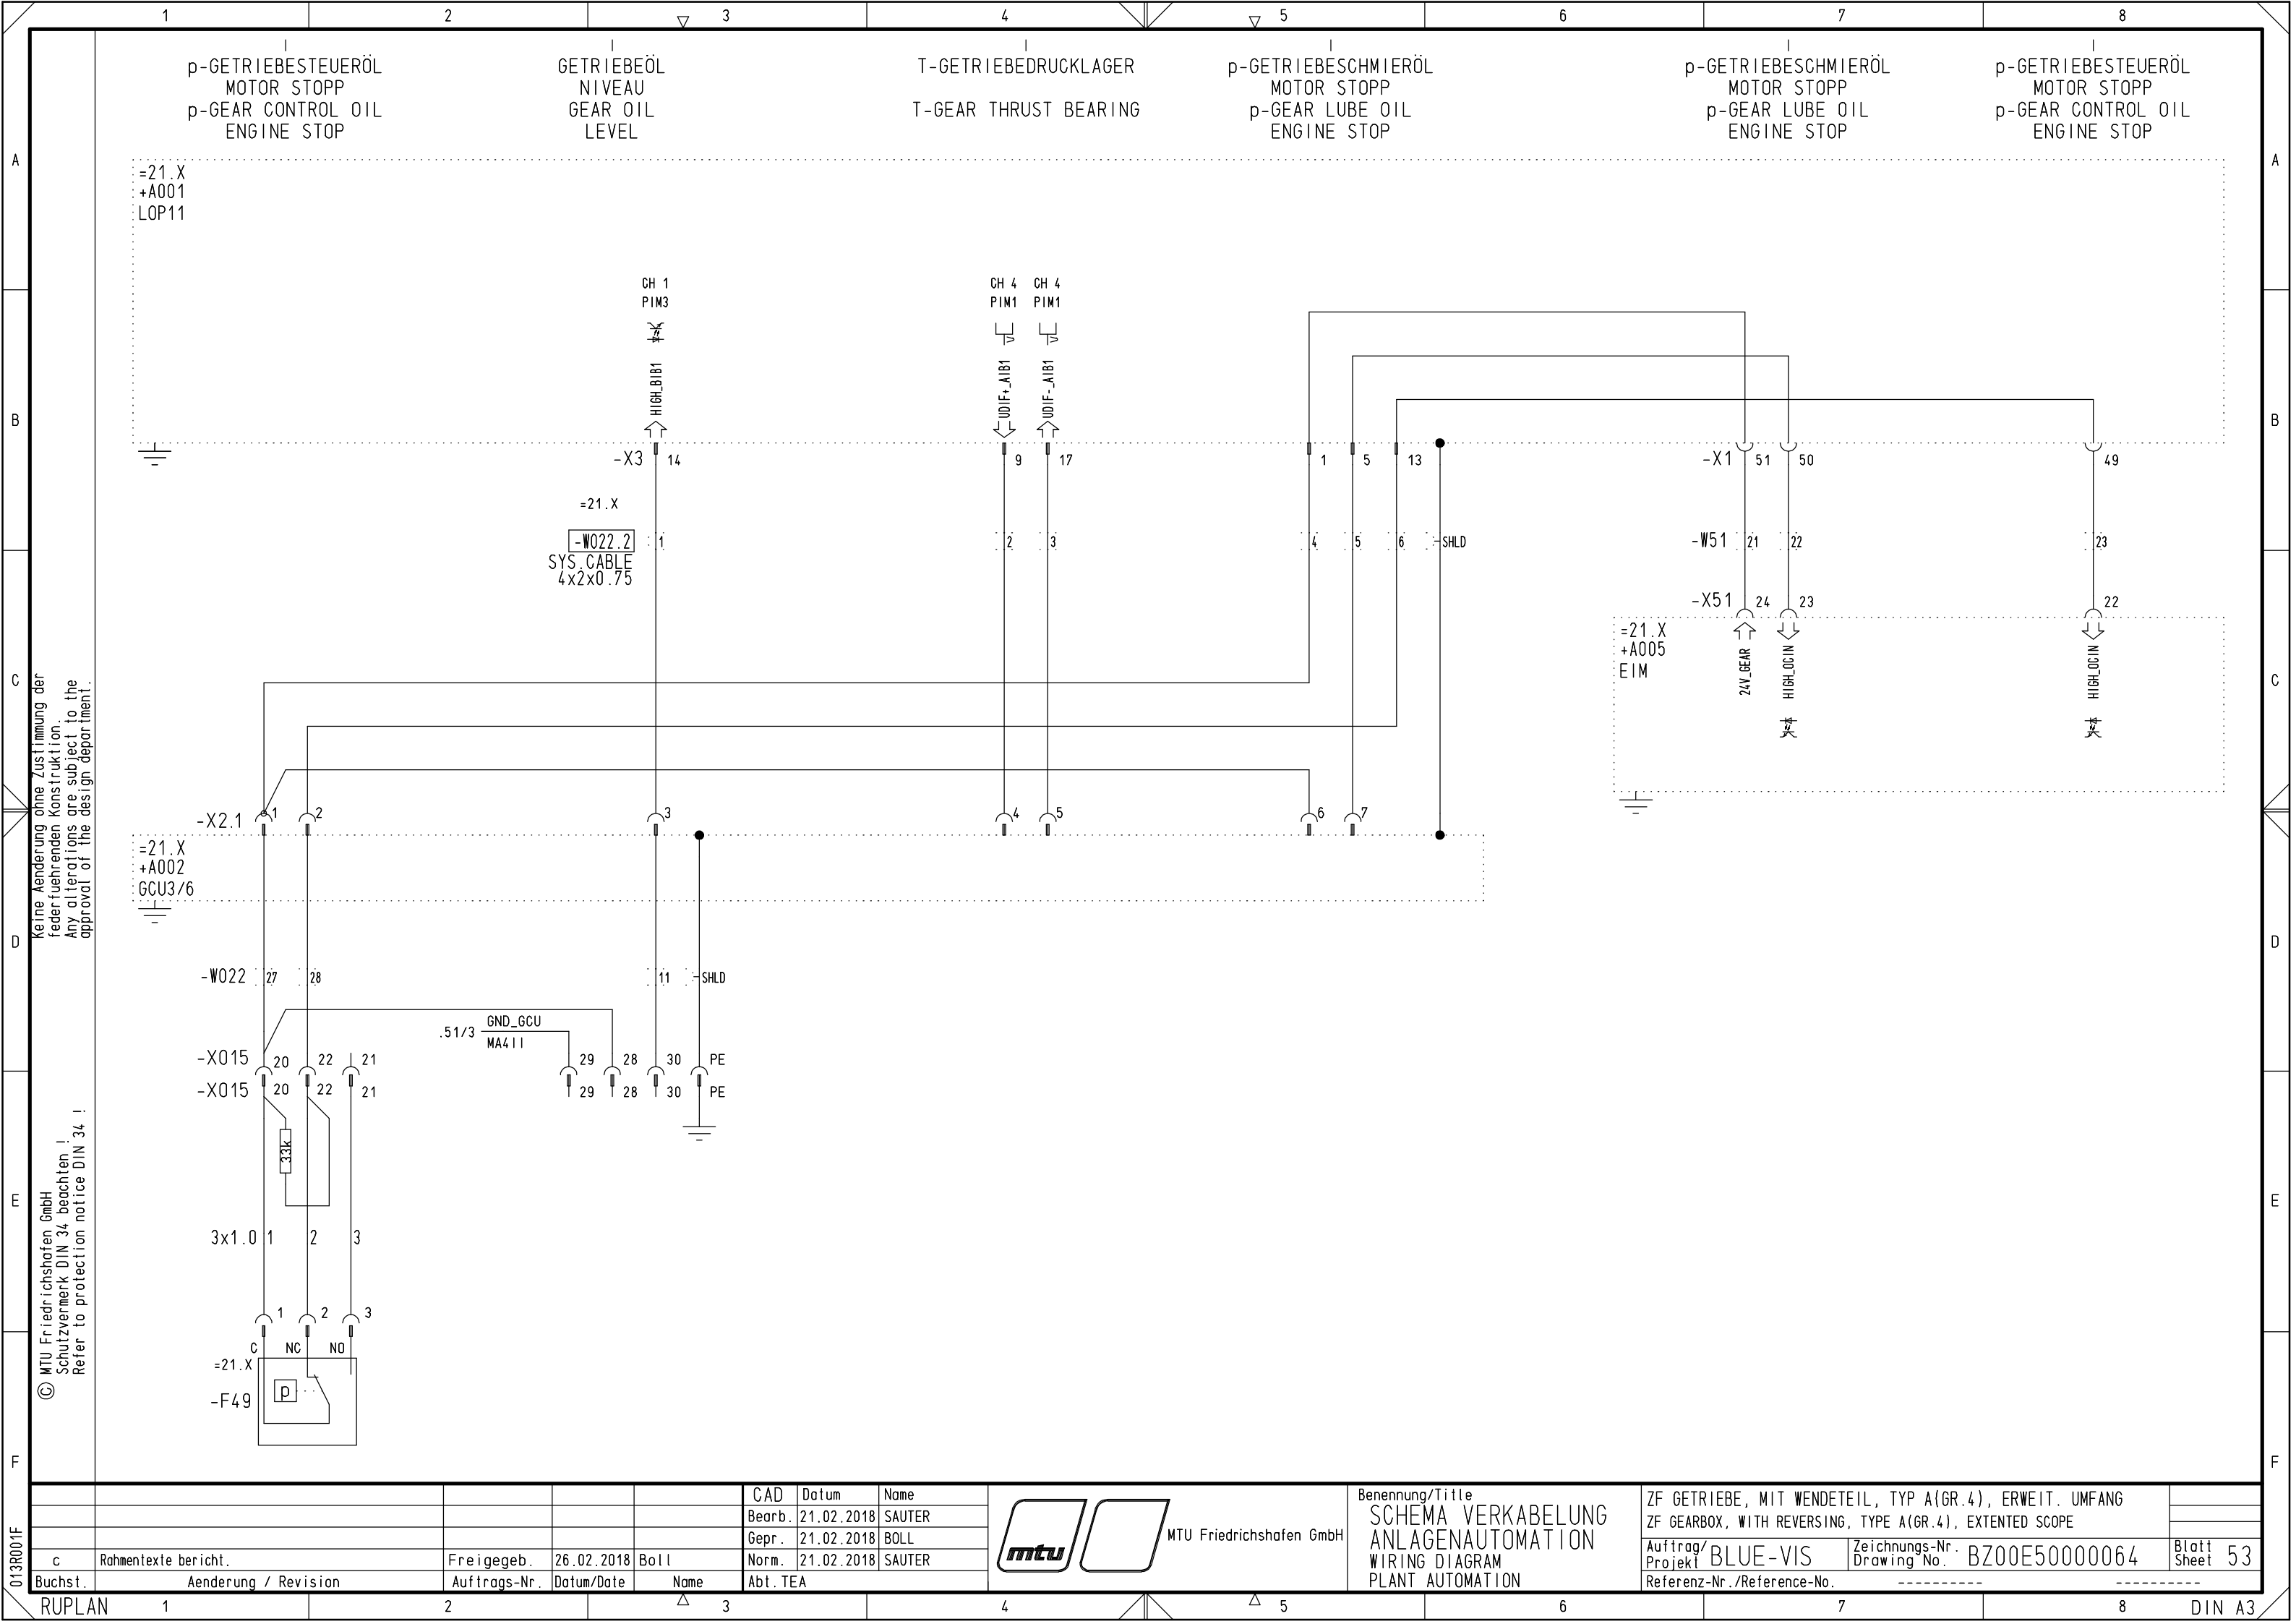


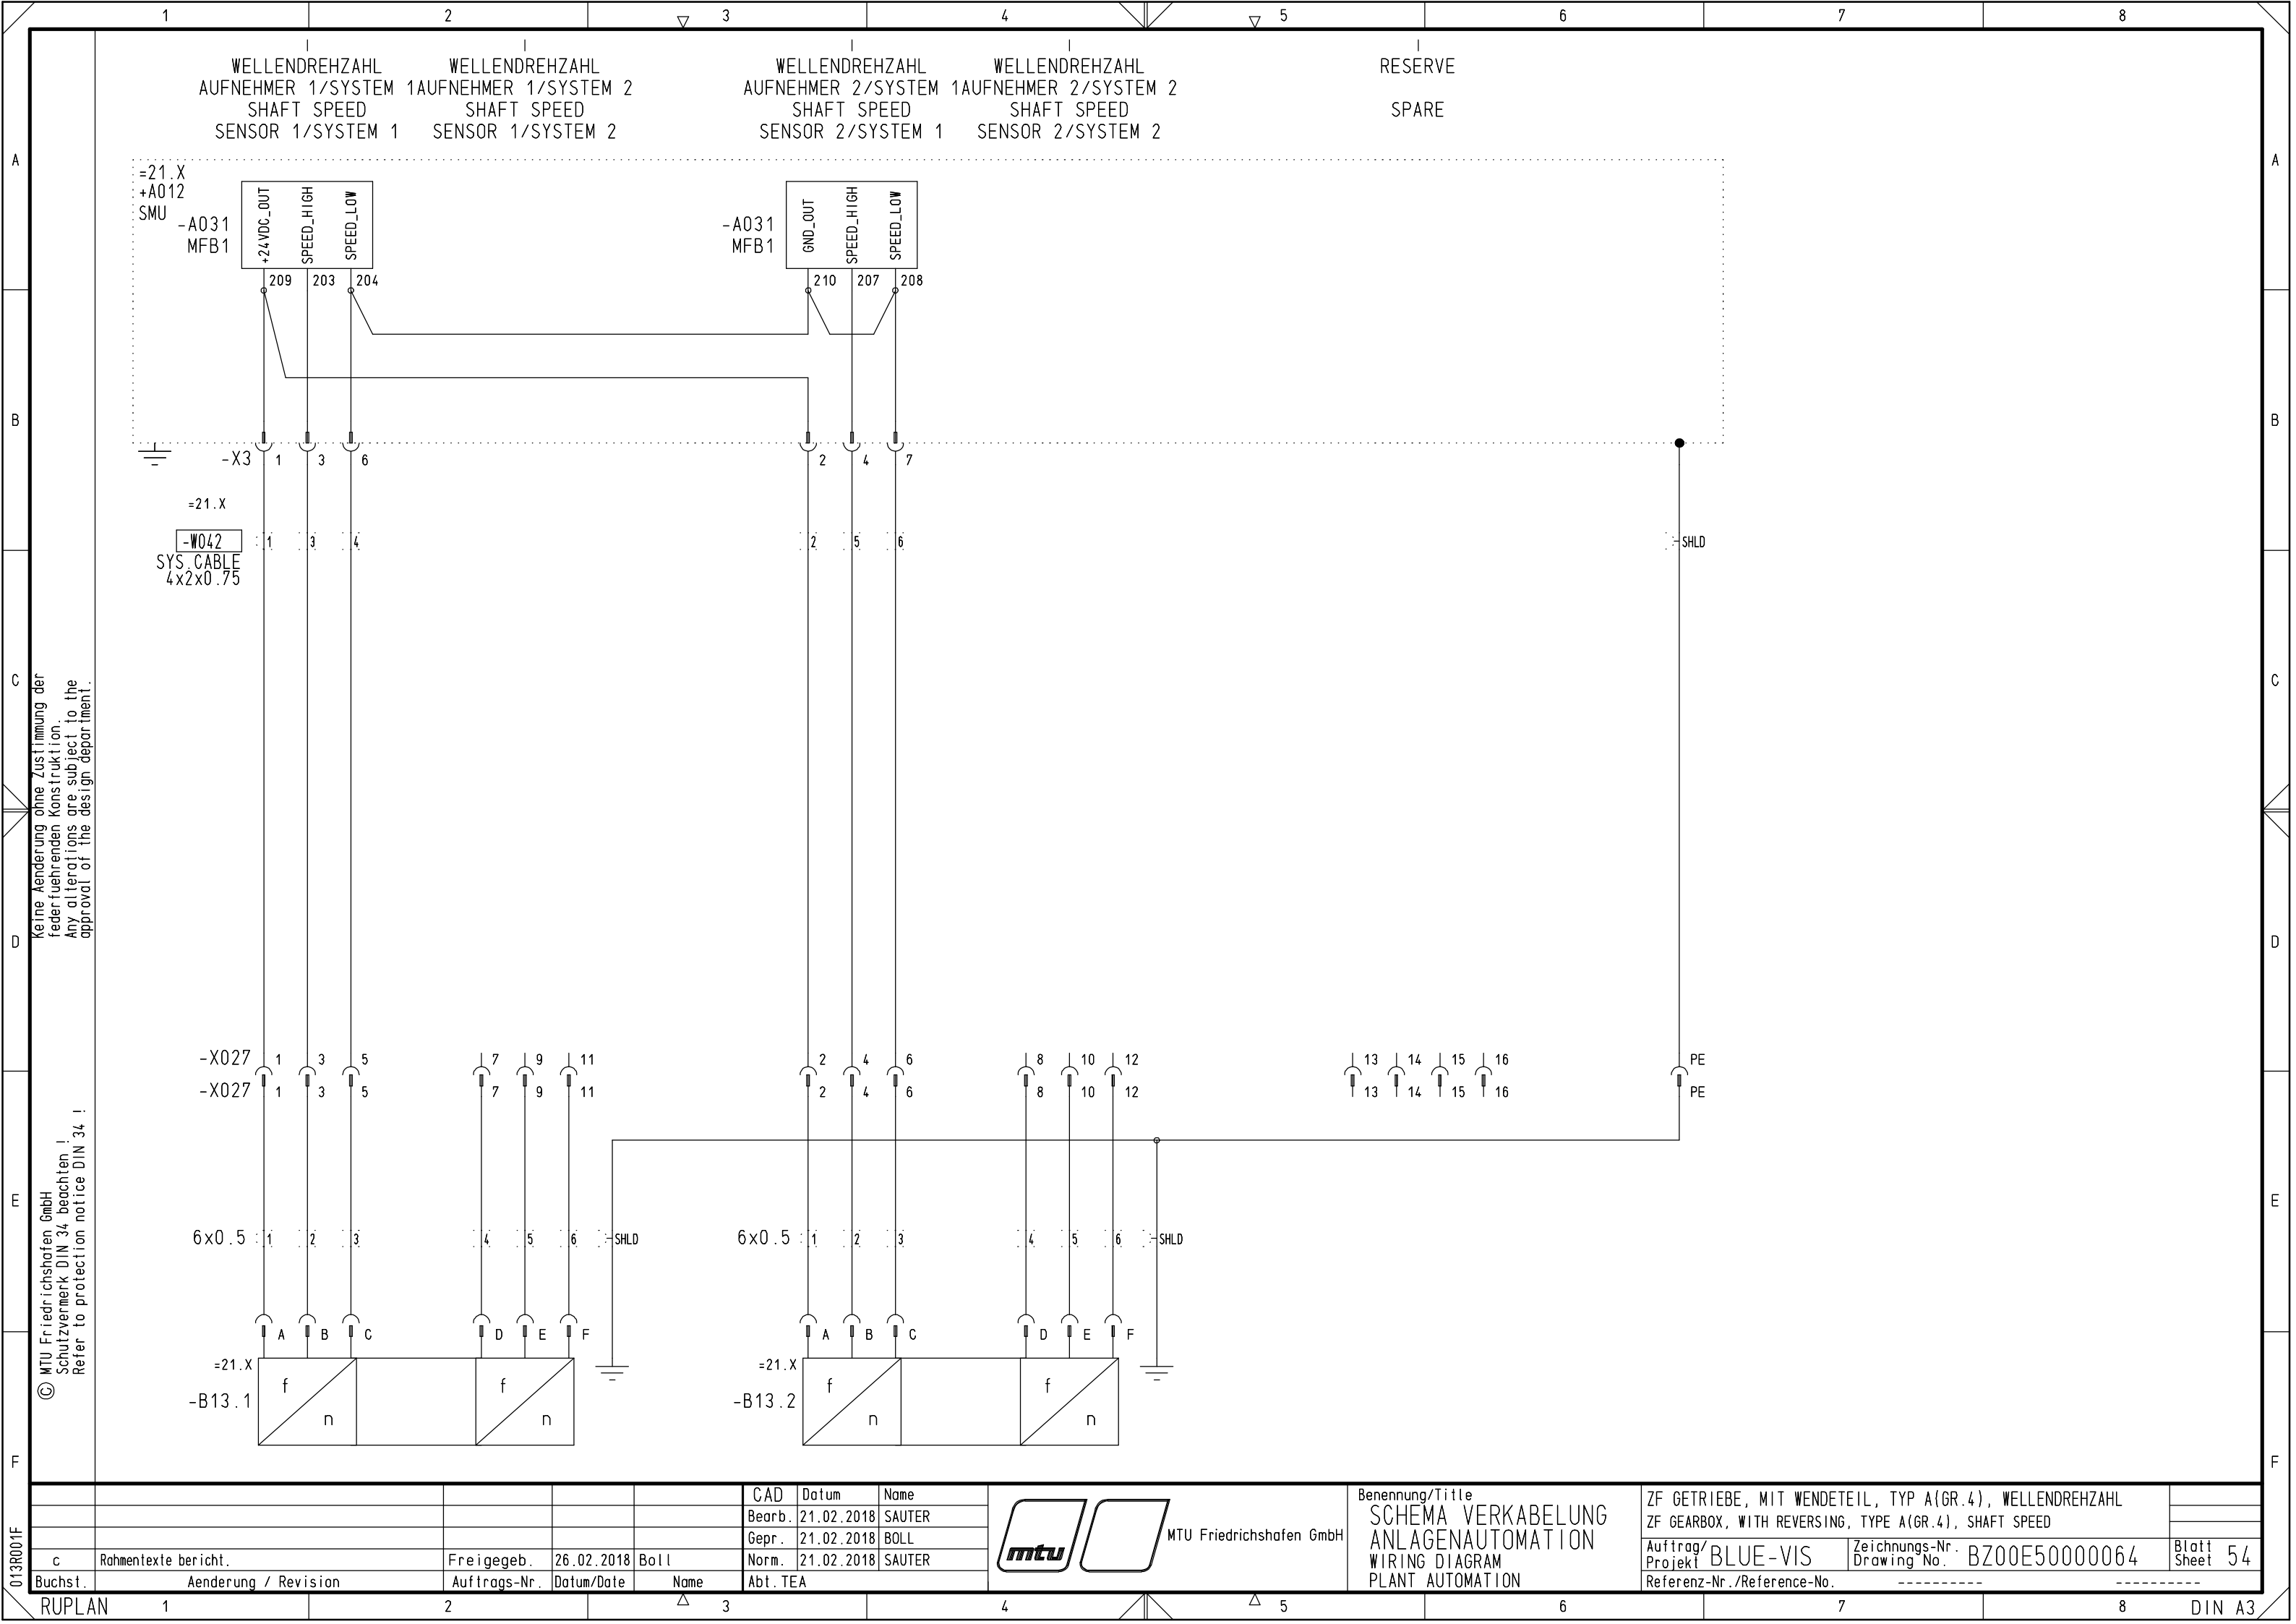


[illegible]

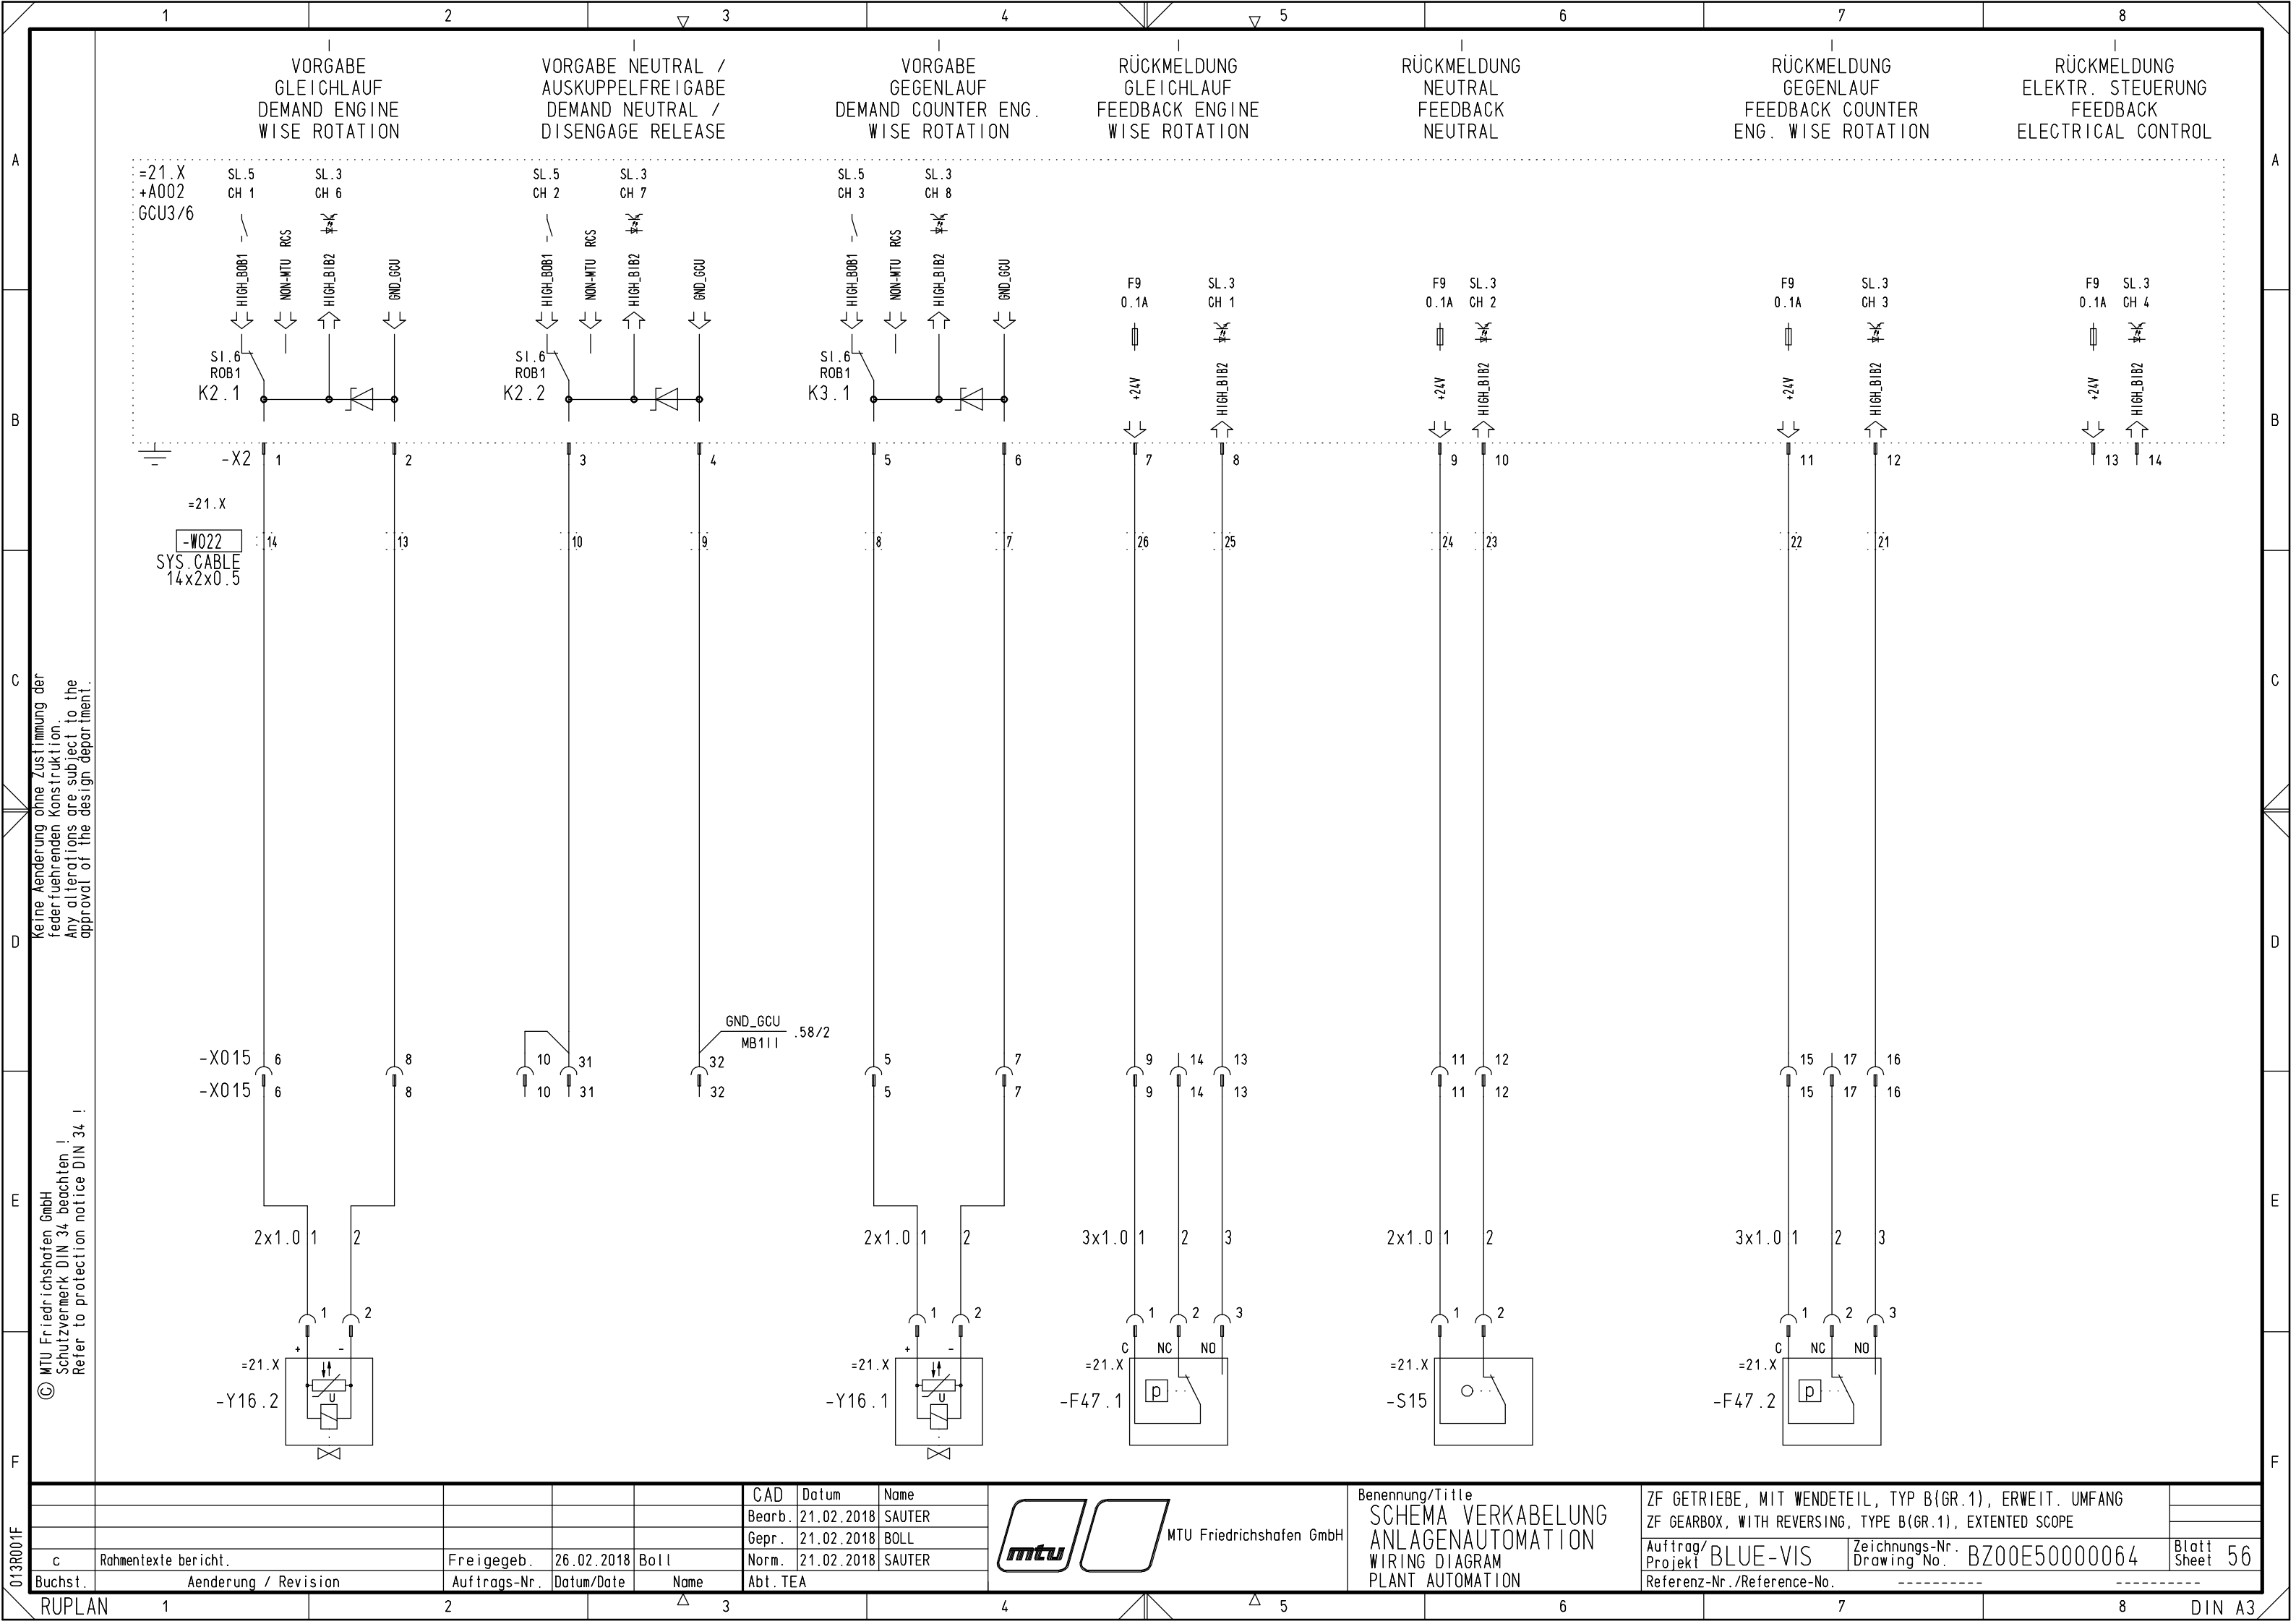


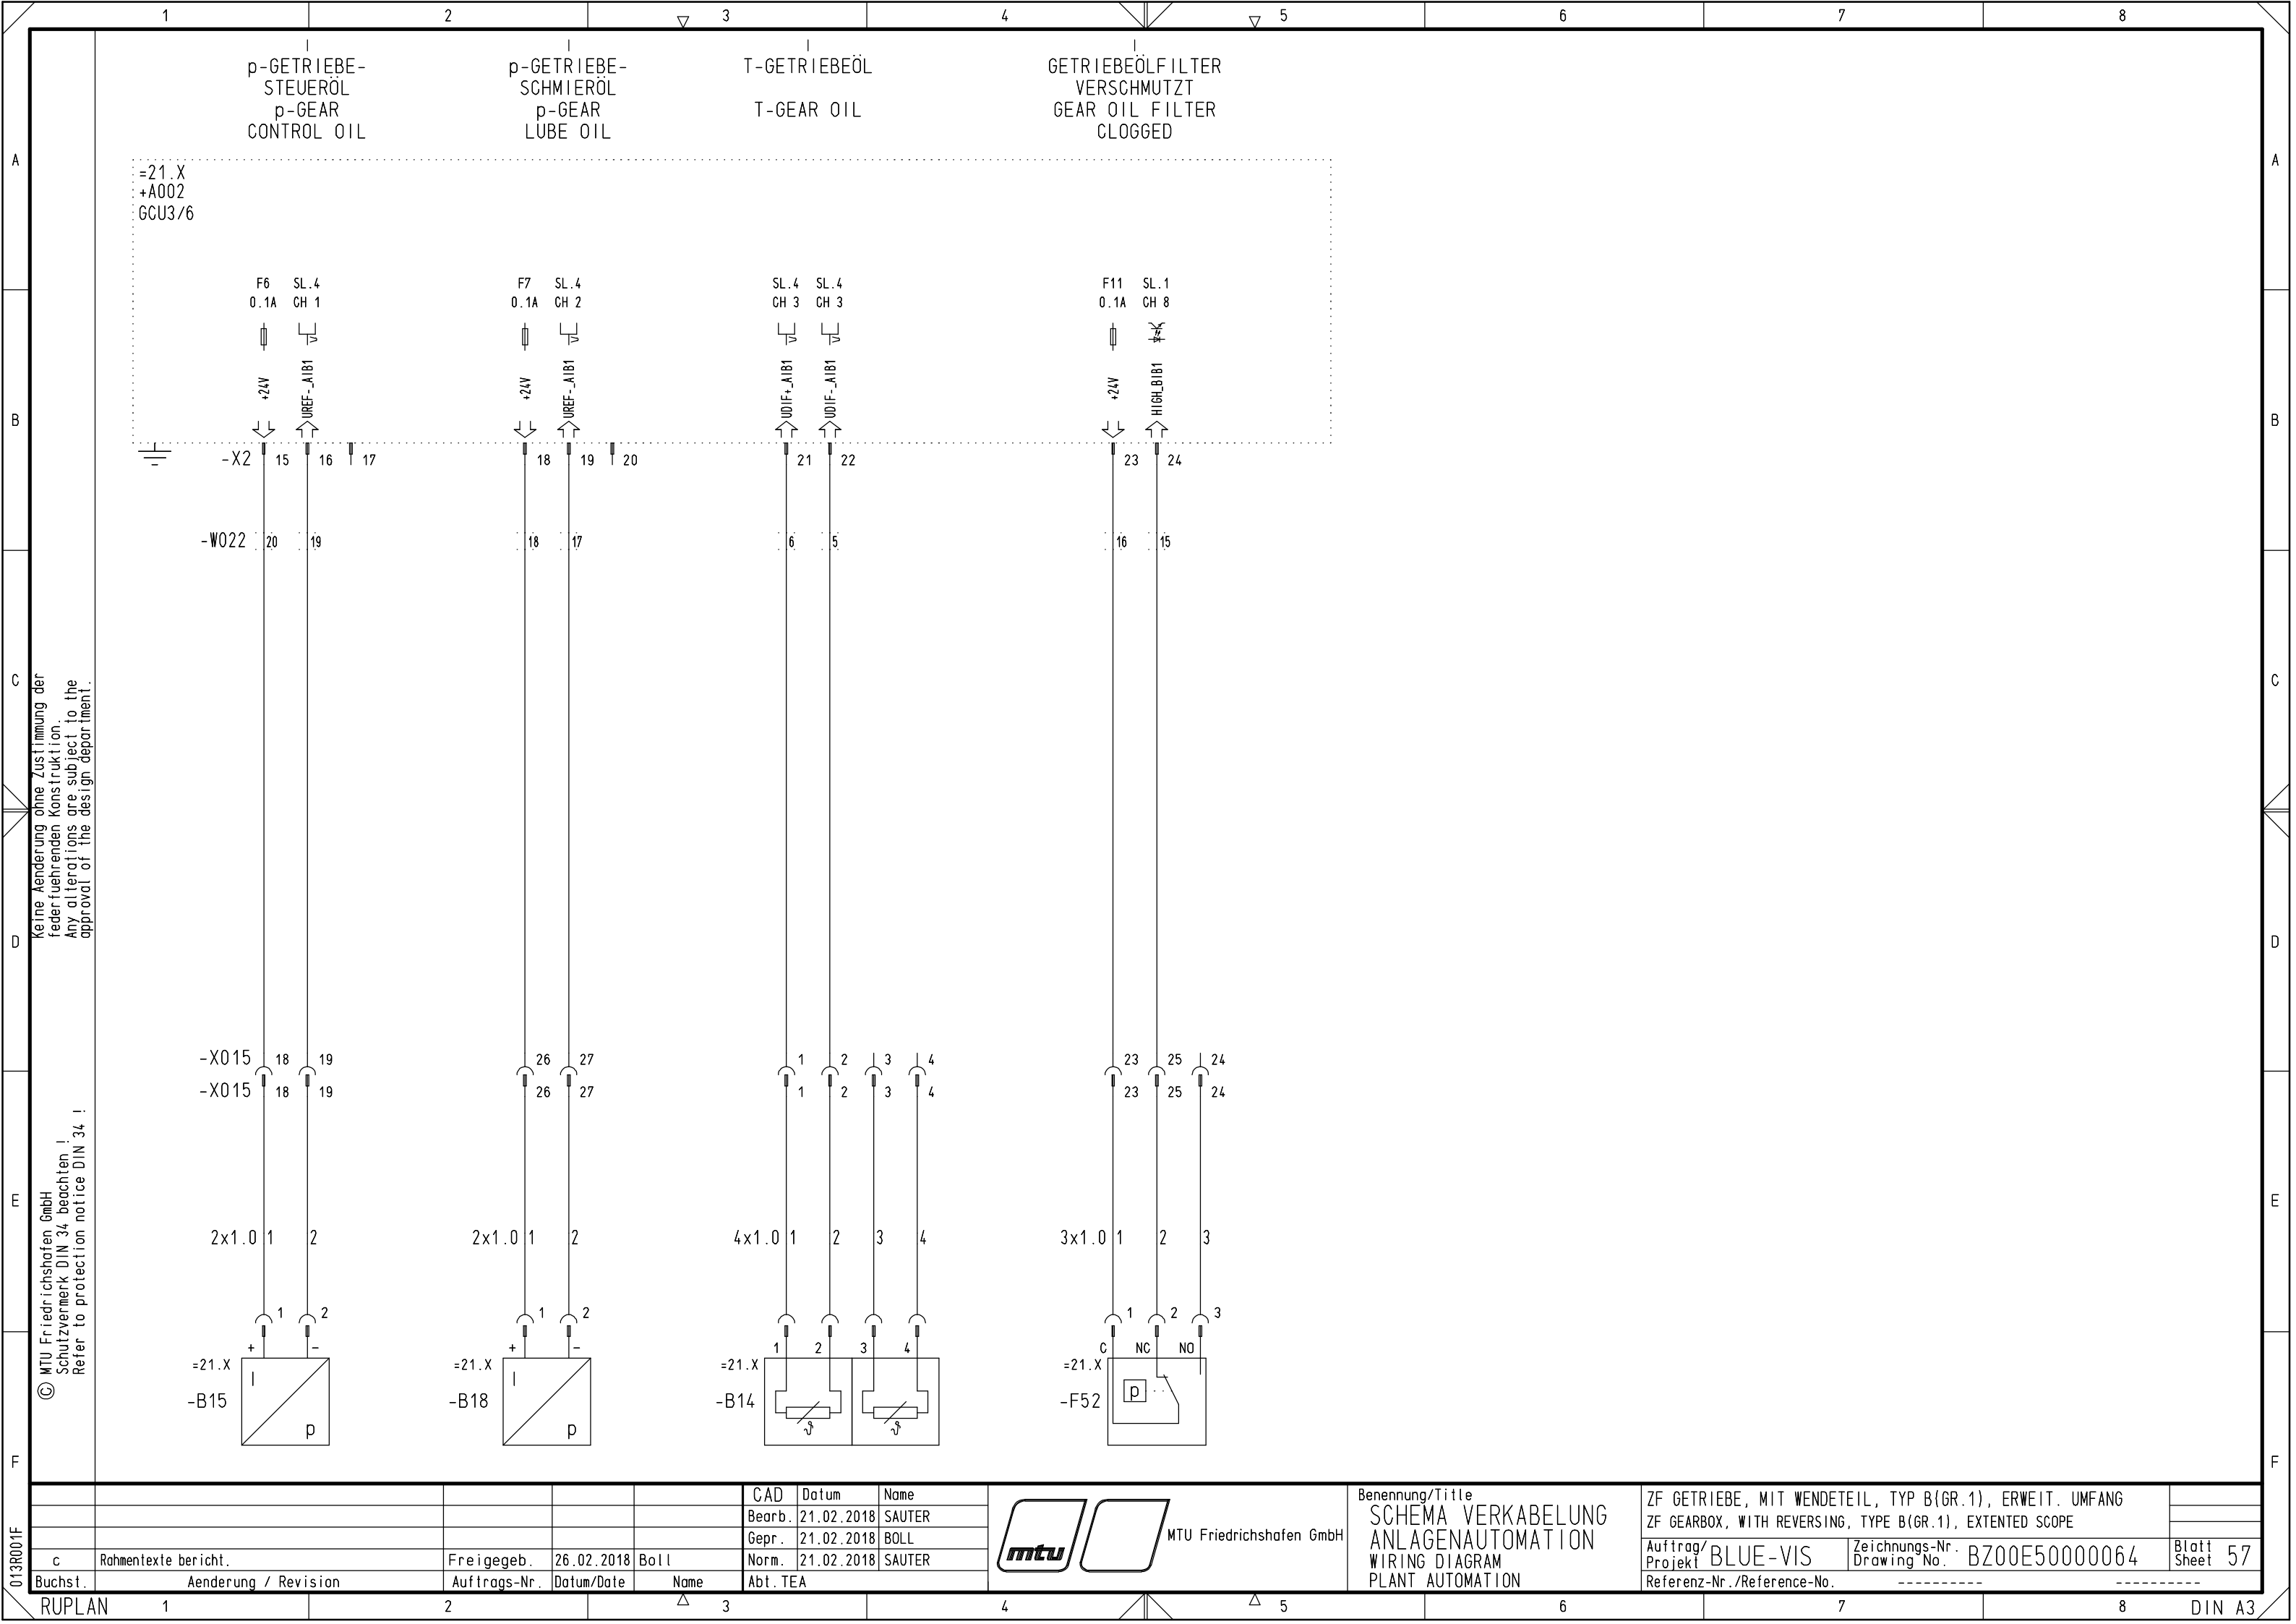

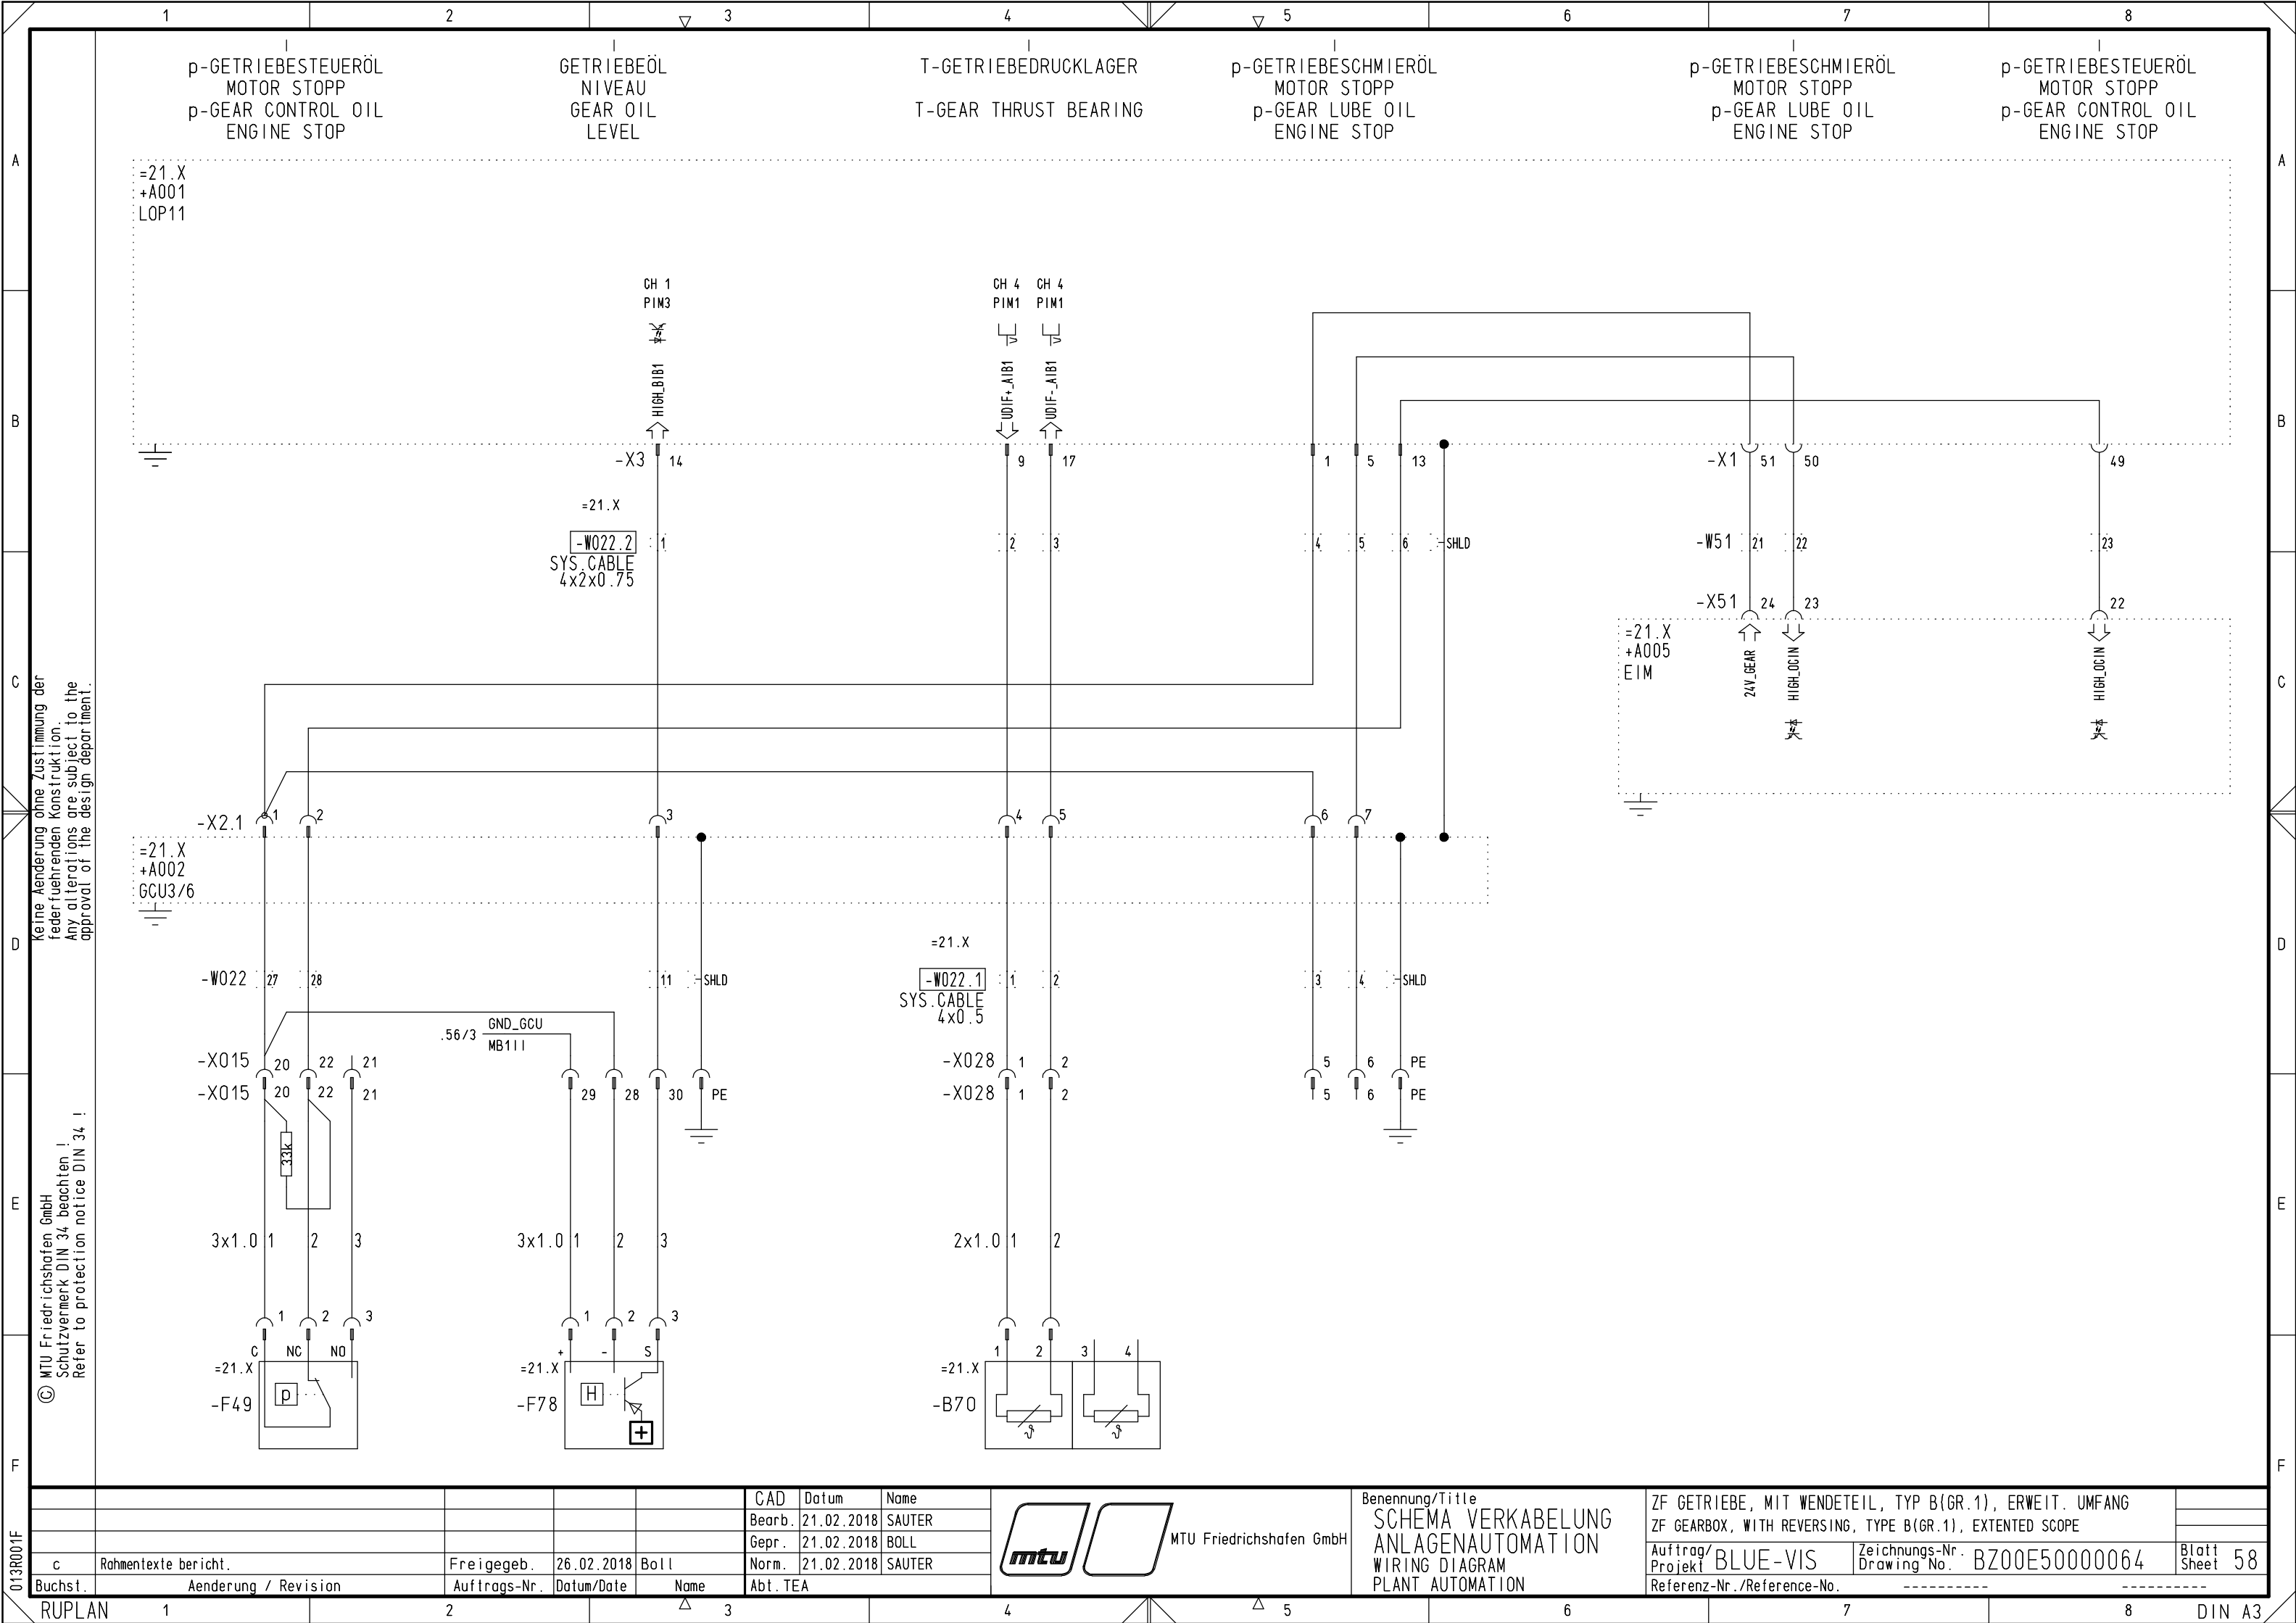

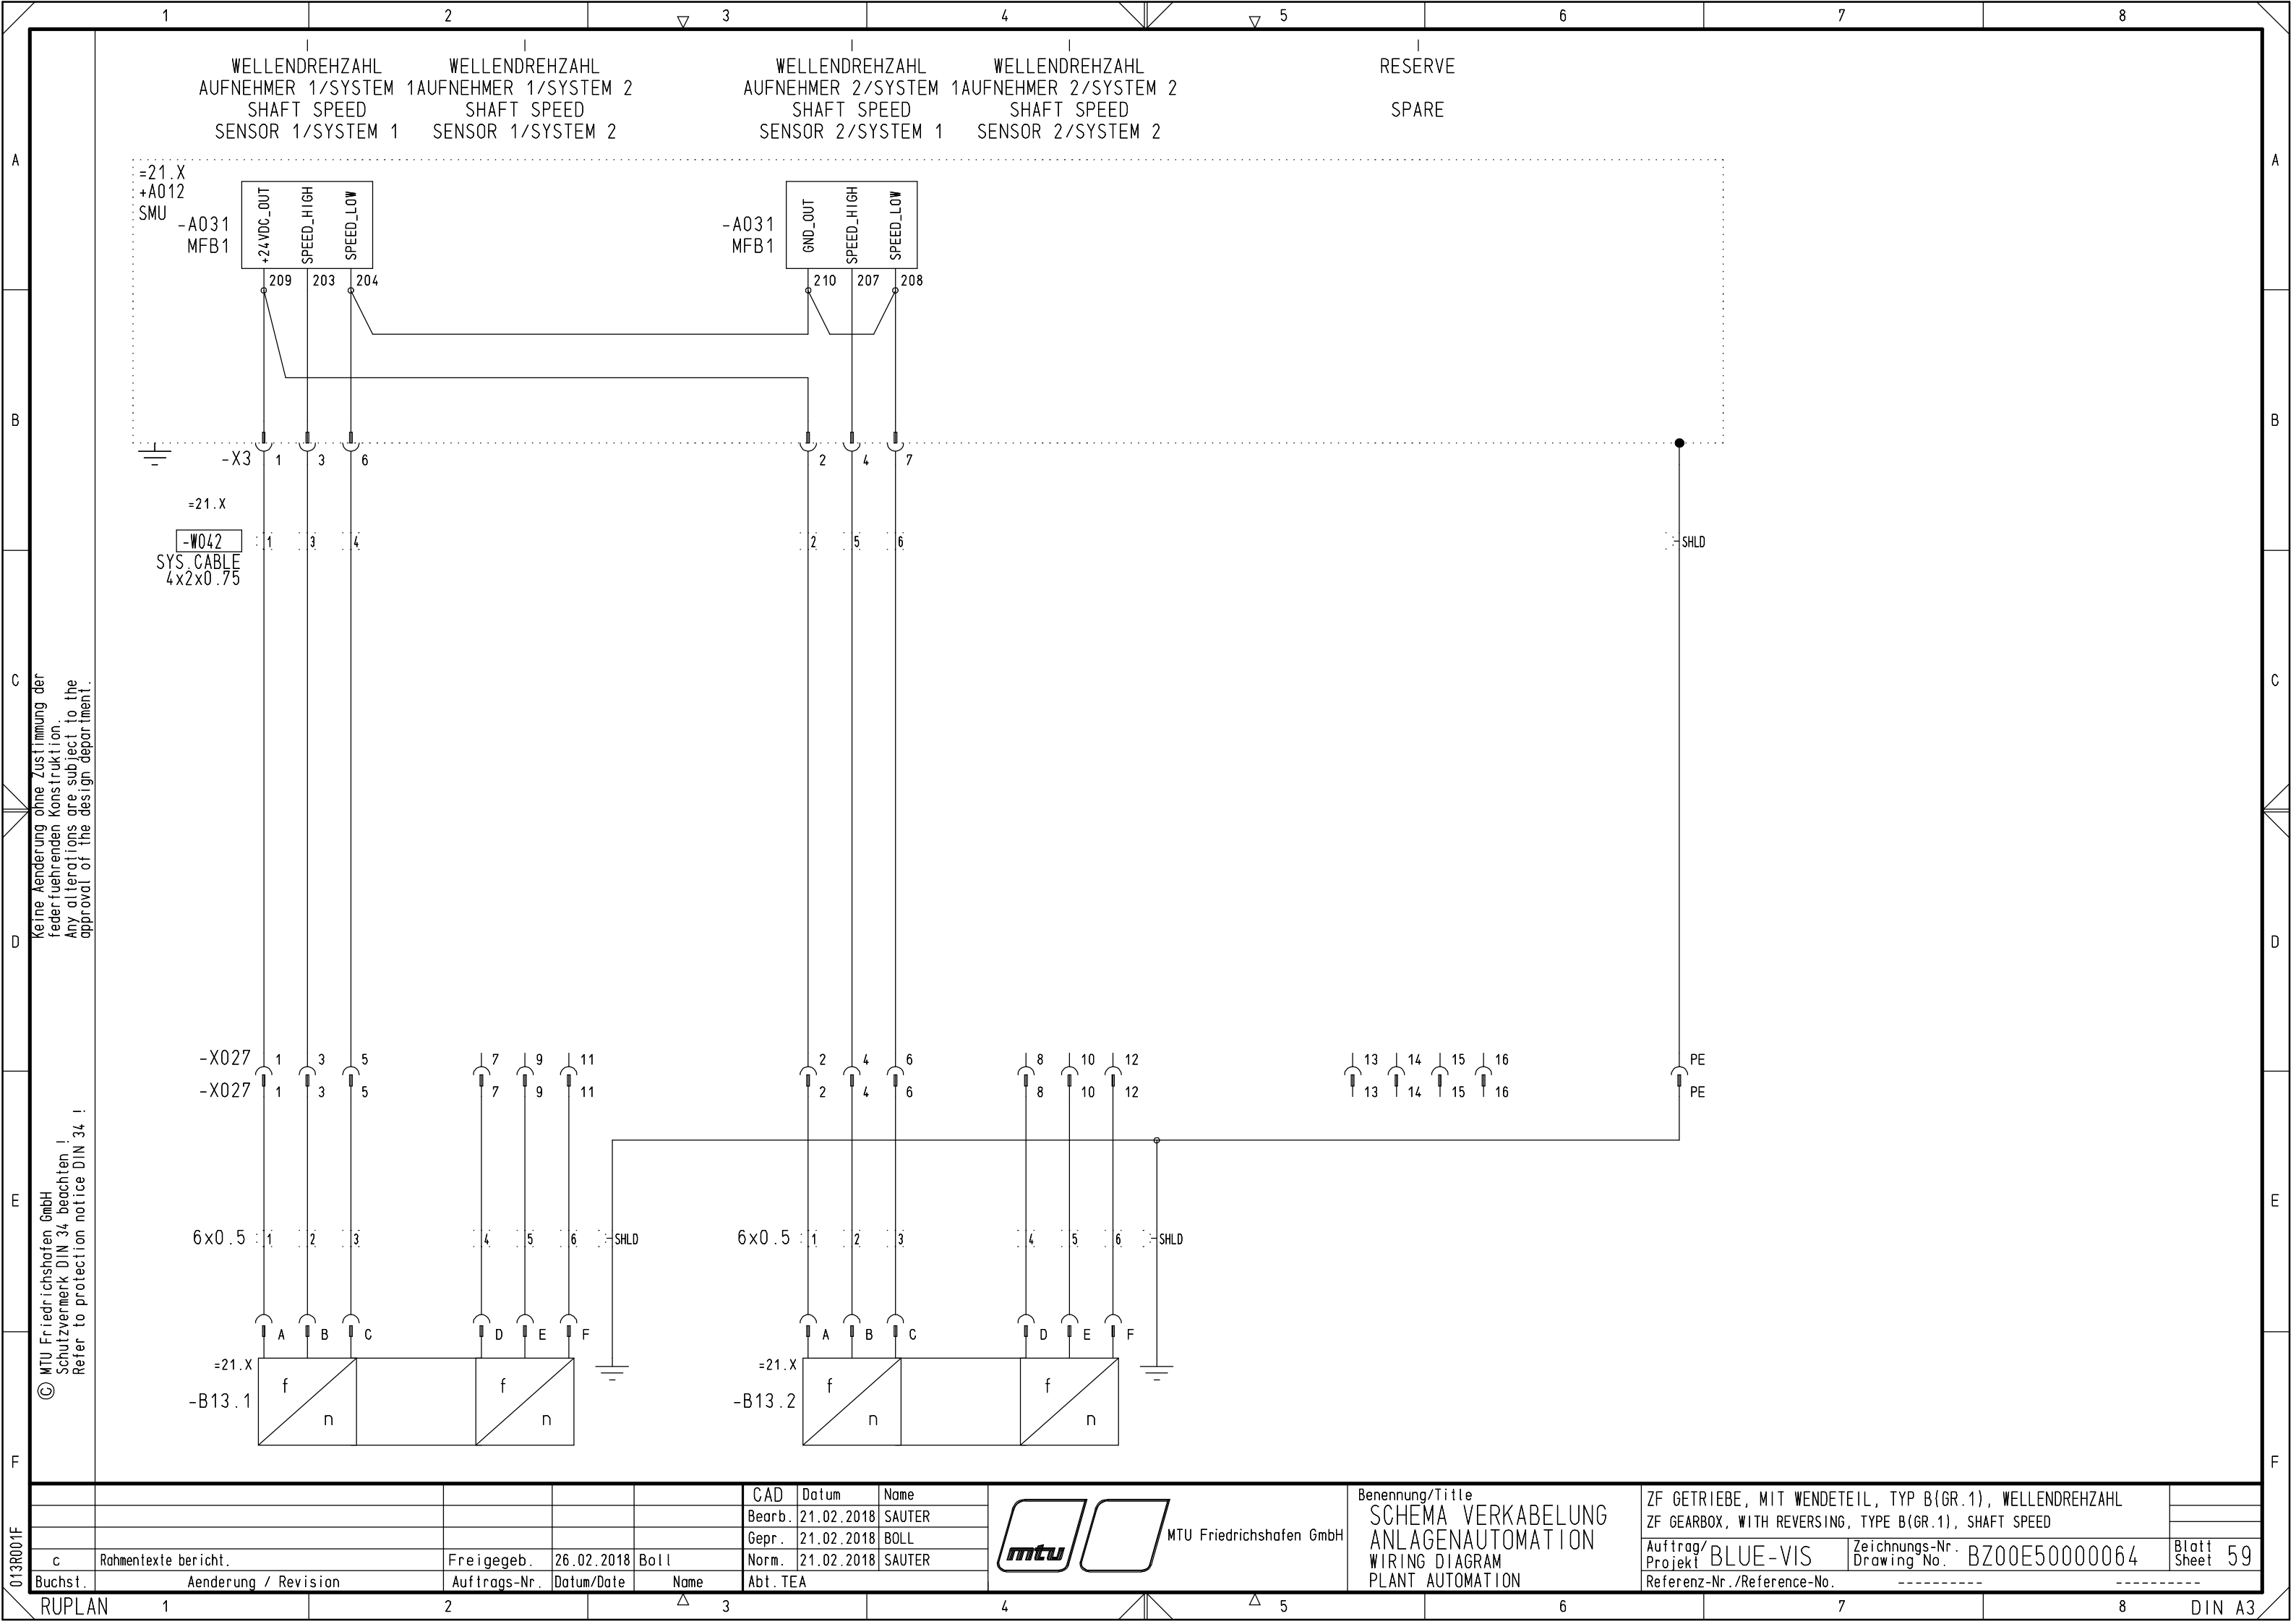


[illegible]

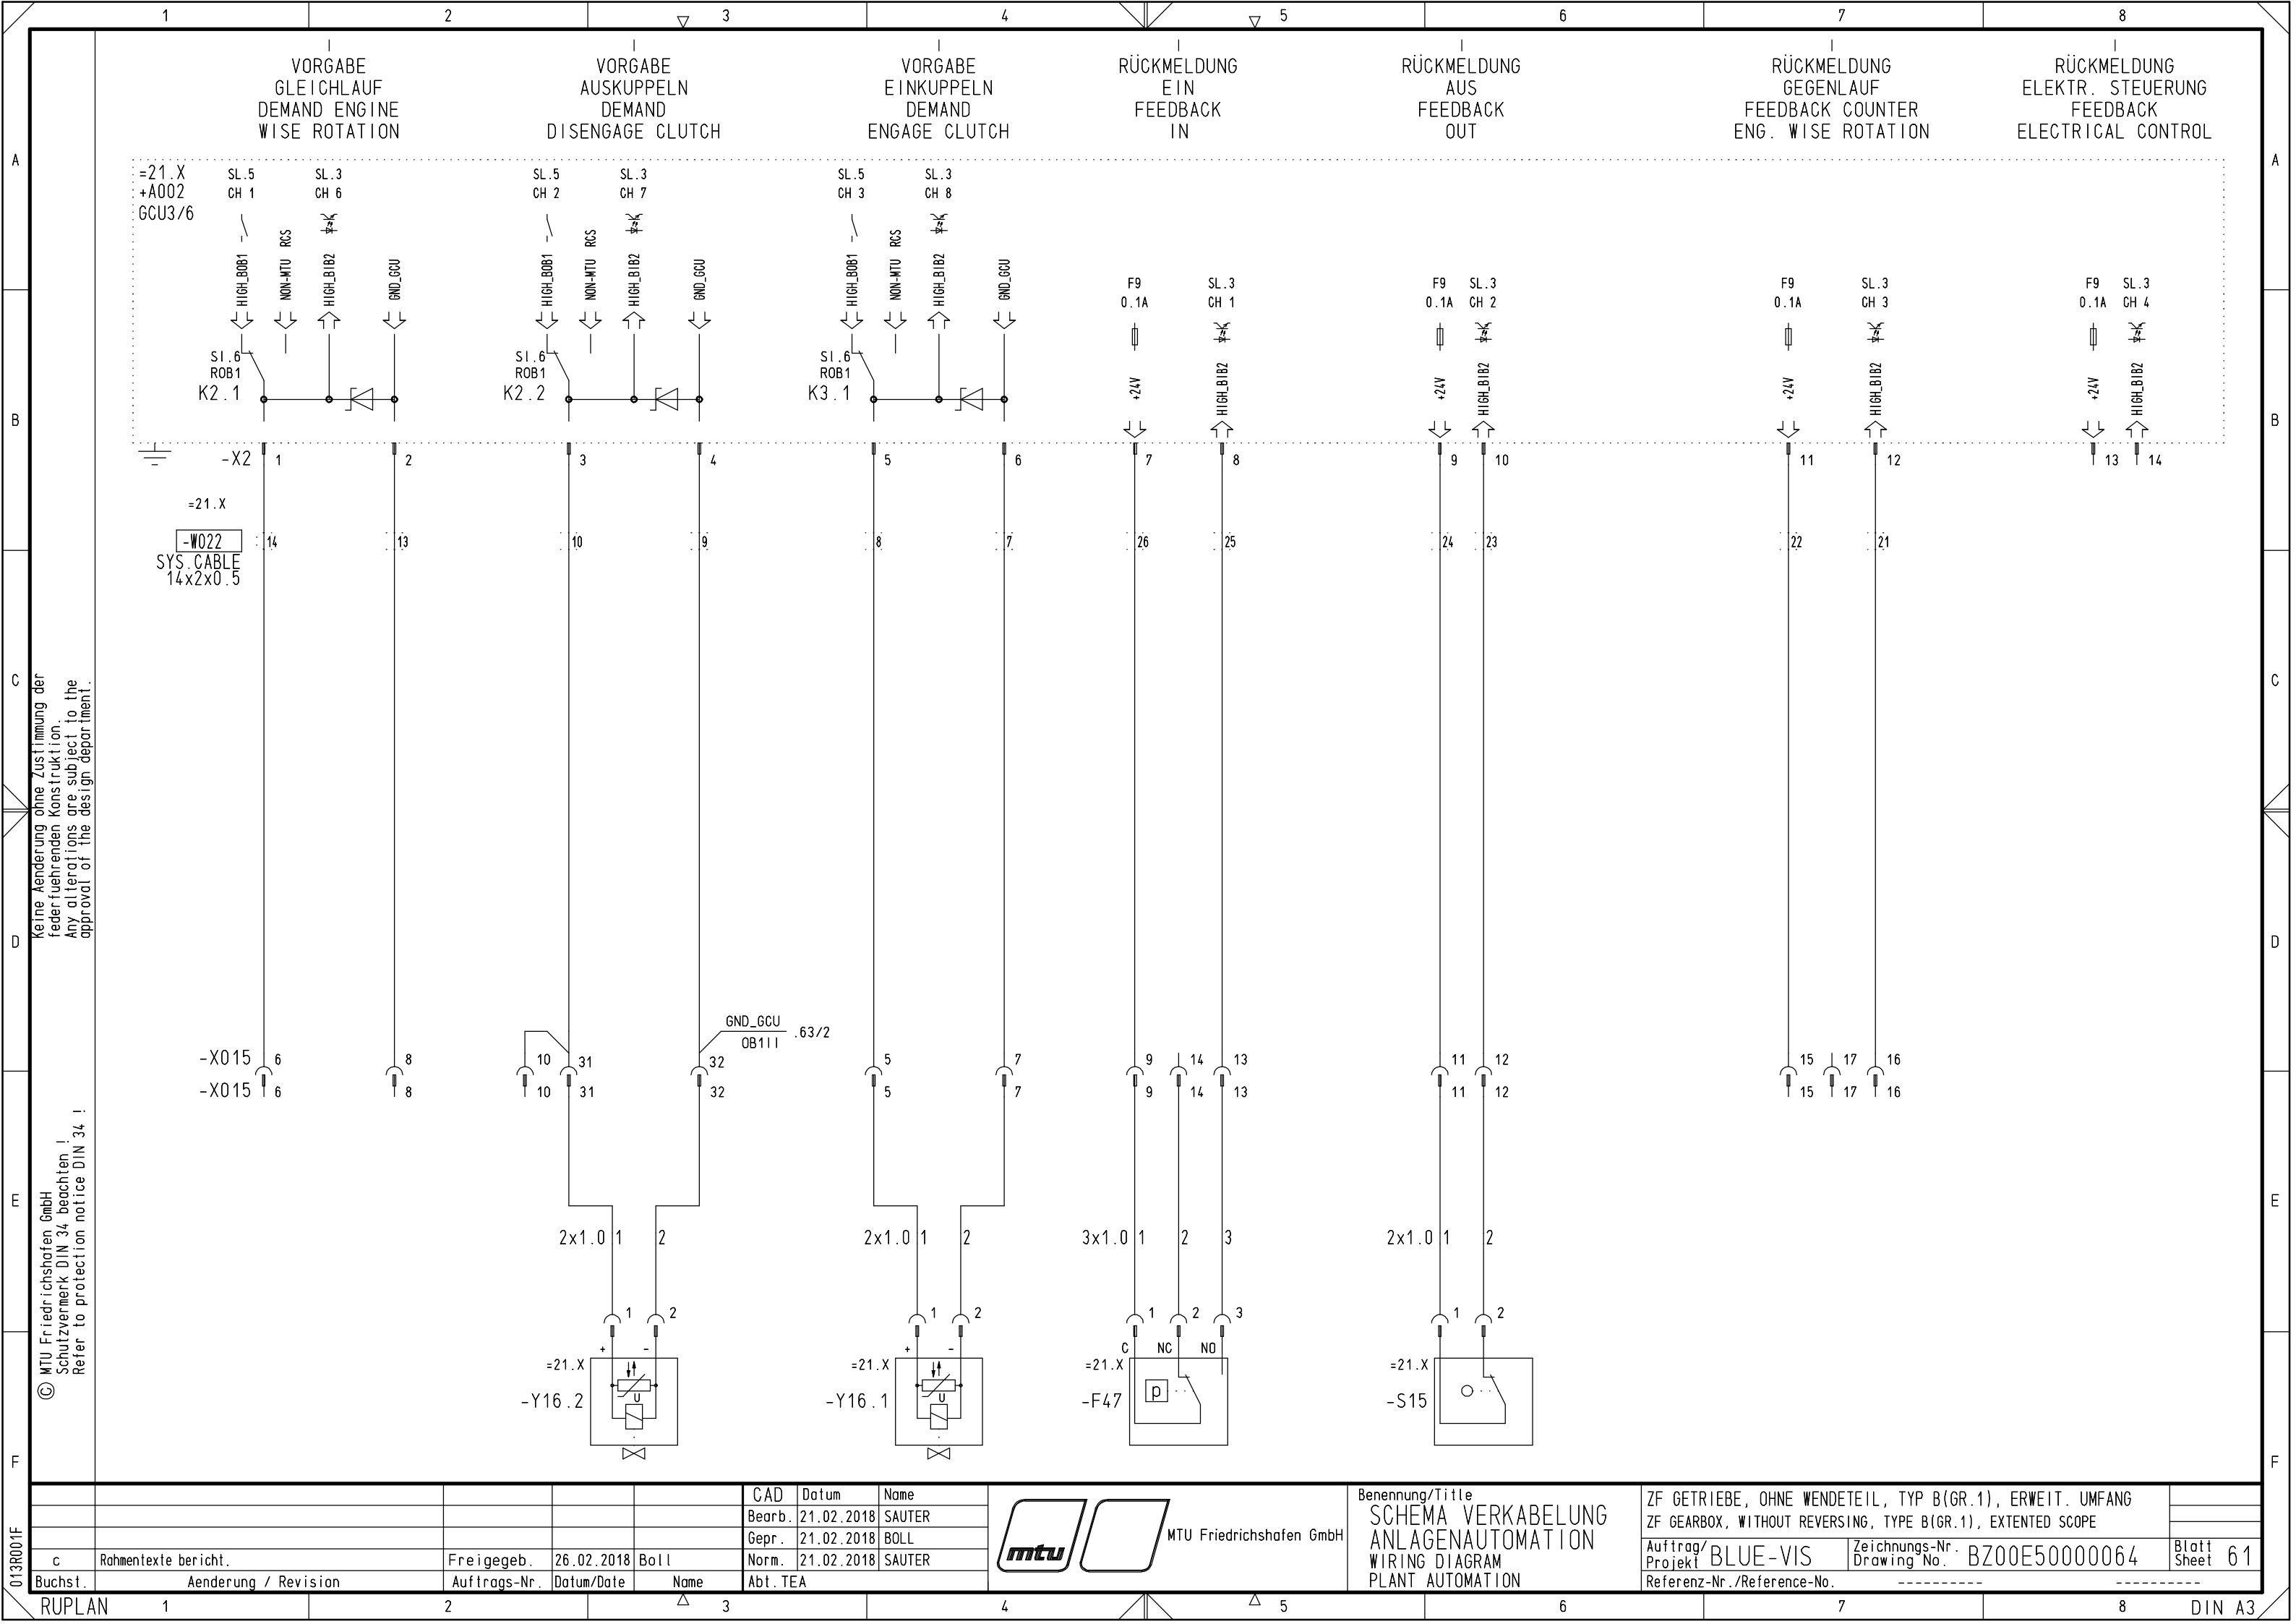

Keine Änderung ohne Zustimmung der
federführenden Konstruktion.
Any alterations are subject to the
approval of the design department.

© MTU Friedrichshafen GmbH
Schutzvermerk DIN 34 beachten !
Refer to protection notice DIN 34 !

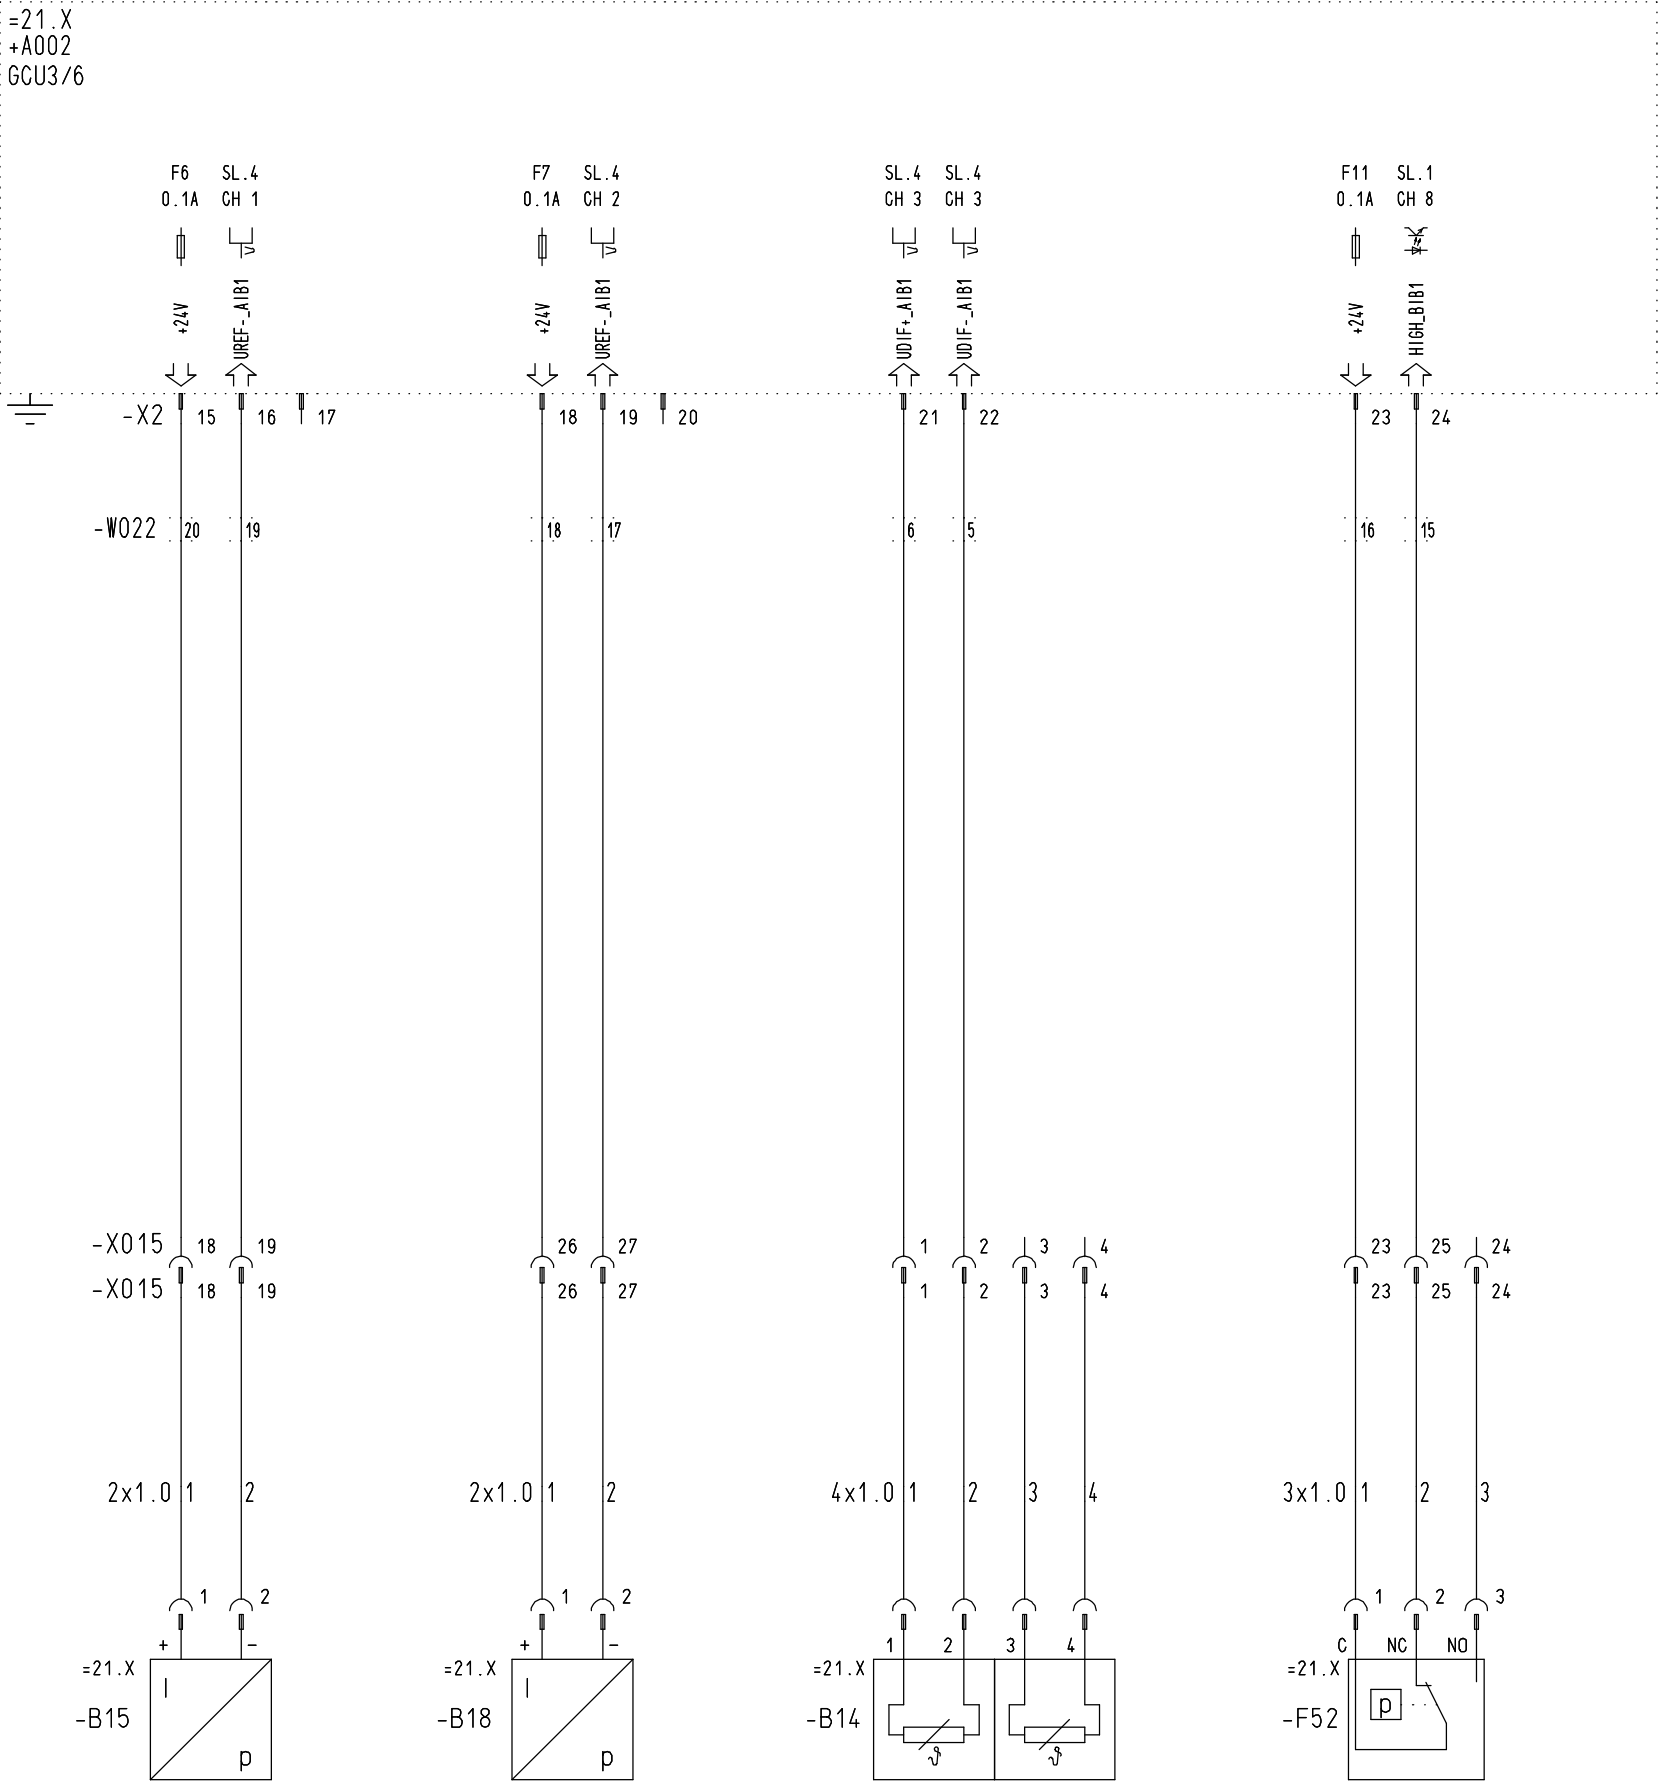


					CAD	Datum	Name
					Bearb.	21.02.2018	SAUTER
					Gepr.	21.02.2018	BOLL
					Norm.	21.02.2018	SAUTER
c	Rahmentexte bericht.	Freigegeb.	26.02.2018	Boll	Abt. TEA		
Buchst.	Aenderung / Revision	Auftrags-Nr.	Datum/Date	Name			




MTU Friedrichshafen GmbH

Benennung/Title
SCHEMA VERKABELUNG
ANLAGENAUTOMATION
WIRING DIAGRAM
PLANT AUTOMATION

ZF GETRIEBE, OHNE WENDETEIL, TYP B(GR.1), ERWEIT. UMFANG ZF GEARBOX, WITHOUT REVERSING, TYPE B(GR.1), EXTENDED SCOPE		
Auftrag/ Projekt	BLUE-VIS	Zeichnungs-Nr. Drawing No. BZ00E50000064
Referenz-Nr./Reference-No.		Blatt Sheet 62

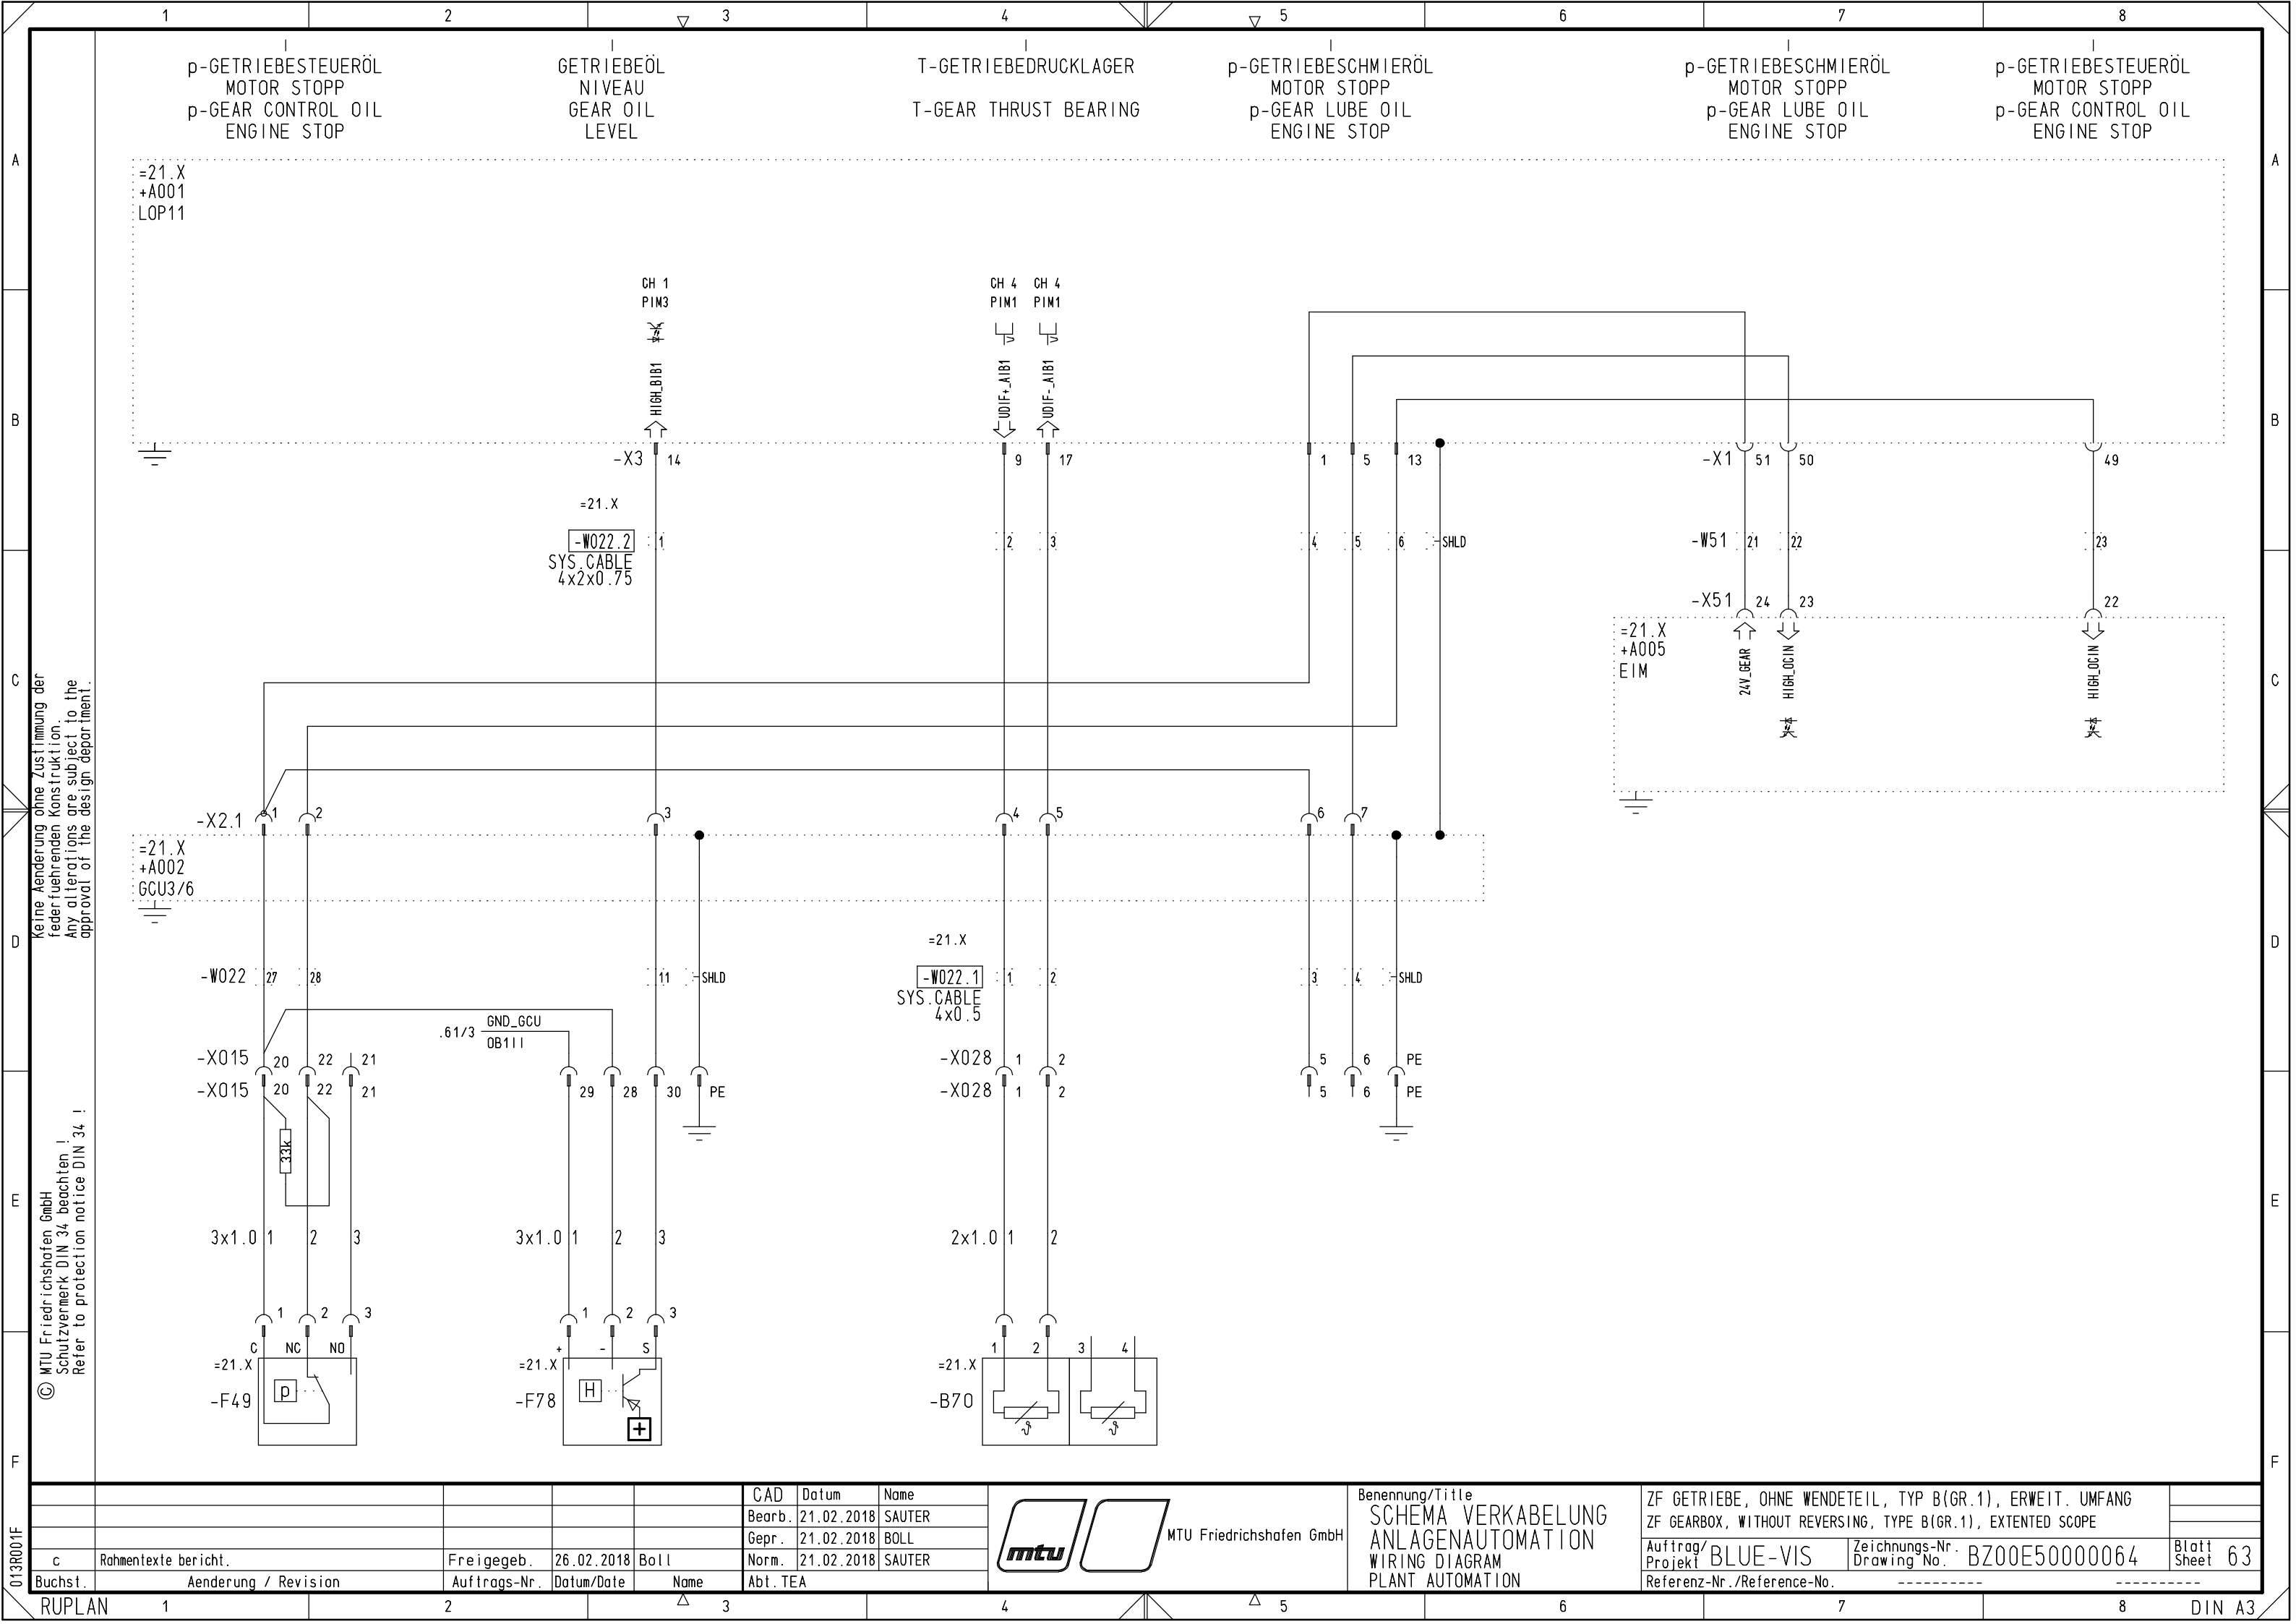

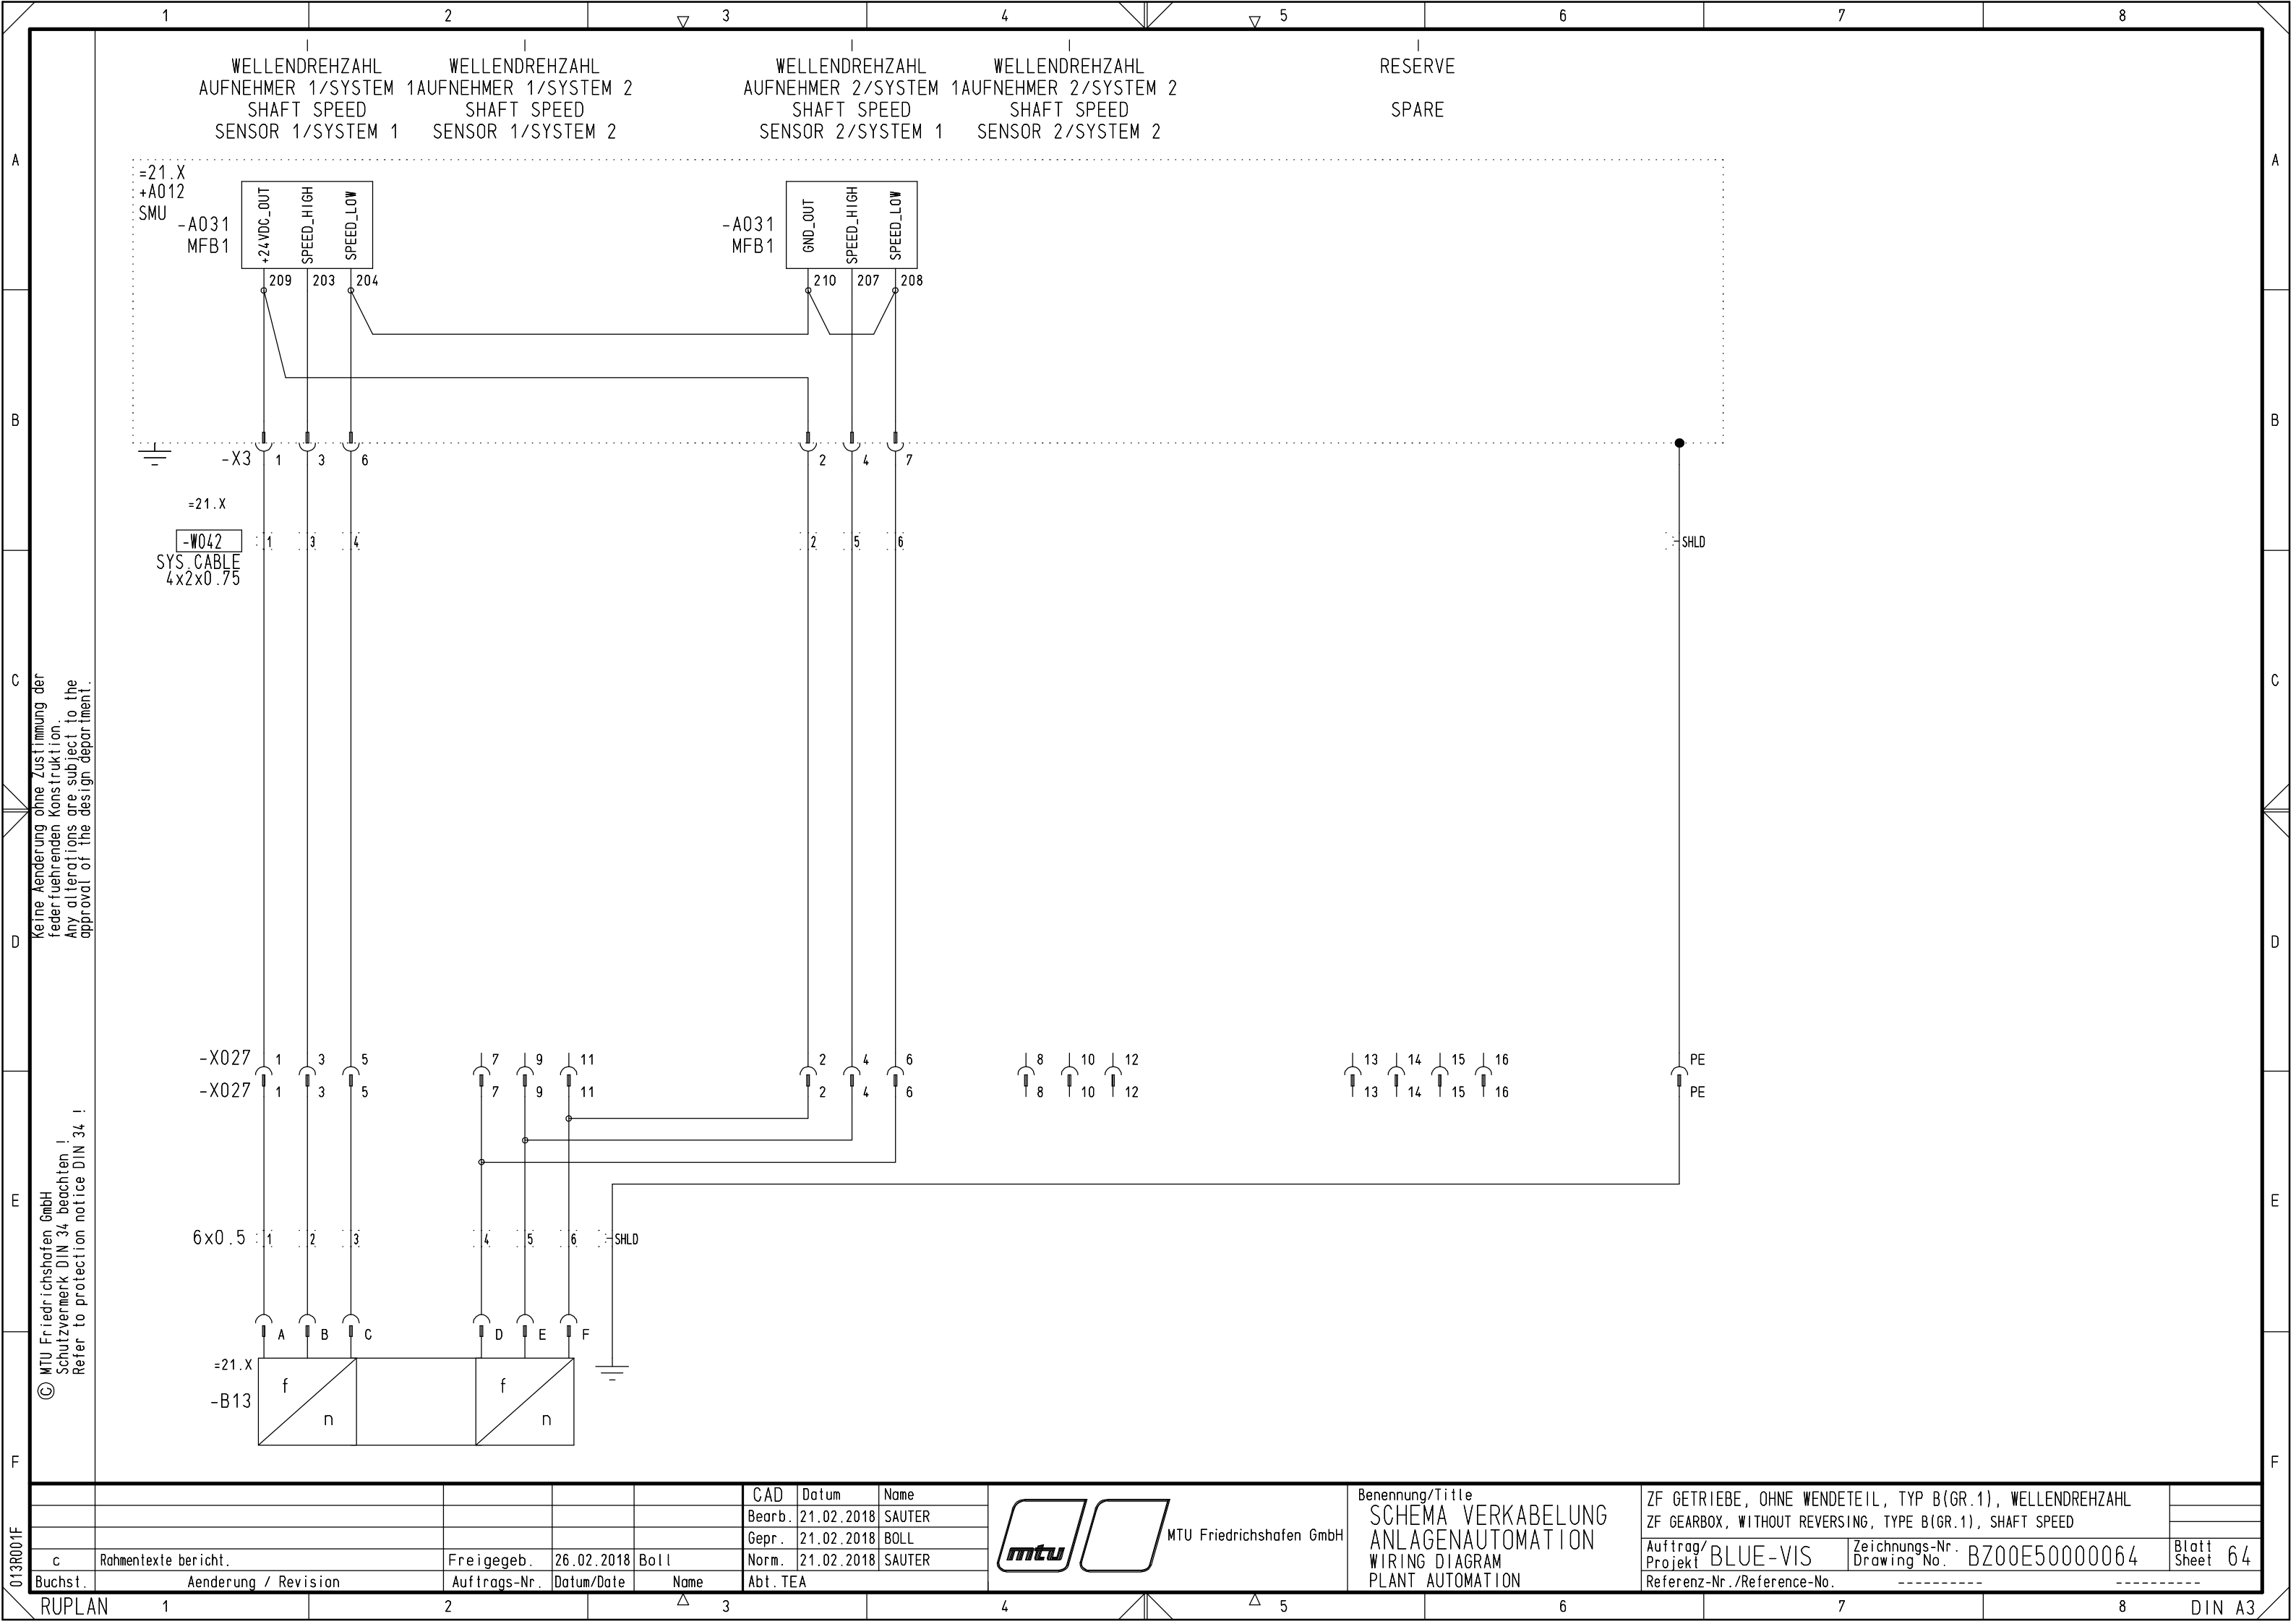

[illegible]

Keine Änderung ohne Zustimmung der
federführenden Konstruktion.
Any alterations are subject to the
approval of the design department.

© MTU Friedrichshafen GmbH
Schutzvermerk DIN 34 beachten !
Refer to protection notice DIN 34 !


					CAD	Datum	Name
					Bearb.	21.02.2018	SAUTER
					Gedr.	21.02.2018	BOLL
					Norm.	21.02.2018	SAUTER
c	Rahmentexte bericht.	Freigegeb.	26.02.2018	Boll	Abt. TEA		
Buchst.	Änderung / Revision	Auftrags-Nr.	Datum/Date	Name			





MTU Friedrichshafen GmbH

Benennung/Title
SCHEMA VERKABELUNG
ANLAGENAUTOMATION
WIRING DIAGRAM
PLANT AUTOMATION


ZF GETRIEBE, MIT WENDETEIL, TYP B(GR.2), ERWEIT. UMFANG ZF GEARBOX, WITH REVERSING, TYPE B(GR.2), EXTENDED SCOPE			
Auftrag/ Projekt	BLUE-VIS	Zeichnungs-Nr. Drawing No.	BZ00E50000064
Referenz-Nr./Reference-No.		-----	
Blatt Sheet			66

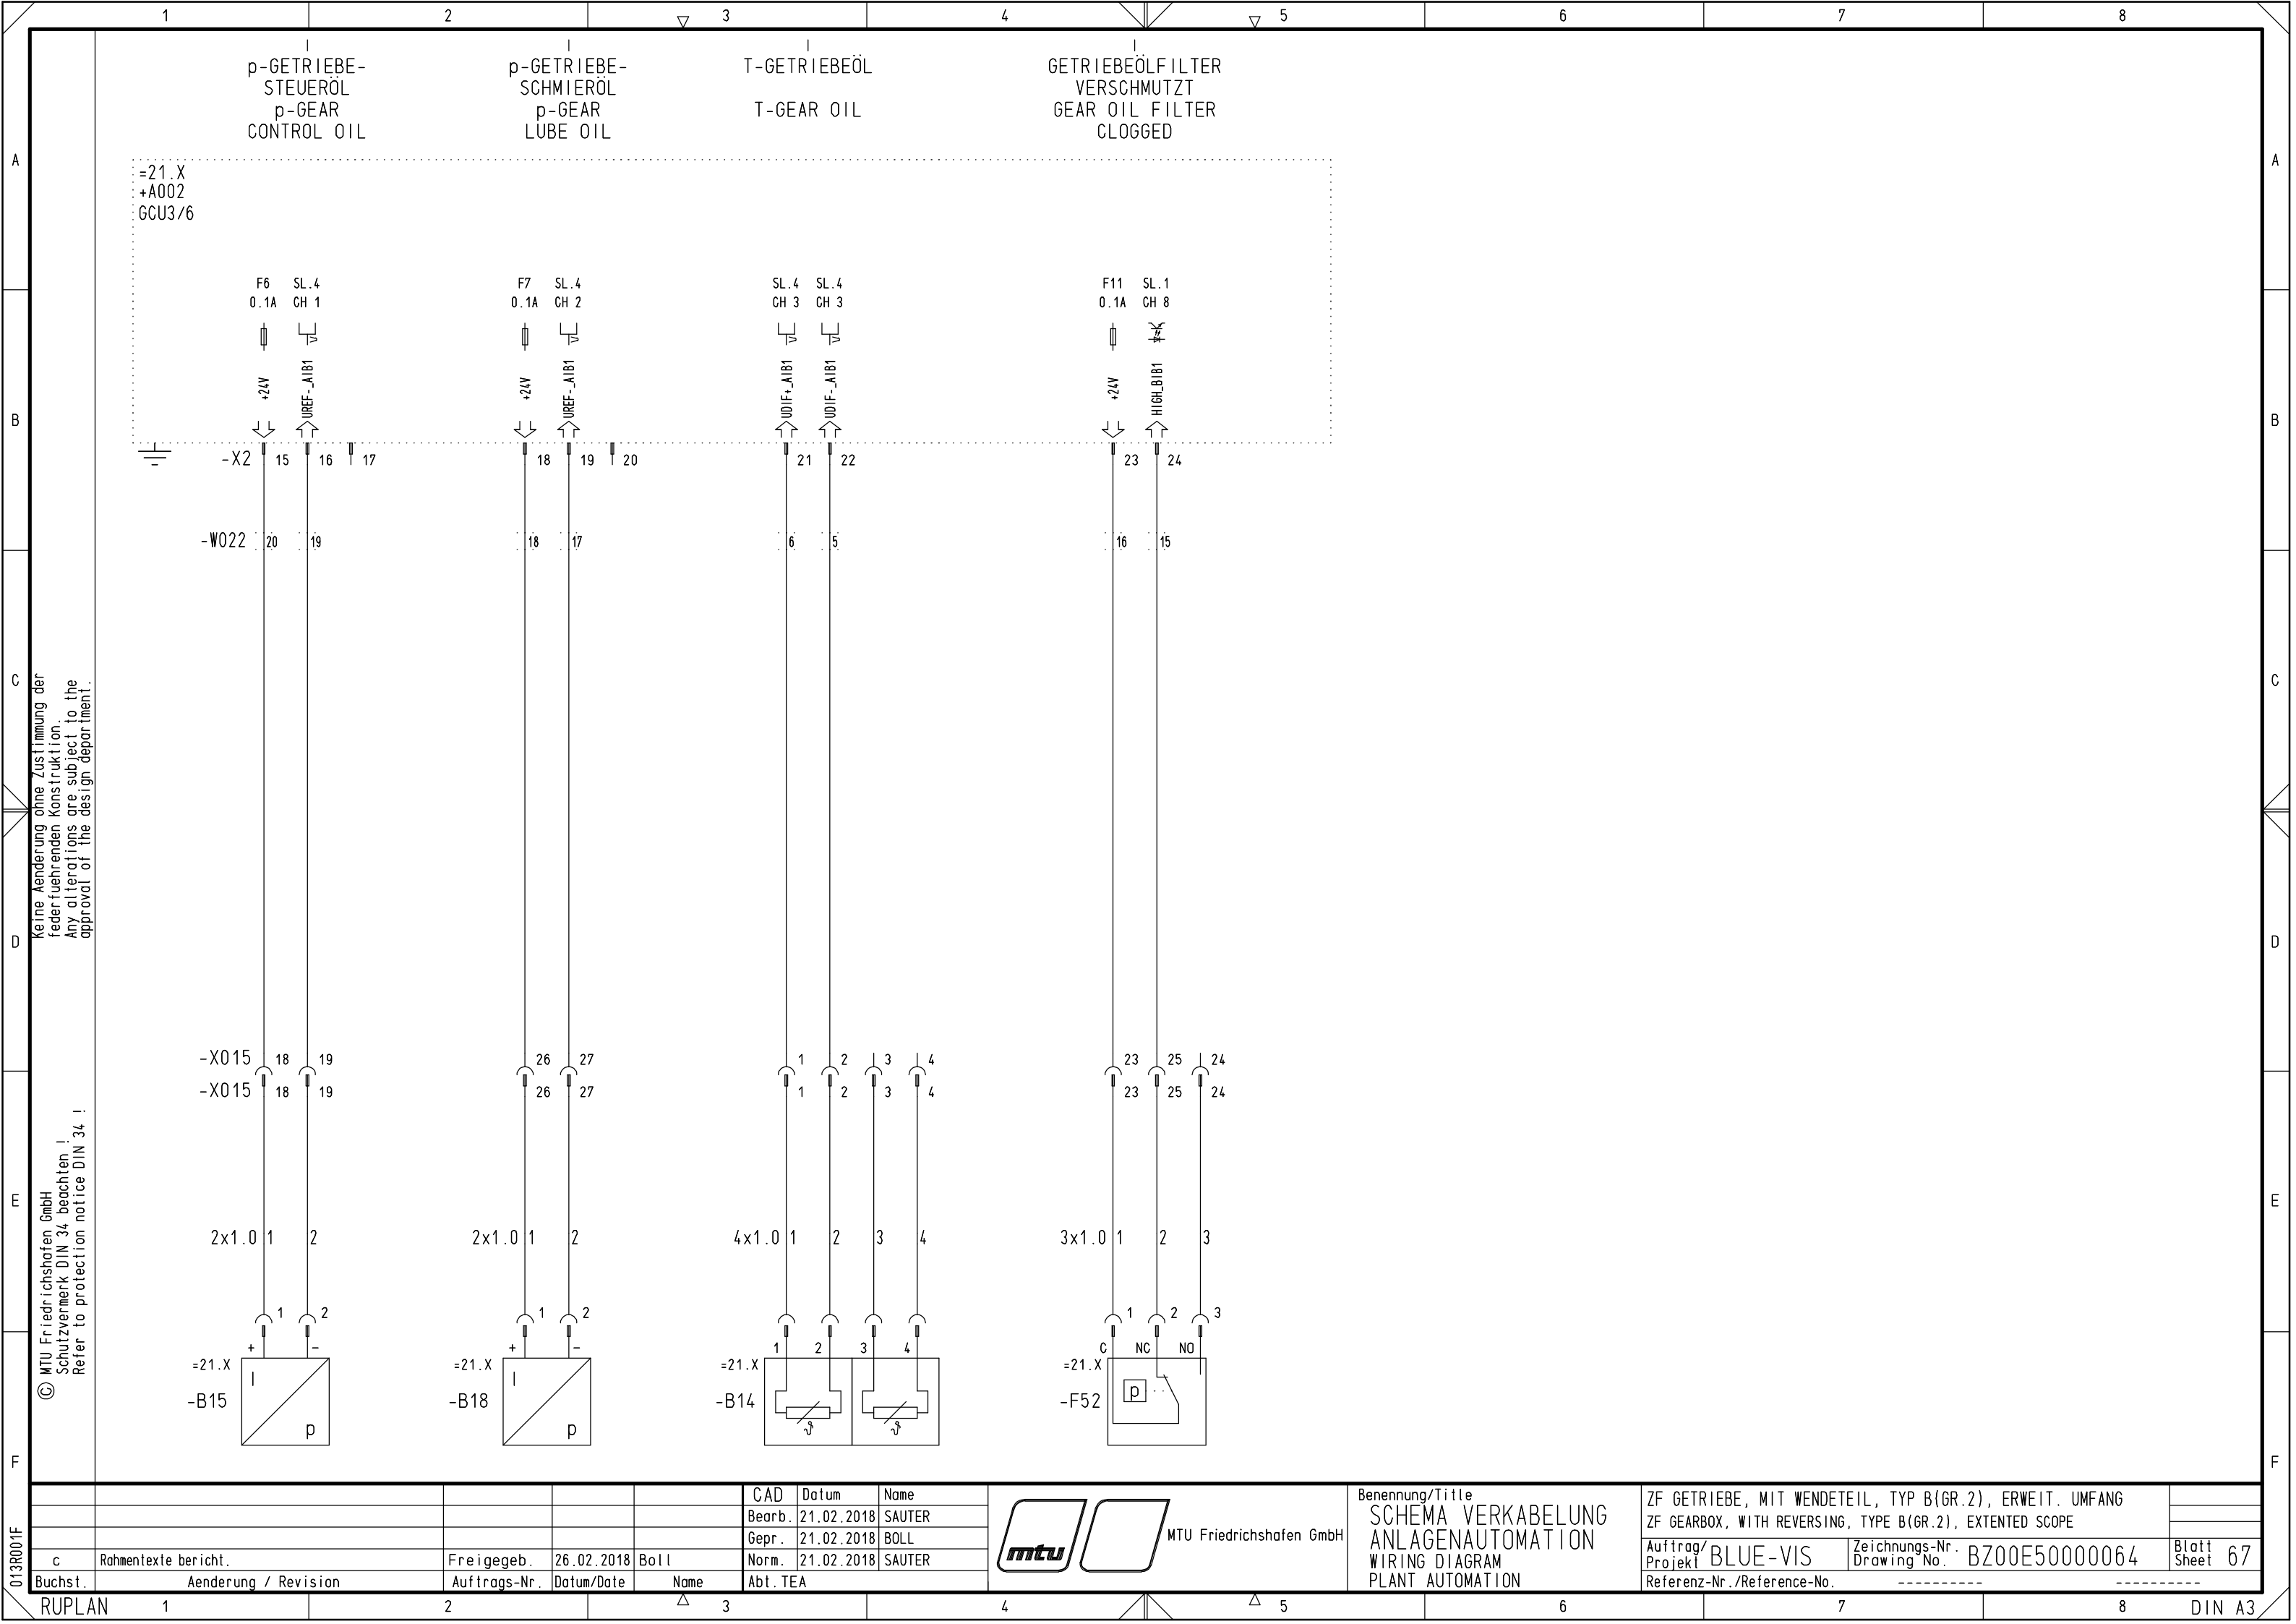

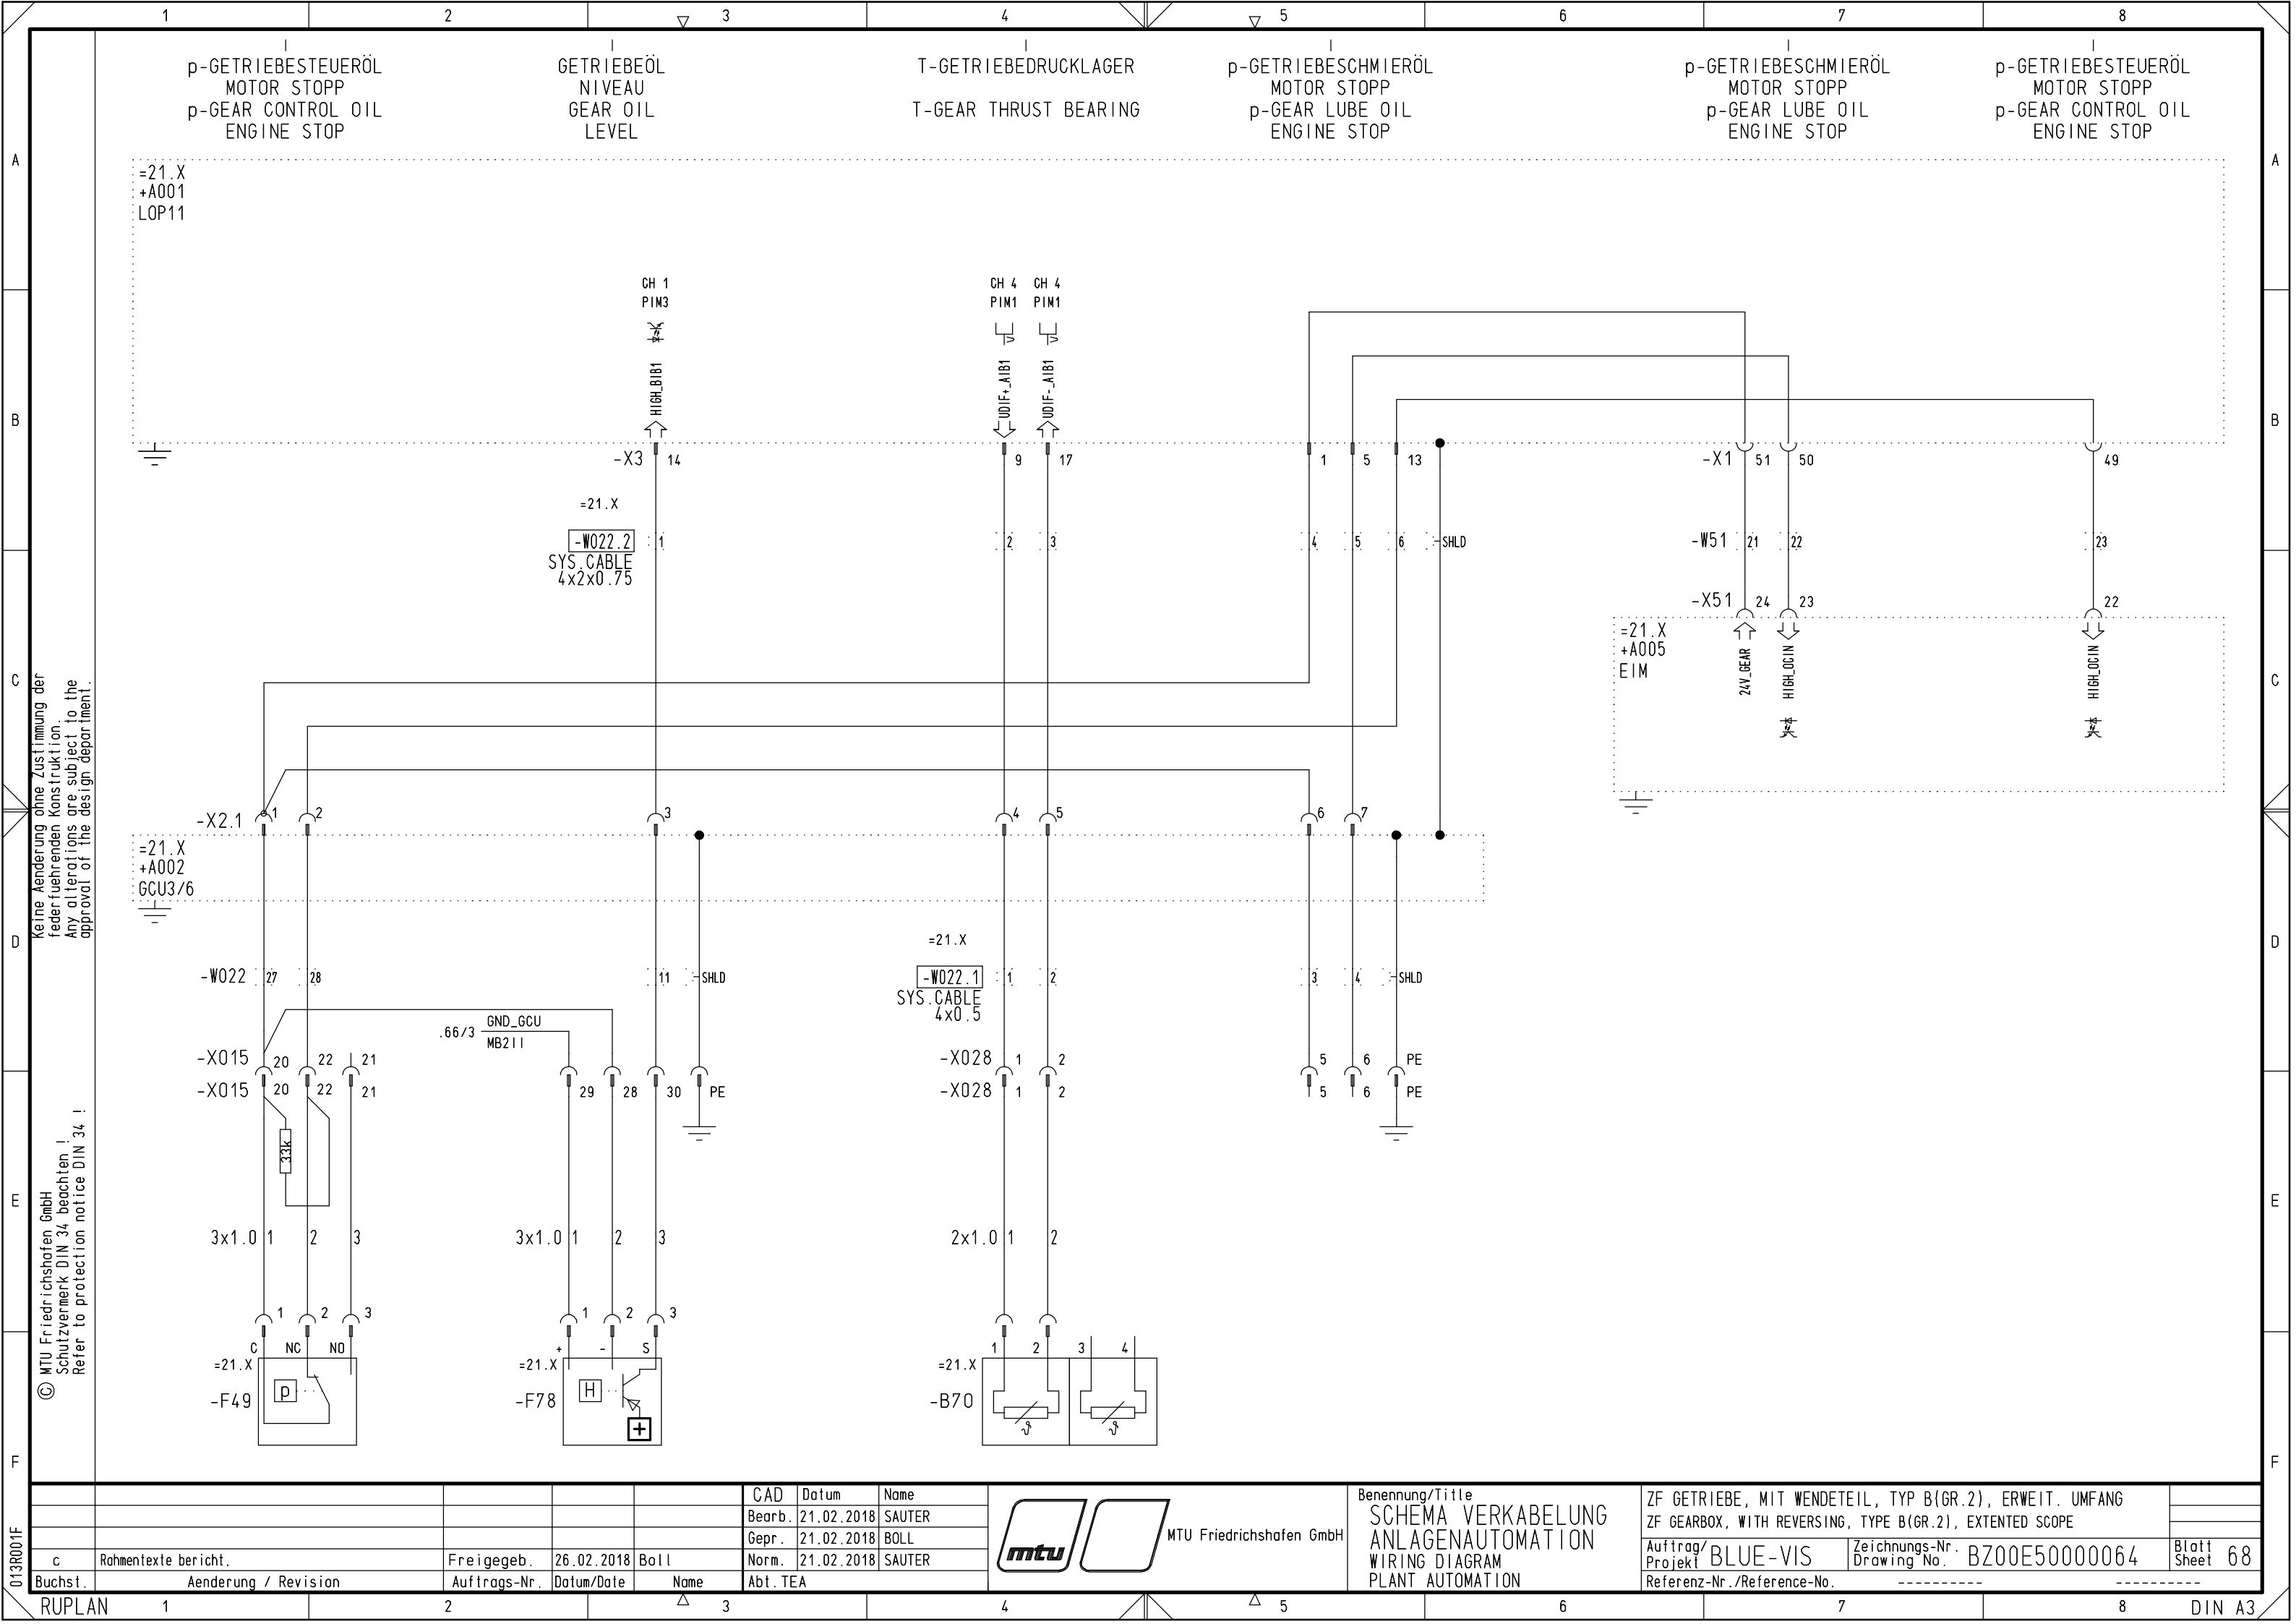

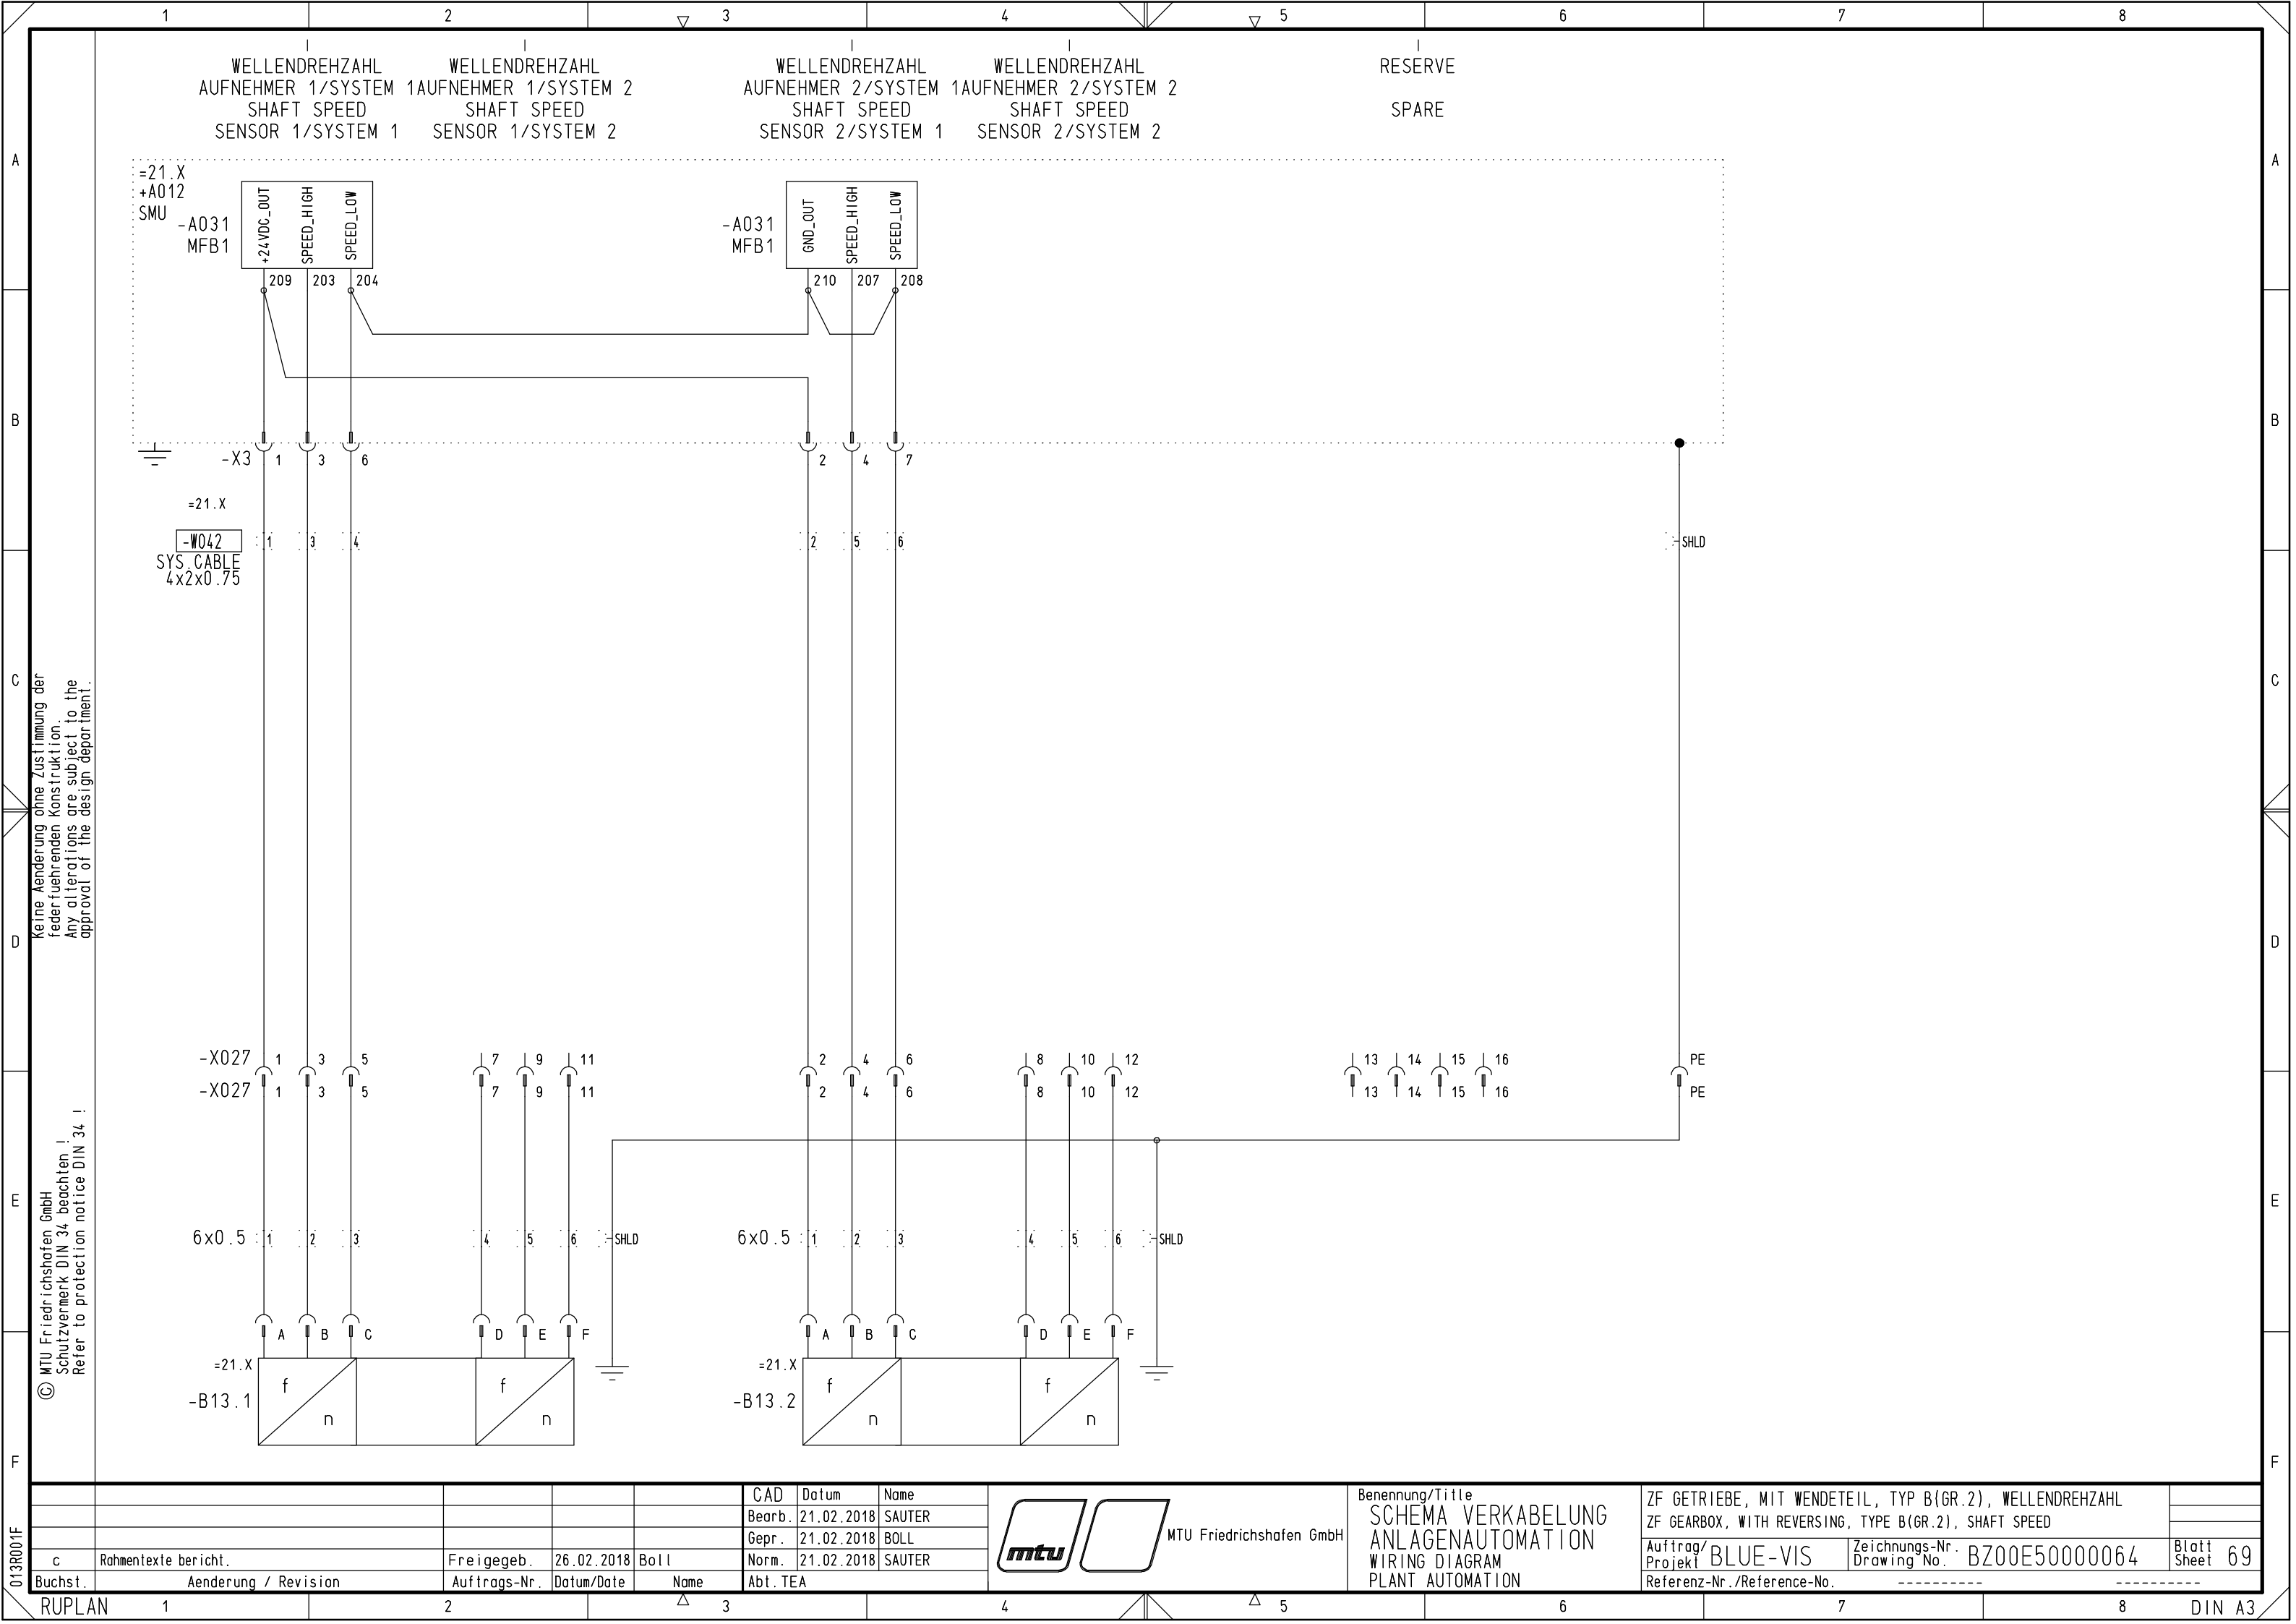

[illegible]

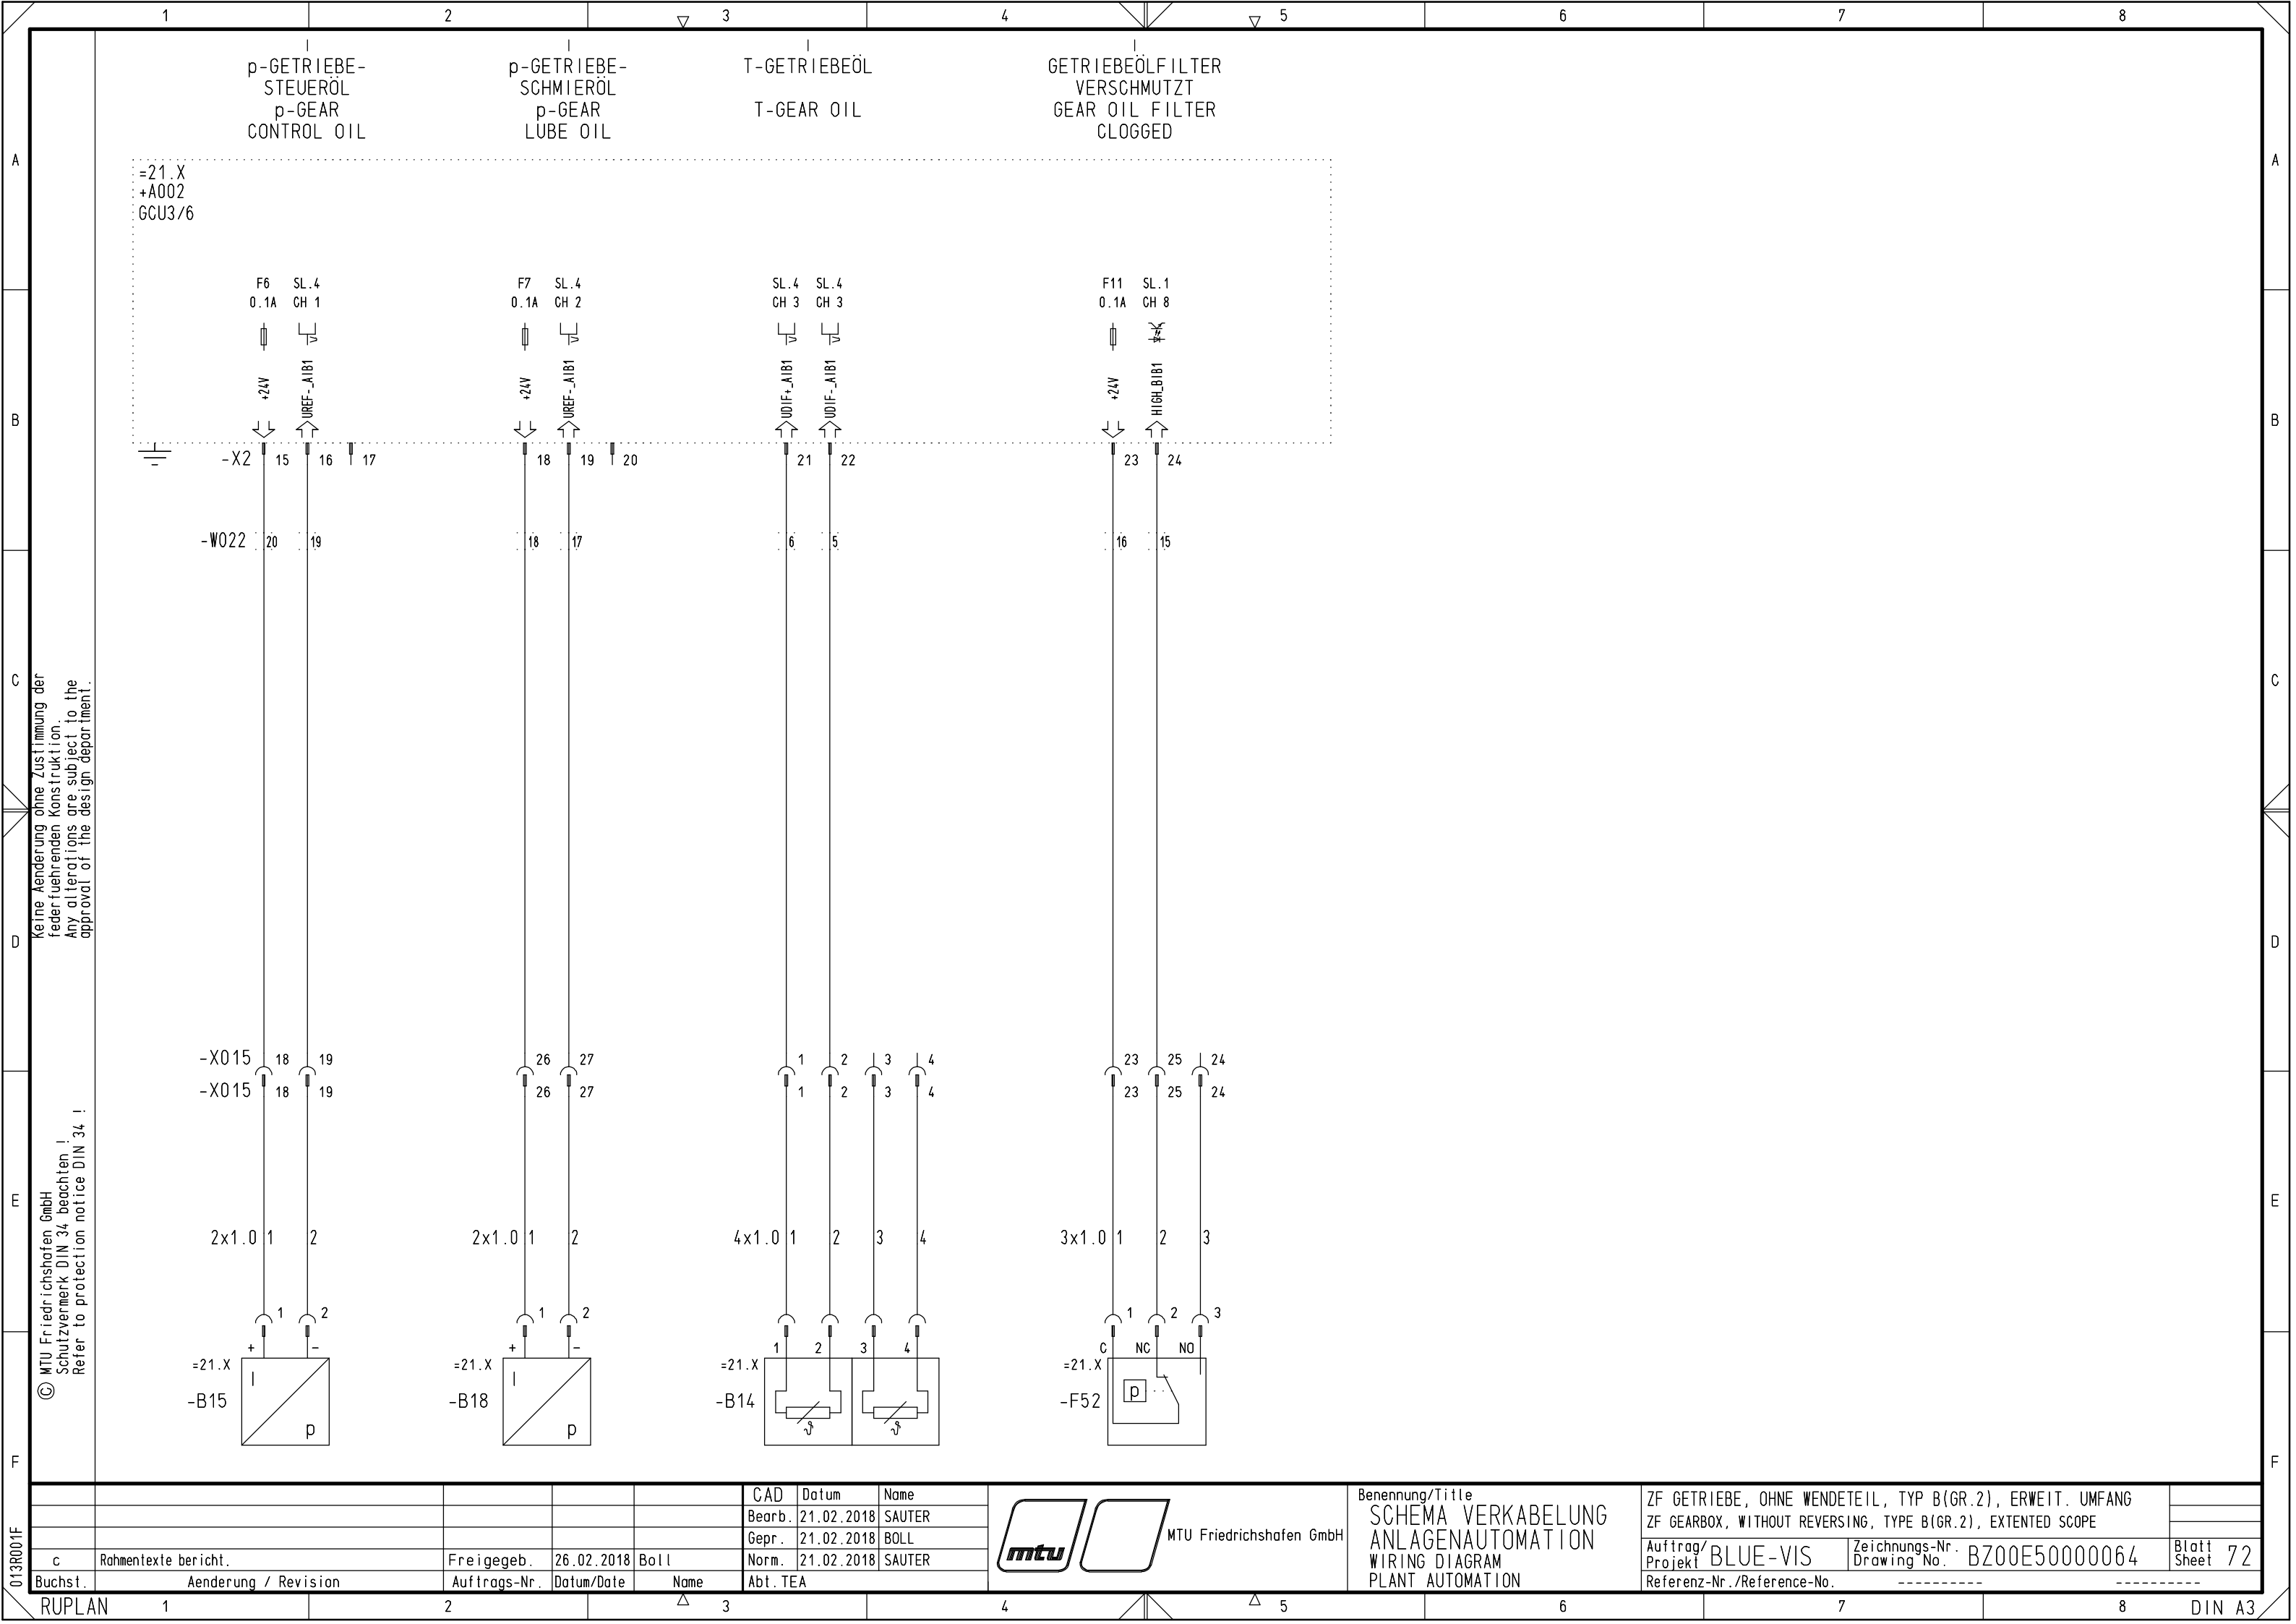


					CAD	Datum	Name
					Bearb.	21.02.2018	SAUTER
					Gepr.	21.02.2018	BOLL
c	Rahmentexte bericht.	Freigegeb.	26.02.2018	Boll	Norm.	21.02.2018	SAUTER
Buchst.	Aenderung / Revision	Auftrags-Nr.	Datum/Date	Name	Abt. TEA		



MTU Friedrichshafen GmbH

Benennung/Title
SCHEMA VERKABELUNG
ANLAGENAUTOMATION
WIRING DIAGRAM
PLANT AUTOMATION

ZF GETRIEBE, OHNE WENDETEIL, TYP B(GR.2), ERWEIT. UMFANG				
ZF GEARBOX, WITHOUT REVERSING, TYPE B(GR.2), EXTENDED SCOPE				
Auftrag/ Projekt		Zeichnungs-Nr. Drawing No.	Blatt Sheet	
BLUE-VIS		BZ00E50000064	72	
Referenz-Nr./Reference-No.		-----		

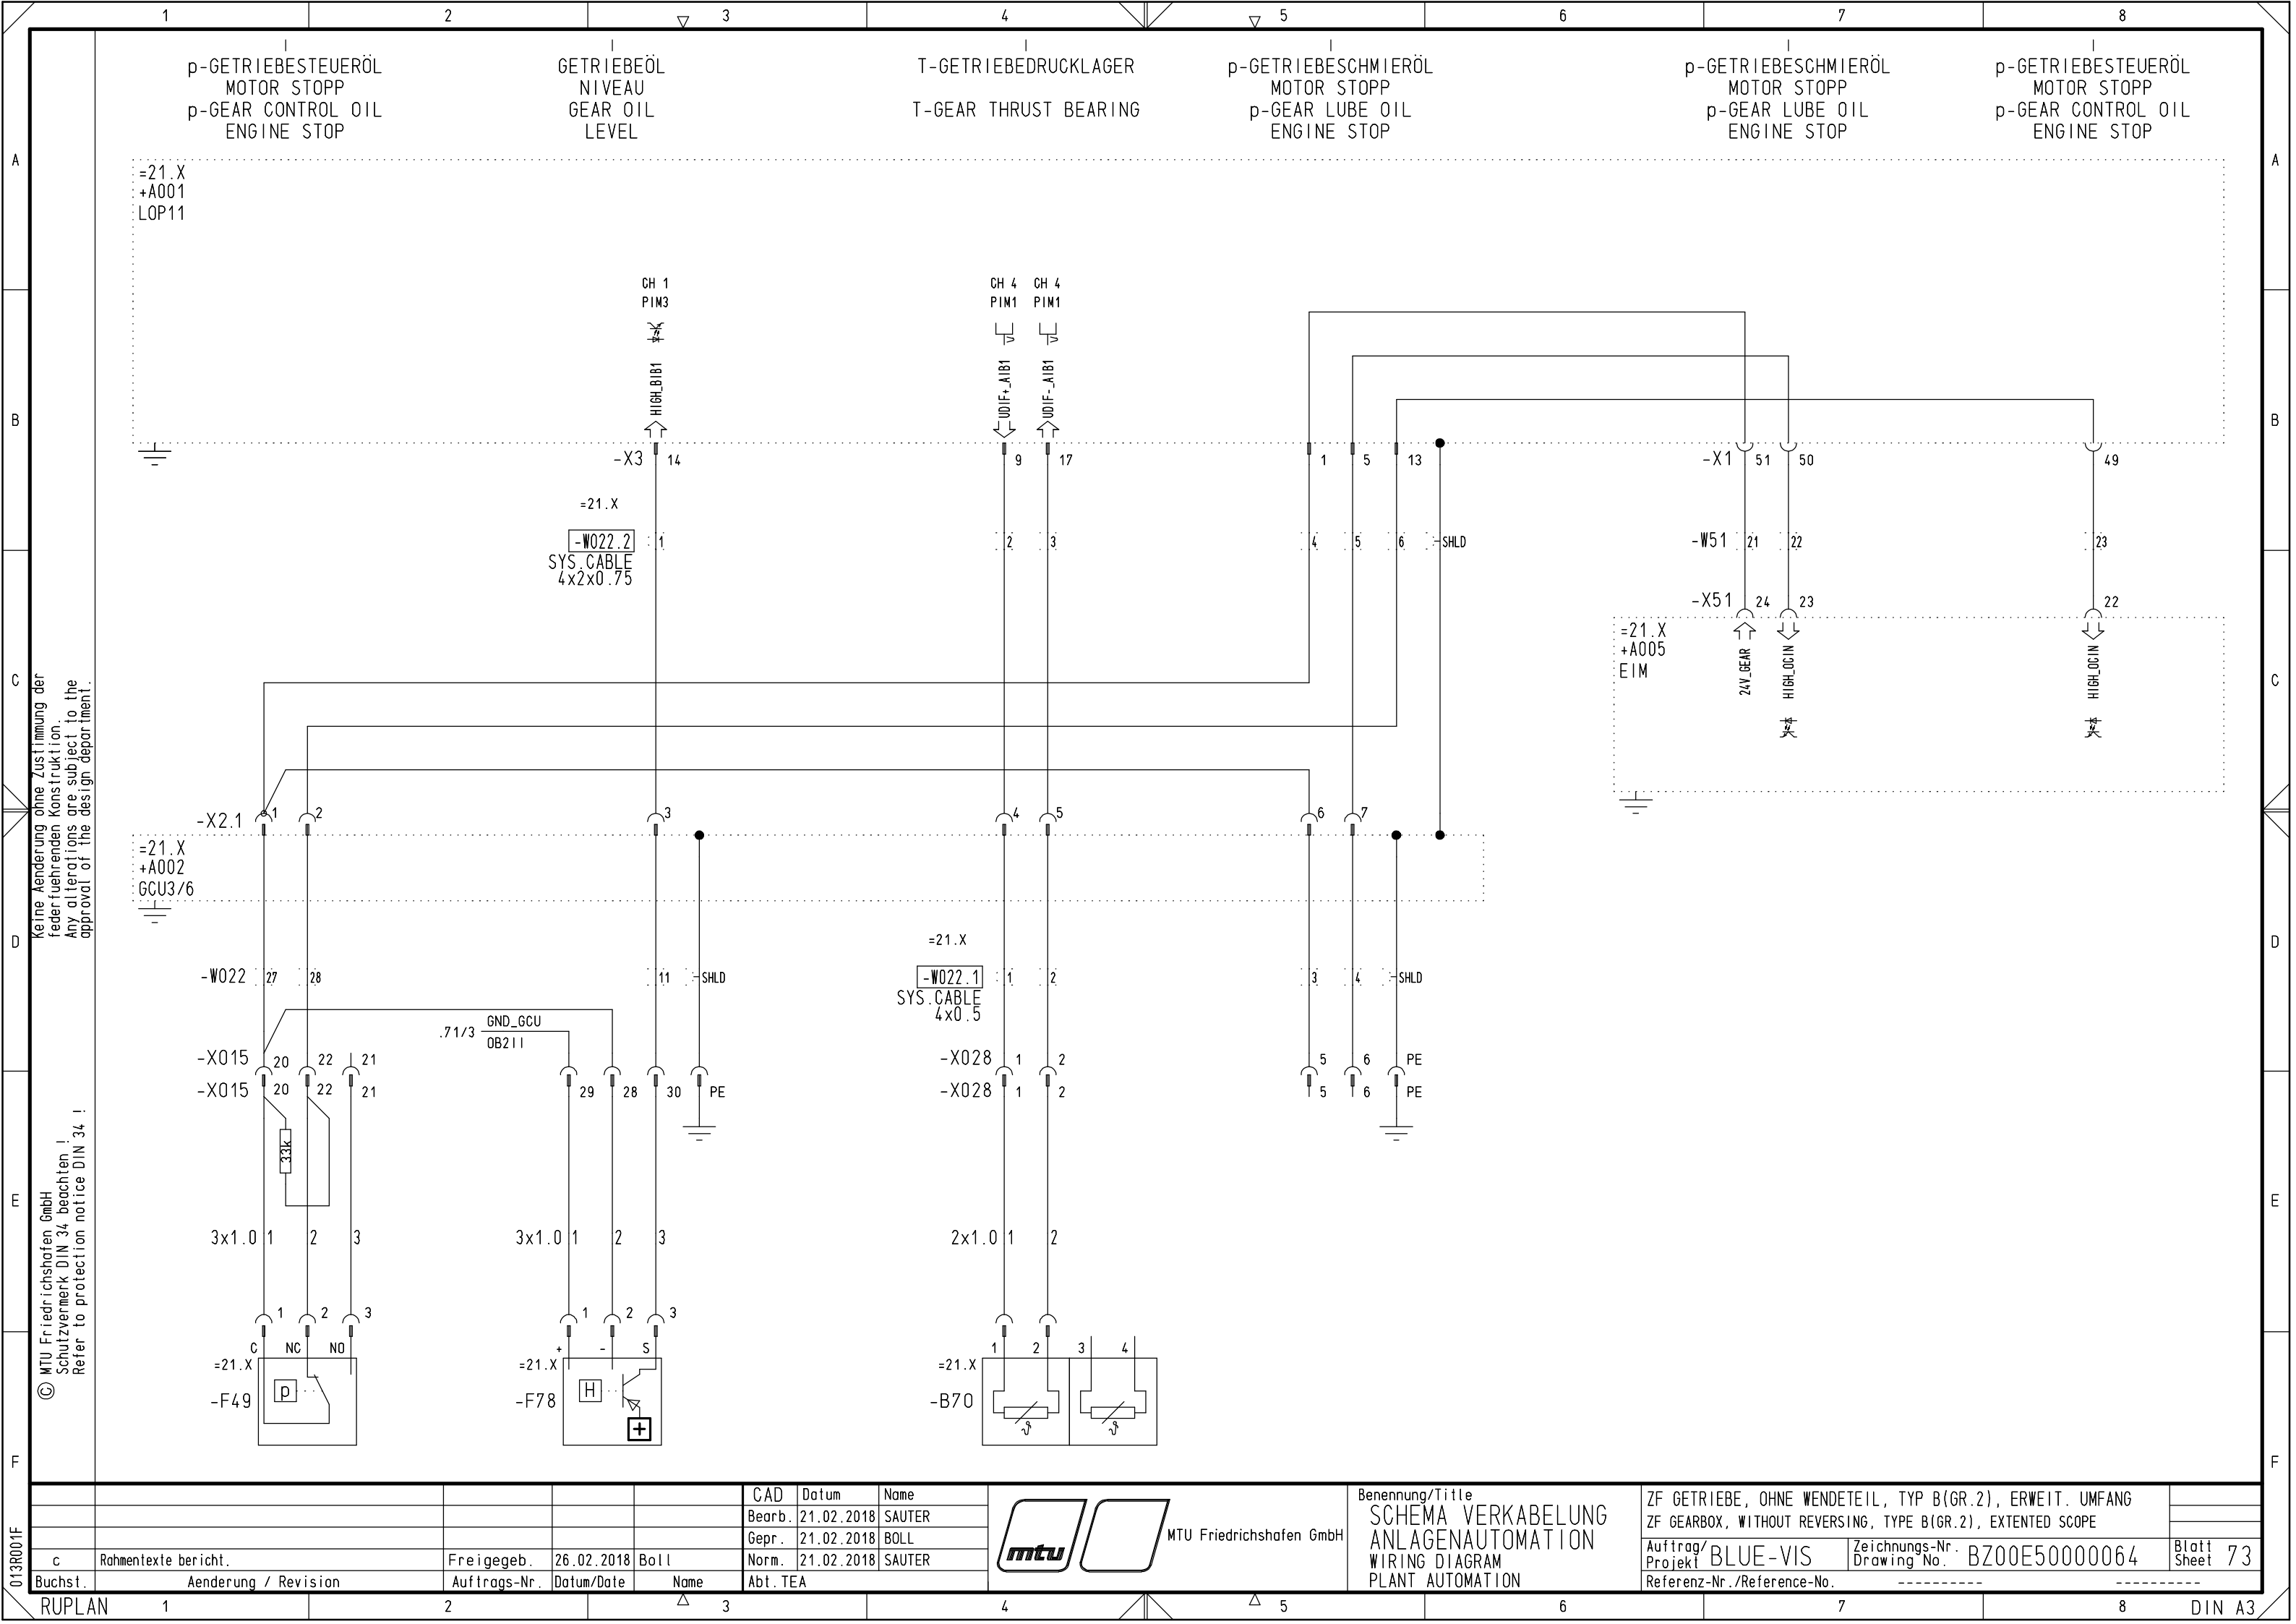

© MTU Friedrichshafen GmbH
Schutzvermerk DIN 34 beachten !
Refer to protection notice DIN 34 !

					CAD	Datum	Name	 MTU Friedrichshafen GmbH	Benennung/Title SCHEMA VERKABELUNG ANLAGENAUTOMATION WIRING DIAGRAM PLANT AUTOMATION	ZF GETRIEBE, OHNE WENDETEIL, TYP B(GR.3), HINWEISE					
					Bearb.	21.02.2018	SAUTER			ZF GEARBOX, WITHOUT REVERSING, TYPE B(GR.3), INSTRUCTIONS					
					Gepr.	21.02.2018	BOLL								
					Norm.	21.02.2018	SAUTER								
c	Rahmentexte bericht.	Freigegeb.	26.02.2018	Boll						Auftrag/ Projekt	BLUE-VIS	Zeichnungs-Nr. Drawing No.	BZ00E500000064	Blatt Sheet	75
Buchst.	Aenderung / Revision	Auftrags-Nr.	Datum/Date	Name	Abt. TEA					Referenz-Nr./Reference-No.					

Keine Änderung ohne Zustimmung der
federführenden Konstruktion.
Any alterations are subject to the
approval of the design department.

© MTU Friedrichshafen GmbH
Schutzvermerk DIN 34 beachten !
Refer to protection notice DIN 34 !

					CAD	Datum	Name
					Bearb.	21.02.2018	SAUTER
					Gepr.	21.02.2018	BOLL
					Norm.	21.02.2018	SAUTER
c	Rahmentexte bericht.	Freigegeb.	26.02.2018	Boll	Abt. TEA		
Buchst.	Aenderung / Revision	Auftrags-Nr.	Datum/Date	Name			




MTU Friedrichshafen GmbH

Benennung/Title
SCHEMA VERKABELUNG
ANLAGENAUTOMATION
WIRING DIAGRAM
PLANT AUTOMATION

ZF GETRIEBE, OHNE WENDETEIL, TYP B(GR.3), ERWEIT. UMFANG
ZF GEARBOX, WITHOUT REVERSING, TYPE B(GR.3), EXTENDED SCOPE
Auftrag/Projekt BLUE-VIS
Zeichnungs-Nr. BZ00E50000064
Referenz-Nr./Reference-No. -----

Blatt 76
Sheet

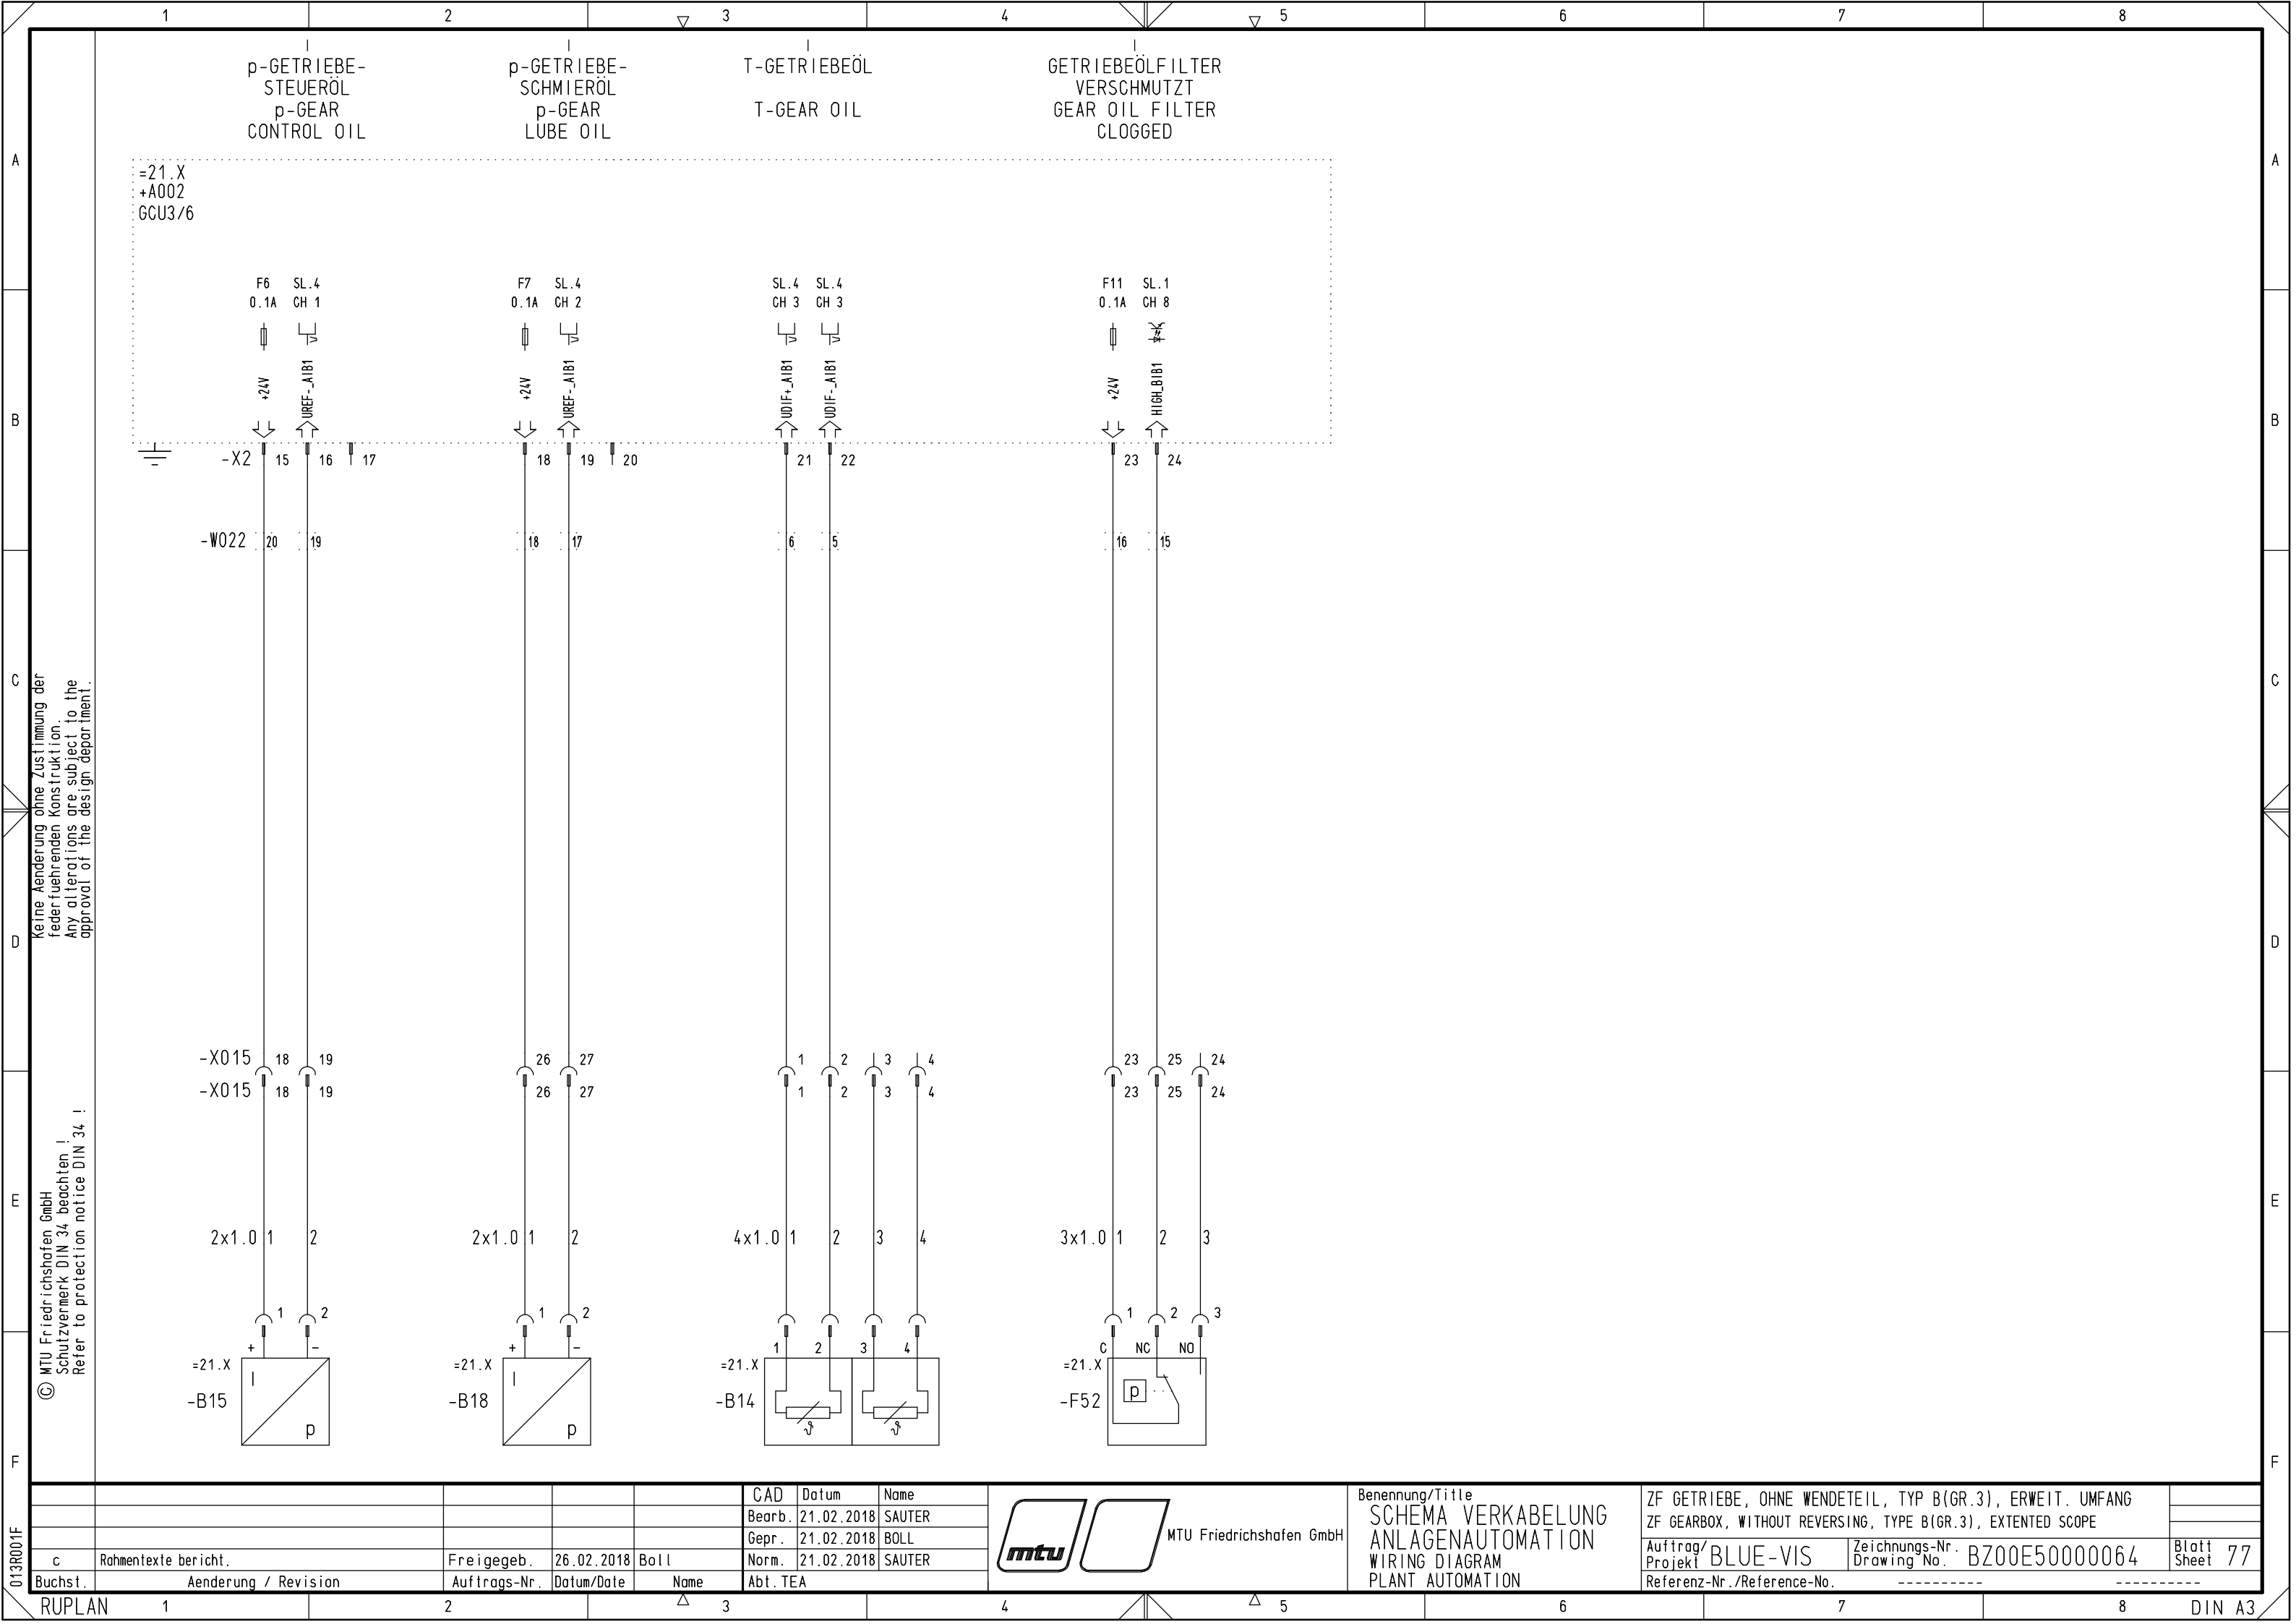


					CAD	Datum	Name
					Bearb.	21.02.2018	SAUTER
					Gepr.	21.02.2018	BOLL
					Norm.	21.02.2018	SAUTER
c	Rahmentexte bericht.	Freigegeb.	26.02.2018	Boll	Abt. TEA		
Buchst.	Aenderung / Revision	Auftrags-Nr.	Datum/Date	Name			




MTU Friedrichshafen GmbH

Benennung/Title
SCHEMA VERKABELUNG
ANLAGENAUTOMATION
WIRING DIAGRAM
PLANT AUTOMATION

ZF GETRIEBE, OHNE WENDETEIL, TYP B(GR.3), ERWEIT. UMFANG ZF GEARBOX, WITHOUT REVERSING, TYPE B(GR.3), EXTENDED SCOPE			
Auftrag/ Projekt	BLUE-VIS	Zeichnungs-Nr. Drawing No.	BZ00E50000064
Referenz-Nr./Reference-No.		-----	
			Blatt Sheet 77

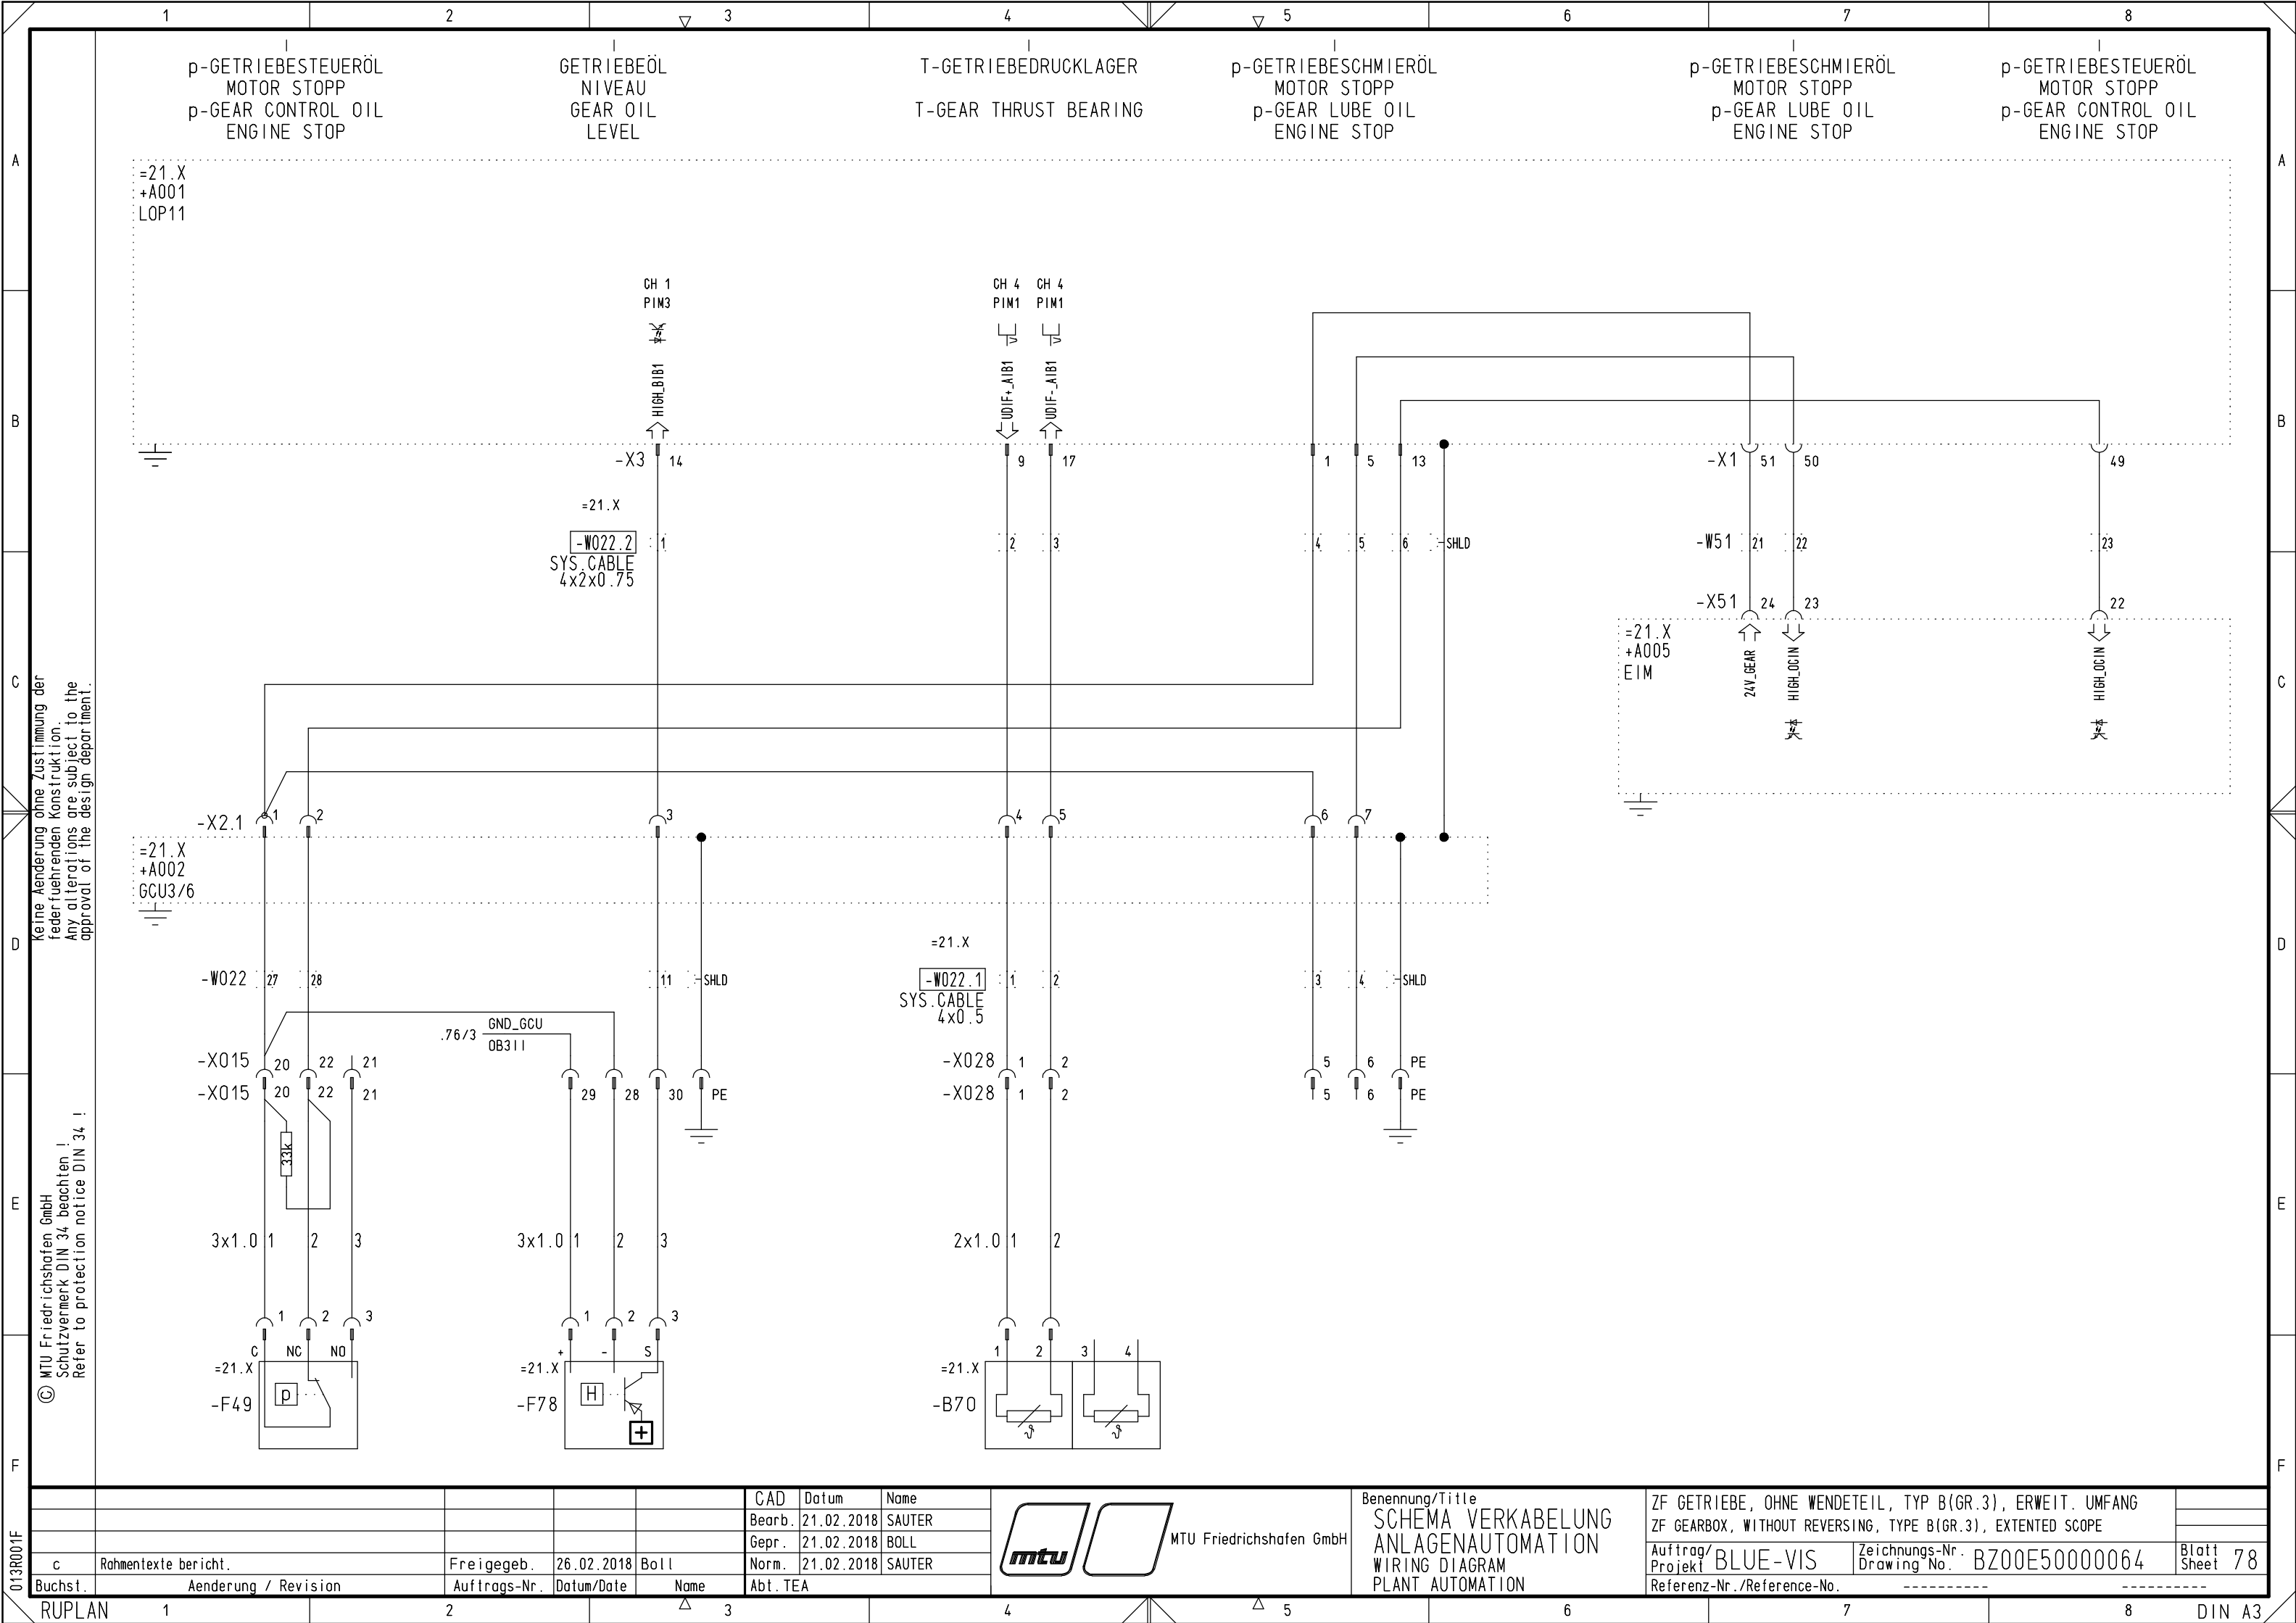

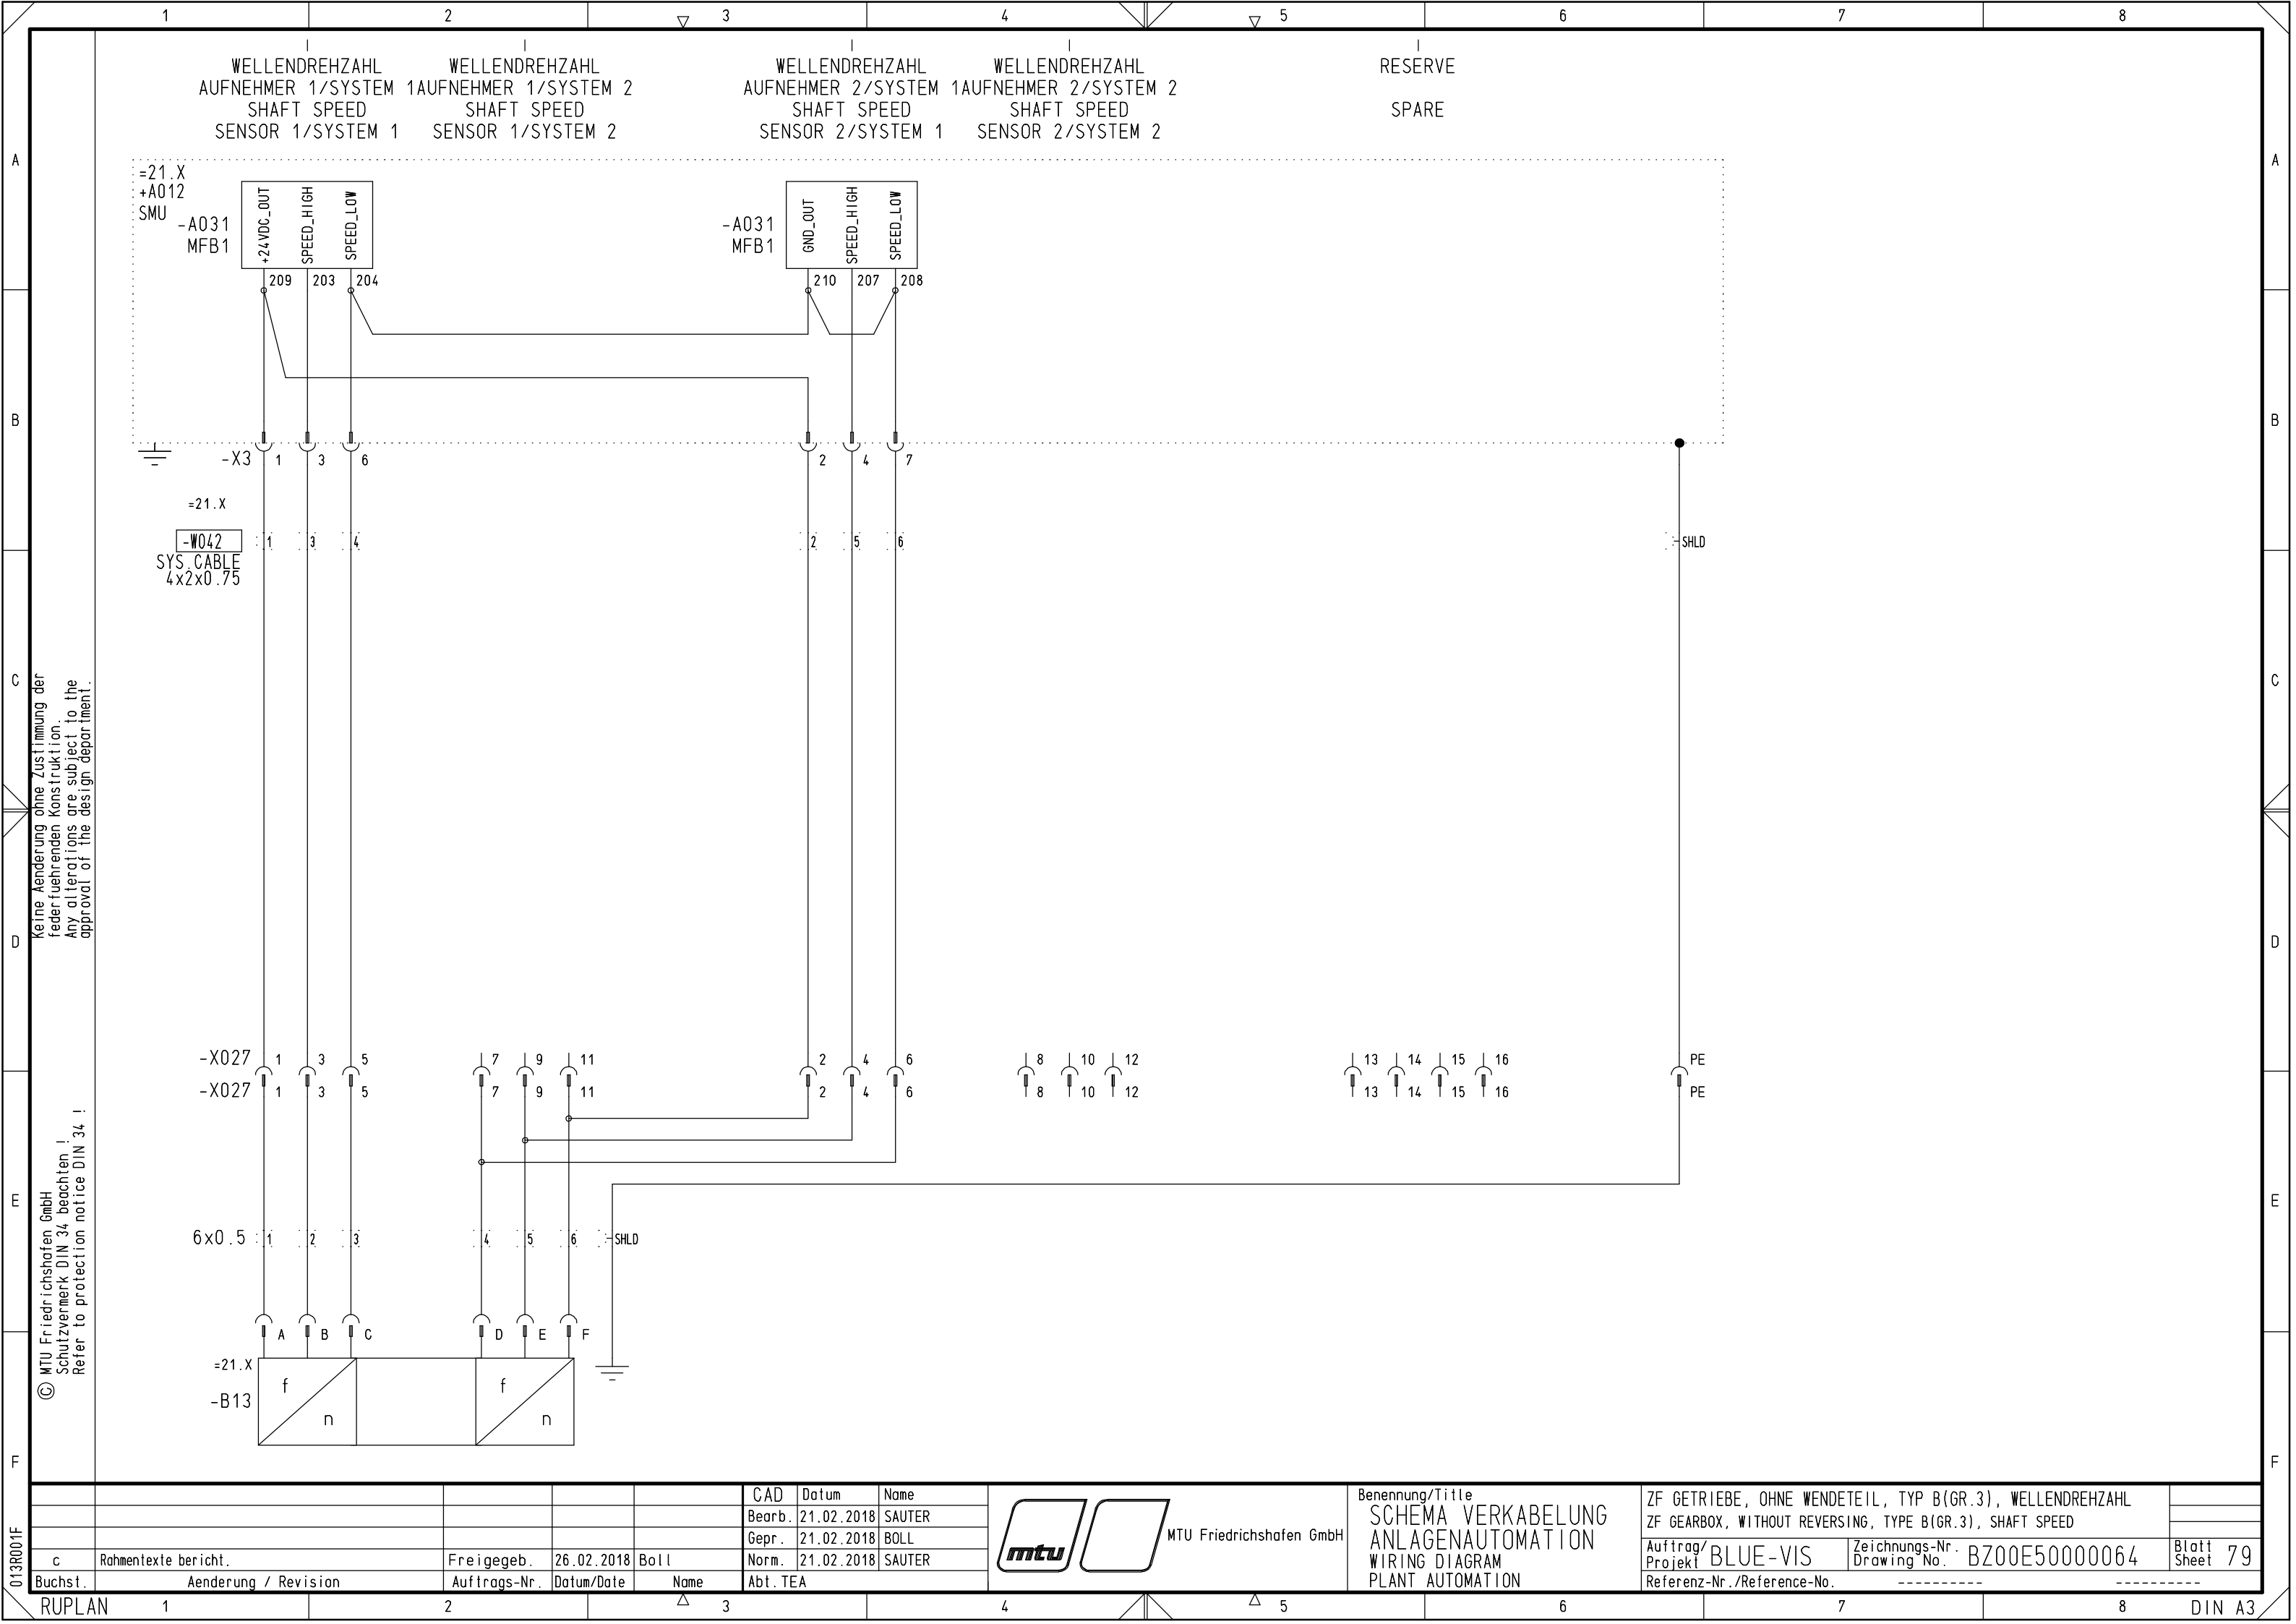


A	B	C	D	E	F	1										2										3										4										5										6										7										8	
						GÜLTIG FÜR: VALID FOR:	

Keine Änderung ohne Zustimmung der
federführenden Konstruktion.
Any alterations are subject to the
approval of the design department.

© MTU Friedrichshafen GmbH
Schutzvermerk DIN 34 beachten !
Refer to protection notice DIN 34 !

013R001F

RUPLAN

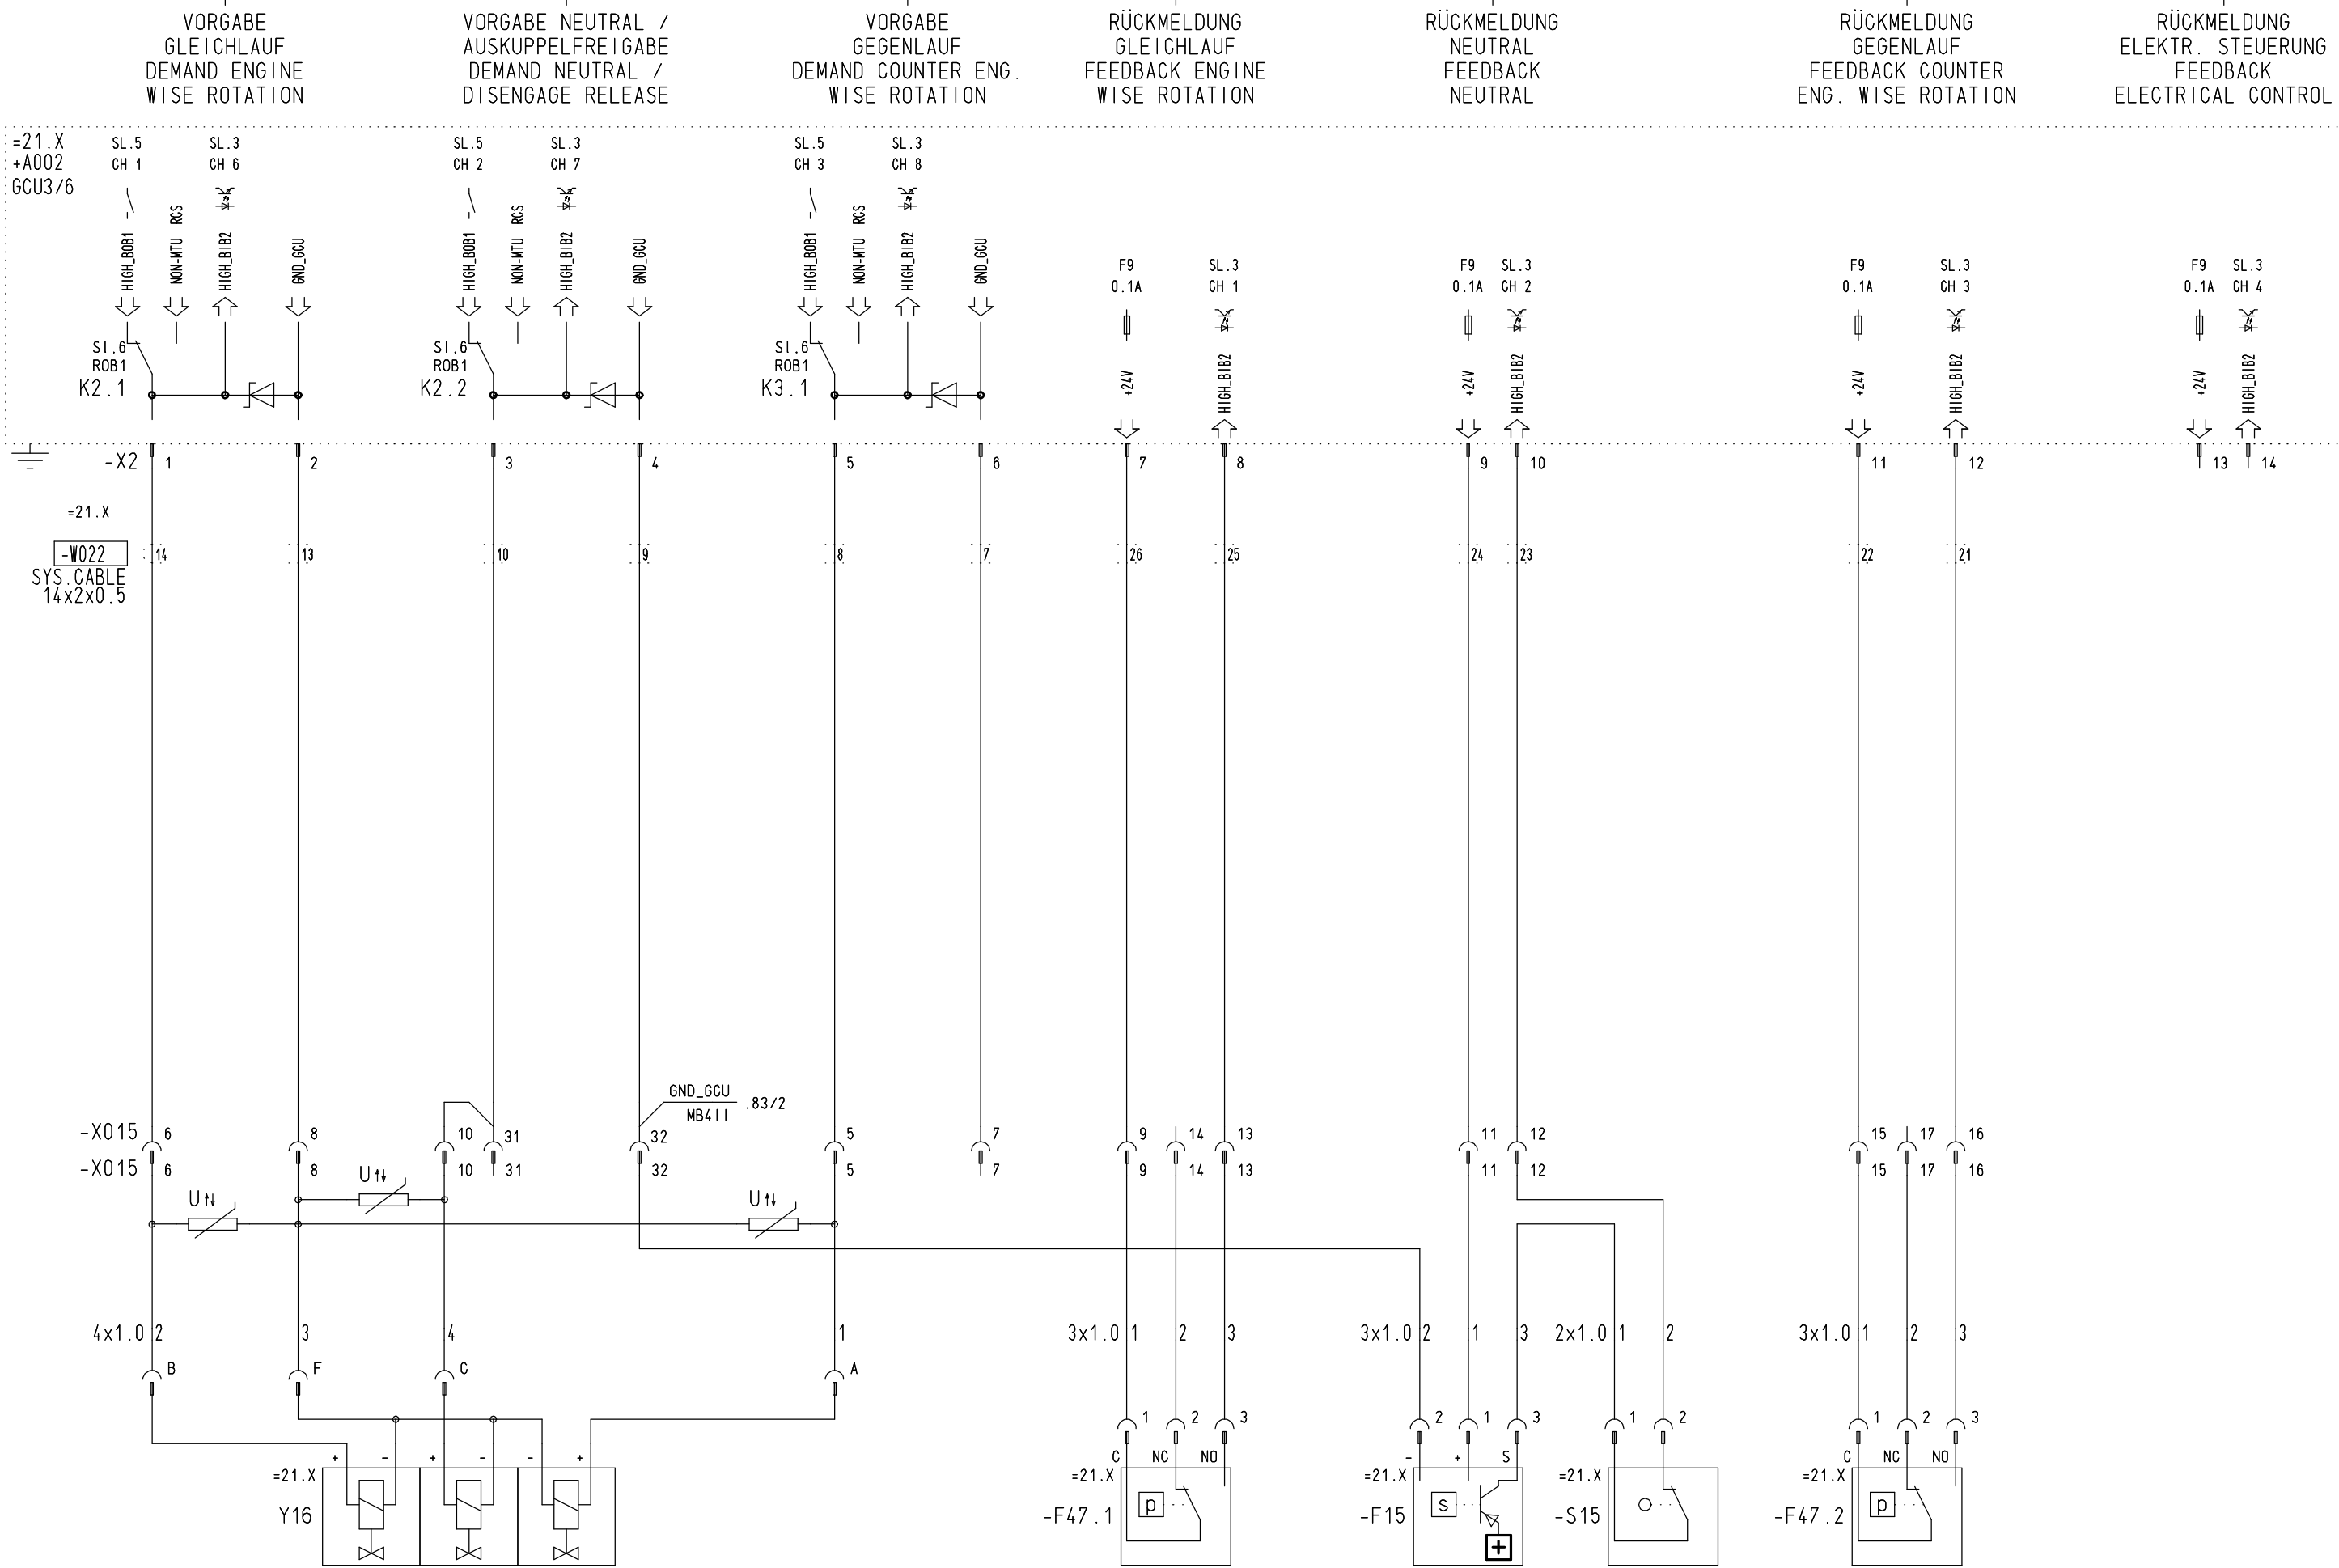


CAD	Datum	Name
Bearb.	21.02.2018	SAUTER
Gedr.	21.02.2018	BOLL
Norm.	21.02.2018	SAUTER
Abt. TEA		




Benennung/Title
SCHEMA VERKABELUNG
ANLAGENAUTOMATION
WIRING DIAGRAM
PLANT AUTOMATION

ZF GETRIEBE, MIT WENDETEIL, TYP B(GR.4), ERWEIT. UMFANG ZF GEARBOX, WITH REVERSING, TYPE B(GR.4), EXTENDED SCOPE		
Auftrag/ Projekt	BLUE-VIS	Zeichnungs-Nr. Drawing No.
Referenz-Nr./Reference-No.		BZ00E50000064
		Blatt Sheet
		81

DIN A3

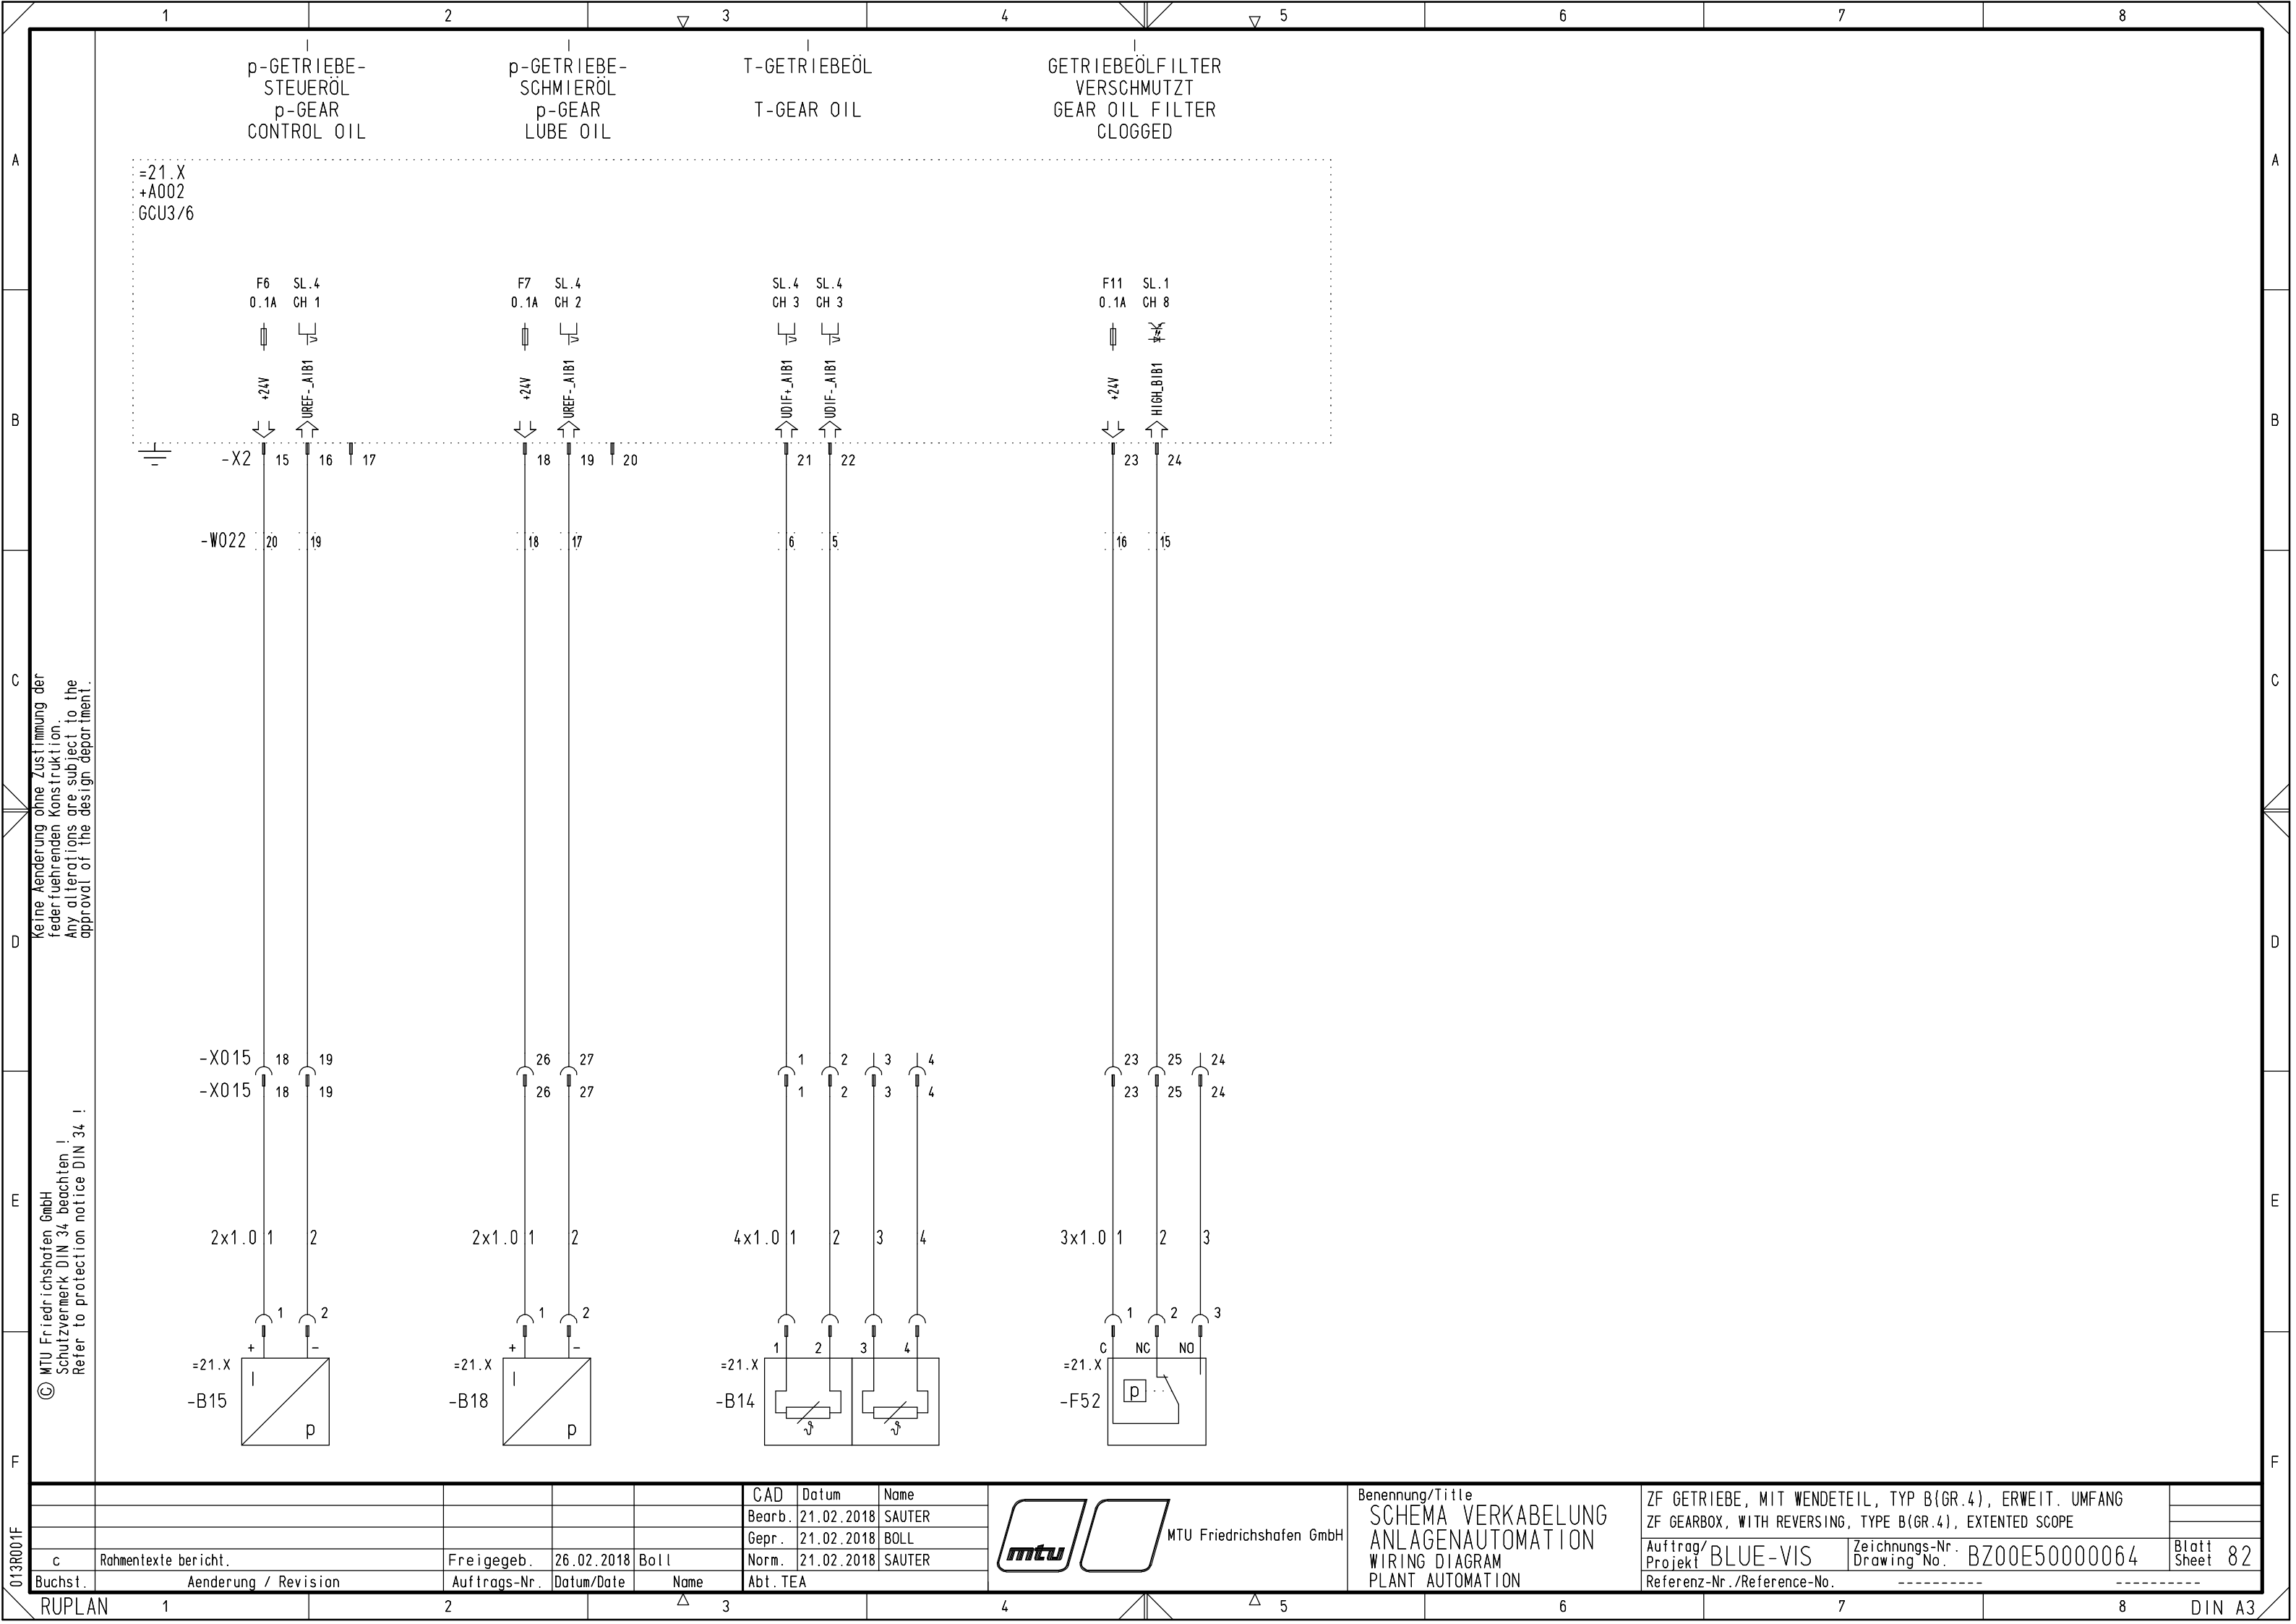

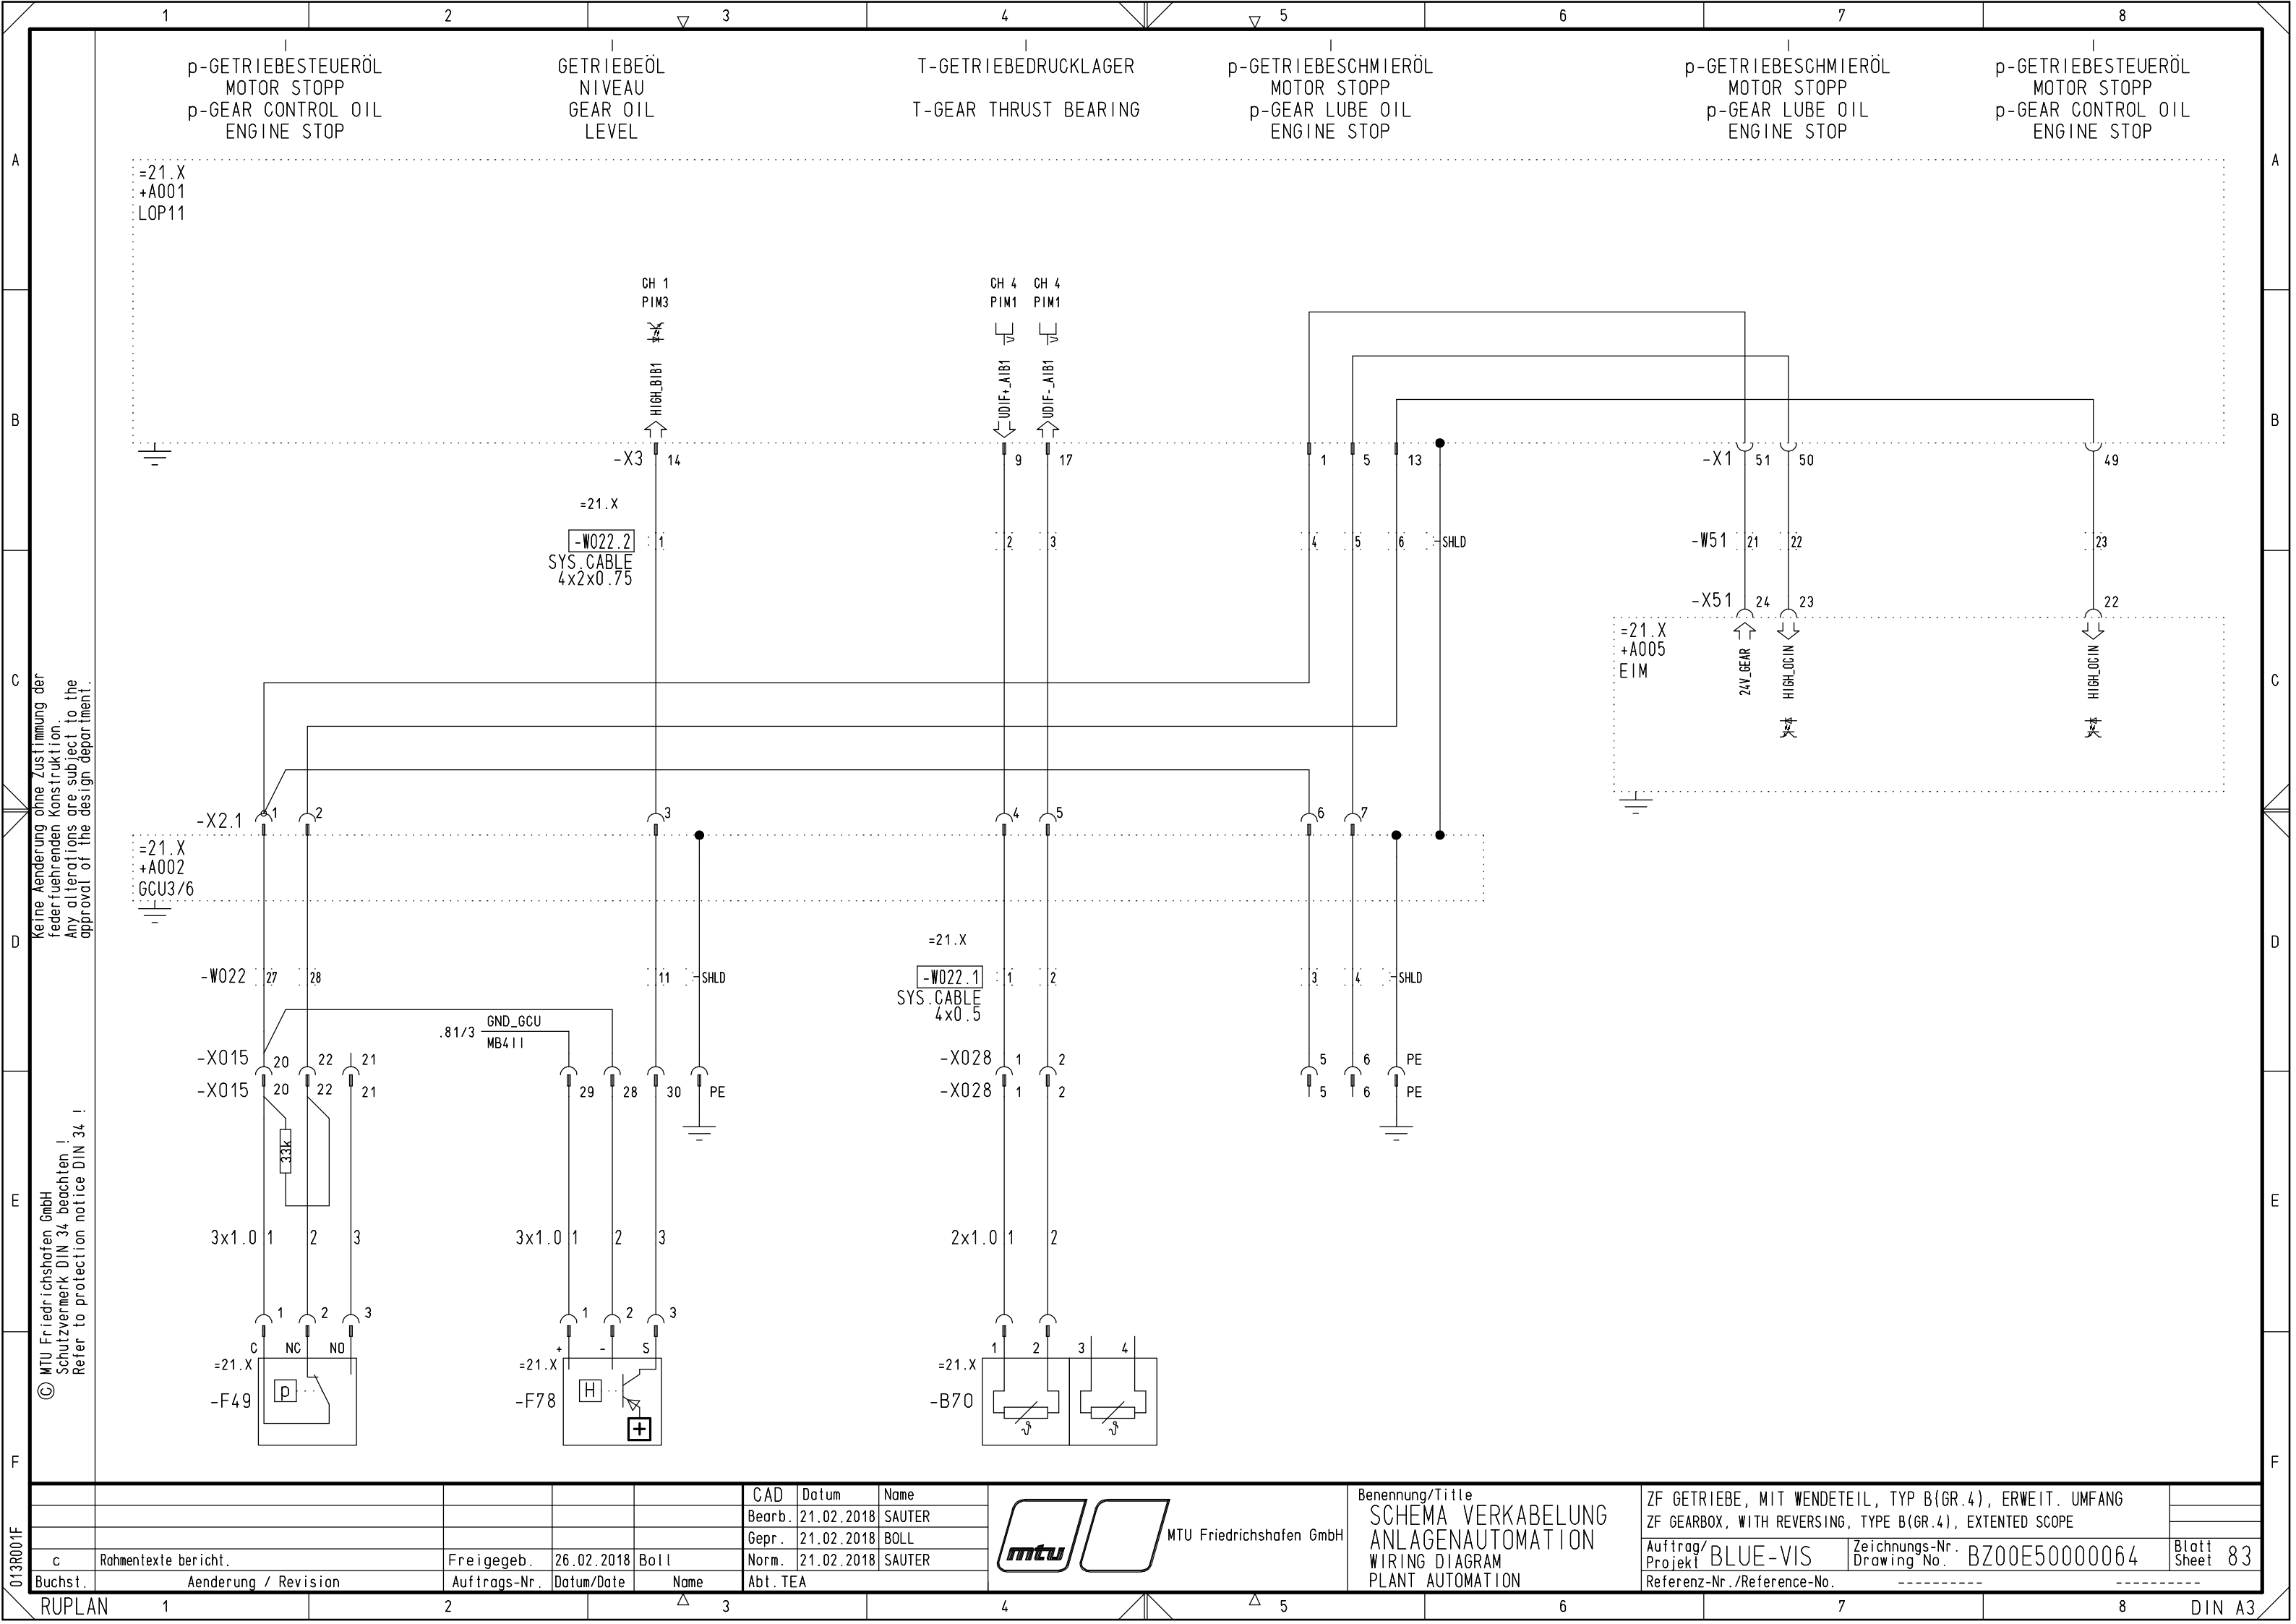

GÜLTIG FÜR: VALID FOR:	
ZF 7XXX	

© MTU Friedrichshafen GmbH
Schutzvermerk DIN 34 beachten !
Refer to protection notice DIN 34 !

 MTU Friedrichshafen GmbH	Benennung/Title	ZF GETRIEBE, MIT WENDETEIL, TYP C, HINWEISE	
	SCHEMA VERKABELUNG ANLAGENAUTOMATION WIRING DIAGRAM PLANT AUTOMATION	ZF GEARBOX, WITH REVERSING, TYPE C, INSTRUCTIONS	
	Auftrag/Projekt	Zeichnungs-Nr./Drawing No.	Blatt/Sheet
	BLUE-VIS	BZ00E50000064	85
	Referenz-Nr./Reference-No.		

Keine Änderung ohne Zustimmung der
federführenden Konstruktion.
Any alterations are subject to the
approval of the design department.

© MTU Friedrichshafen GmbH
Schutzvermerk DIN 34 beachten !
Refer to protection notice DIN 34 !


					CAD	Datum	Name
					Bearb.	21.02.2018	SAUTER
					Gepr.	21.02.2018	BOLL
					Norm.	21.02.2018	SAUTER
c	Rahmentexte bericht.	Freigegeb.	26.02.2018	Boll	Abt. TEA		
Buchst.	Aenderung / Revision	Auftrags-Nr.	Datum/Date	Name			



MTU Friedrichshafen GmbH

Benennung/Title
SCHEMA VERKABELUNG
ANLAGENAUTOMATION
WIRING DIAGRAM
PLANT AUTOMATION

ZF GETRIEBE, MIT WENDETEIL, TYP C, GRUNDUMFANG ZF GEARBOX, WITH REVERSING, TYPE C, BASIC SCOPE			Zeichnungs-Nr. Drawing No. BZ00E50000064	Blatt Sheet 86
Auftrag/ Projekt	BLUE-VIS	Referenz-Nr./Reference-No.		

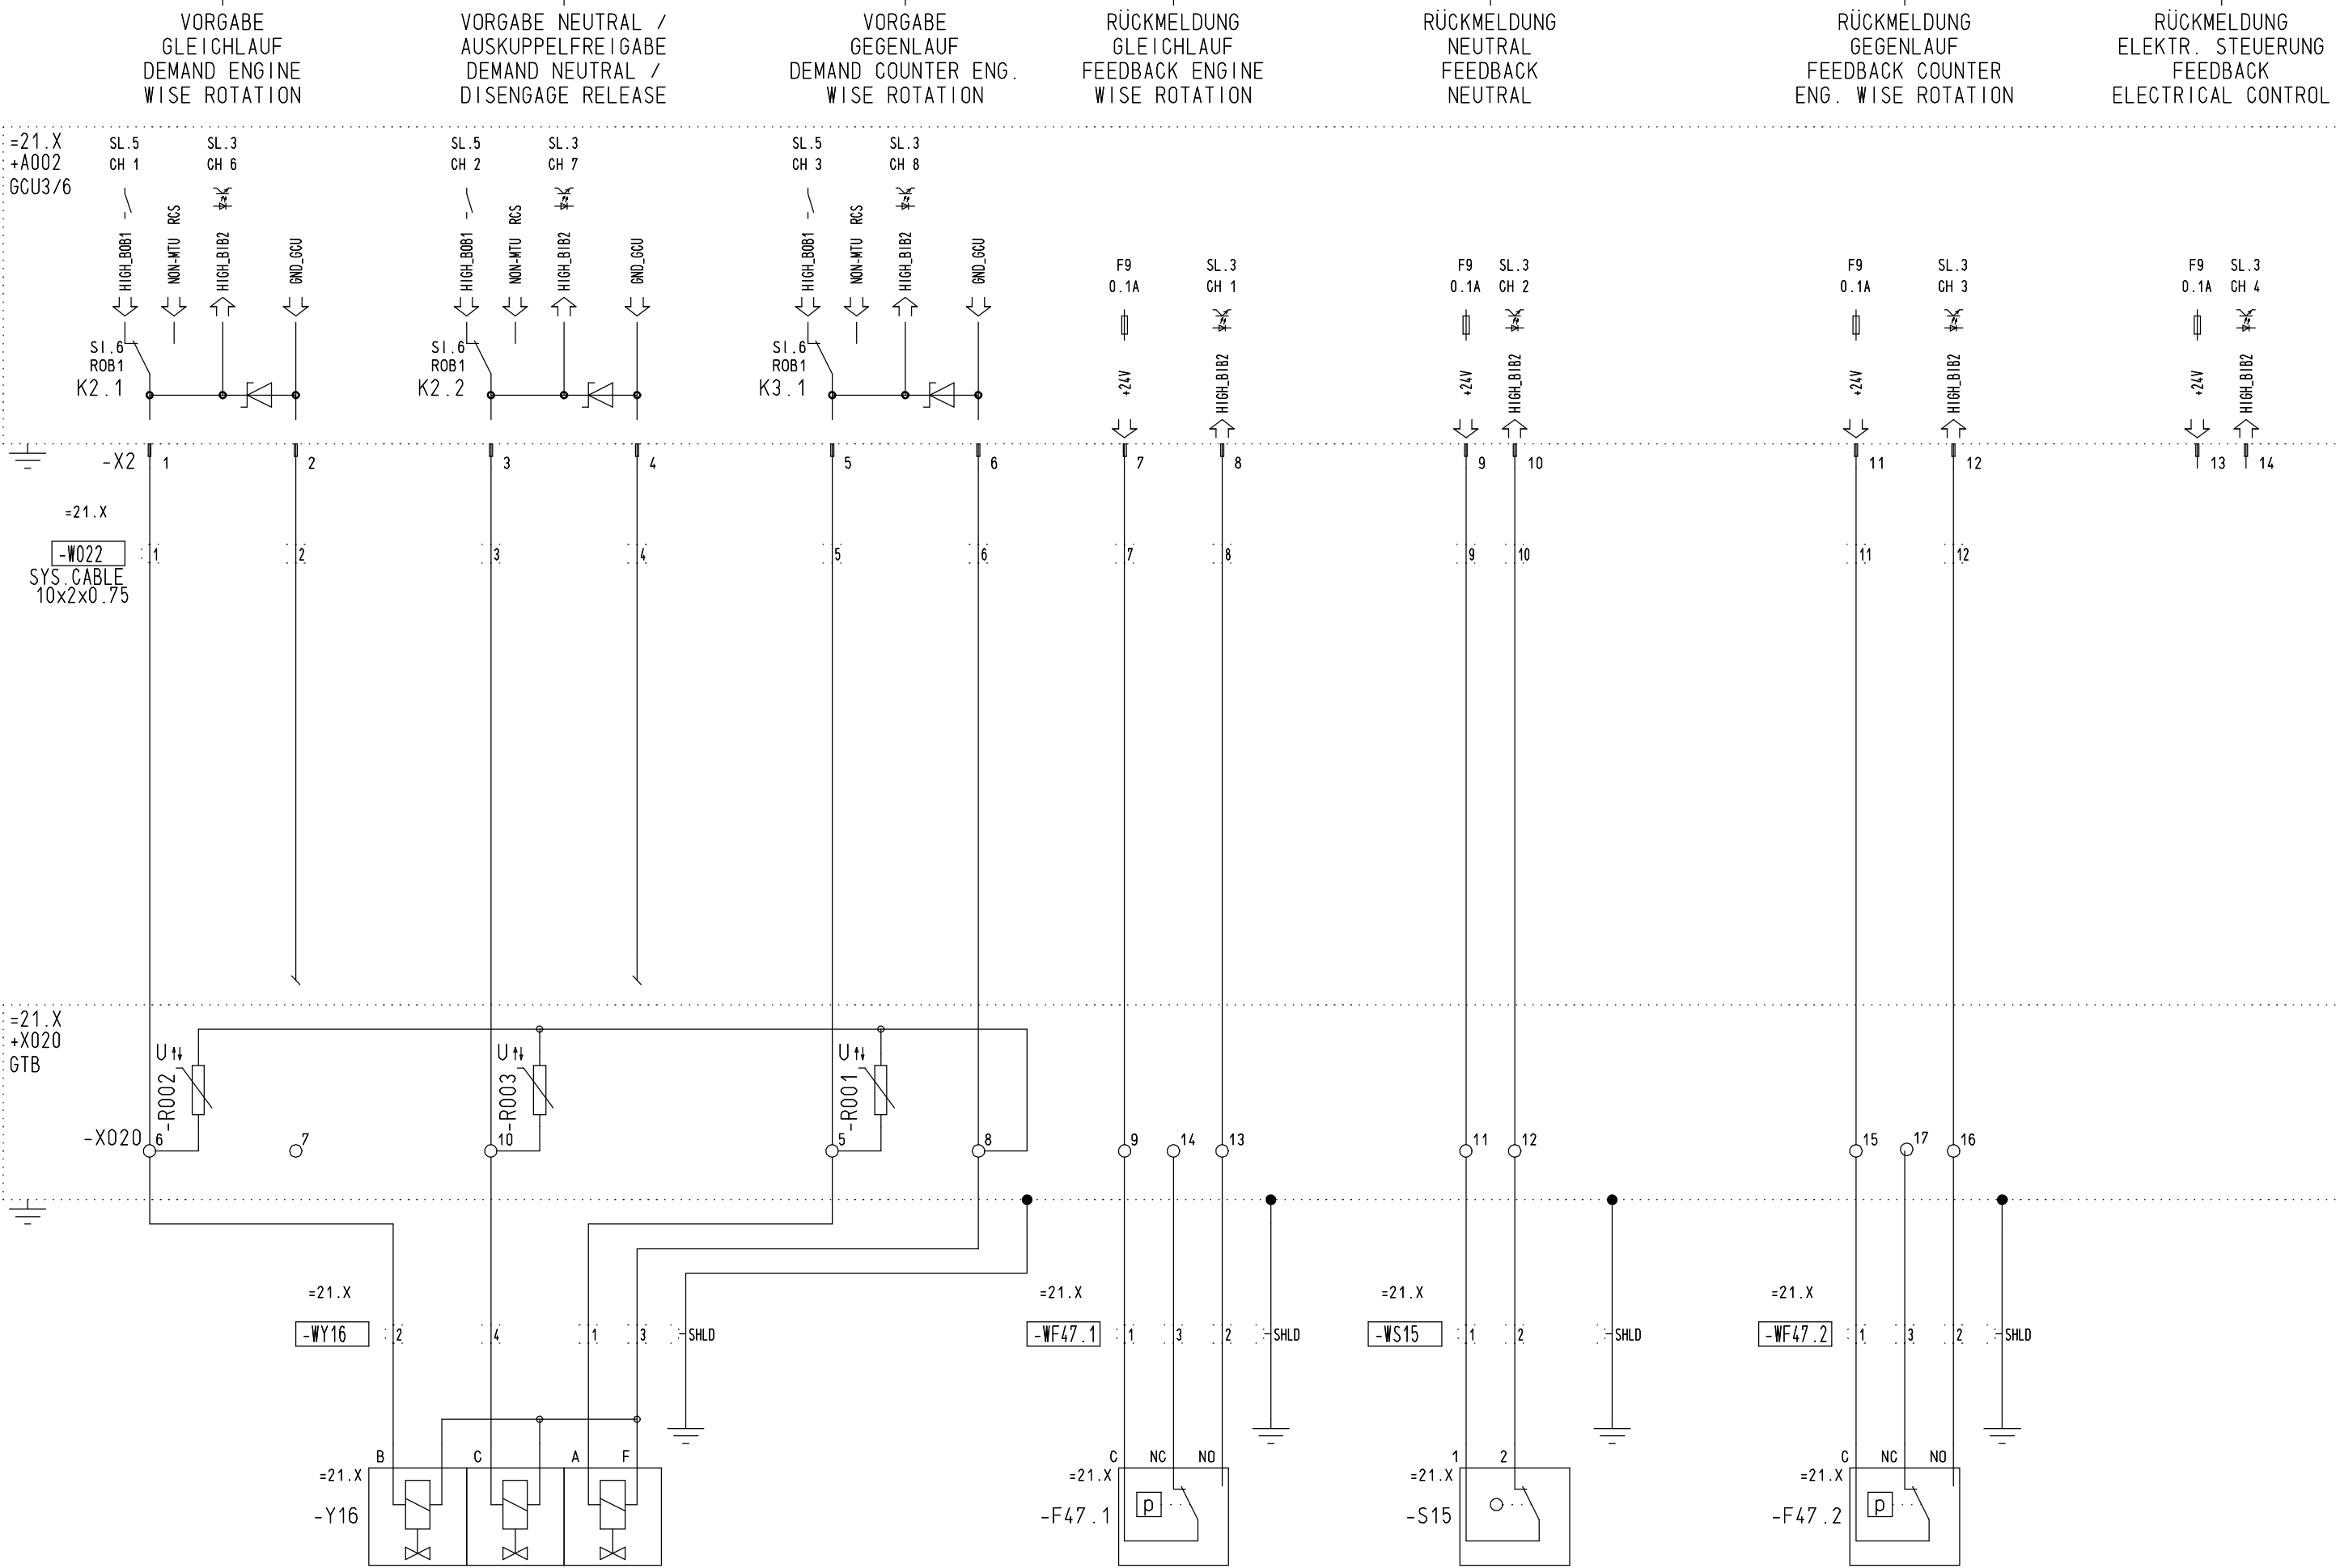


Keine Änderung ohne Zustimmung der
federführenden Konstruktion.
Any alterations are subject to the
approval of the design department.

© MTU Friedrichshafen GmbH
Schutzmerk DIN 34 beachten !
Refer to protection notice DIN 34 !

013R001F
Buchst. Aenderung / Revision

RUPLAN

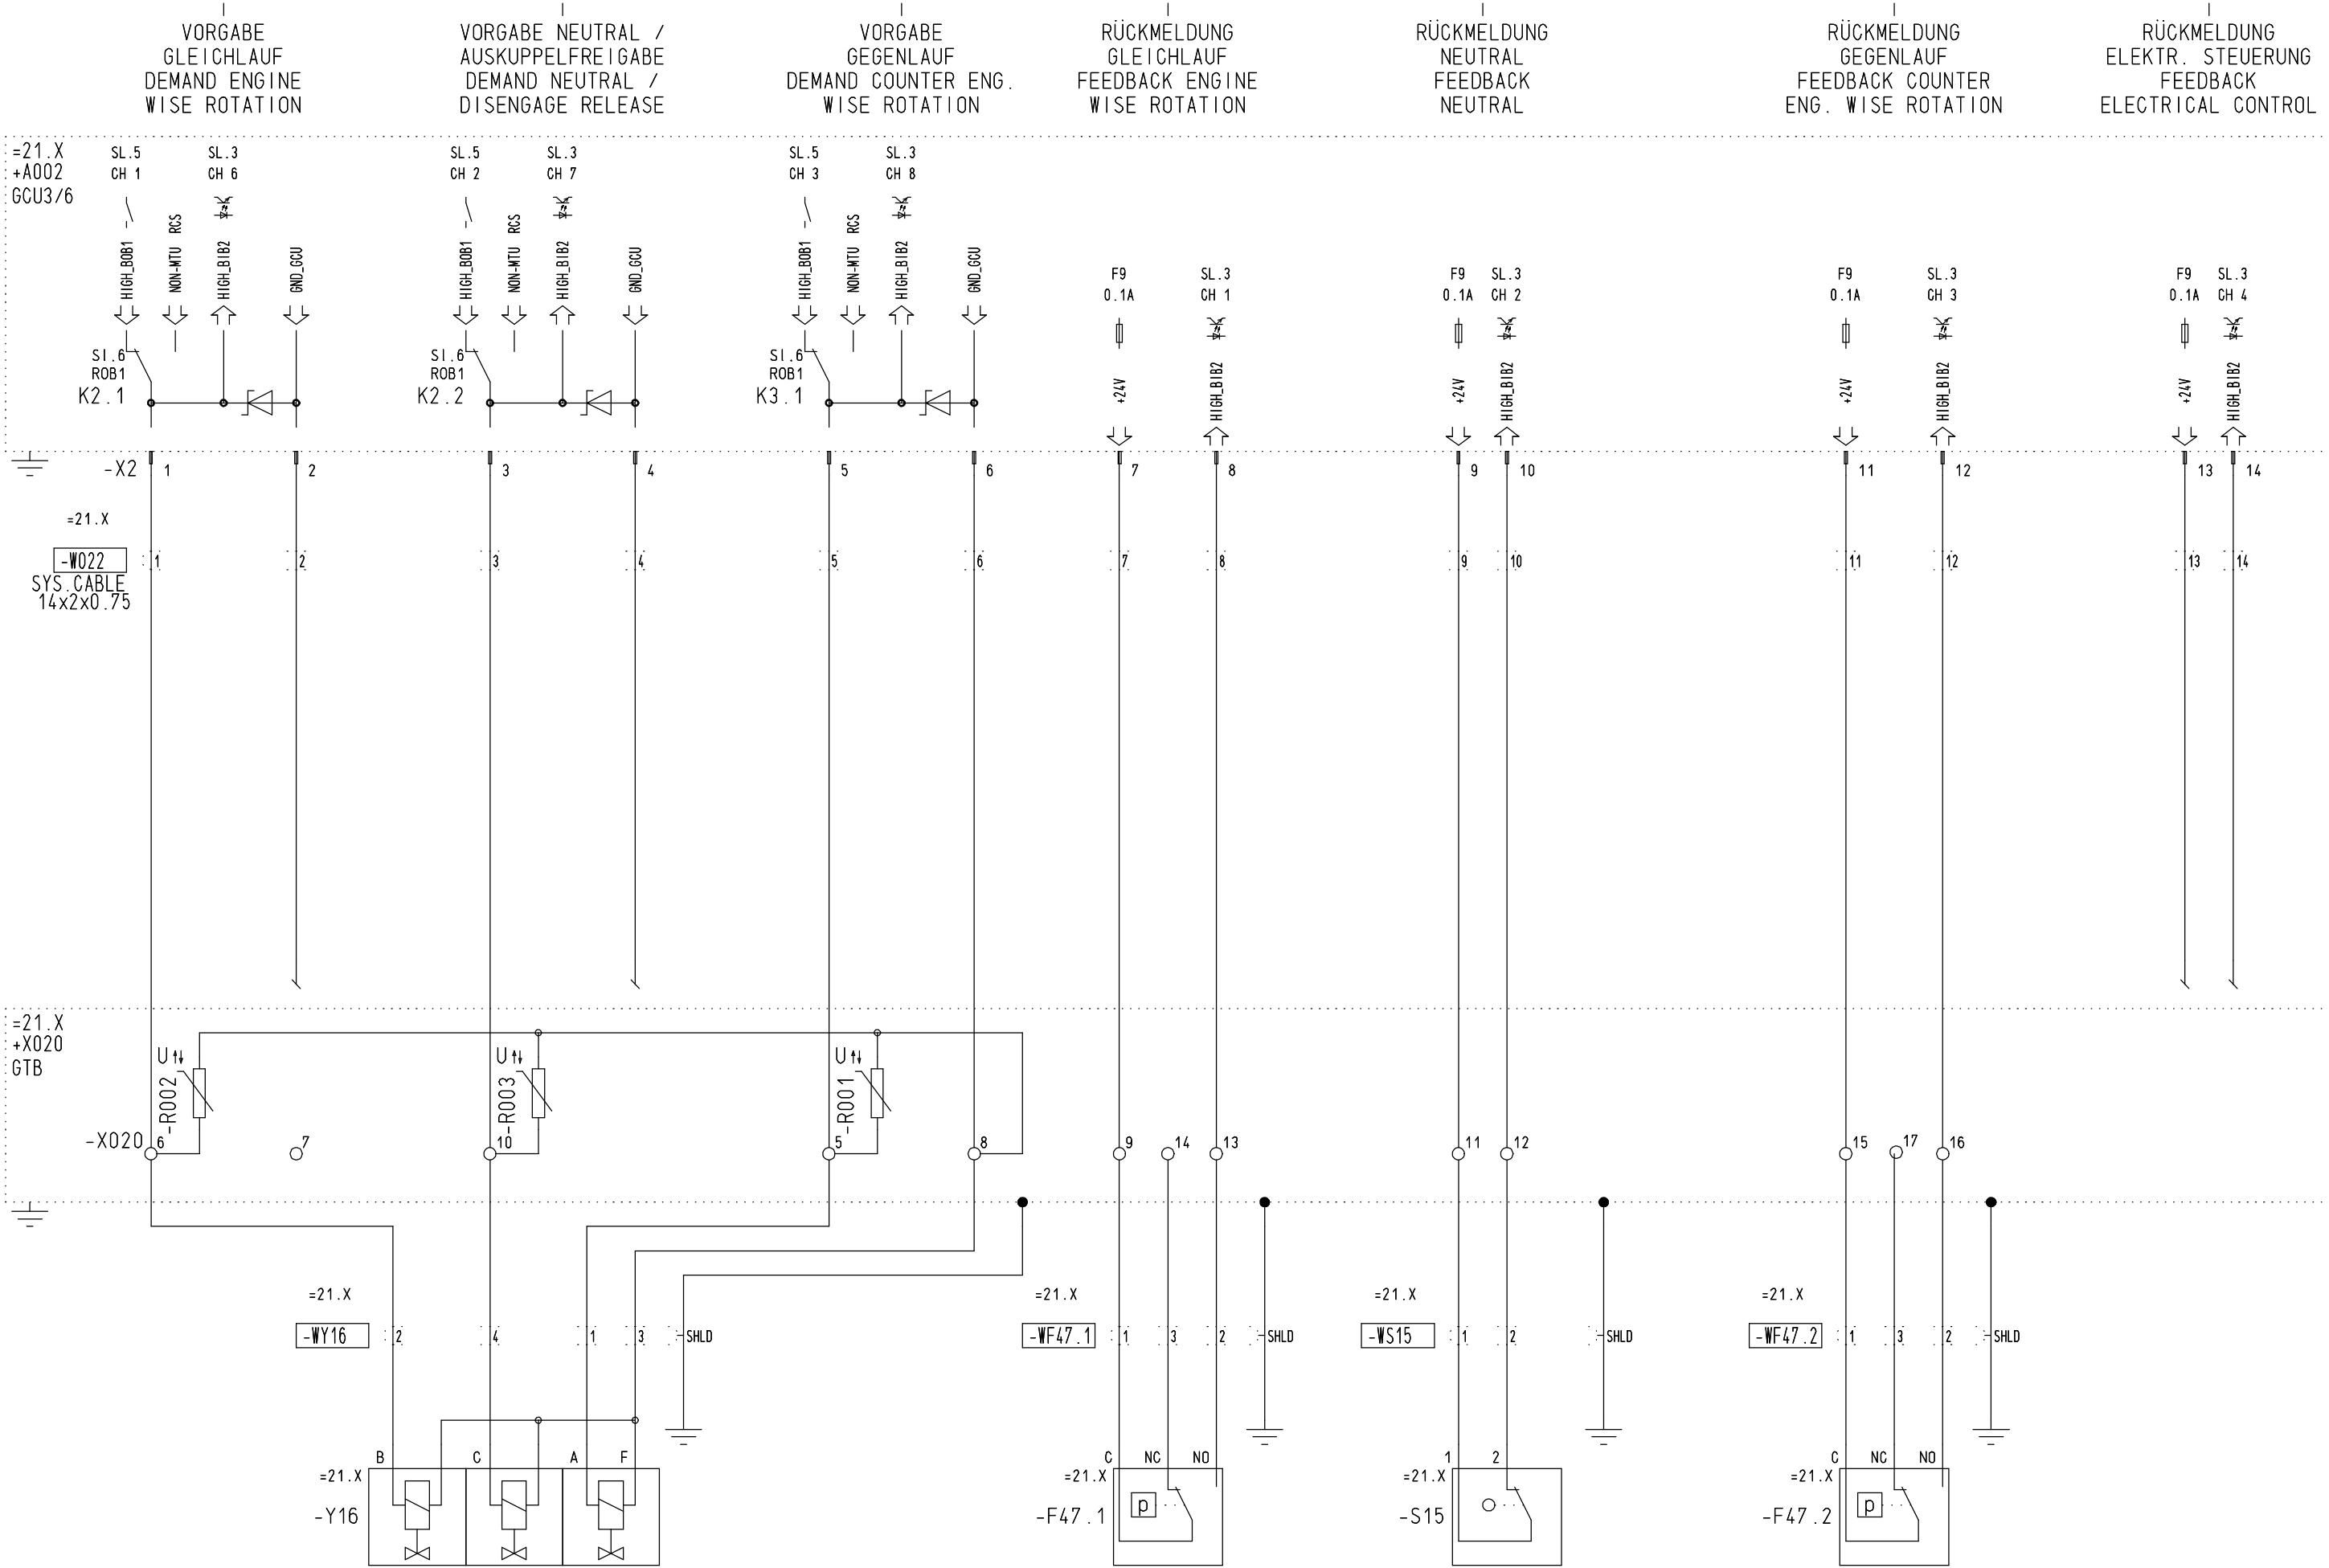

CAD	Datum	Name
Bearb.	21.02.2018	SAUTER
Gepr.	21.02.2018	BOLL
Norm.	21.02.2018	SAUTER
Abt. TEA		



MTU Friedrichshafen GmbH


Benennung/Title
SCHEMA VERKABELUNG
ANLAGENAUTOMATION
WIRING DIAGRAM
PLANT AUTOMATION

ZF GETRIEBE, MIT WENDETEIL, TYP C, ERWEIT. UMFANG
ZF GEARBOX, WITH REVERSING, TYPE C, EXTENDED SCOPE

Auftrag/Projekt BLUE-VIS
Zeichnungs-Nr. BZ00E50000064
Referenz-Nr./Reference-No. -----

Blatt 88
Sheet

DIN A3

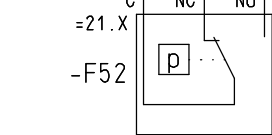


RUPLAN	1	2	3	4	5	6	7	8	DIN A3
--------	---	---	---	---	---	---	---	---	--------

Keine Änderung ohne Zustimmung der
federführenden Konstruktion.
Any alterations are subject to the
approval of the design department.

© MTU Friedrichshafen GmbH
Schutzvermerk DIN 34 beachten !
Refer to protection notice DIN 34 !

013R001F

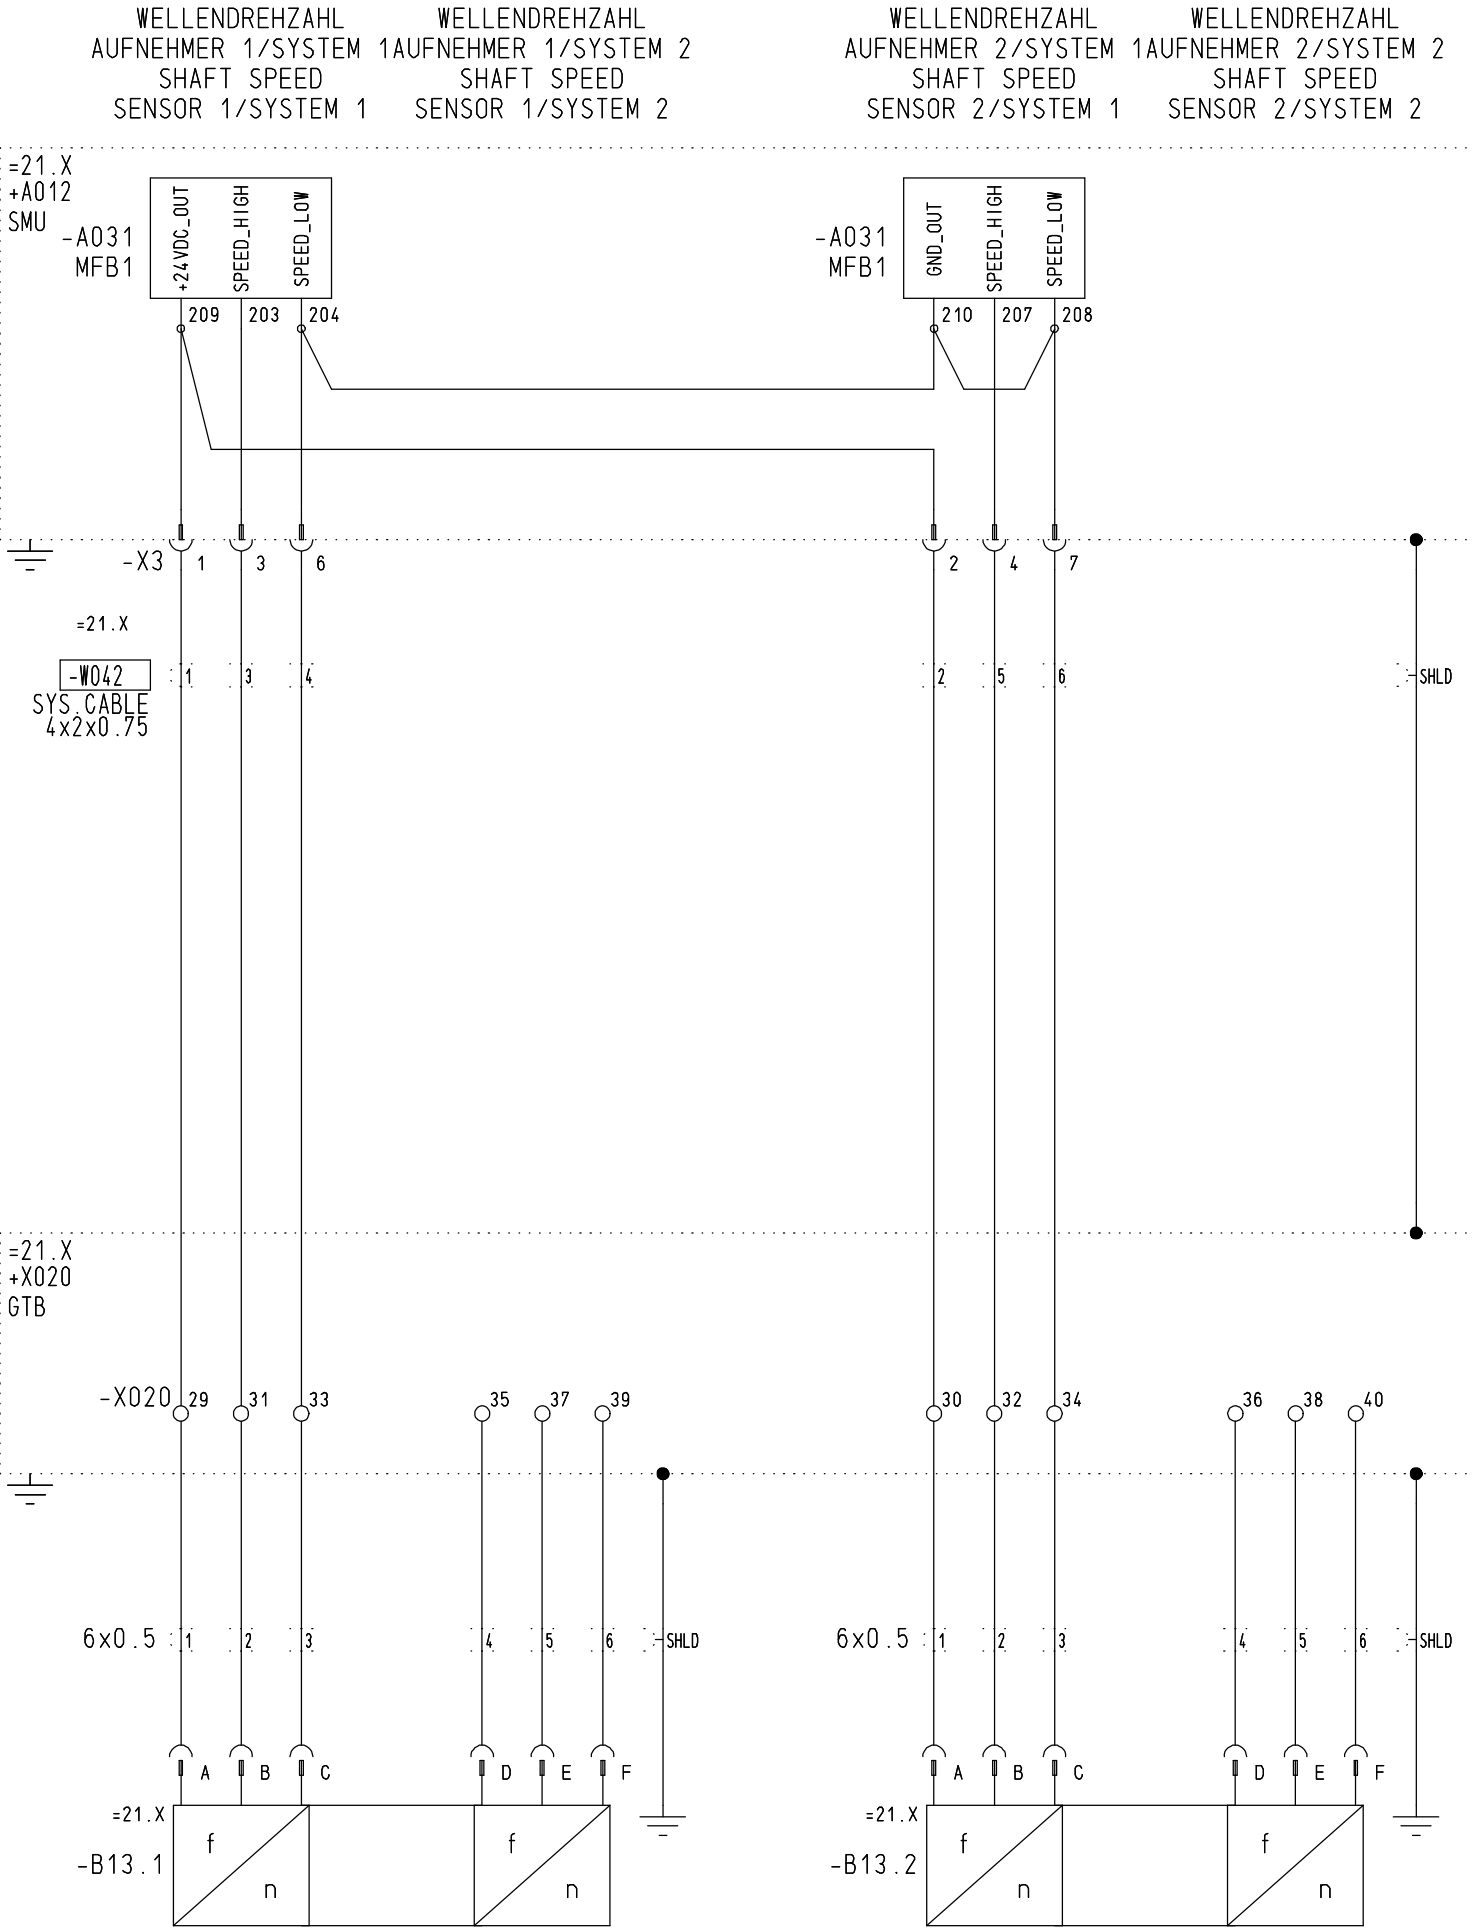


					CAD	Datum	Name
					Bearb.	21.02.2018	SAUTER
					Gepr.	21.02.2018	BOLL
					Norm.	21.02.2018	SAUTER
c	Rahmentexte bericht.	Freigegeb.	26.02.2018	Boll	Abt. TEA		
Buchst.	Aenderung / Revision	Auftrags-Nr.	Datum/Date	Name			



MTU Friedrichshafen GmbH

Benennung/Title
SCHEMA VERKABELUNG
ANLAGENAUTOMATION
WIRING DIAGRAM
PLANT AUTOMATION

ZF GETRIEBE, MIT WENDETEIL, TYP C, WELLENDREHZAHL ZF GEARBOX, WITH REVERSING, TYPE C, SHAFT SPEED		Auftrag/ Projekt BLUE-VIS		Zeichnungs-Nr. Drawing No. BZ00E50000064	Blatt Sheet 91
Referenz-Nr./Reference-No.		-----		-----	

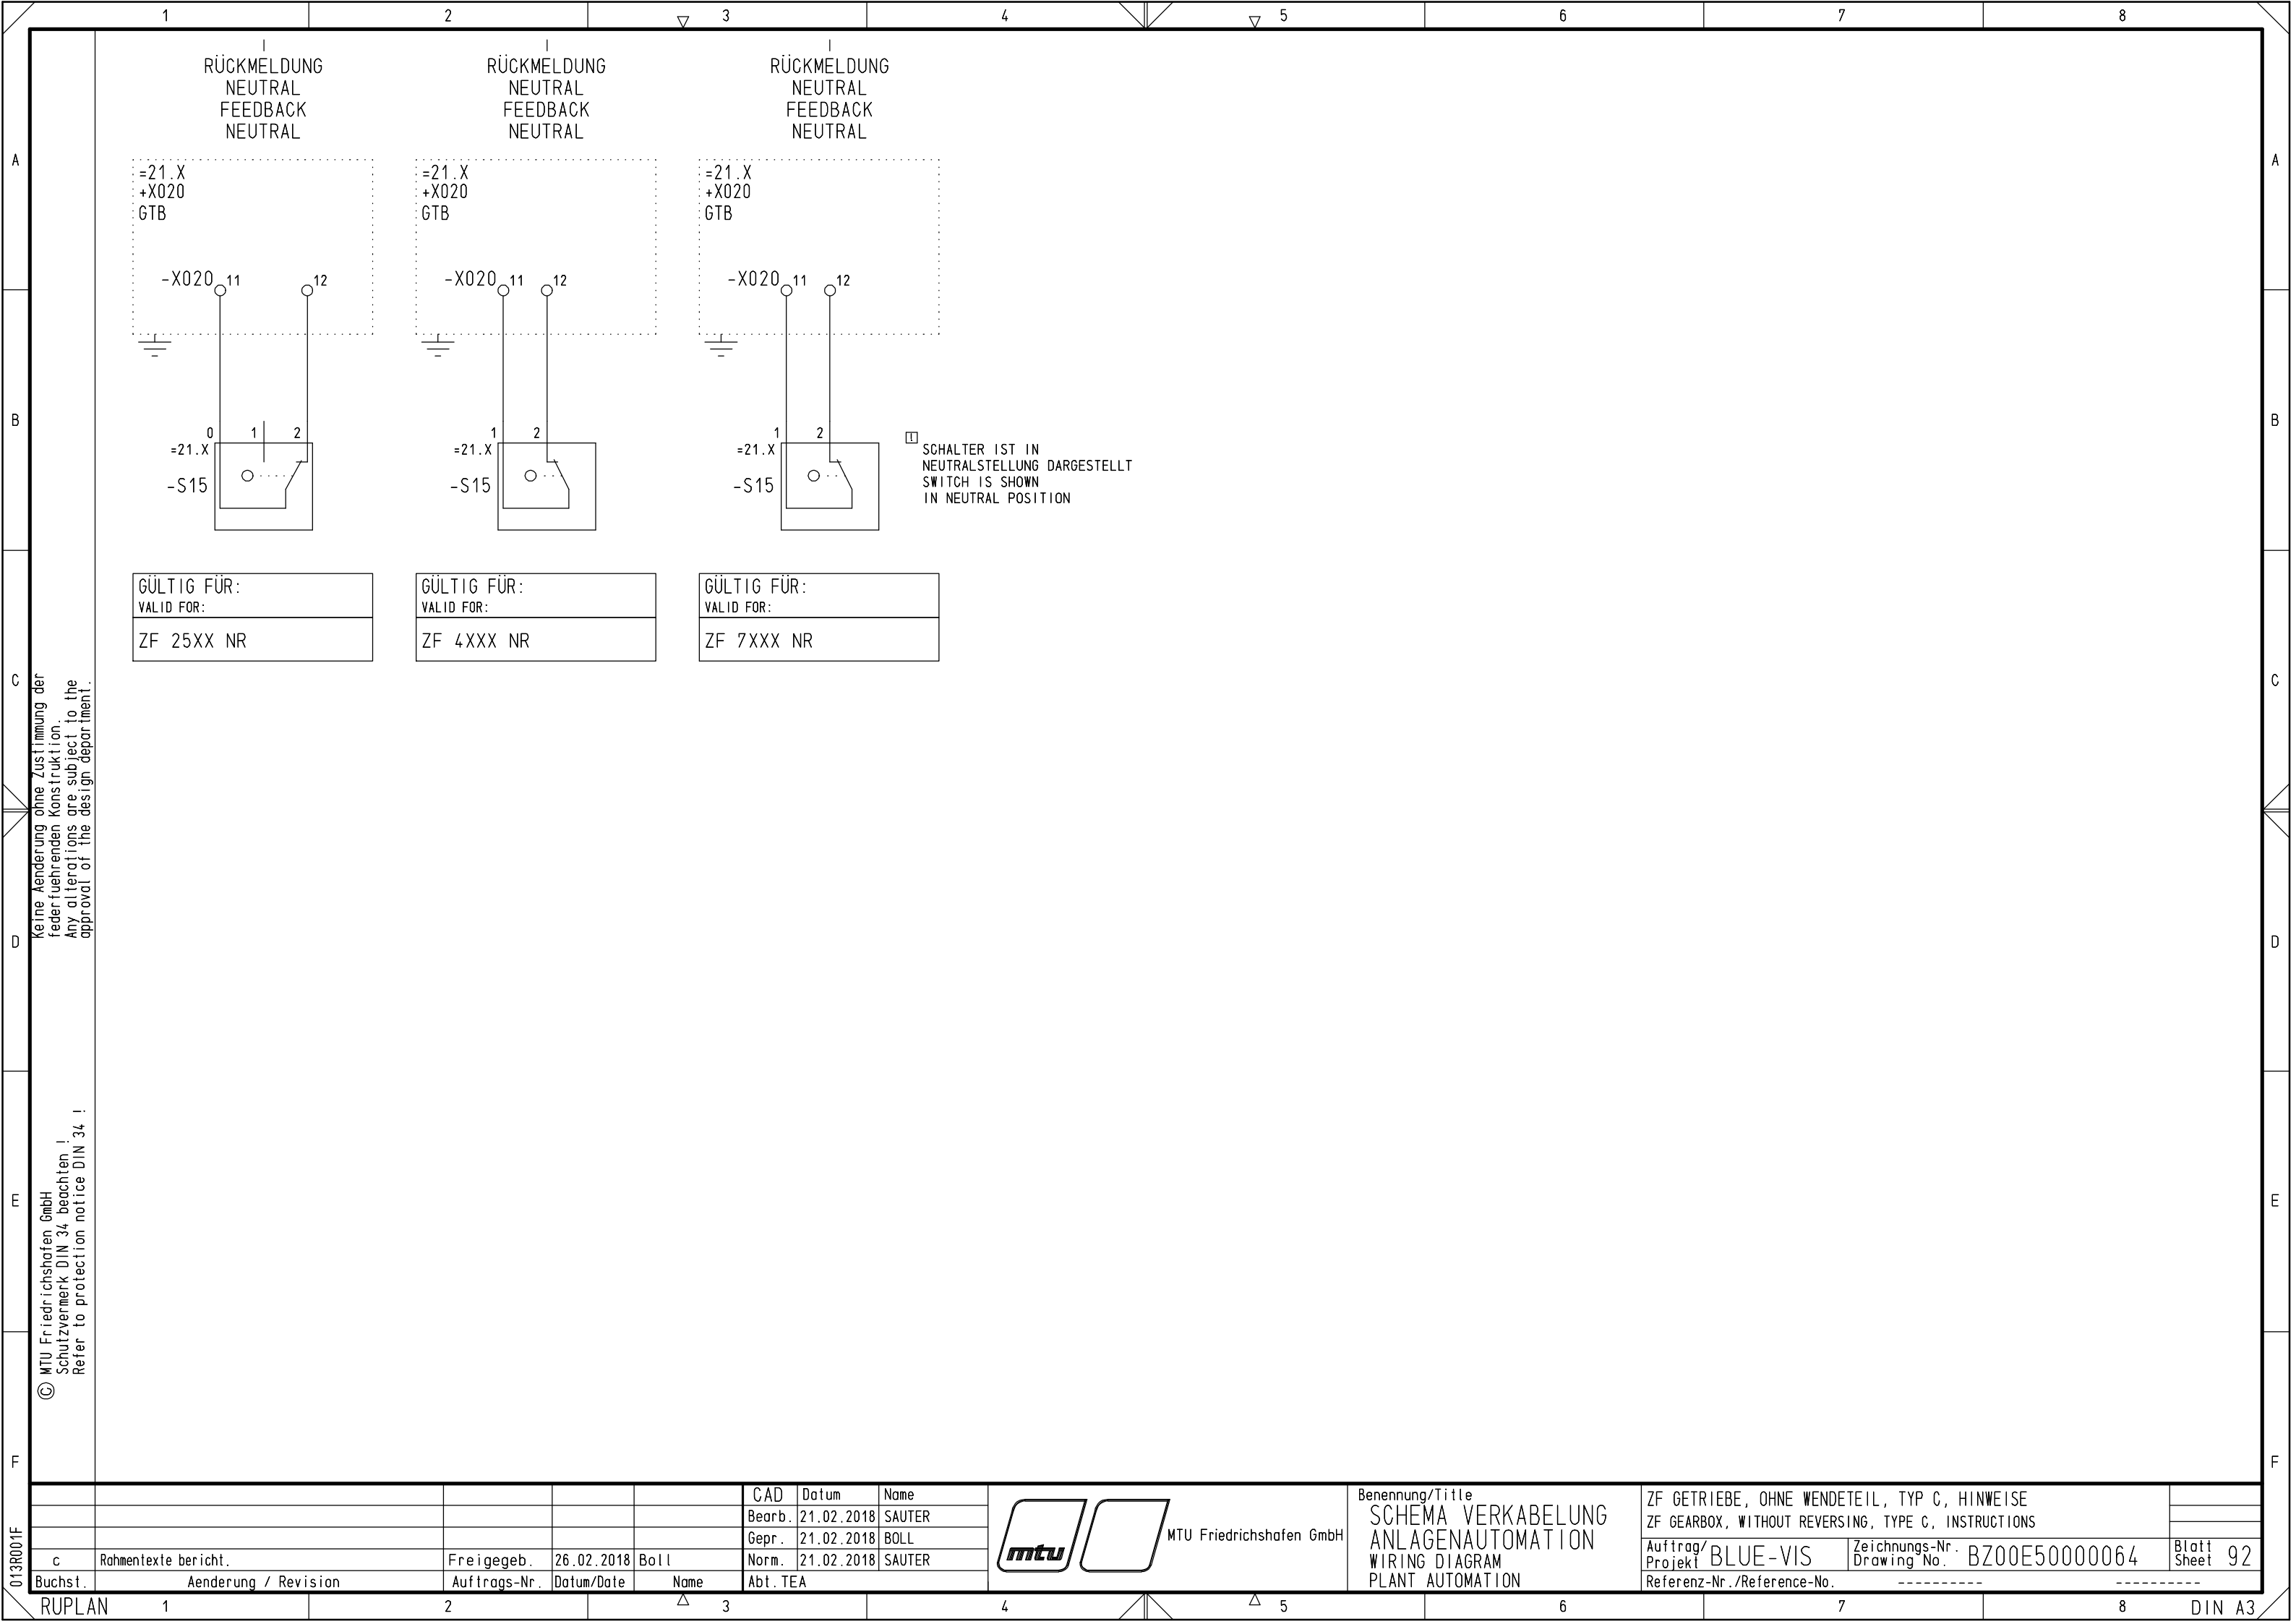

Keine Änderung ohne Zustimmung der
federführenden Konstruktion.
Any alterations are subject to the
approval of the design department.

© MTU Friedrichshafen GmbH
Schutzvermerk DIN 34 beachten !
Refer to protection notice DIN 34 !


					CAD	Datum	Name
					Bearb.	21.02.2018	SAUTER
					Gepr.	21.02.2018	BOLL
					Norm.	21.02.2018	SAUTER
c	Rahmentexte bericht.	Freigegeb.	26.02.2018	Boll	Abt. TEA		
Buchst.	Aenderung / Revision	Auftrags-Nr.	Datum/Date	Name			



MTU Friedrichshafen GmbH

Benennung/Title
SCHEMA VERKABELUNG
ANLAGENAUTOMATION
WIRING DIAGRAM
PLANT AUTOMATION

ZF GETRIEBE, OHNE WENDETEIL, TYP C, GRUNDUMFANG ZF GEARBOX, WITHOUT REVERSING, TYPE C, BASIC SCOPE			Blatt Sheet 93
Auftrag/ Projekt	BLUE-VIS	Zeichnungs-Nr. Drawing No.	
Referenz-Nr./Reference-No.		BZ00E50000064	

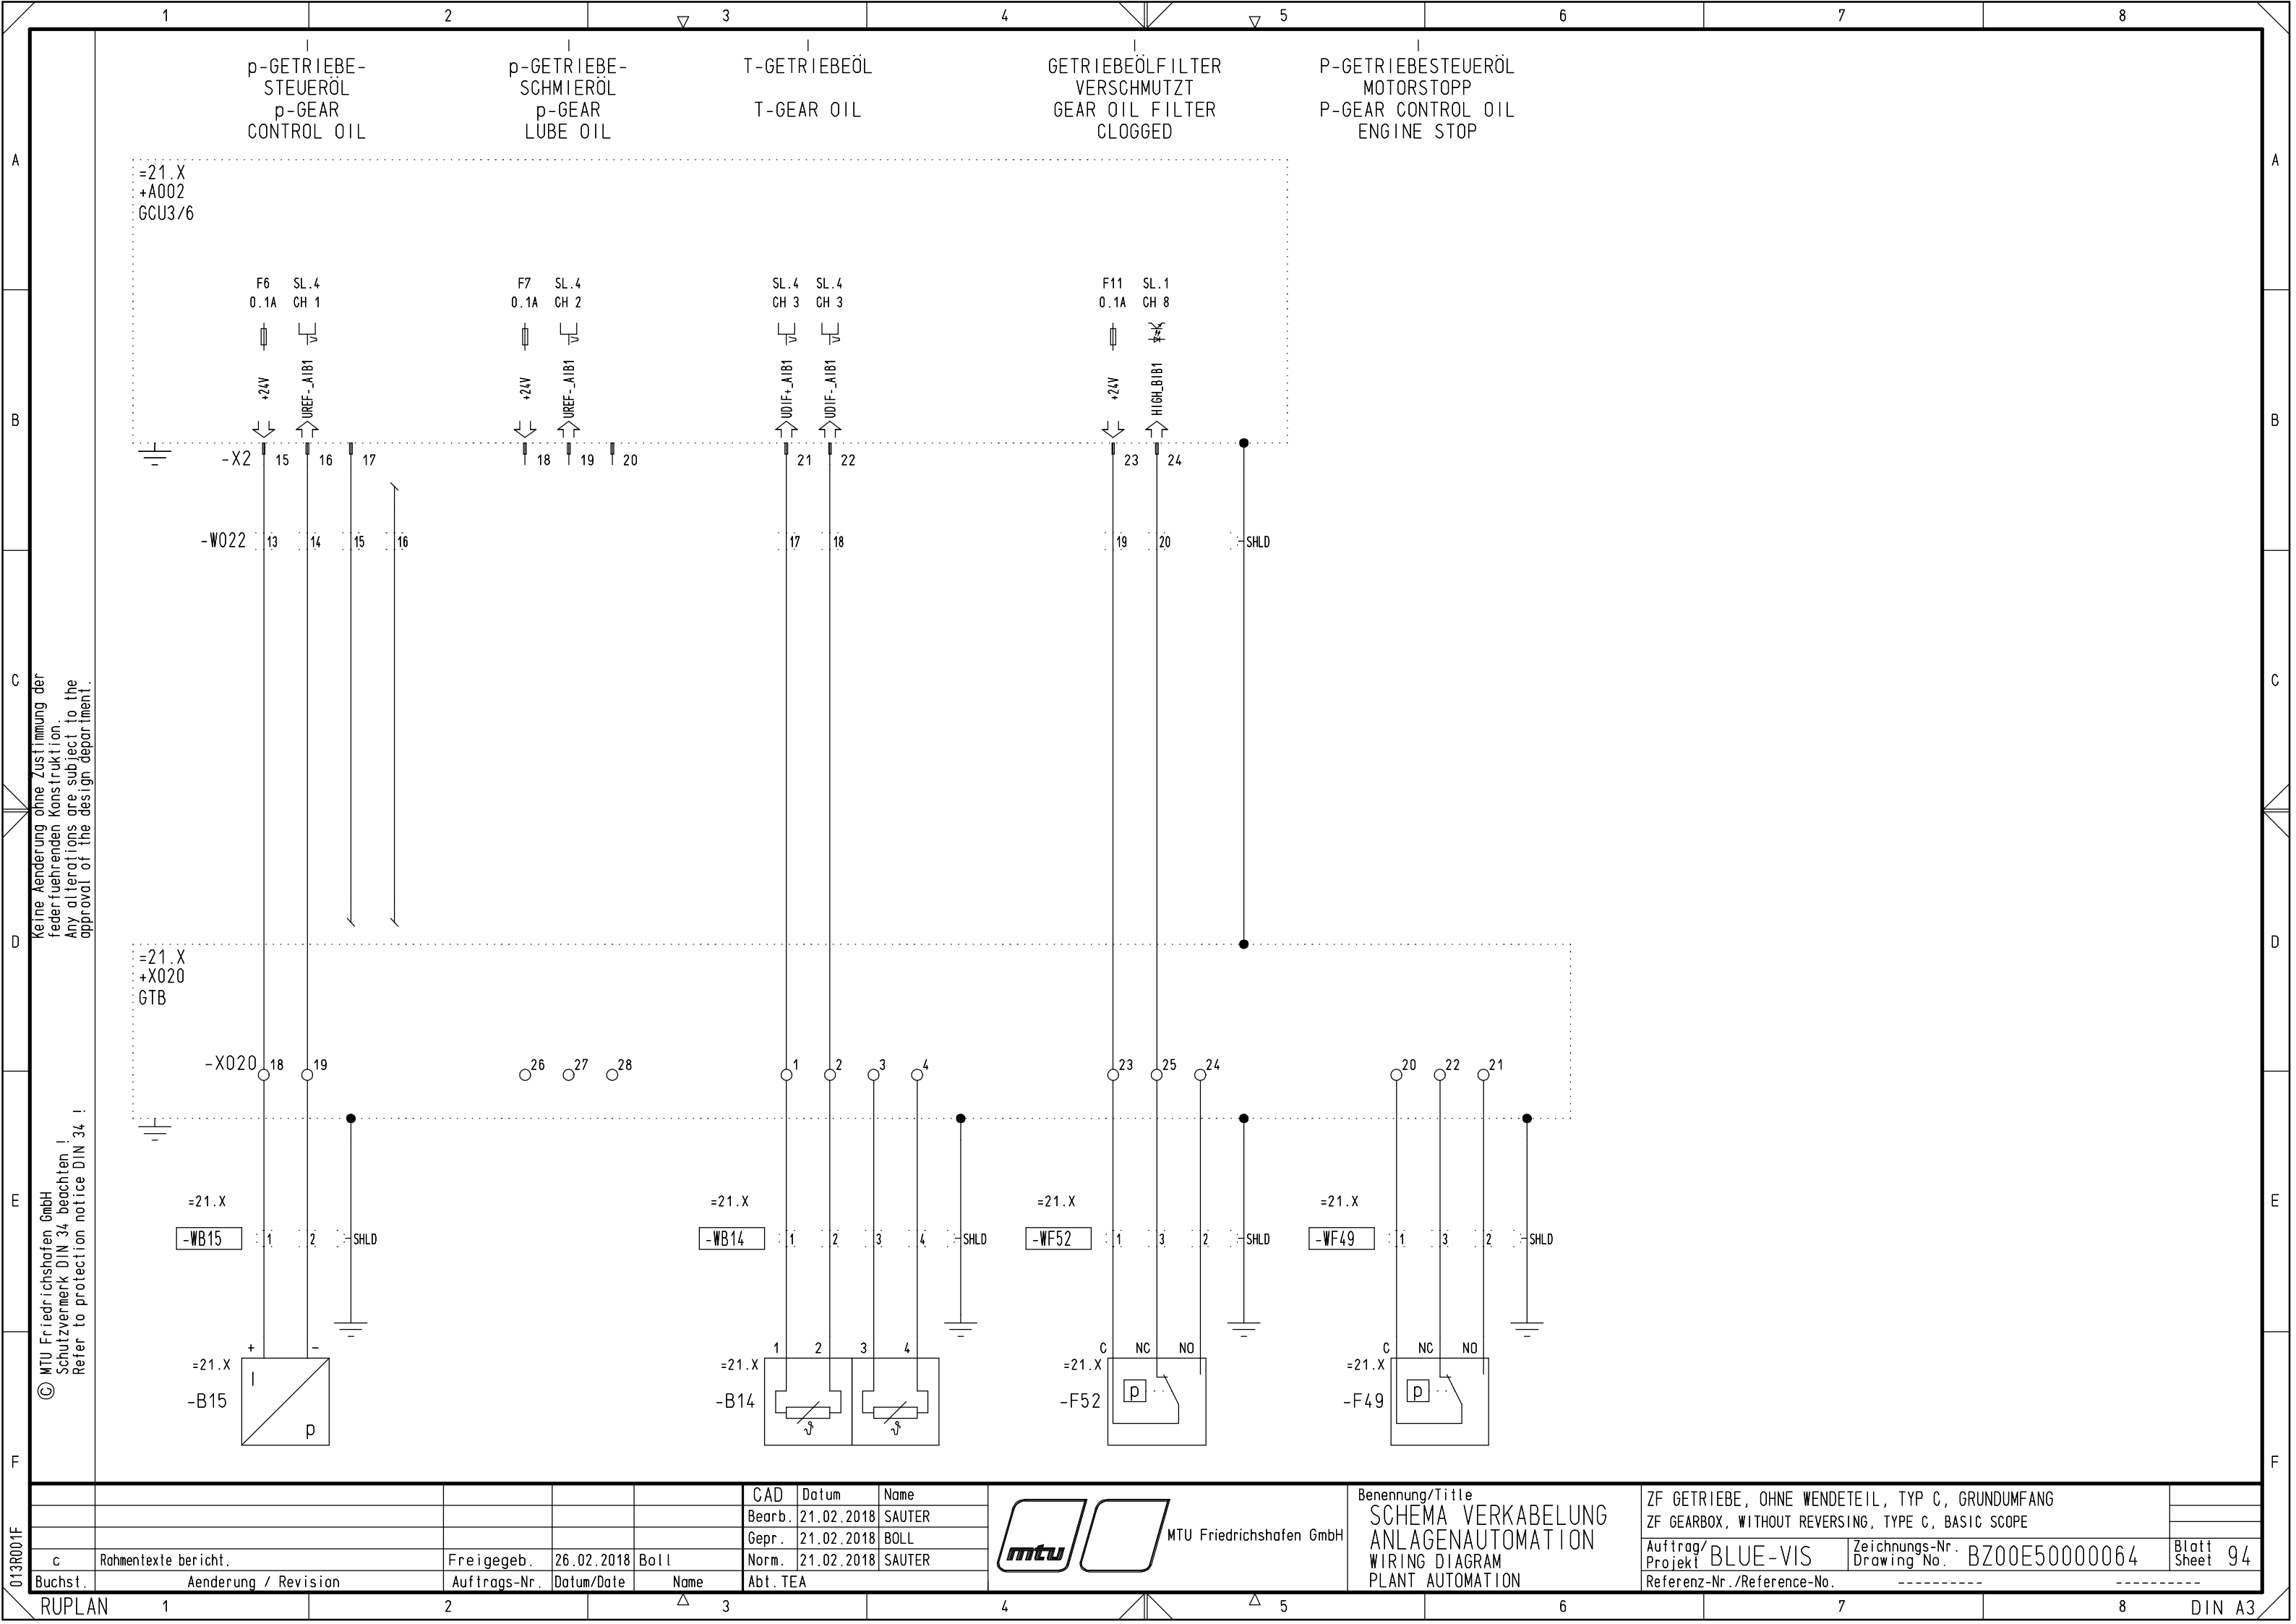

					CAD	Datum	Name	 MTU Friedrichshafen GmbH	Benennung/Title SCHEMA VERKABELUNG ANLAGENAUTOMATION WIRING DIAGRAM PLANT AUTOMATION	ZF GETRIEBE, OHNE WENDETEIL, TYP C, GRUNDUMFANG ZF GEARBOX, WITHOUT REVERSING, TYPE C, BASIC SCOPE					
					Bearb.	21.02.2018	SAUTER								
					Gepr.	21.02.2018	BOLL								
					Norm.	21.02.2018	SAUTER								
c	Rahmentexte bericht.	Freigegeb.	26.02.2018	Boll						Auftrag/ Projekt	BLUE-VIS	Zeichnungs-Nr. Drawing No.	BZ00E50000064	Blatt Sheet	94
Buchst.	Aenderung / Revision	Auftrags-Nr.	Datum/Date	Name	Abt. TEA					Referenz-Nr./Reference-No.		-----			

Keine Änderung ohne Zustimmung der
federführenden Konstruktion.
Any alterations are subject to the
approval of the design department.

© MTU Friedrichshafen GmbH
Schutzvermerk DIN 34 beachten !
Refer to protection notice DIN 34 !

					CAD	Datum	Name
					Bearb.	21.02.2018	SAUTER
					Gepr.	21.02.2018	BOLL
					Norm.	21.02.2018	SAUTER
c	Rahmentexte bericht.	Freigegeb.	26.02.2018	Boll	Abt. TEA		
Buchst.	Aenderung / Revision	Auftrags-Nr.	Datum/Date	Name			



MTU Friedrichshafen GmbH

Benennung/Title
SCHEMA VERKABELUNG
ANLAGENAUTOMATION
WIRING DIAGRAM
PLANT AUTOMATION

ZF GETRIEBE, OHNE WENDETEIL, TYP C, ERWEIT. UMFANG
ZF GEARBOX, WITHOUT REVERSING, TYPE C, EXTENTED SCOPE


Auftrag/Projekt BLUE-VIS
Zeichnungs-Nr. BZ00E50000064
Drawing No.

Referenz-Nr./Reference-No. -----


Blatt
Sheet 95

Keine Änderung ohne Zustimmung der
federführenden Konstruktion.
Any alterations are subject to the
approval of the design department.

© MTU Friedrichshafen GmbH
Schutzvermerk DIN 34 beachten !
Refer to protection notice DIN 34 !

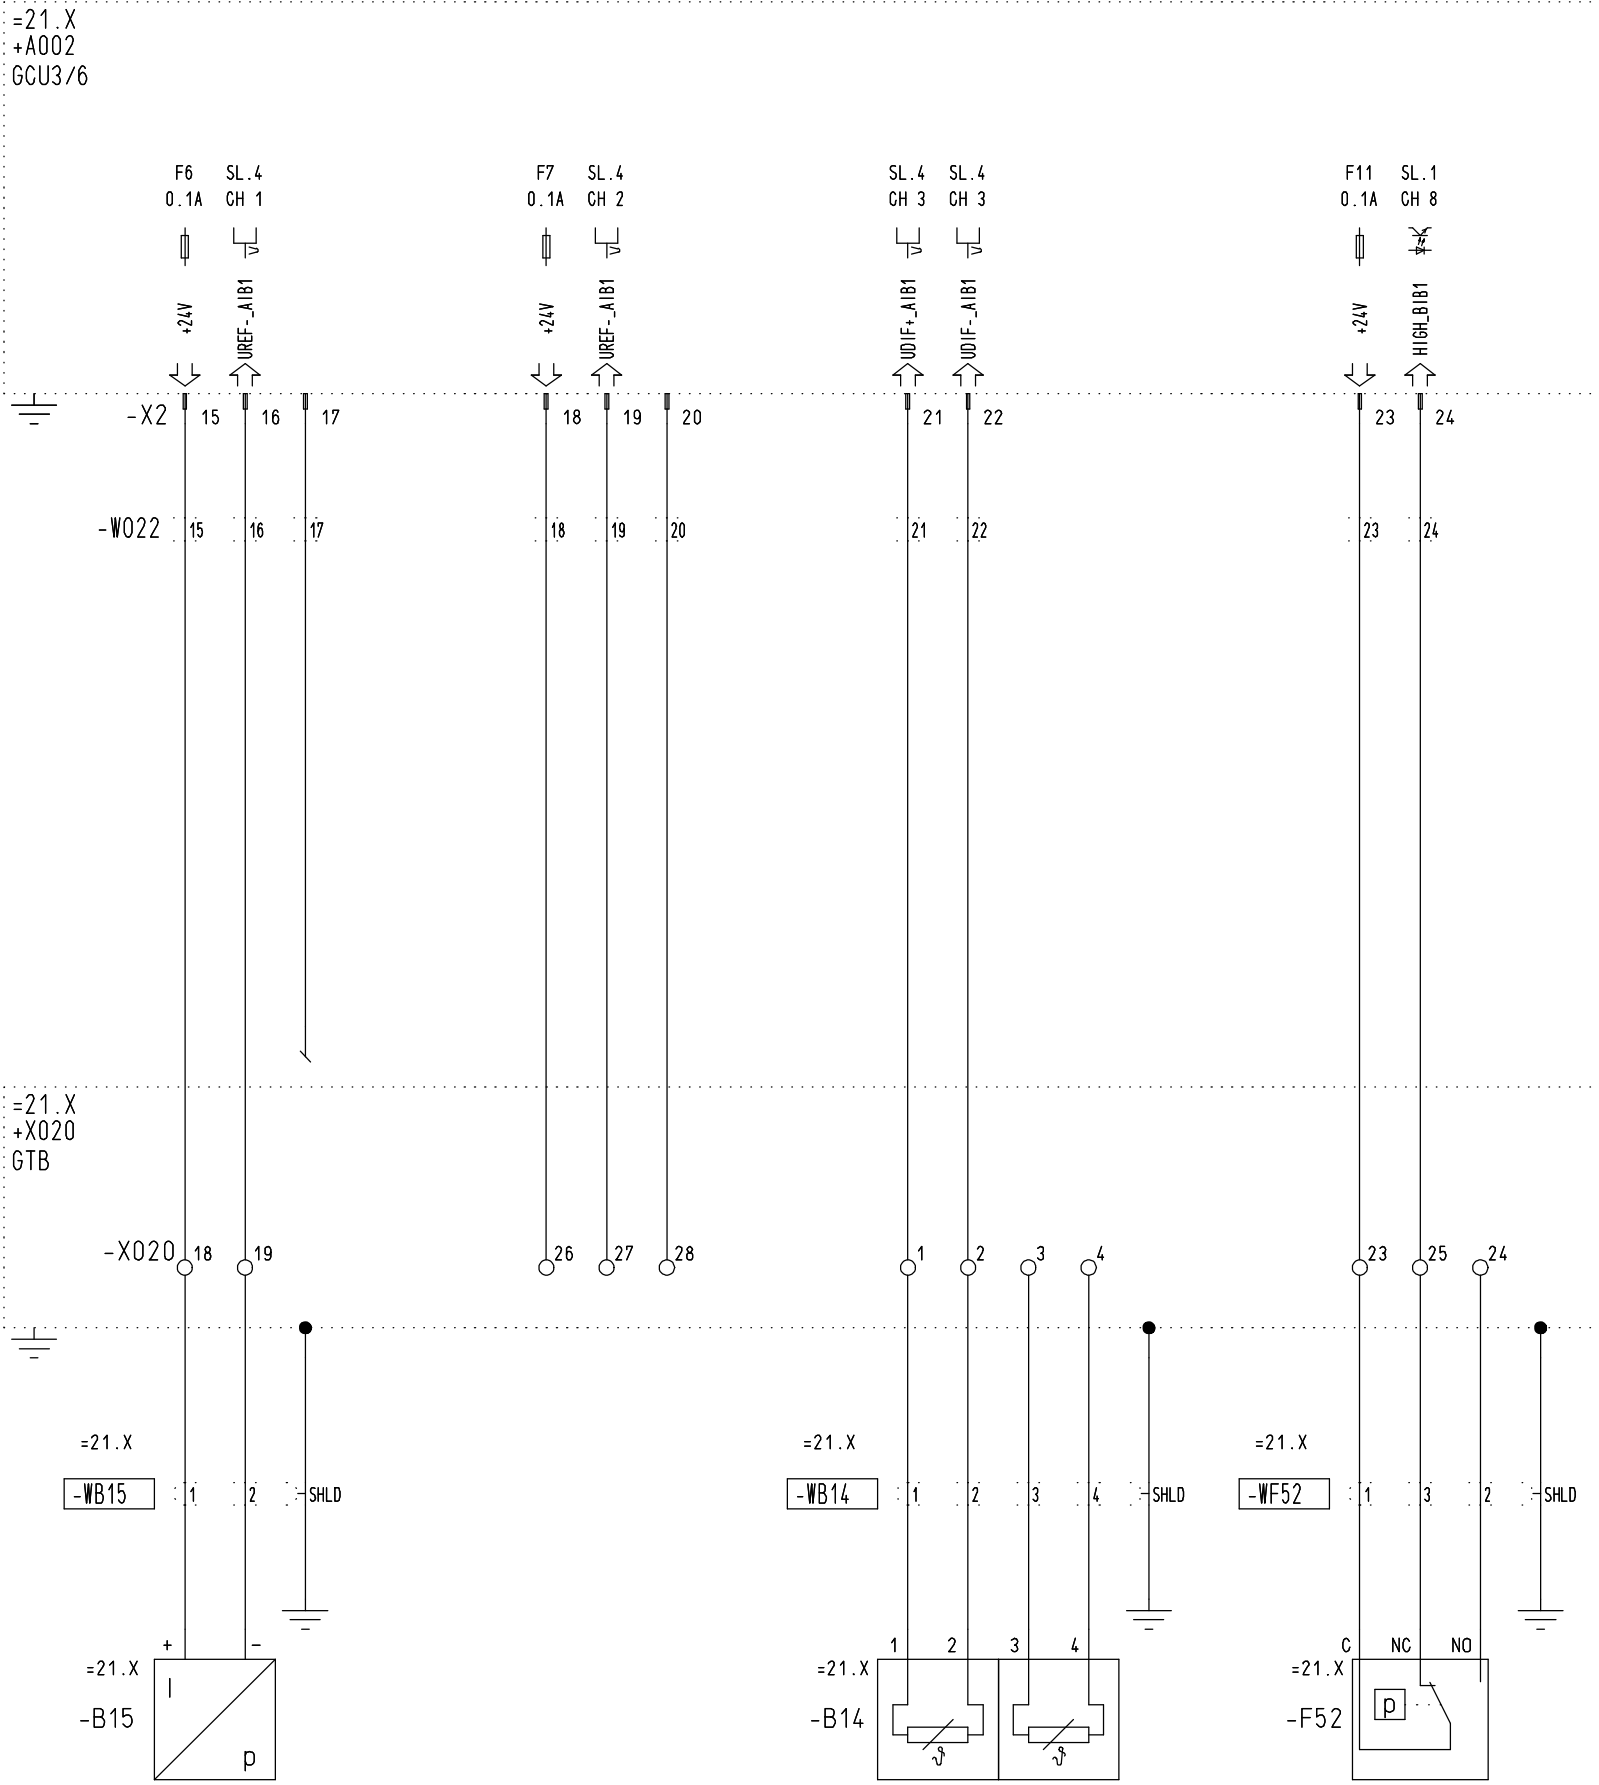


					CAD	Datum	Name	 MTU Friedrichshafen GmbH	Benennung/Title SCHEMA VERKABELUNG ANLAGENAUTOMATION WIRING DIAGRAM PLANT AUTOMATION	ZF GETRIEBE, OHNE WENDETEIL, TYP C, ERWEIT. UMFANG			
					Bearb.	21.02.2018	SAUTER			ZF GEARBOX, WITHOUT REVERSING, TYPE C, EXTENDED SCOPE			
					Gepr.	21.02.2018	BOLL						
					Norm.	21.02.2018	SAUTER						
c	Rahmentexte bericht.	Freigegeb.	26.02.2018	Boll						Auftrag/Projekt		Zeichnungs-Nr. Drawing No.	Blatt Sheet
Buchst.	Aenderung / Revision	Auftrags-Nr.	Datum/Date	Name	Abt. TEA					BLUE-VIS		BZ00E50000064	96
										Referenz-Nr./Reference-No.			

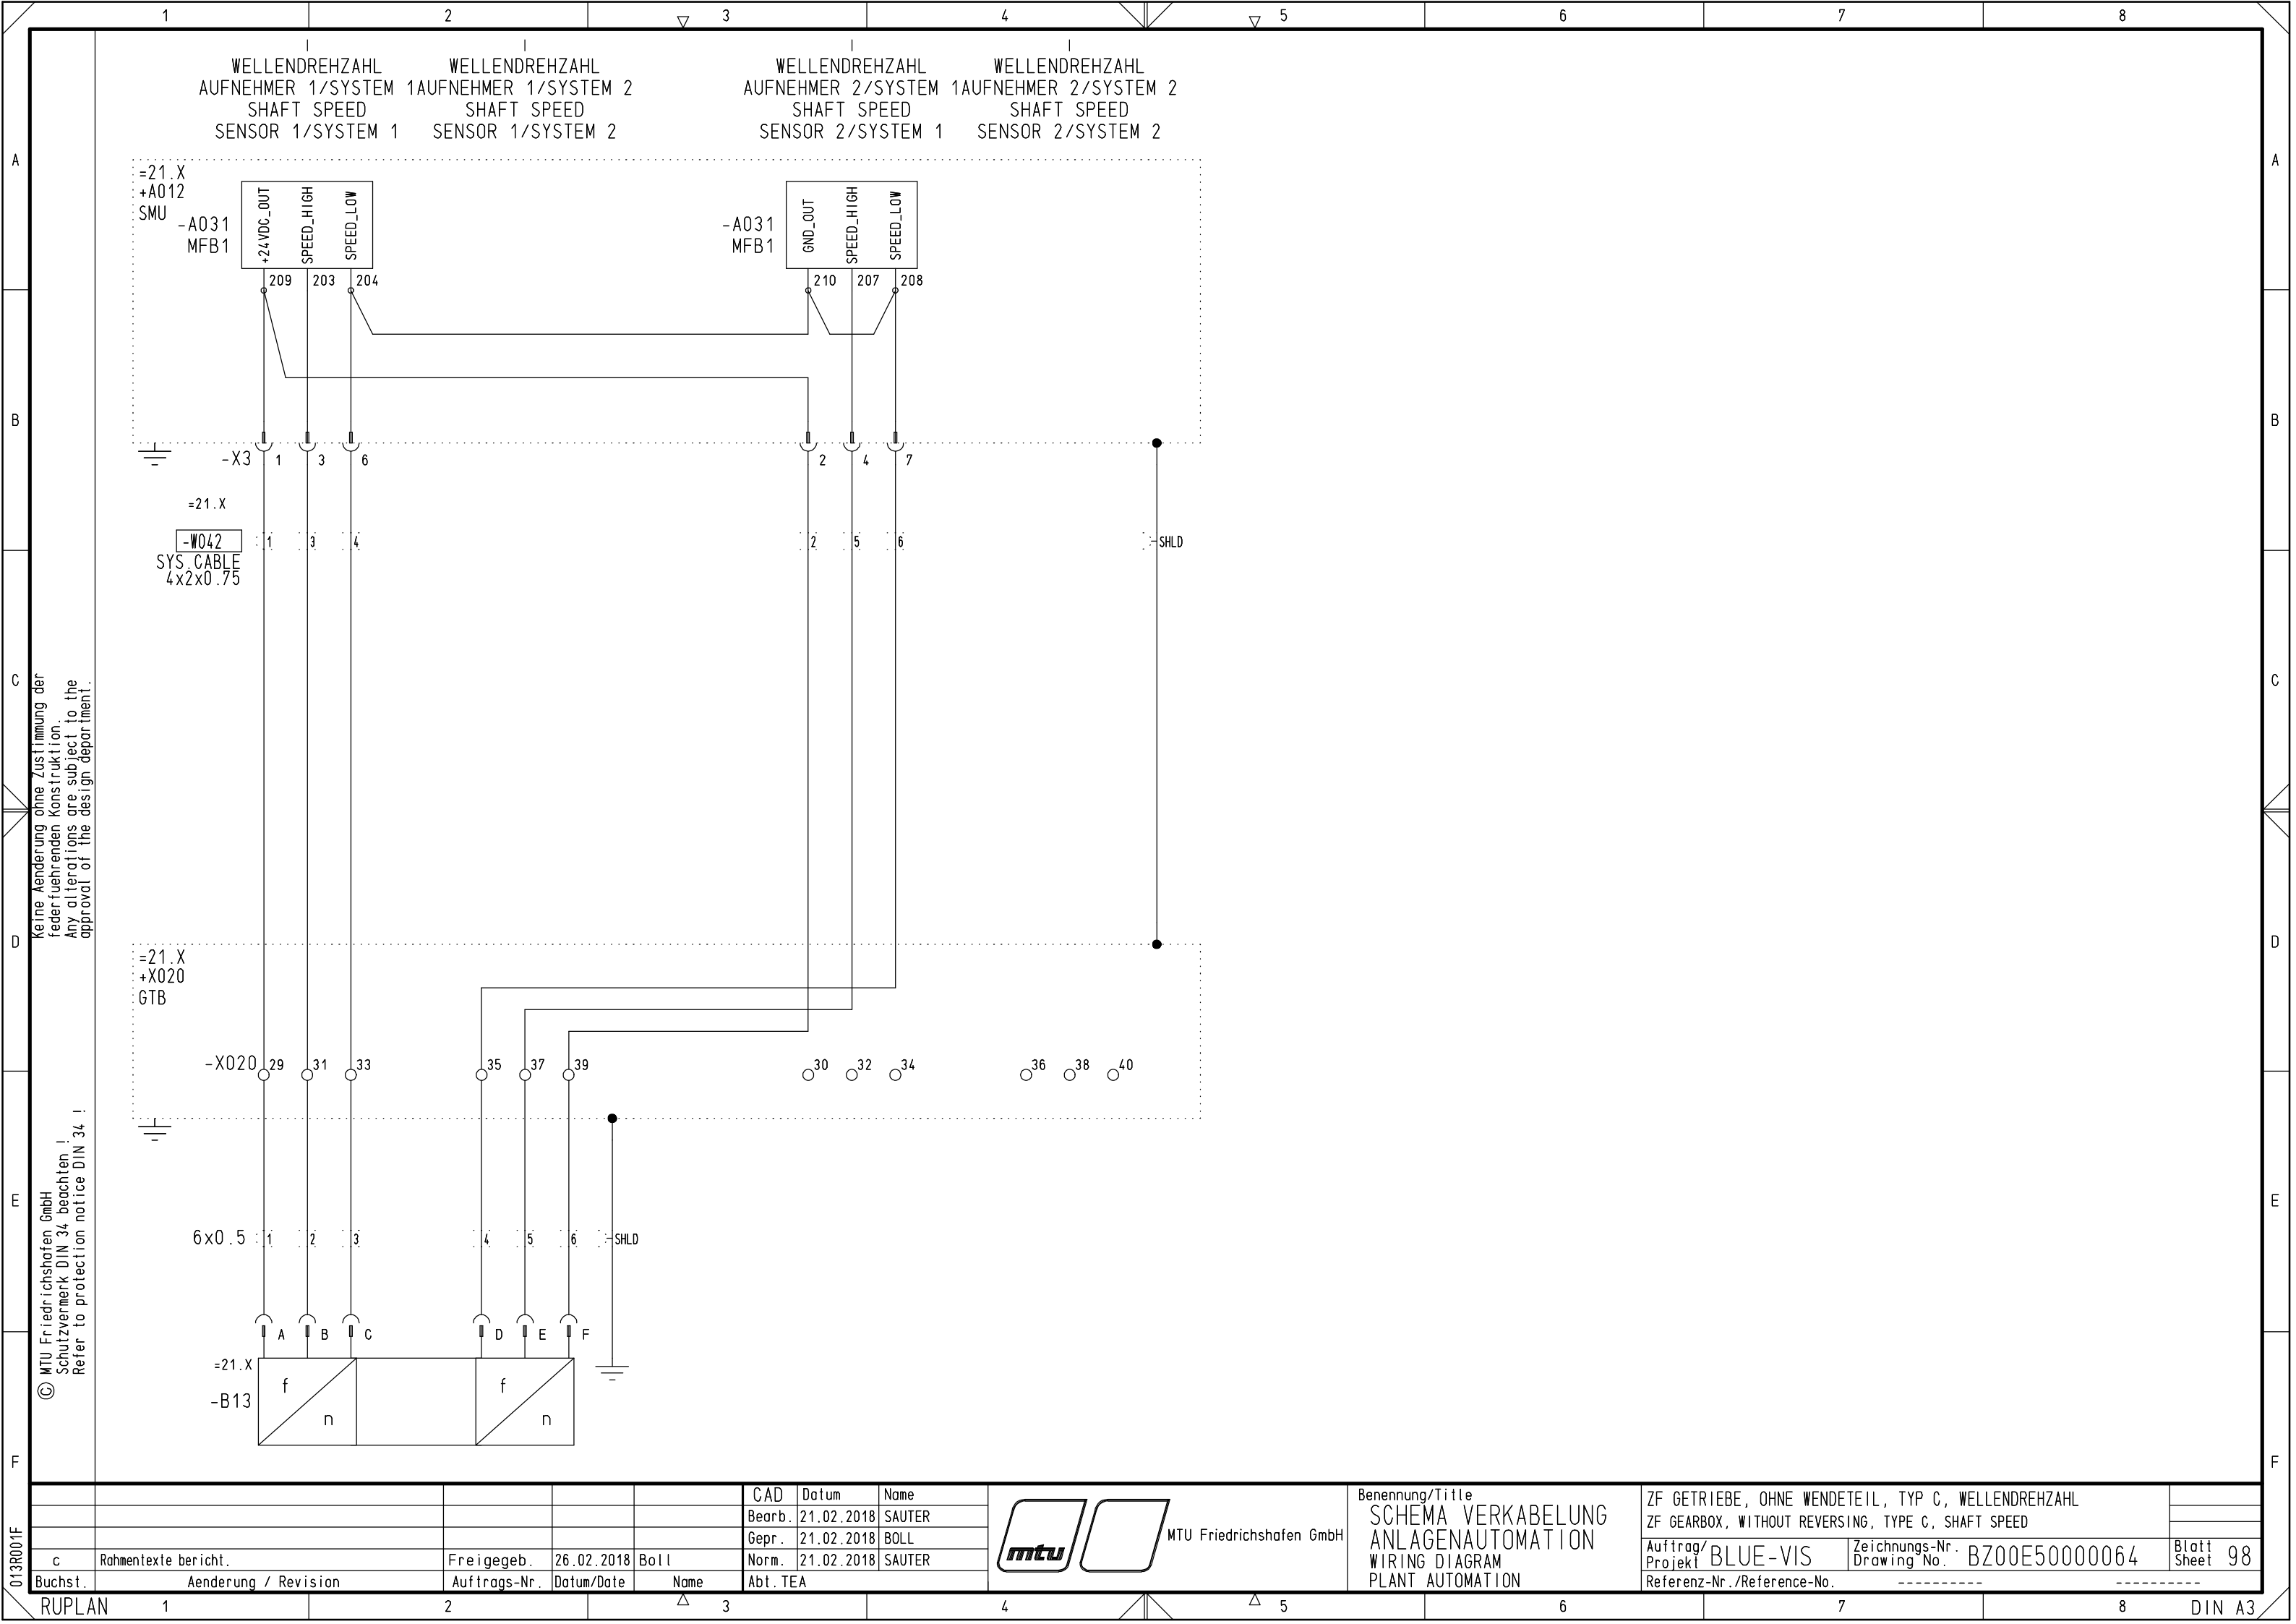

	1	2	3	4	5	6	7	8
A								
B								
C								
D								
E								
F								
	GÜLTIG FÜR: VALID FOR: ZF 2000 ZF 2000A ZF 2000V ZF 2050 ZF 2050A ZF 2050V ZF 2060 ZF 2060A ZF 2060V ZF 2150 ZF 2150A ZF 2150V ZF 2250 ZF 2250A ZF 2250V							
	MTU Friedrichshafen GmbH Schutzvermerk DIN 34 beachten ! Refer to protection notice DIN 34 ! MTU Friedrichshafen GmbH Benennung/Title SCHEMA VERKABELUNG ANLAGENAUTOMATION WIRING DIAGRAM PLANT AUTOMATION ZF GETRIEBE, MIT WENDETEIL, TYP D, HINWEISE ZF GEARBOX, WITH REVERSING, TYPE D, INSTRUCTIONS Auftrag/ Projekt BLUE-VIS Zeichnungs-Nr. Drawing No. BZ00E50000064 Blatt Sheet 99							
	RUPLAN 1 2 3 4 5 6 7 8 DIN A3							

Keine Änderung ohne Zustimmung der
federführenden Konstruktion.
Any alterations are subject to the
approval of the design department.

© MTU Friedrichshafen GmbH
Schutzvermerk DIN 34 beachten !
Refer to protection notice DIN 34 !

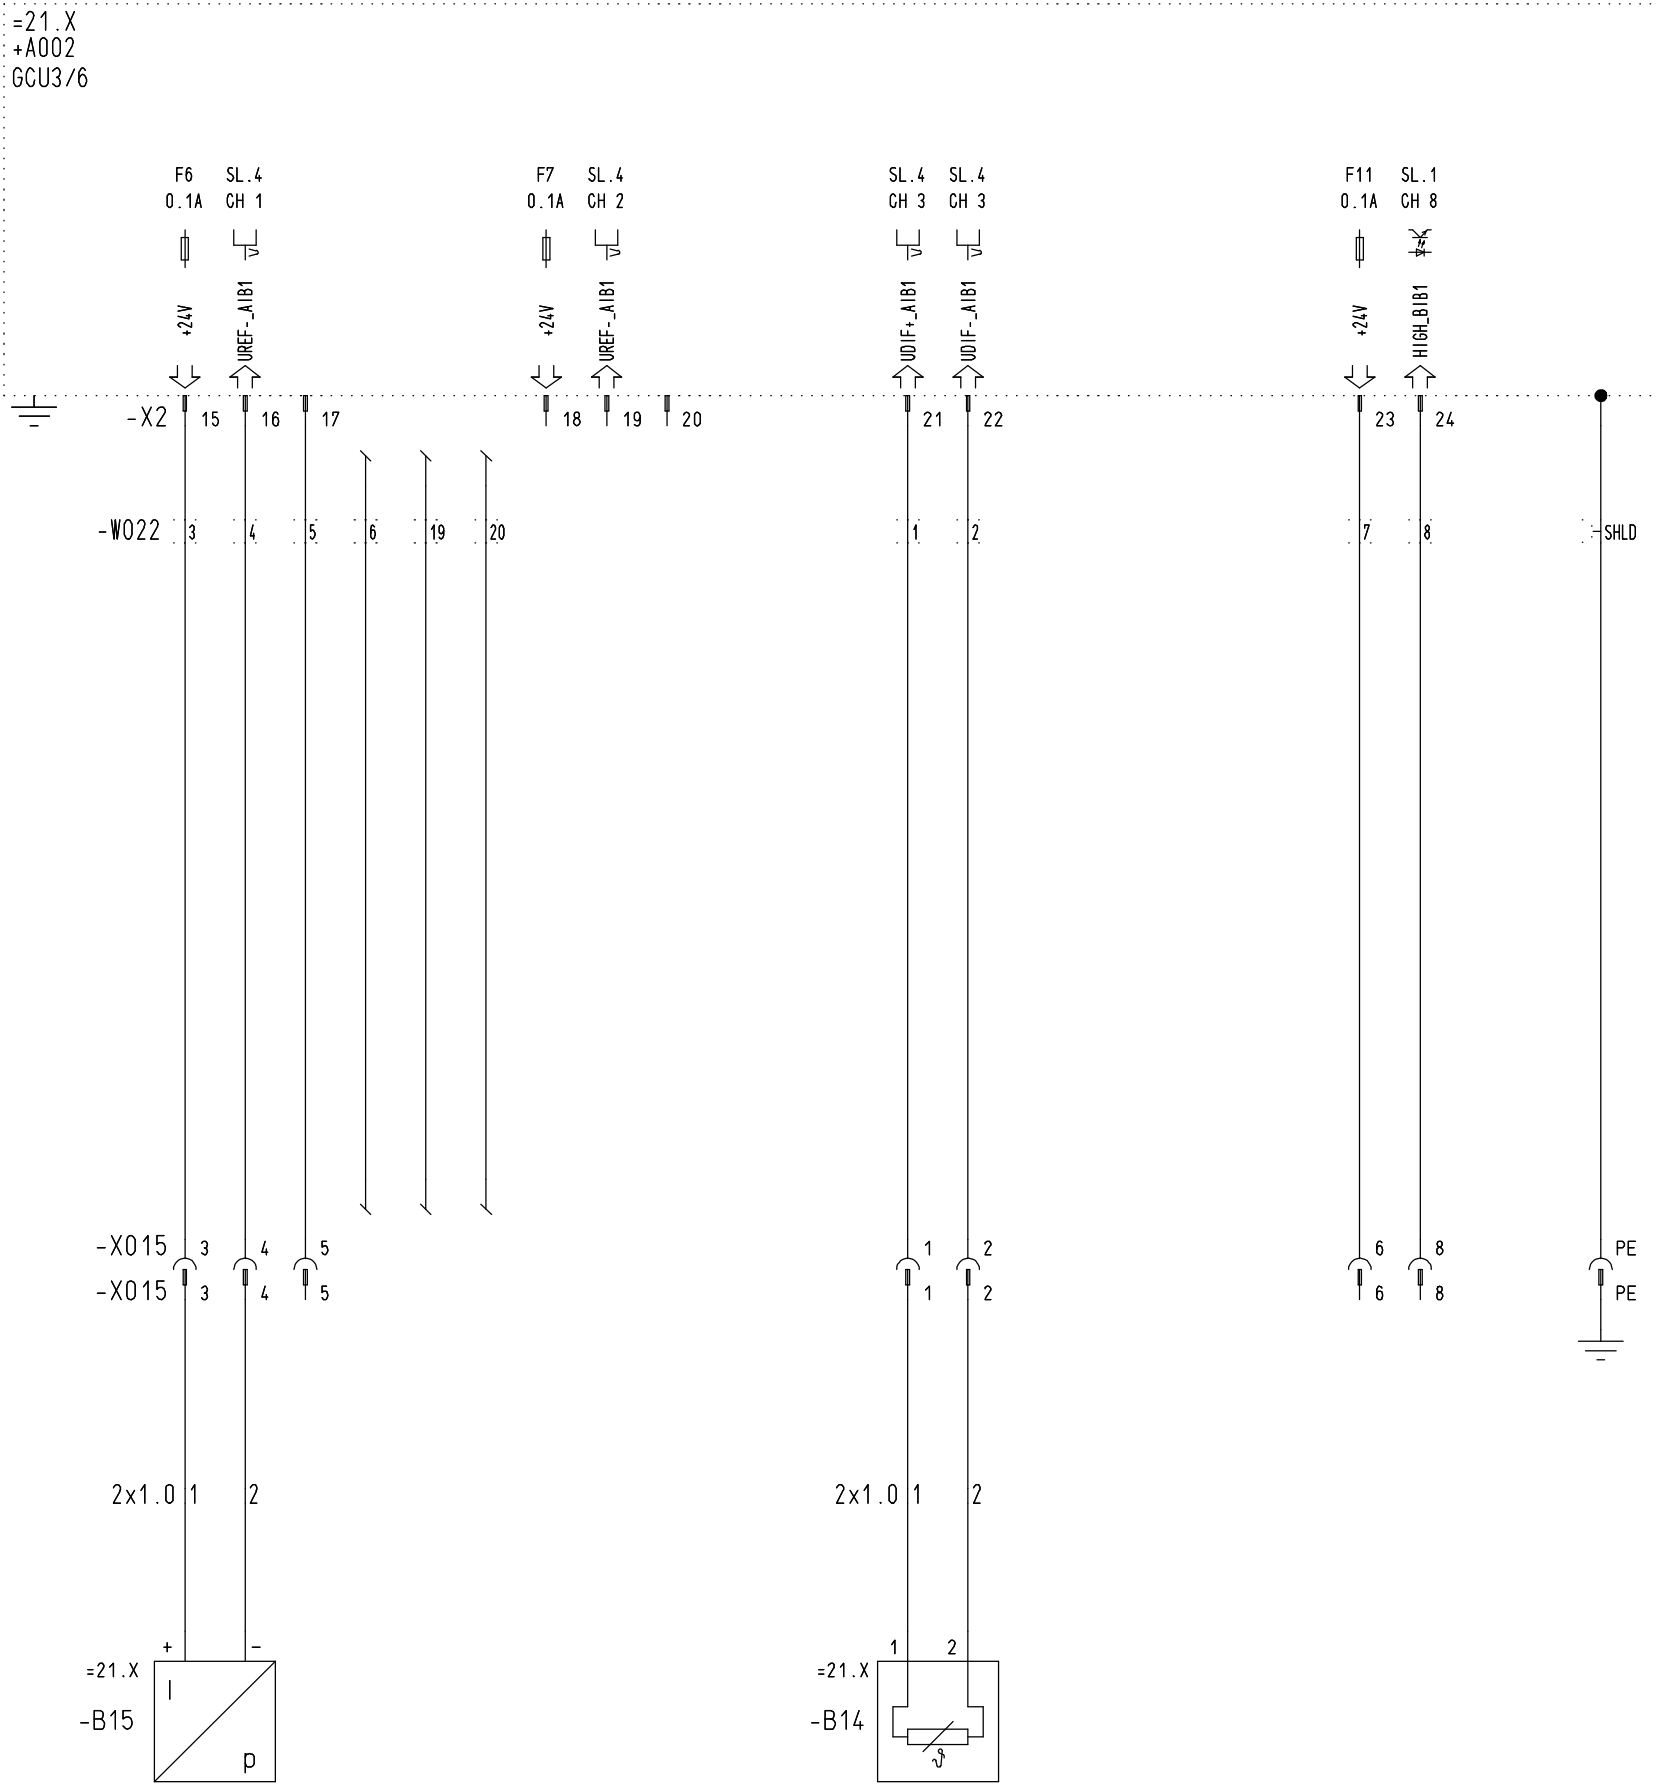

					CAD	Datum	Name	 MTU Friedrichshafen GmbH	Benennung/Title SCHEMA VERKABELUNG ANLAGENAUTOMATION WIRING DIAGRAM PLANT AUTOMATION	ZF GETRIEBE, MIT WENDETEIL, TYP D, GRUND-/ERWEIT.UMFANG			
					Bearb.	21.02.2018	SAUTER			ZF GEARBOX, WITH REVERSING, TYPE D, BASIC/EXTENDED SCOPE			
					Gepr.	21.02.2018	BOLL						
					Norm.	21.02.2018	SAUTER						
c	Rahmentexte bericht.		Freigegeb.	26.02.2018	Boll					Auftrag/ Projekt		Zeichnungs-Nr. Drawing No.	Blatt Sheet
Buchst.	Änderung / Revision		Auftrags-Nr.	Datum/Date	Name	Abt. TEA				BLUE-VIS		BZ00E50000064	101
										Referenz-Nr./Reference-No.			

	1	2	▽3	4	▽5	6	7	8																									
A	<table><tr><td colspan="2">GÜLTIG FÜR: VALID FOR:</td></tr><tr><td colspan="2">ZF 350</td></tr><tr><td colspan="2">ZF 350A</td></tr><tr><td colspan="2">ZF 350V</td></tr><tr><td colspan="2"> </td></tr><tr><td colspan="2">ZF 550</td></tr><tr><td colspan="2">ZF 550A</td></tr><tr><td colspan="2">ZF 550V</td></tr><tr><td colspan="2"> </td></tr><tr><td colspan="2">ZF 665</td></tr><tr><td colspan="2">ZF 665A</td></tr><tr><td colspan="2">ZF 665V</td></tr></table>								GÜLTIG FÜR: VALID FOR:		ZF 350		ZF 350A		ZF 350V				ZF 550		ZF 550A		ZF 550V				ZF 665		ZF 665A		ZF 665V		B
GÜLTIG FÜR: VALID FOR:																																	
ZF 350																																	
ZF 350A																																	
ZF 350V																																	
ZF 550																																	
ZF 550A																																	
ZF 550V																																	
ZF 665																																	
ZF 665A																																	
ZF 665V																																	
C	Keine Änderung ohne Zustimmung der federführenden Konstruktion. Any alterations are subject to the approval of the design department.								C																								
D									D																								
E	© MTU Friedrichshafen GmbH Schutzvermerk DIN 34 beachten ! Refer to protection notice DIN 34 !								E																								
F									F																								
013R00IF																																	
c	Rahmentexte bericht.	Freigegeb.	26.02.2018	Boll	Norm.	21.02.2018	SAUTER																										
Buchst.	Aenderung / Revision	Auftrags-Nr.	Datum/Date	Name	Abt. TEA																												
					CAD	Datum	Name																										
					Bearb.	21.02.2018	SAUTER																										
					Gepr.	21.02.2018	BOLL																										
					Norm.	21.02.2018	SAUTER																										
							Benennung/Title SCHEMA VERKABELUNG ANLAGENAUTOMATION WIRING DIAGRAM PLANT AUTOMATION																										
					Zf GETRIEBE, MIT WENDETEIL, TYP E(Gr.1), HINWEISE ZF GEARBOX, WITH REVERSING, TYPE E(Gr.1), INSTRUCTIONS		Auftrag/ Projekt BLUE-VIS Zeichnungs-Nr. Drawing No. BZ00E50000064 Referenz-Nr./Reference-No. -----																										
							Blatt Sheet 102																										
RUPLAN	1	2	△3	4	△5	6	7	8 DIN A3																									

Keine Änderung ohne Zustimmung der
federführenden Konstruktion.
Any alterations are subject to the
approval of the design department.

© MTU Friedrichshafen GmbH
Schutzvermerk DIN 34 beachten !
Refer to protection notice DIN 34 !


					CAD	Datum	Name
					Bearb.	21.02.2018	SAUTER
					Gedr.	21.02.2018	BOLL
					Norm.	21.02.2018	SAUTER
c	Rahmentexte bericht.	Freigegeb.	26.02.2018	Boll	Abt. TEA		
Buchst.	Aenderung / Revision	Auftrags-Nr.	Datum/Date	Name			




MTU Friedrichshafen GmbH

Benennung/Title
SCHEMA VERKABELUNG
ANLAGENAUTOMATION
WIRING DIAGRAM
PLANT AUTOMATION


ZF GETRIEBE, MIT WENDETEIL, TYP E(GR.1),GRUND-/ERWEIT.UMFANG		
ZF GEARBOX, WITH REVERSING, TYPE E(GR.1),BASIC/EXTENT. SCOPE		
Auftrag/ Projekt	BLUE-VIS	Zeichnungs-Nr. Drawing No.
Referenz-Nr./Reference-No.		
BZ00E50000064		Blatt Sheet
		103

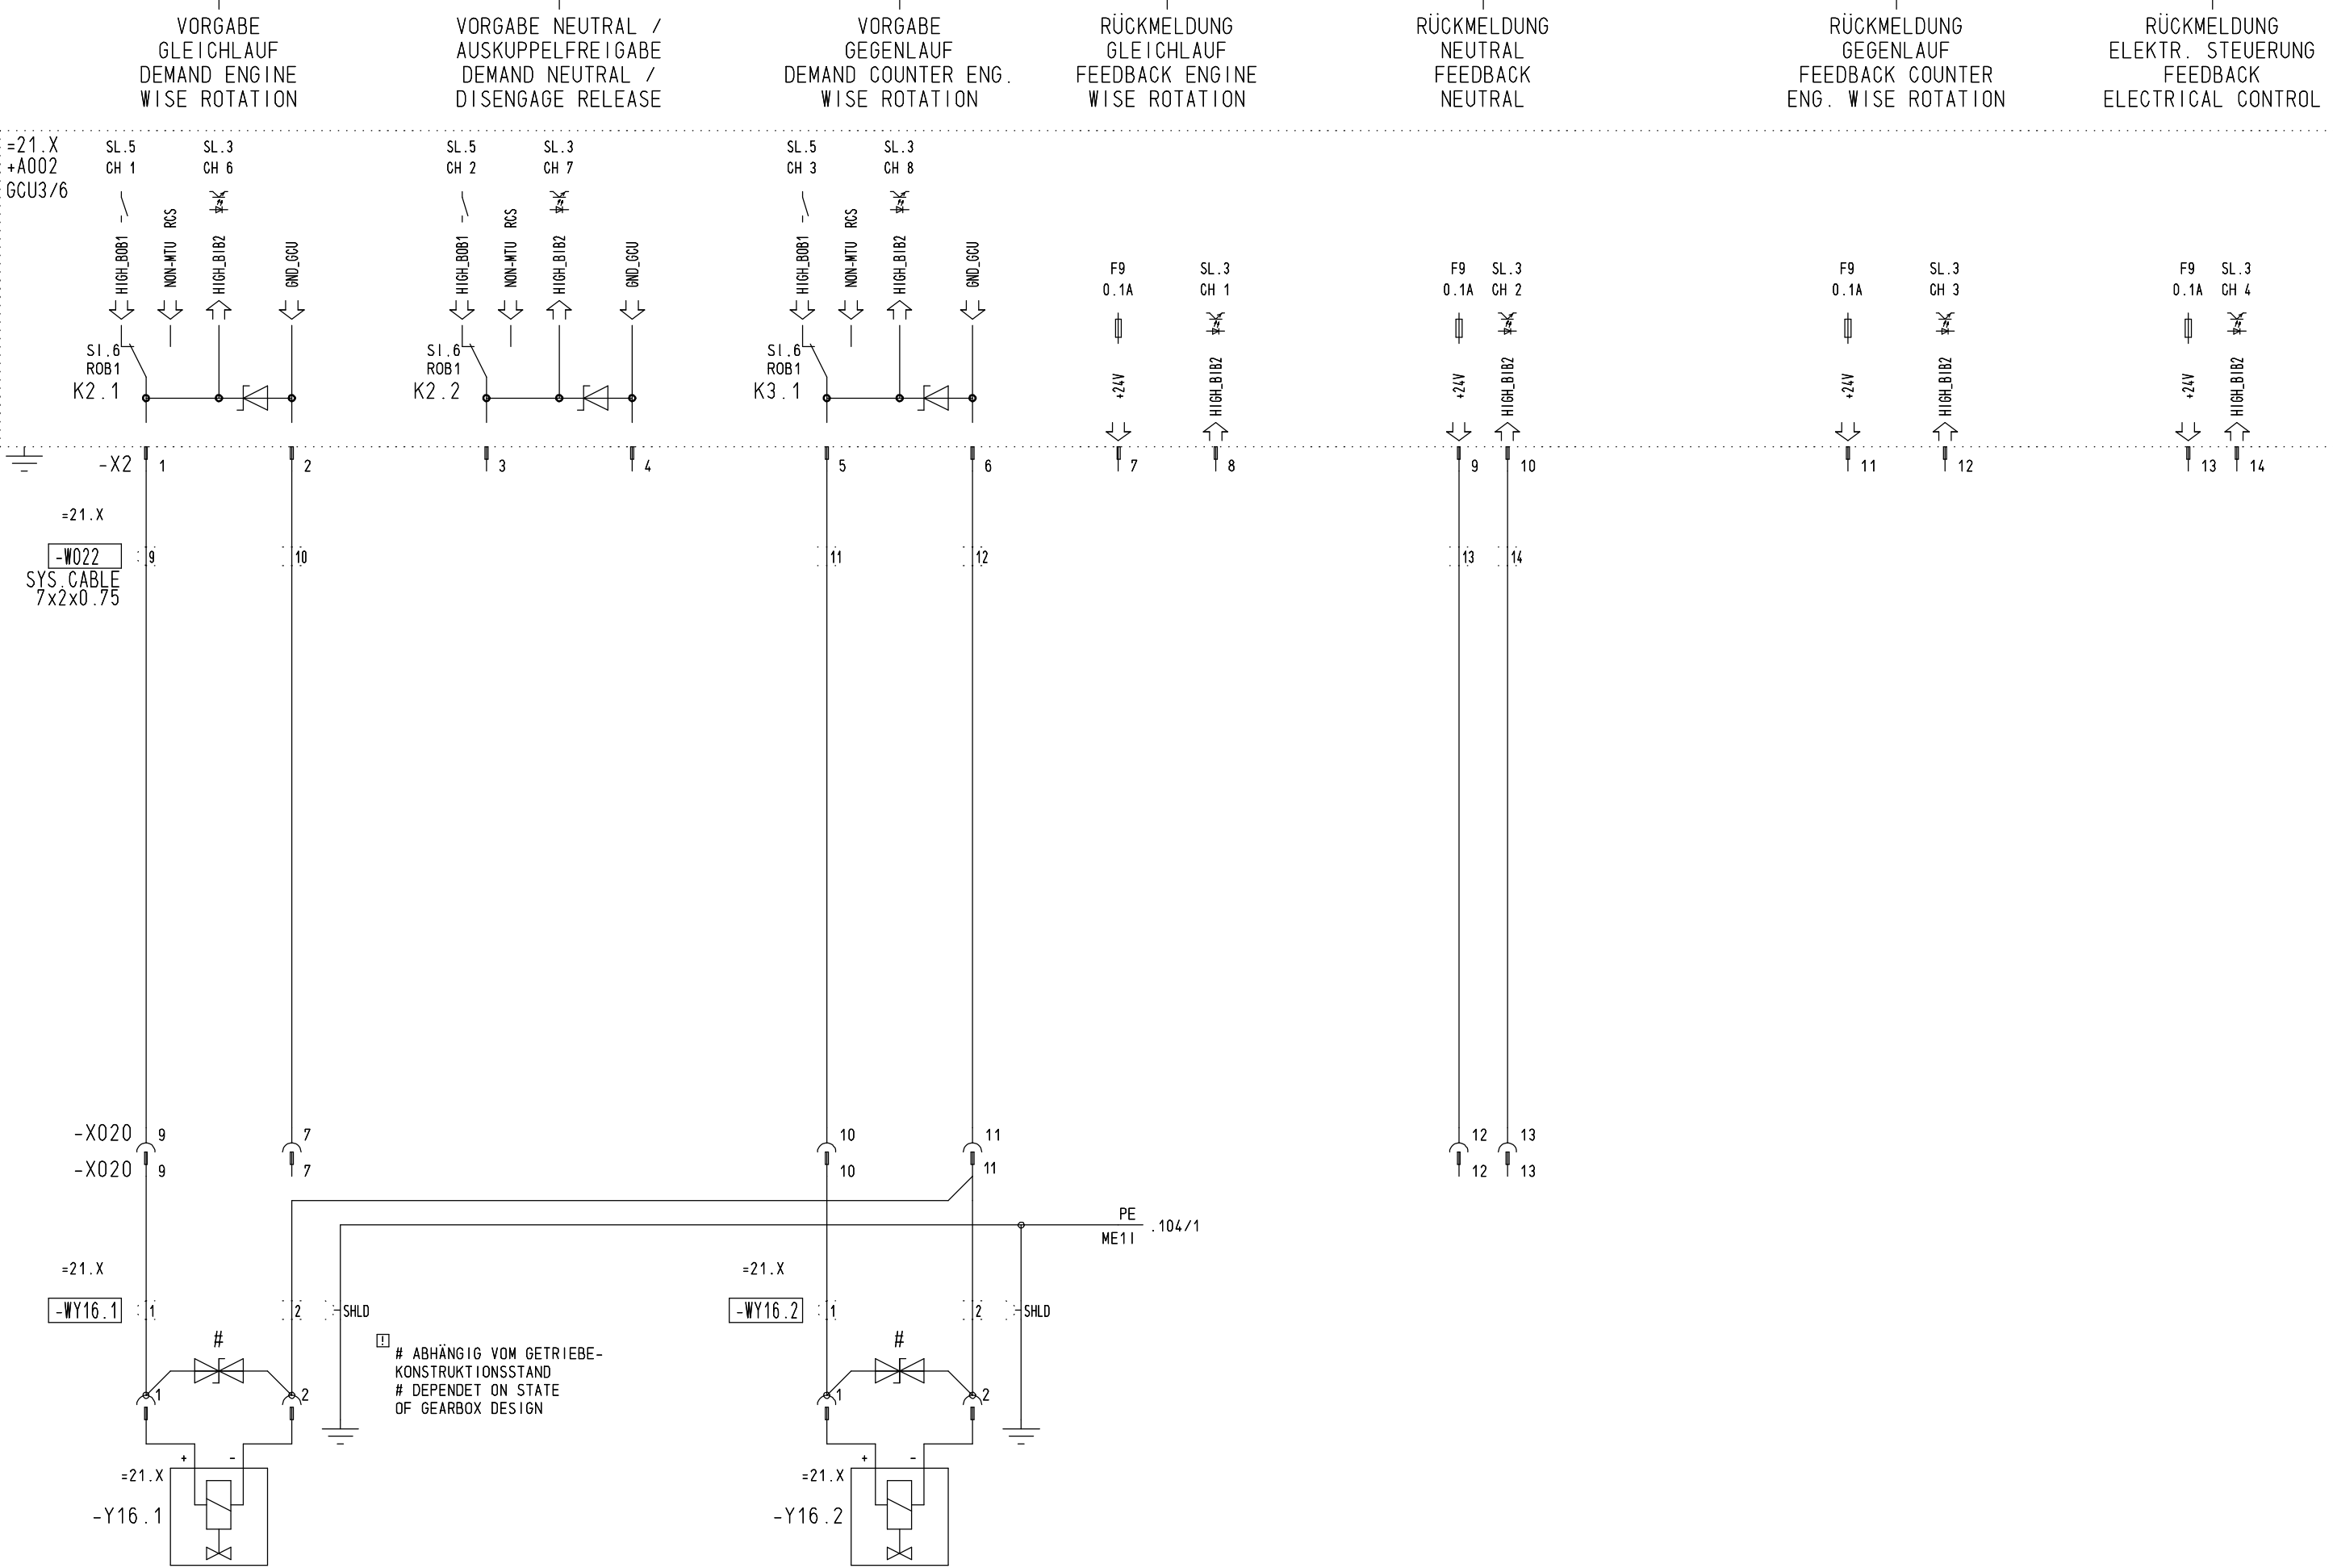

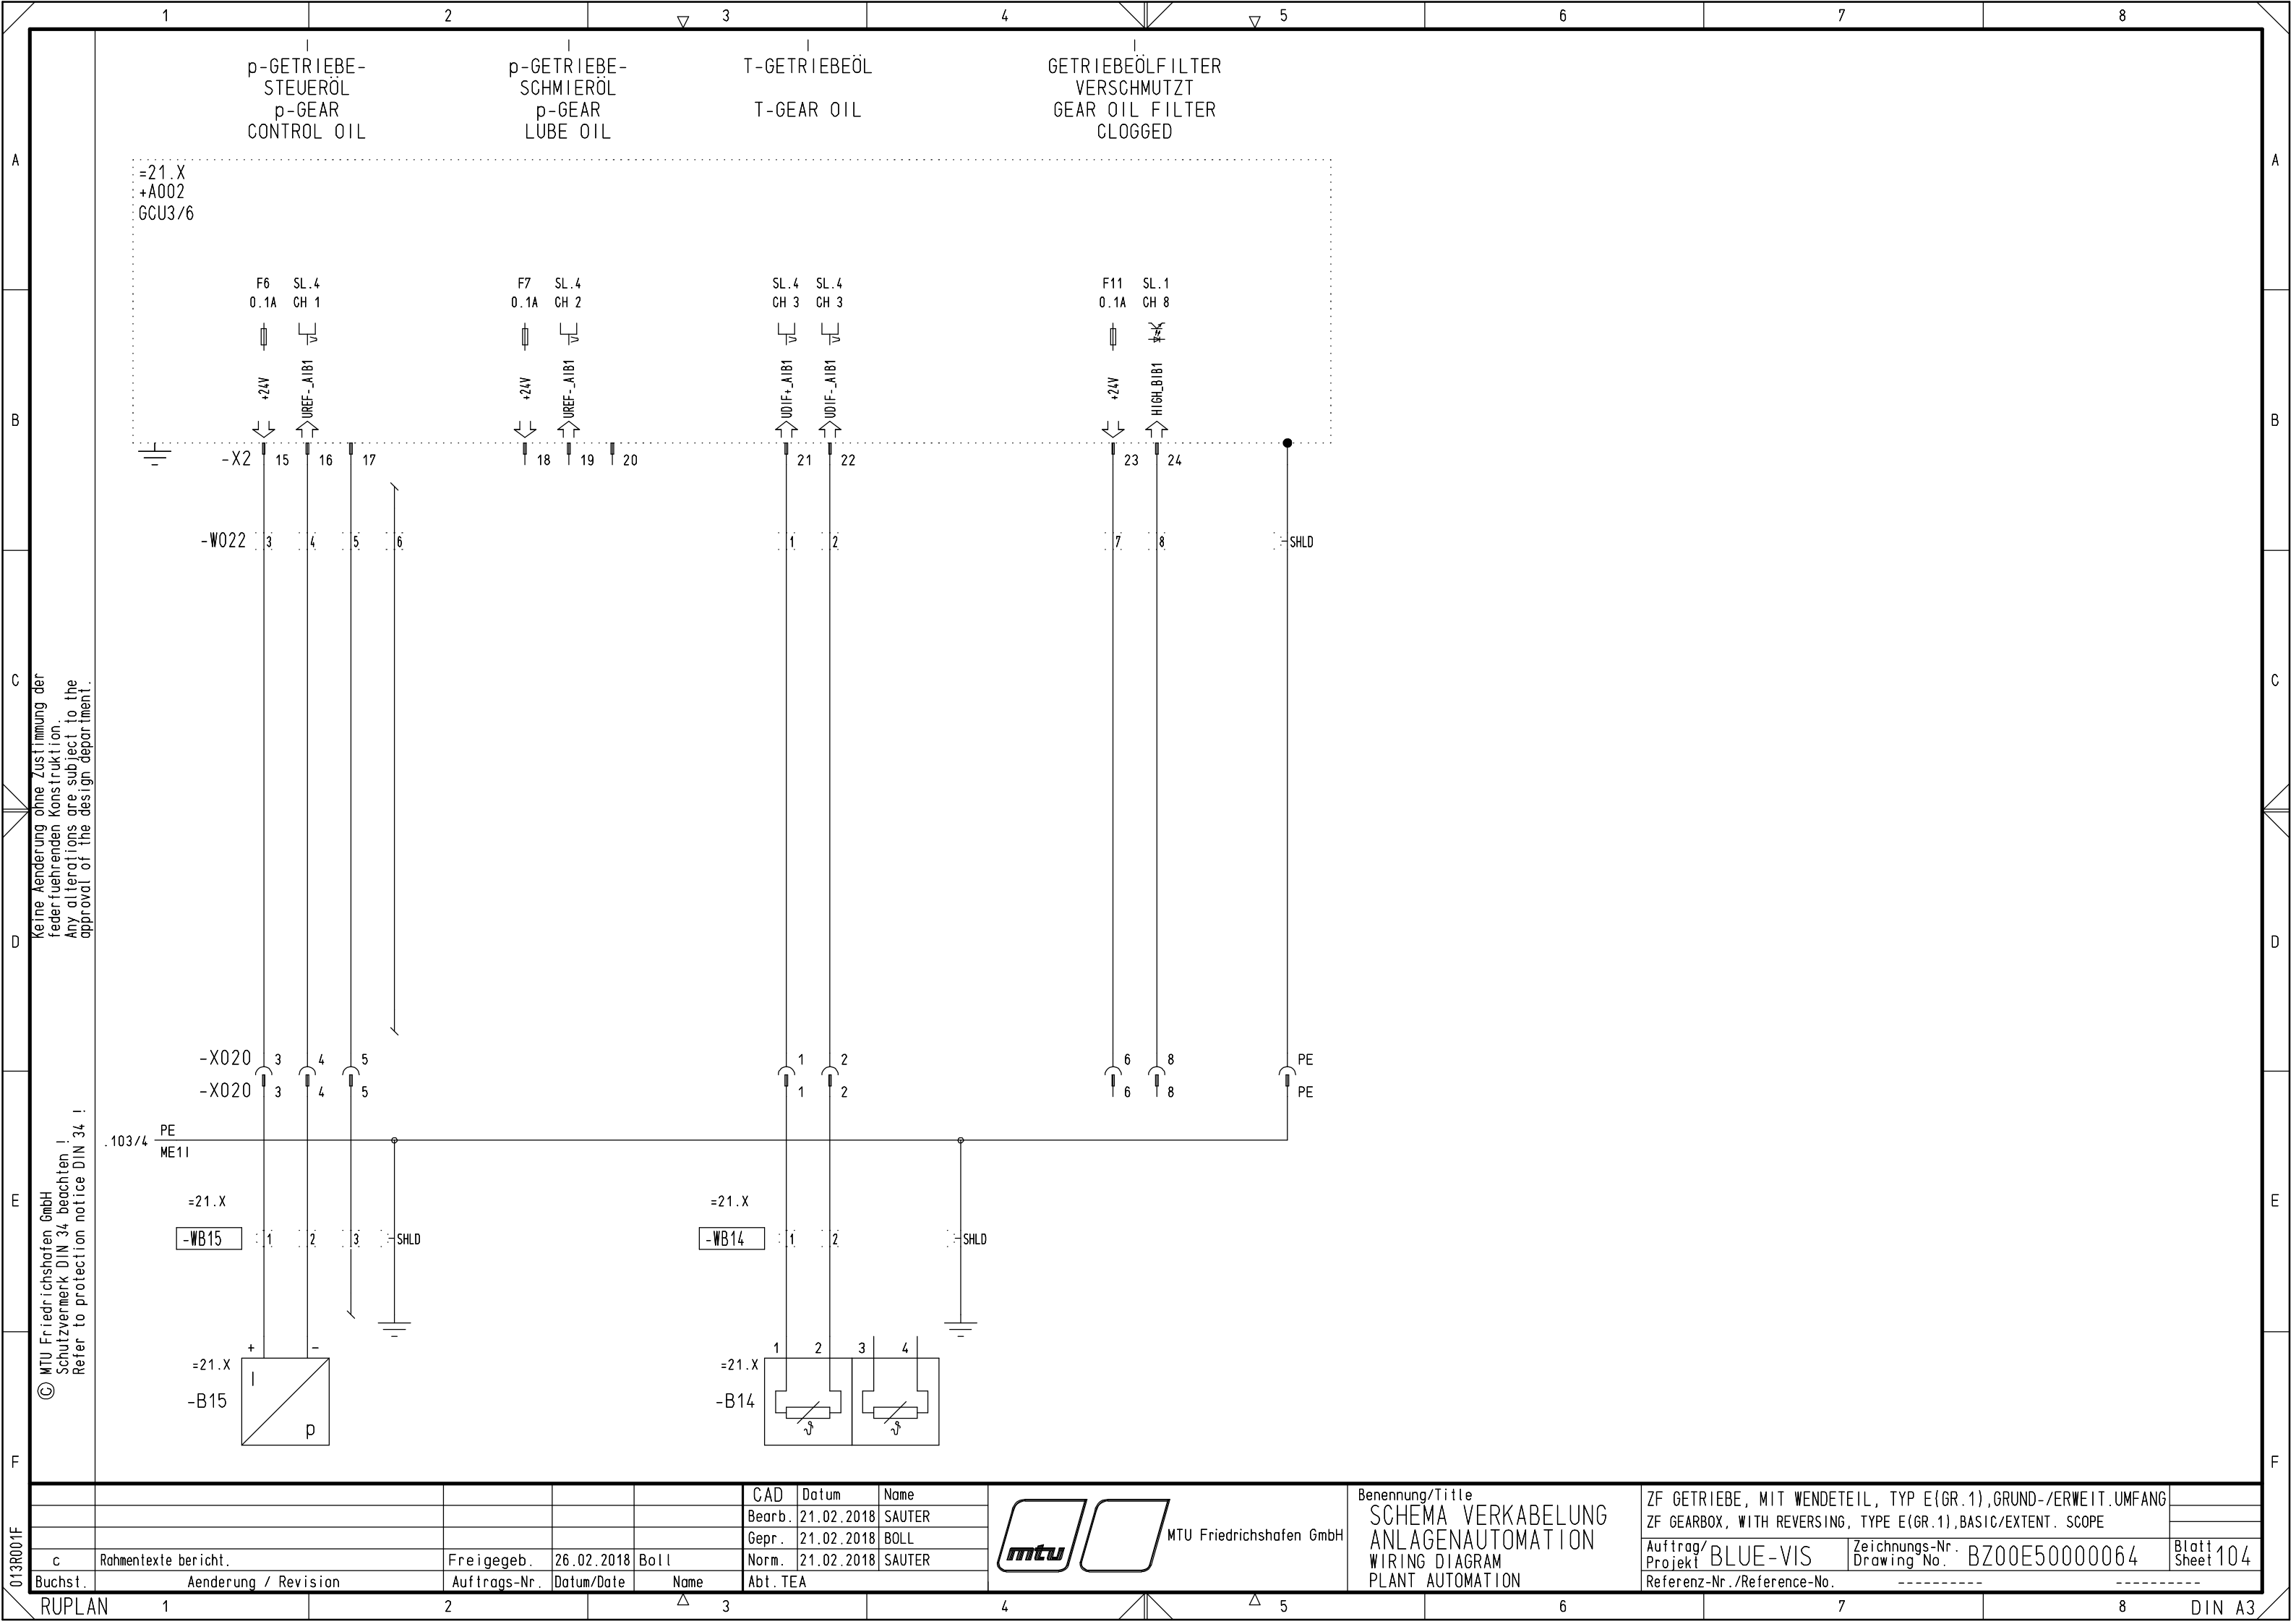

Keine Änderung ohne Zustimmung der
Federführenden Konstruktion.
Any alterations are subject to the
approval of the design department.

© MTU Friedrichshafen GmbH
Schutzvermerk DIN 34 beachten !
Refer to protection notice DIN 34 !

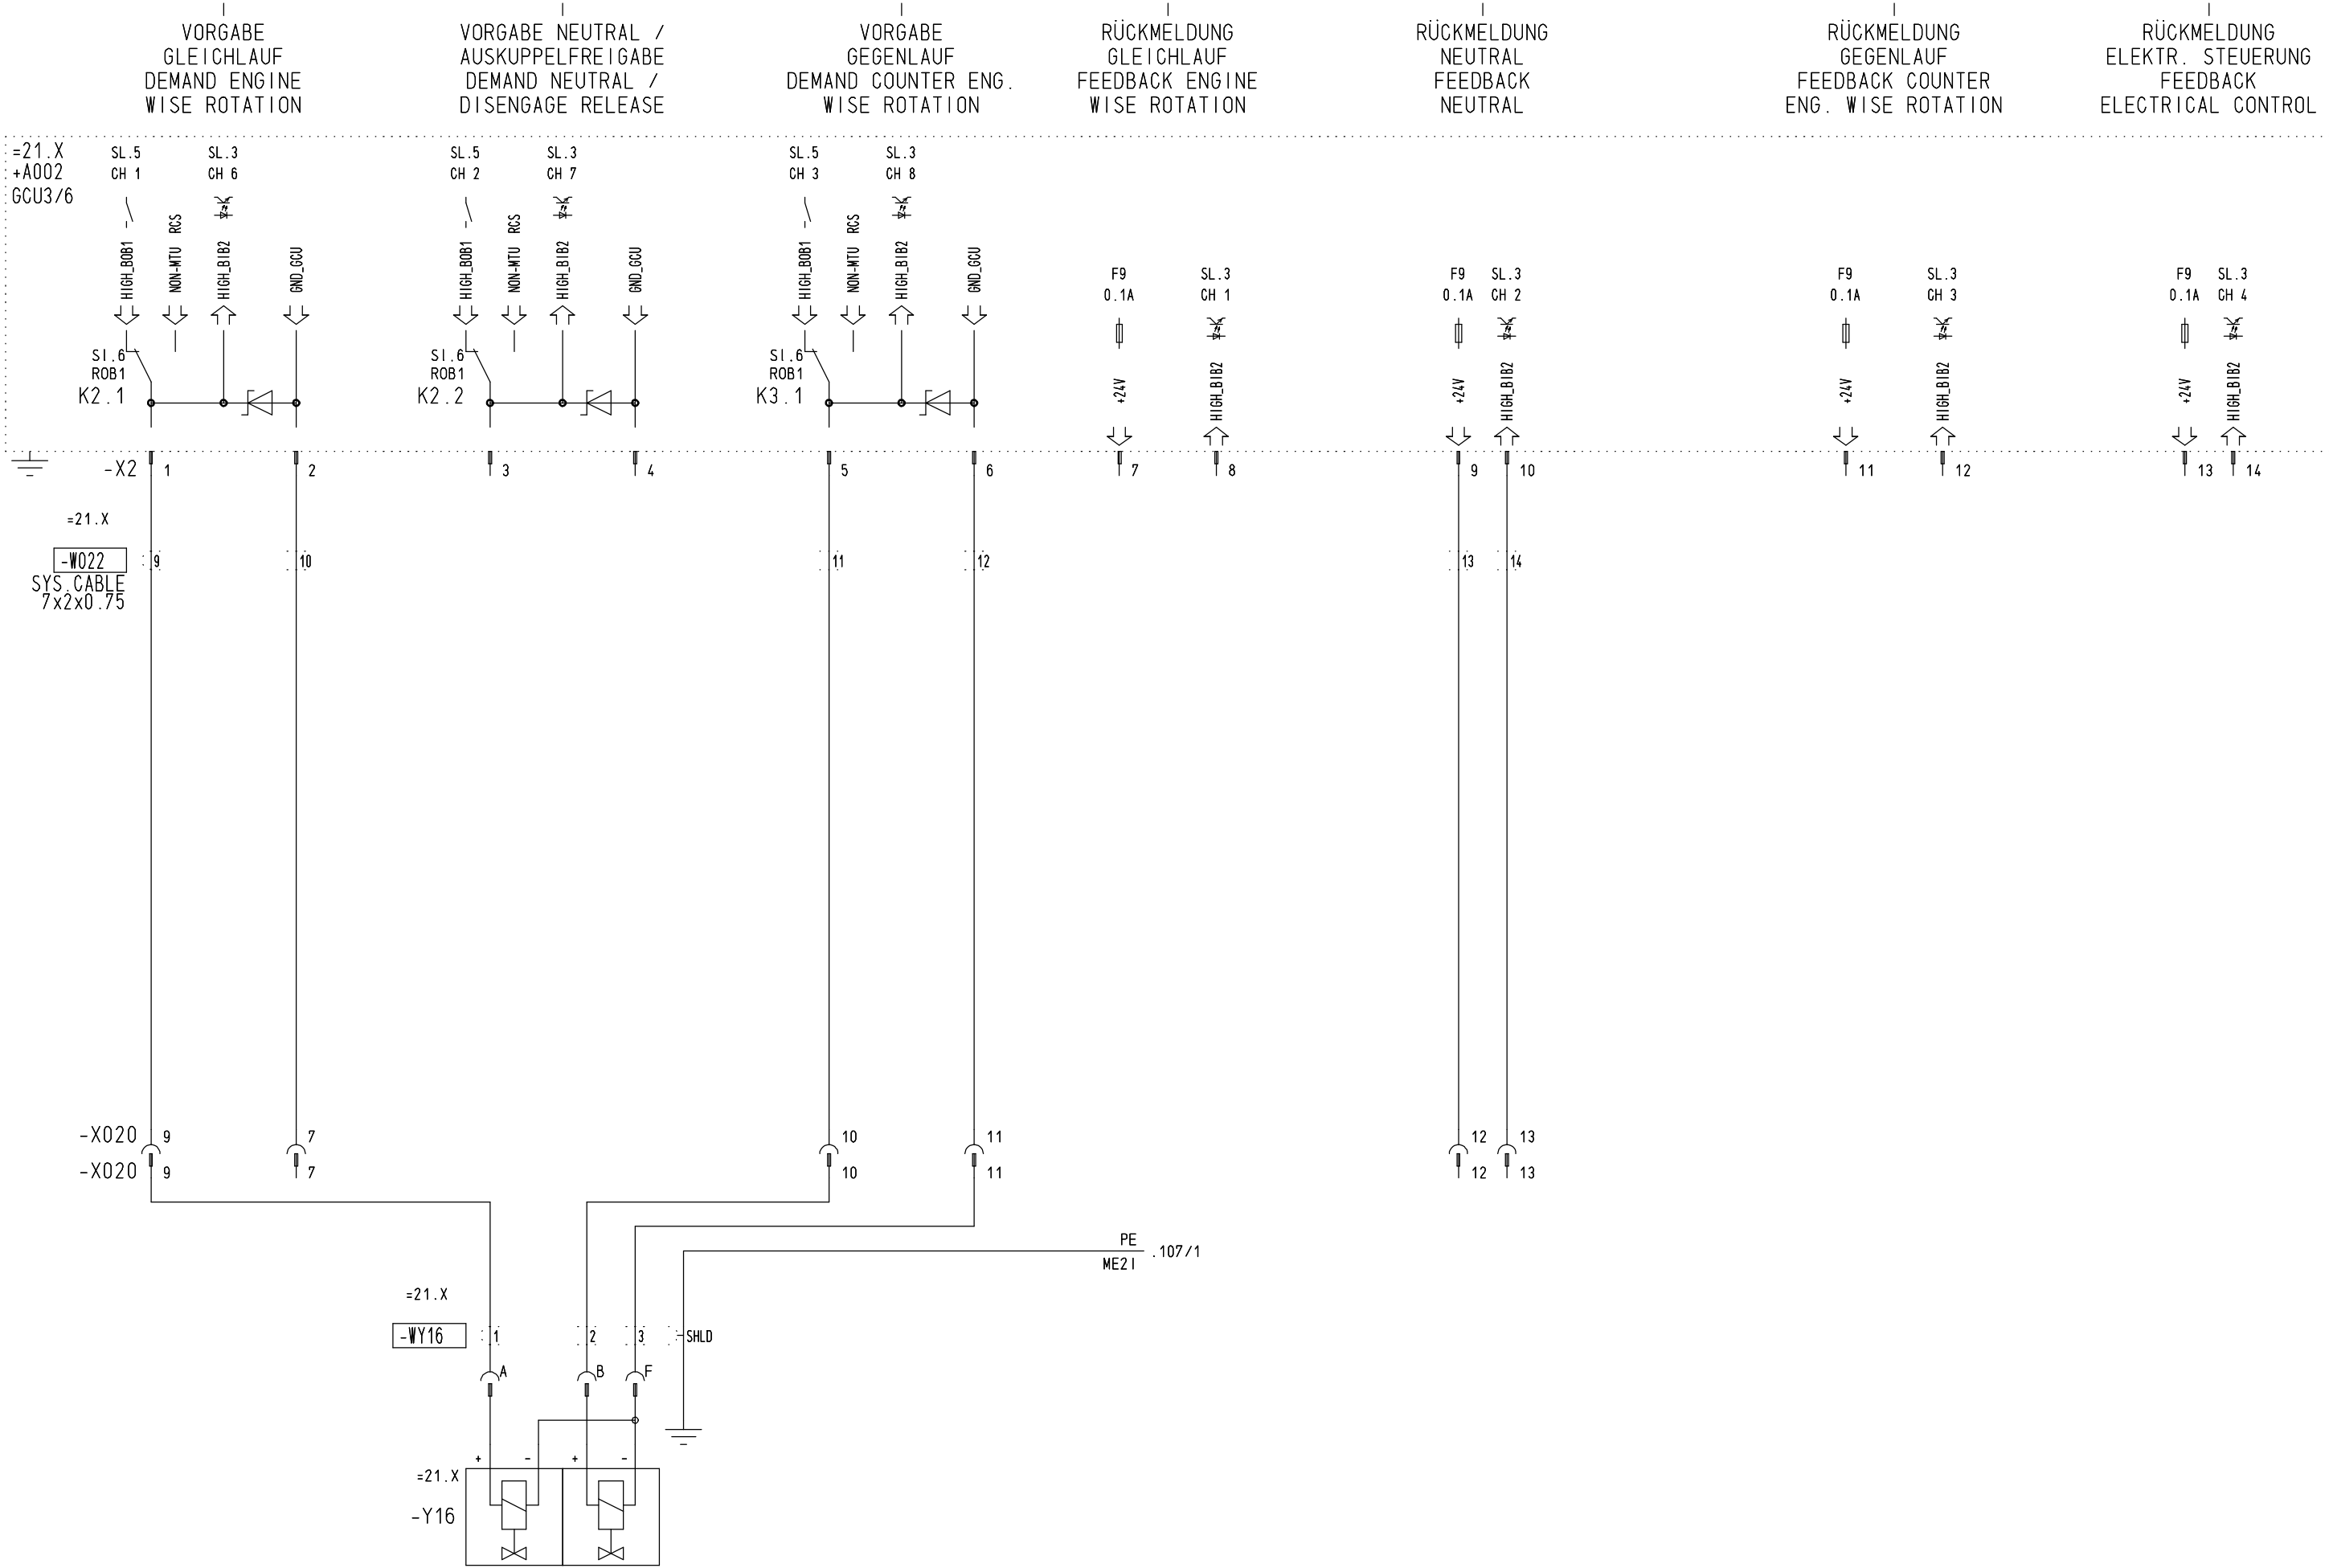

					CAD	Datum	Name
					Bearb.	21.02.2018	SAUTER
						21.02.2018	BOLL
c	Rahmentexte bericht.	Freigegeb.	26.02.2018	Boll	Norm.	21.02.2018	SAUTER
Buchst.	Aenderung / Revision	Auftrags-Nr.	Datum/Date	Name	Abt. TEA		




MTU Friedrichshafen GmbH

Benennung/Title
SCHEMA VERKABELUNG
ANLAGENAUTOMATION
WIRING DIAGRAM
PLANT AUTOMATION

ZF GETRIEBE, MIT WENDETEIL, TYP E(GR.2),GRUND-/ERWEIT.UMFANG
ZF GEARBOX, WITH REVERSING, TYPE E(GR.2),BASIC/EXTENT. SCOPE
Auftrag/Projekt BLUE-VIS
Zeichnungs-Nr./Drawing No. BZ00E50000064
Referenz-Nr./Reference-No. -----

Blatt 106
Sheet 106

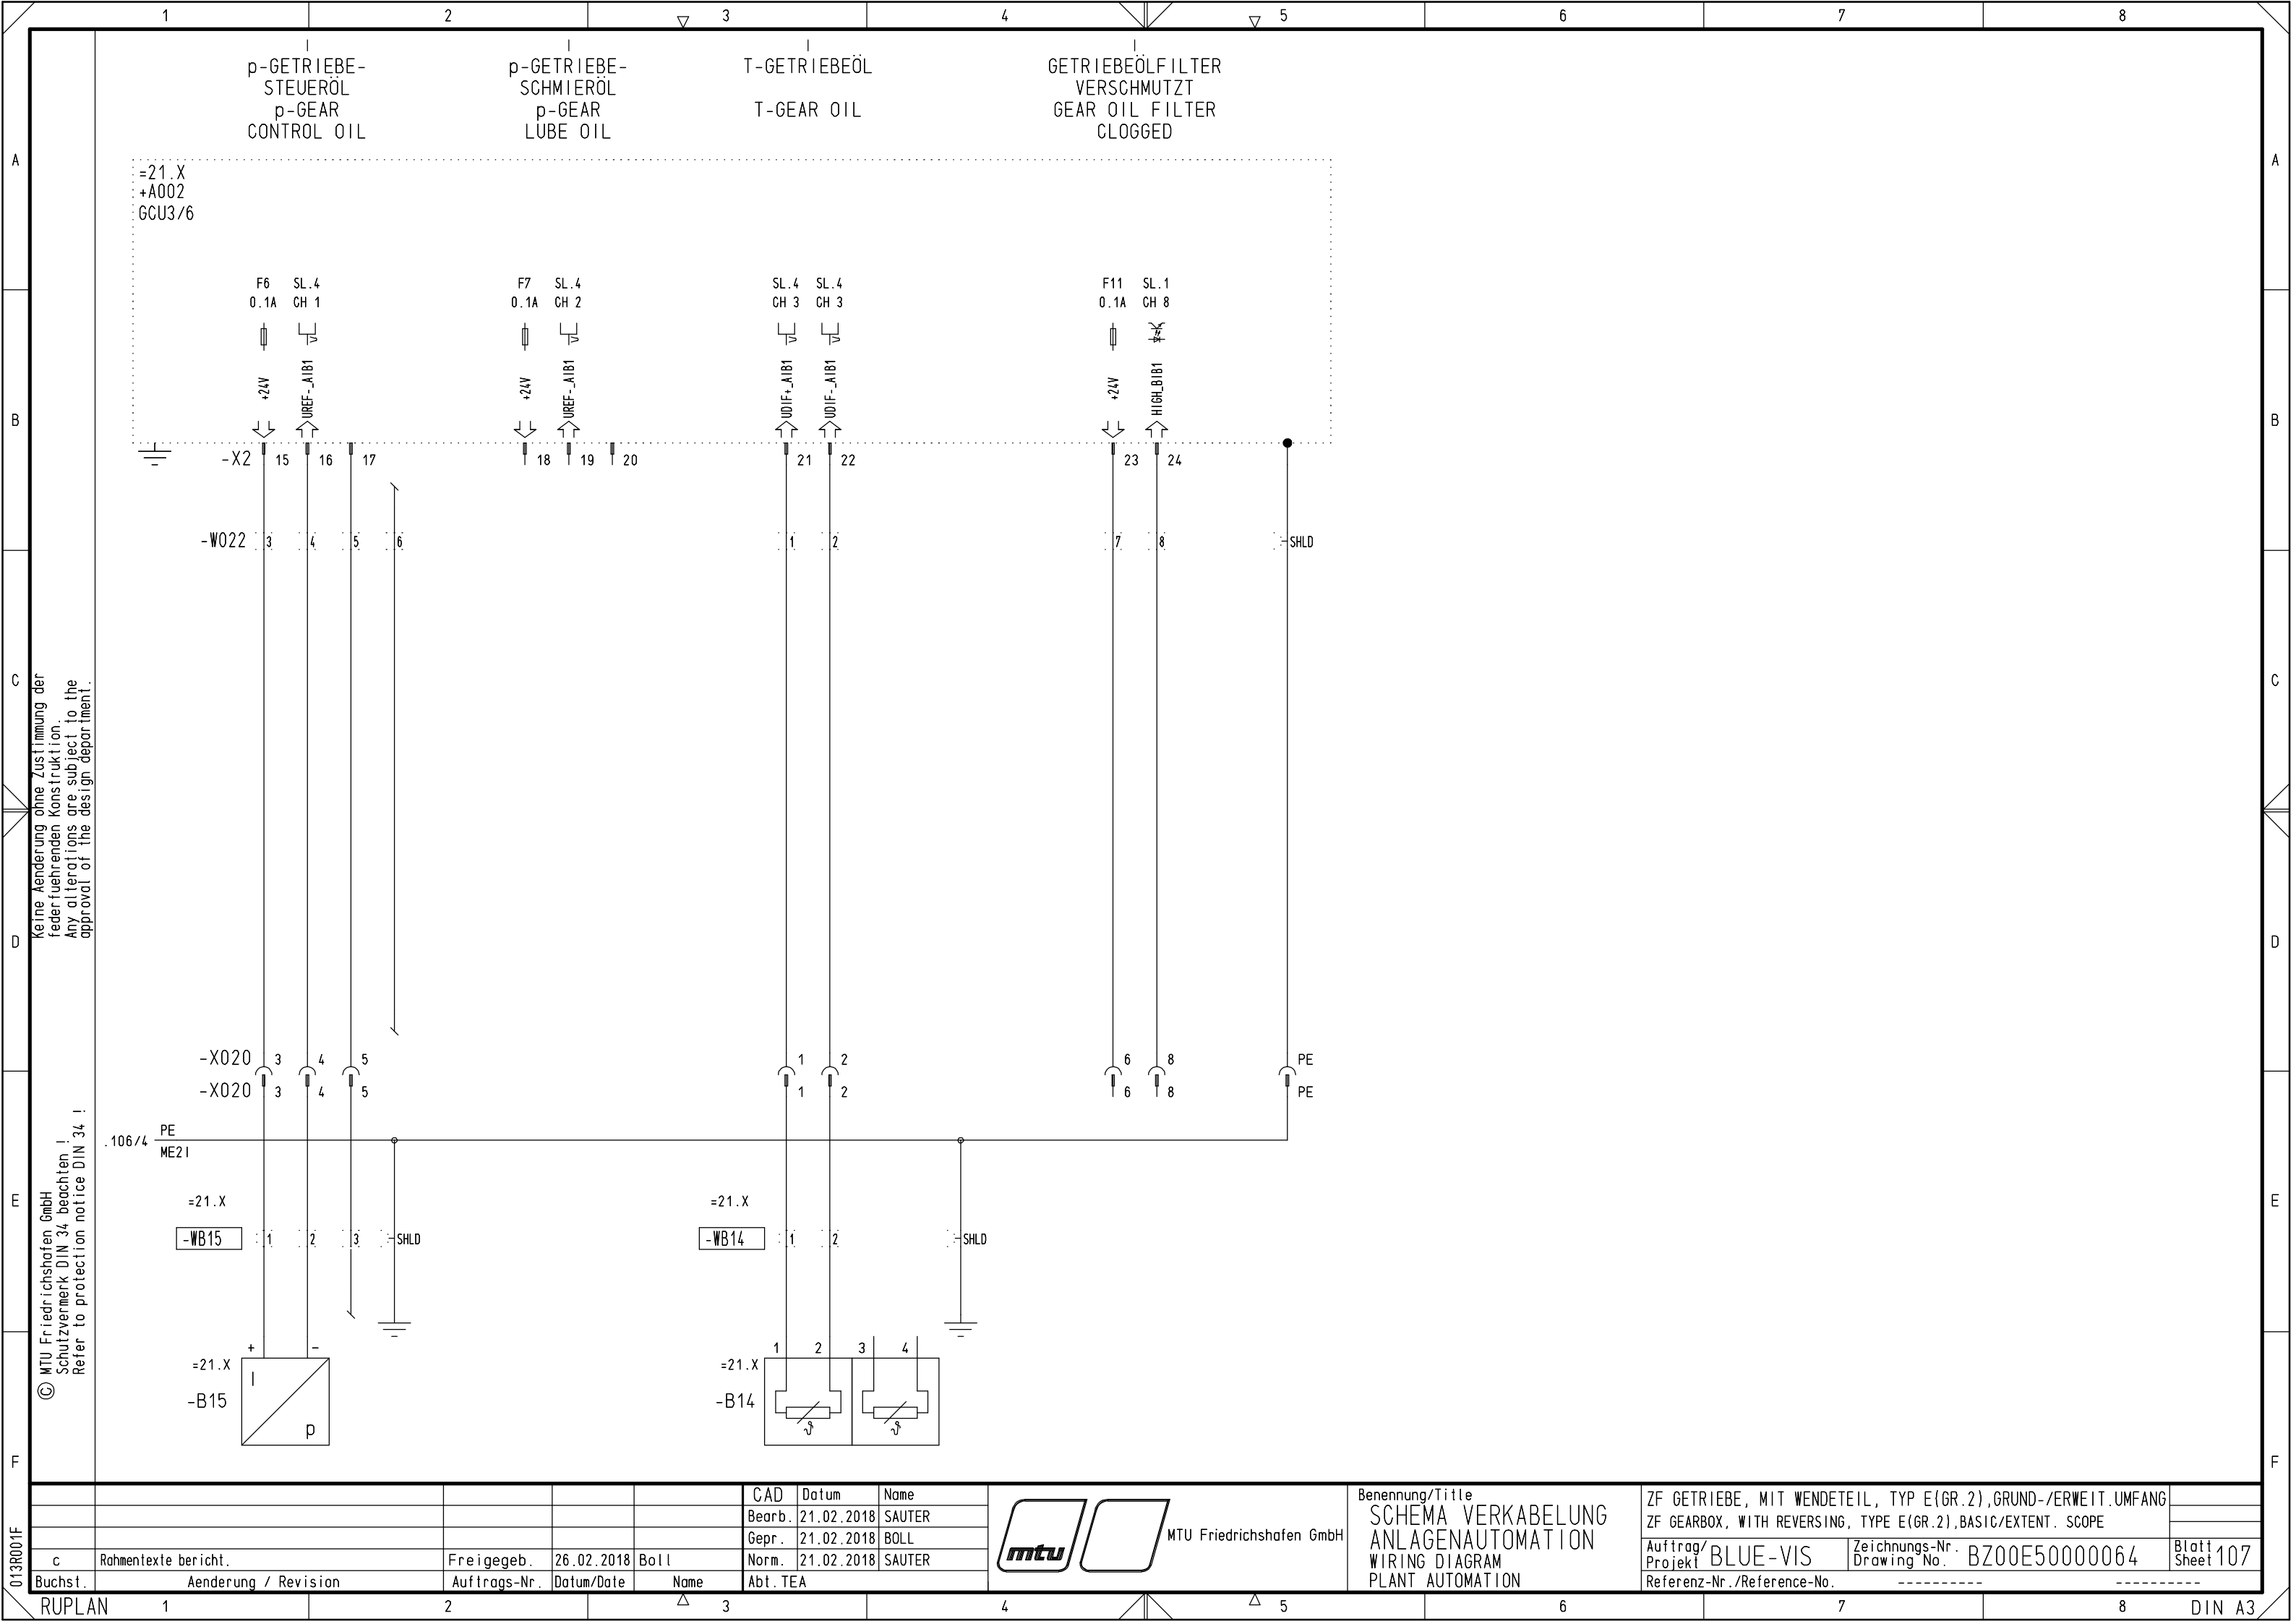


ZF 2150
ZF 2150A
ZF 2150V

© MTU Friedrichshafen GmbH
Schutzvermerk DIN 34 beachten !
Refer to protection notice DIN 34 !

					CAD	Datum	Name	 MTU Friedrichshafen GmbH	Benennung/Title SCHEMA VERKABELUNG ANLAGENAUTOMATION WIRING DIAGRAM PLANT AUTOMATION	ZF GETRIEBE, MIT WENDETEIL, TYP E(GR.3), HINWEISE					
					Bearb.	21.02.2018	SAUTER			ZF GEARBOX, WITH REVERSING, TYPE E(GR.3), INSTRUCTIONS					
					Gepr.	21.02.2018	BOLL								
					Norm.	21.02.2018	SAUTER								
c	Rahmentexte bericht.	Freigegeb.	26.02.2018	Boll						Auftrag/ Projekt	BLUE-VIS	Zeichnungs-Nr. Drawing No.	BZ00E500000064	Blatt Sheet	108
Buchst.	Aenderung / Revision	Auftrags-Nr.	Datum/Date	Name	Abt.	TEA				Referenz-Nr./Reference-No.			-----		

Keine Änderung ohne Zustimmung der
federführenden Konstruktion.
Any alterations are subject to the
approval of the design department.

© MTU Friedrichshafen GmbH
Schutzvermerk DIN 34 beachten !
Refer to protection notice DIN 34 !

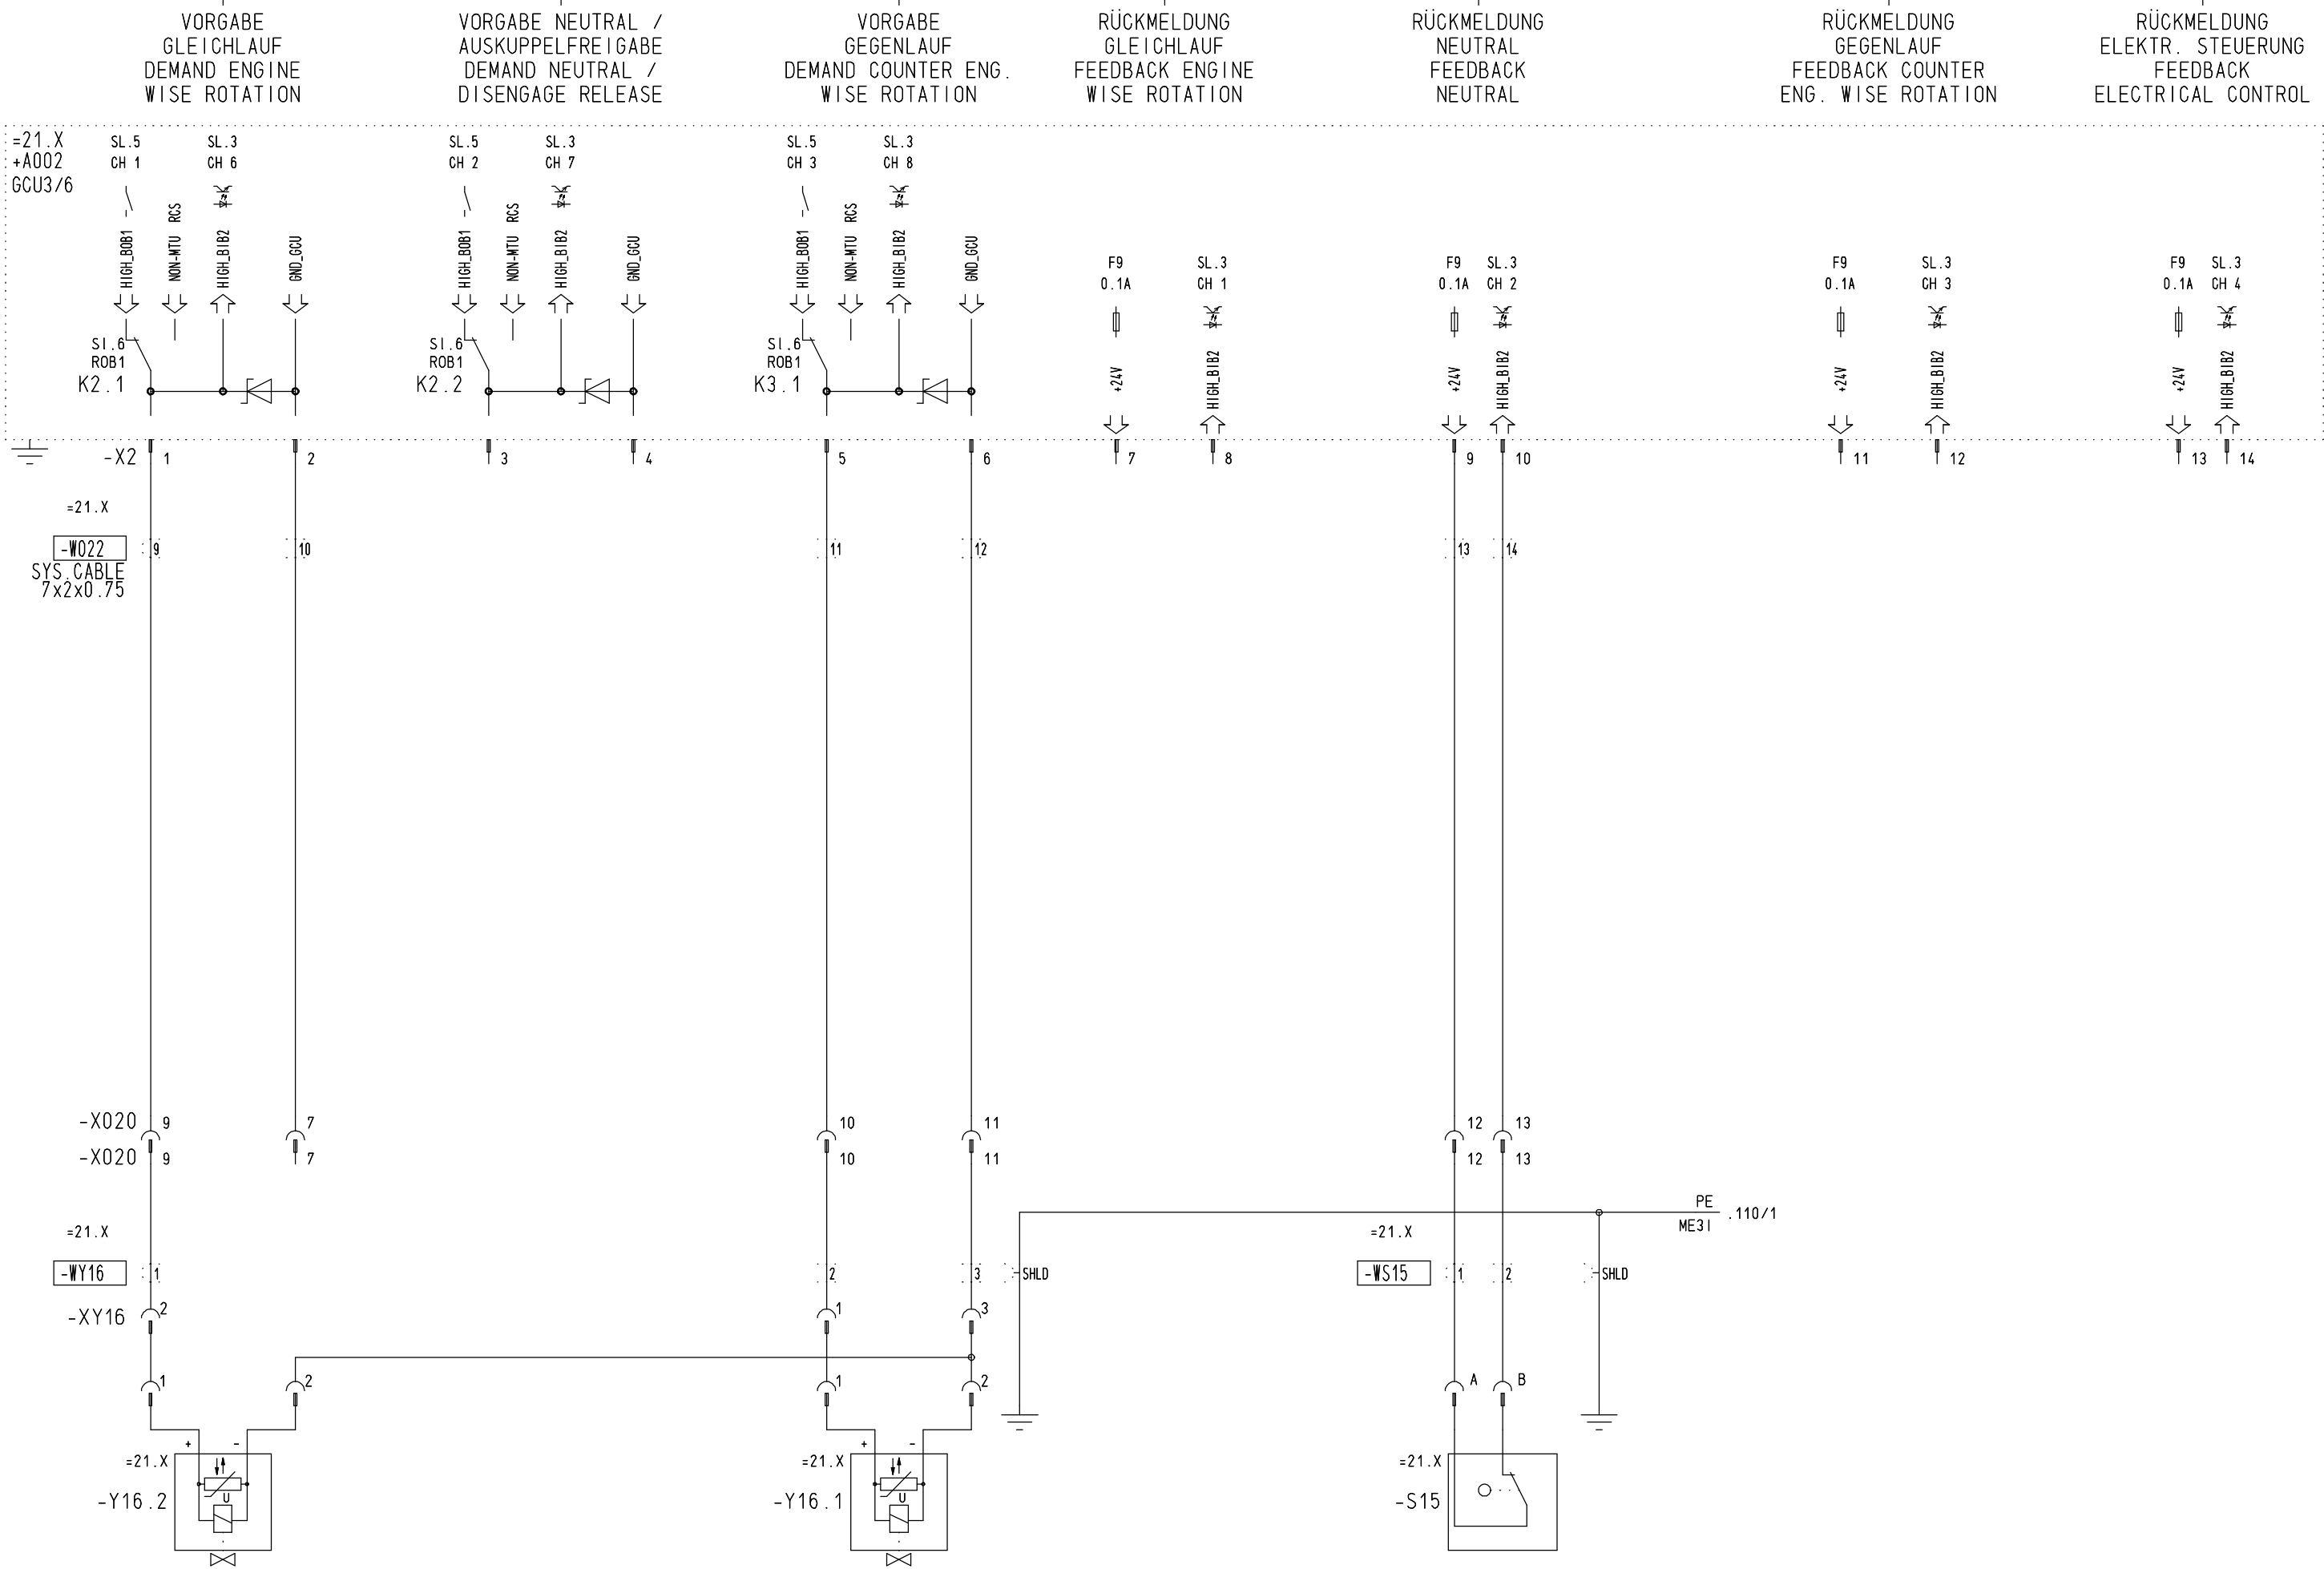

					CAD	Datum	Name
					Bearb.	21.02.2018	SAUTER
					Gedr.	21.02.2018	BOLL
					Norm.	21.02.2018	SAUTER
c	Rahmentexte bericht.	Freigegeb.	26.02.2018	Boll	Abt. TEA		
Buchst.	Aenderung / Revision	Auftrags-Nr.	Datum/Date	Name			




MTU Friedrichshafen GmbH

Benennung/Title
SCHEMA VERKABELUNG
ANLAGENAUTOMATION
WIRING DIAGRAM
PLANT AUTOMATION

ZF GETRIEBE, MIT WENDETEIL, TYP E(GR.3),GRUND-/ERWEIT.UMFANG
ZF GEARBOX, WITH REVERSING, TYPE E(GR.3),BASIC/EXTENT. SCOPE
Auftrag/Projekt BLUE-VIS
Zeichnungs-Nr. Drawing No. BZ00E50000064
Referenz-Nr./Reference-No. -----

Blatt 109
Sheet

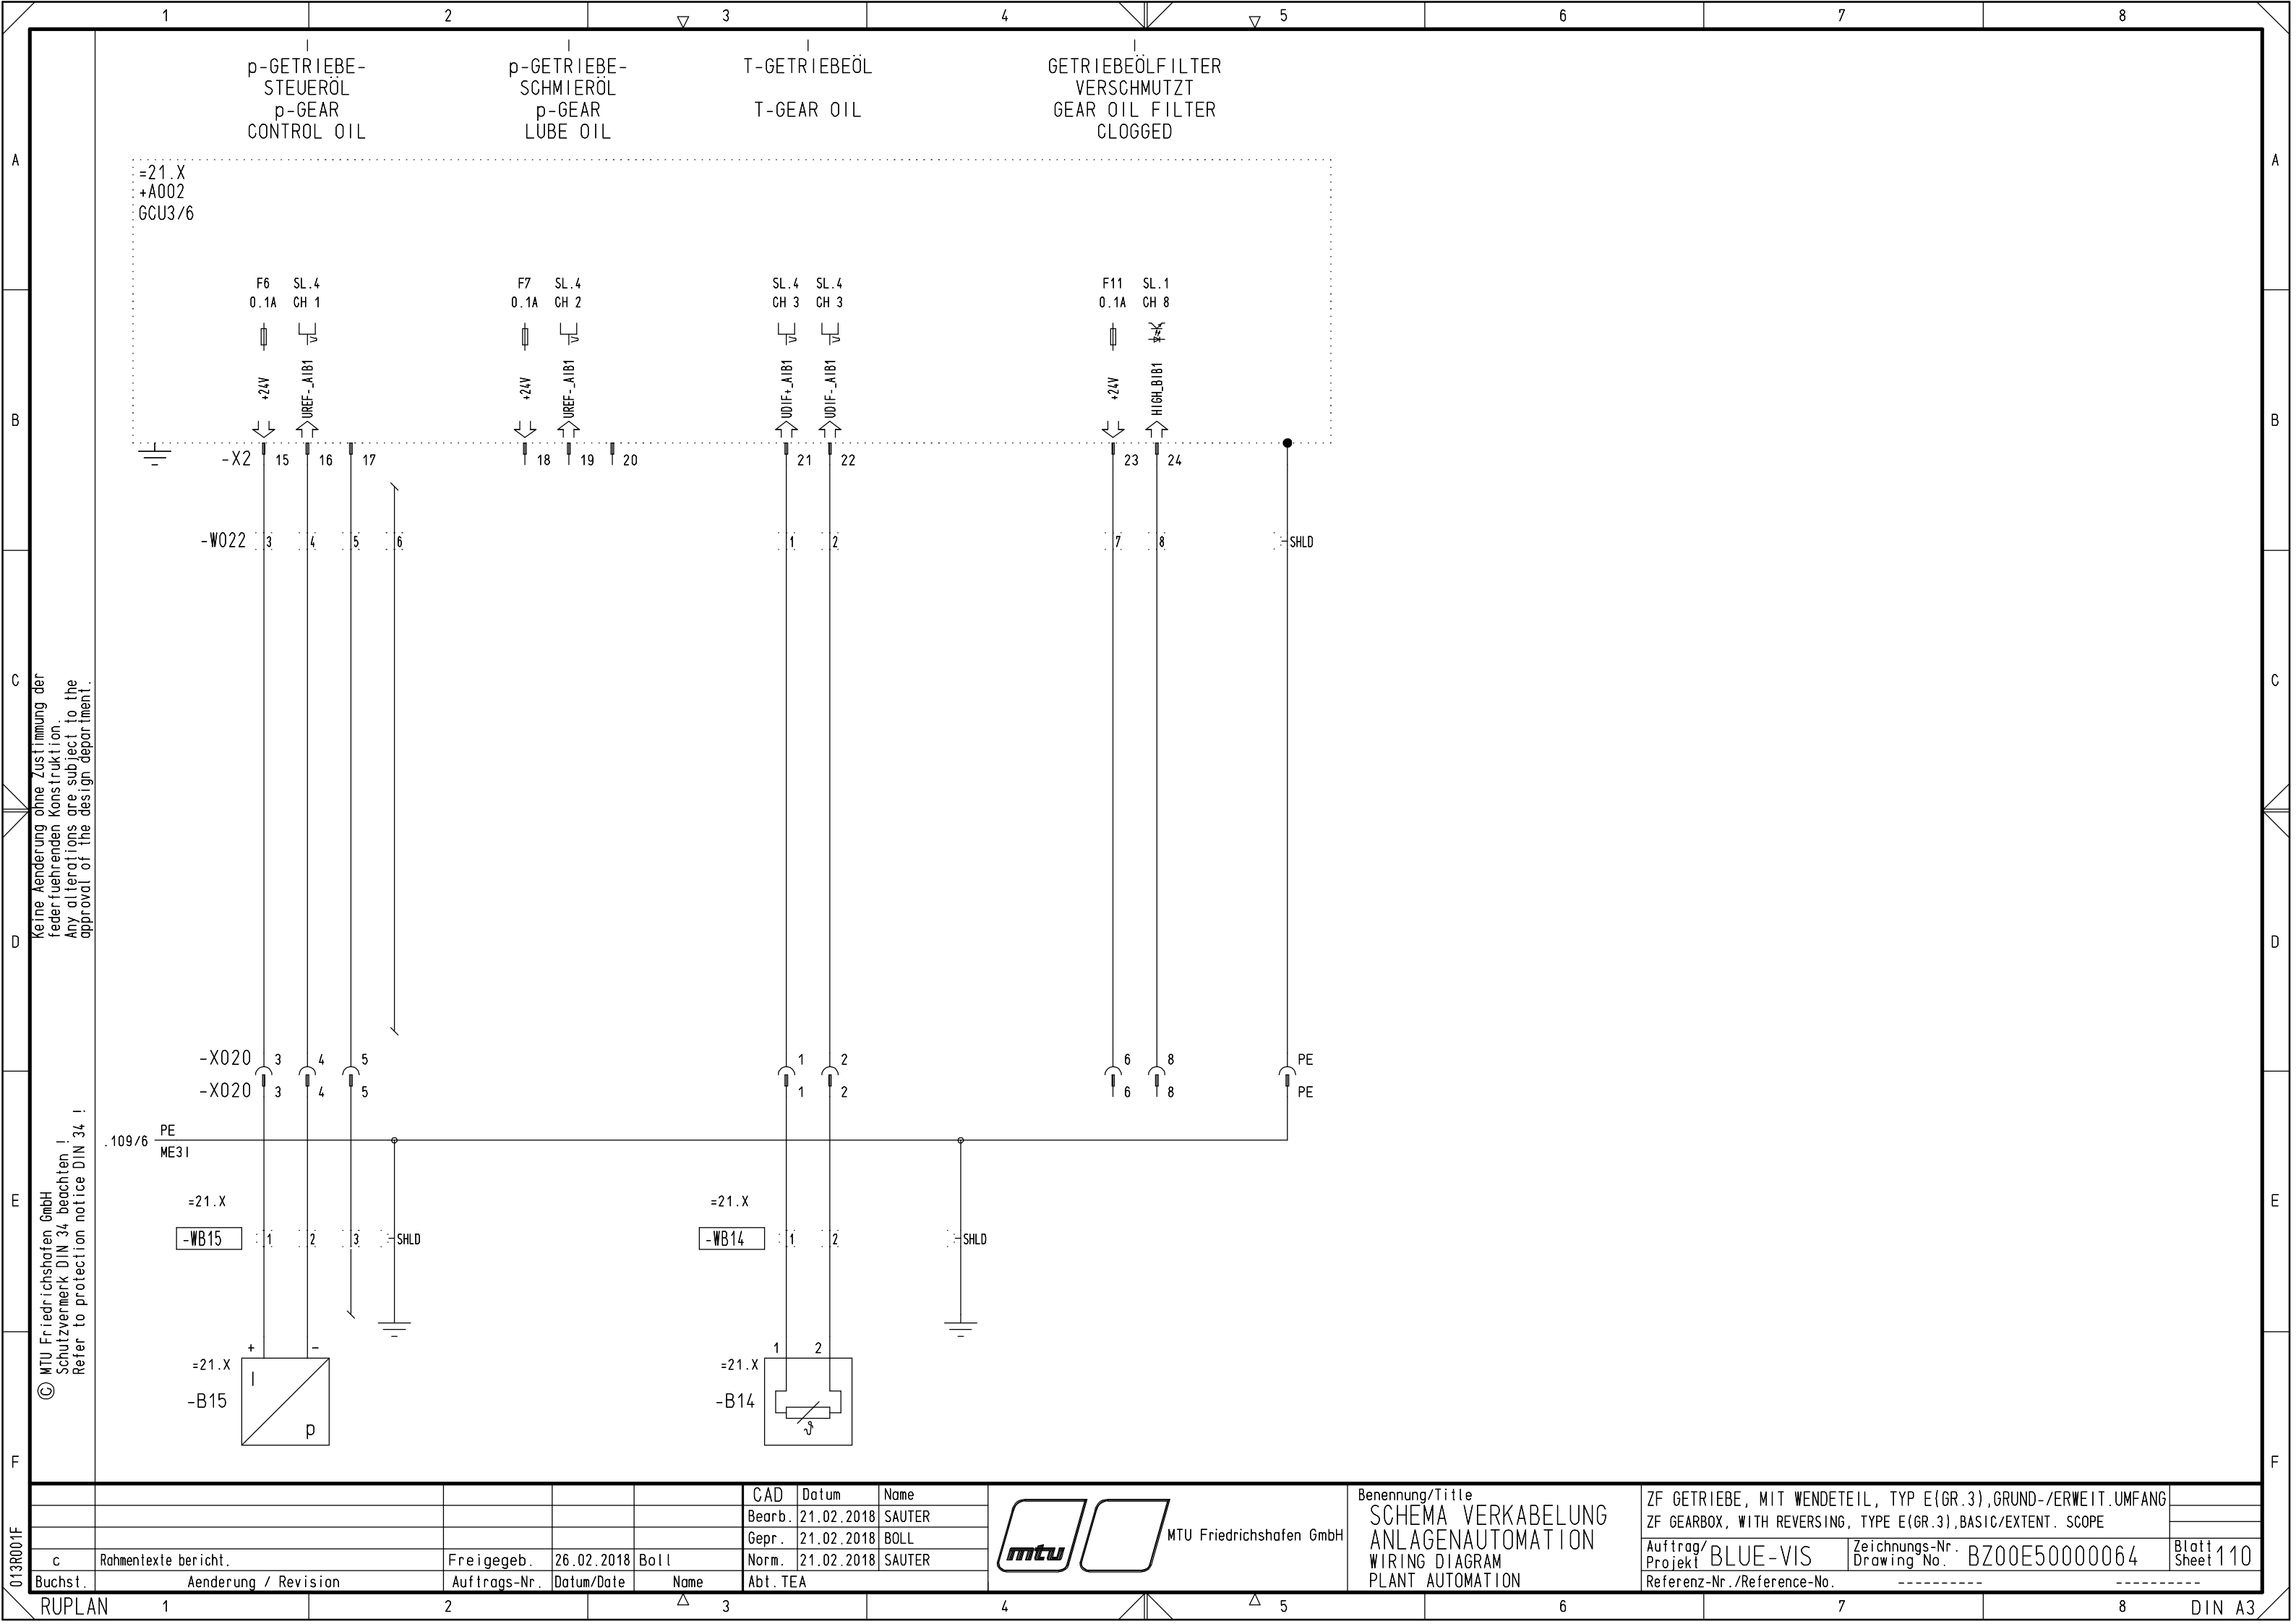

1

2

3

4

5

6

7

8

A

B

C

D

E

F

HINWEIS

PRINZIP-SCHALTPLAN FÜR UNBEKANNTES
ZF GETRIEBE

NUR ZUR INFORMATION

NOTE

GENERAL CIRCUIT DIAGRAM FOR UNKNOWN
ZF GEARBOX

FOR INFORMATION ONLY

Keine Änderung ohne Zustimmung der
federführenden Konstruktion.
Any alterations are subject to the
approval of the design department.

© MTU Friedrichshafen GmbH
Schutzmerk DIN 34 beachten !
Refer to protection notice DIN 34 !

					CAD	Datum	Name	 MTU Friedrichshafen GmbH	Benennung/Title SCHEMA VERKABELUNG ANLAGENAUTOMATION WIRING DIAGRAM PLANT AUTOMATION	ZF GETRIEBE, MAXIMALUMFANG, TYP F, HINWEISE ZF GEARBOX, MAXIMAL SCOPE, TYPE F, INSTRUCTIONS	Auftrag/ Projekt BLUE-VIS	Zeichnungs-Nr. Drawing No. BZ00E50000064	Blatt Sheet 111
					Bearb.	21.02.2018	SAUTER						
					Gepr.	21.02.2018	BOLL						
c	Rahmentexte bericht.	Freigegeb.	26.02.2018	Boll	Norm.	21.02.2018	SAUTER						
Buchst.	Aenderung / Revision	Auftrags-Nr.	Datum/Date	Name	Abt. TEA								

RUPLAN

1

2

3

4

5

6


7

8

DIN A3

Keine Änderung ohne Zustimmung der
federführenden Konstruktion.
Any alterations are subject to the
approval of the design department.


© MTU Friedrichshafen GmbH
Schutzmerk DIN 34 beachten !
Refer to protection notice DIN 34 !

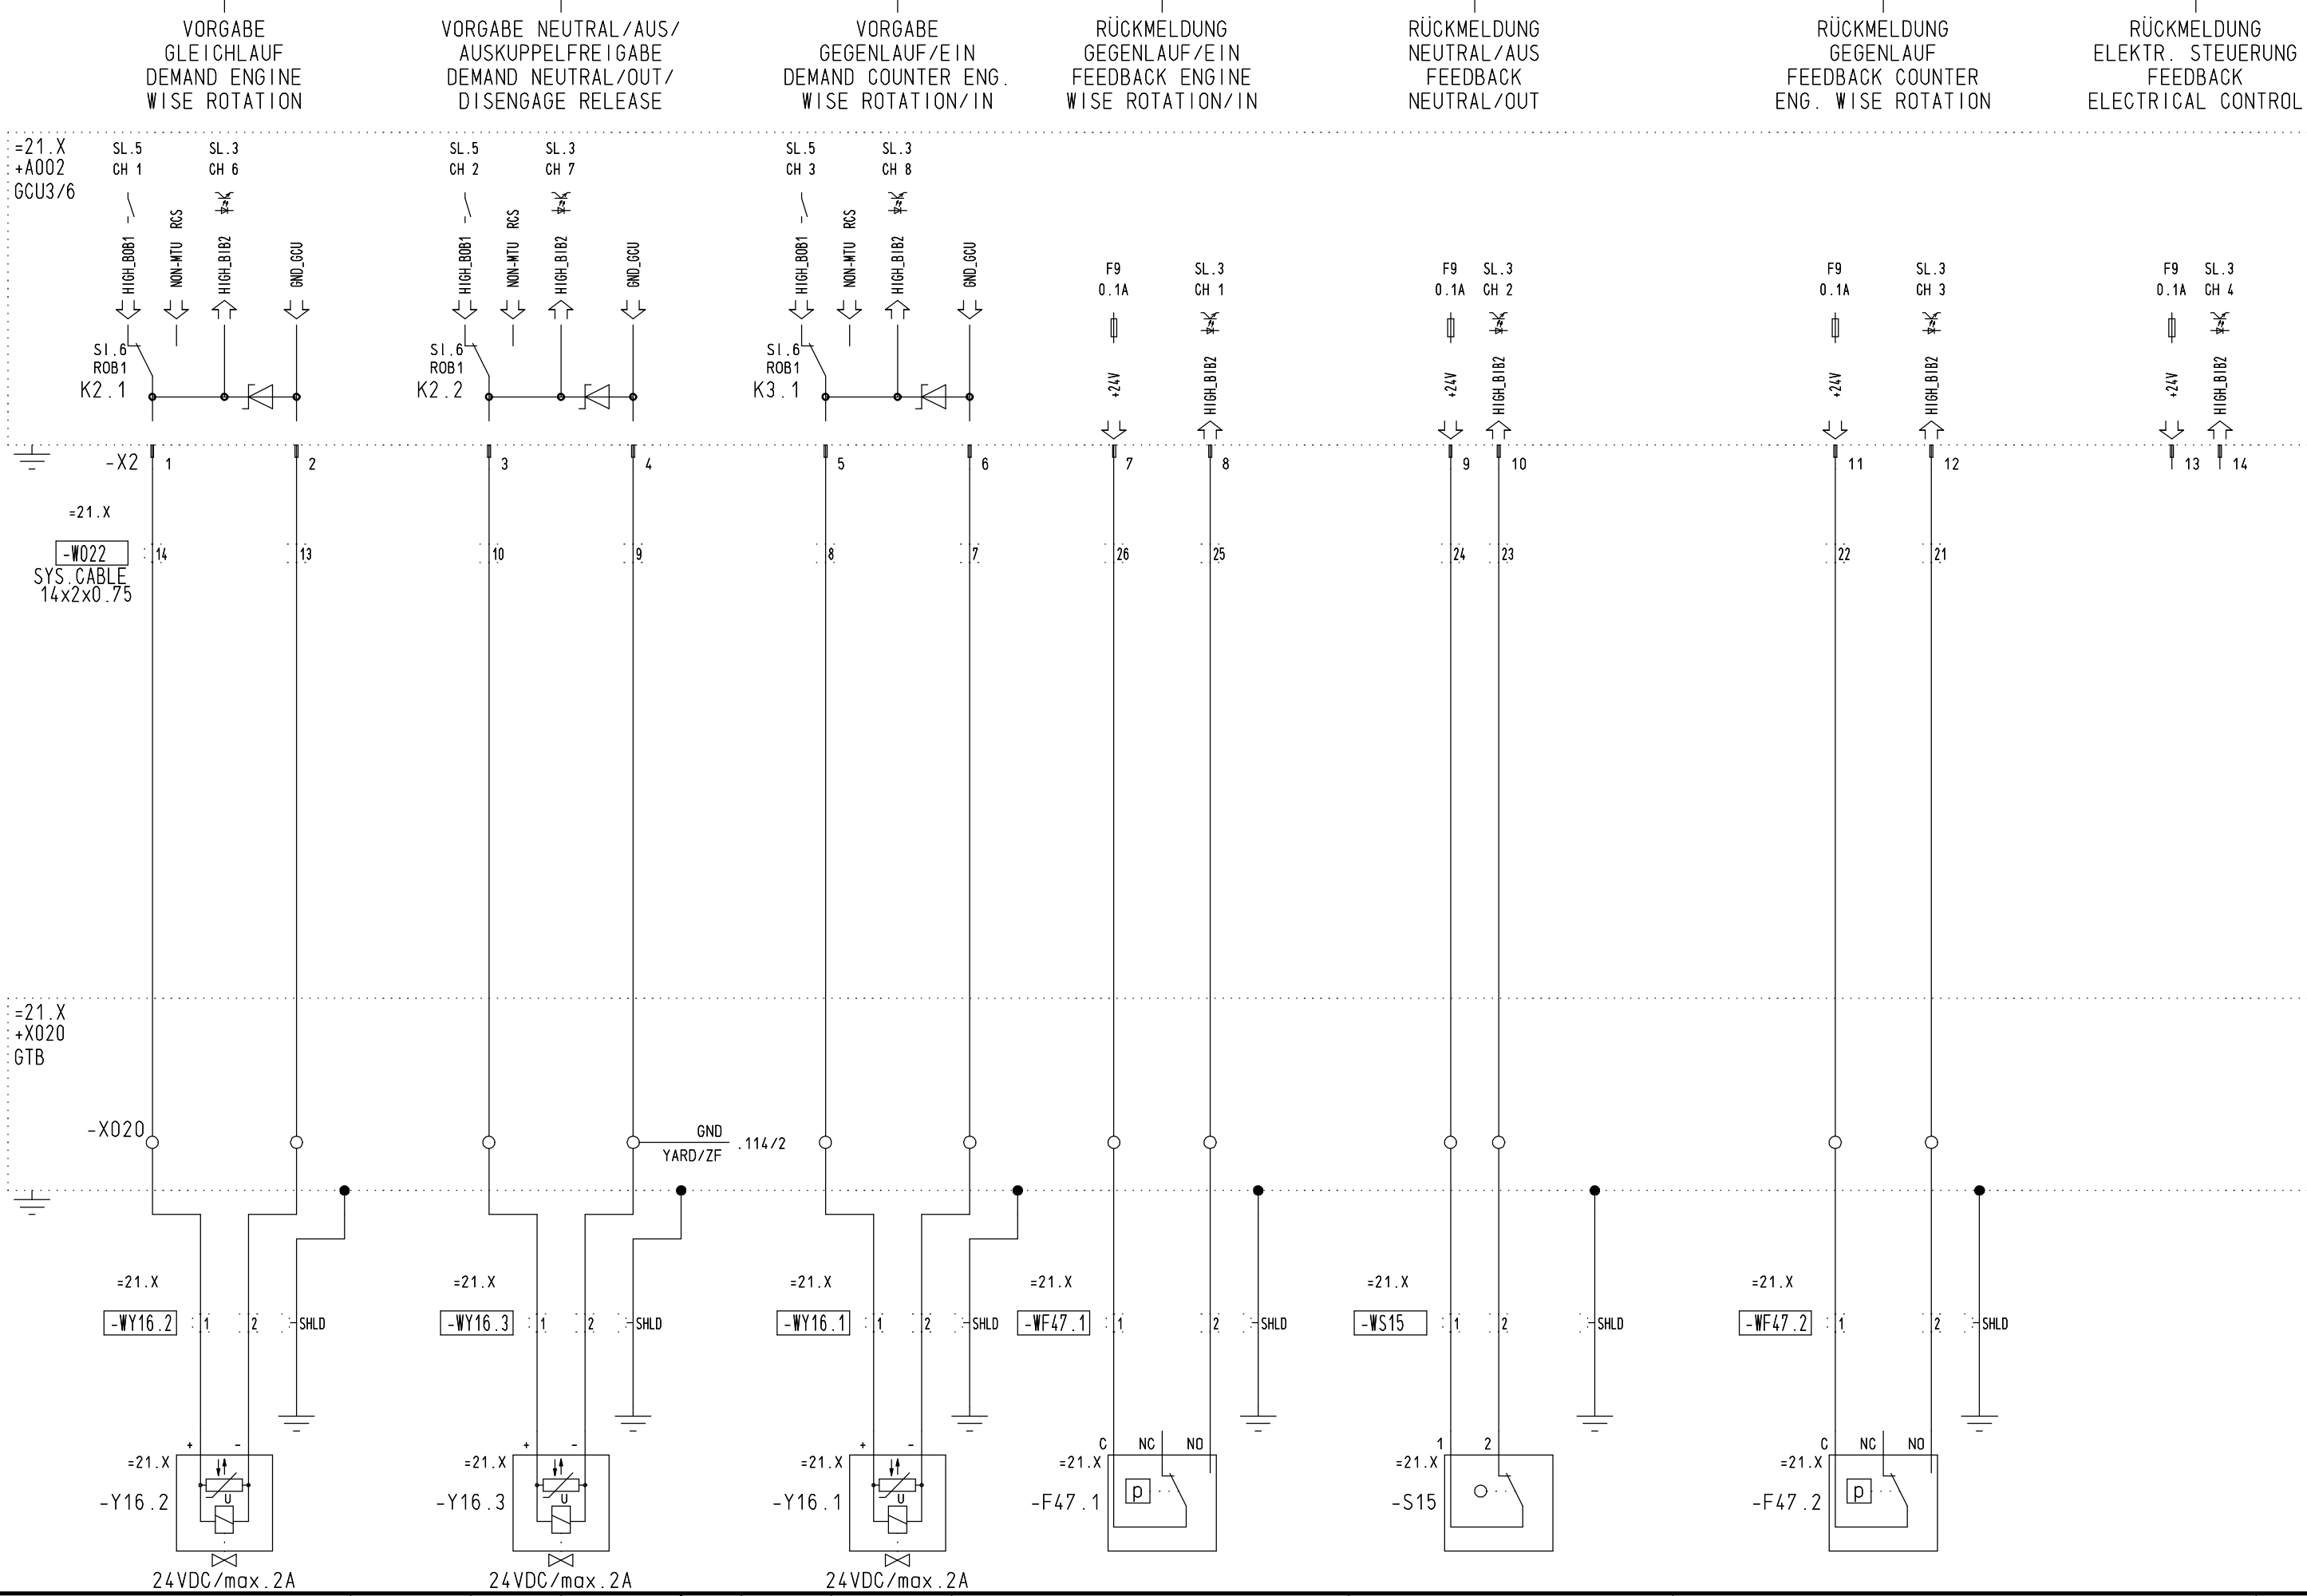

					CAD	Datum	Name	 MTU Friedrichshafen GmbH	Benennung/Title SCHEMA VERKABELUNG ANLAGENAUTOMATION WIRING DIAGRAM PLANT AUTOMATION	ZF GETRIEBE, MAXIMALUMFANG, TYP F, ERWEIT. UMFANG			Blatt Sheet 112
					Bearb.	21.02.2018	SAUTER			ZF GEARBOX, MAXIMAL SCOPE, TYPE F, EXTENDED SCOPE			
					Gepr.	21.02.2018	BOLL						
					Norm.	21.02.2018	SAUTER						
c	Rahmentexte bericht.		Freigegeb.	26.02.2018	Boll	Norm.	21.02.2018	SAUTER					
Buchst.	Aenderung / Revision		Auftrags-Nr.	Datum/Date	Name	Abt. TEA							

Keine Änderung ohne Zustimmung der
federführenden Konstruktion.
Any alterations are subject to the
approval of the design department.

© MTU Friedrichshafen GmbH
Schutzvermerk DIN 34 beachten !
Refer to protection notice DIN 34 !


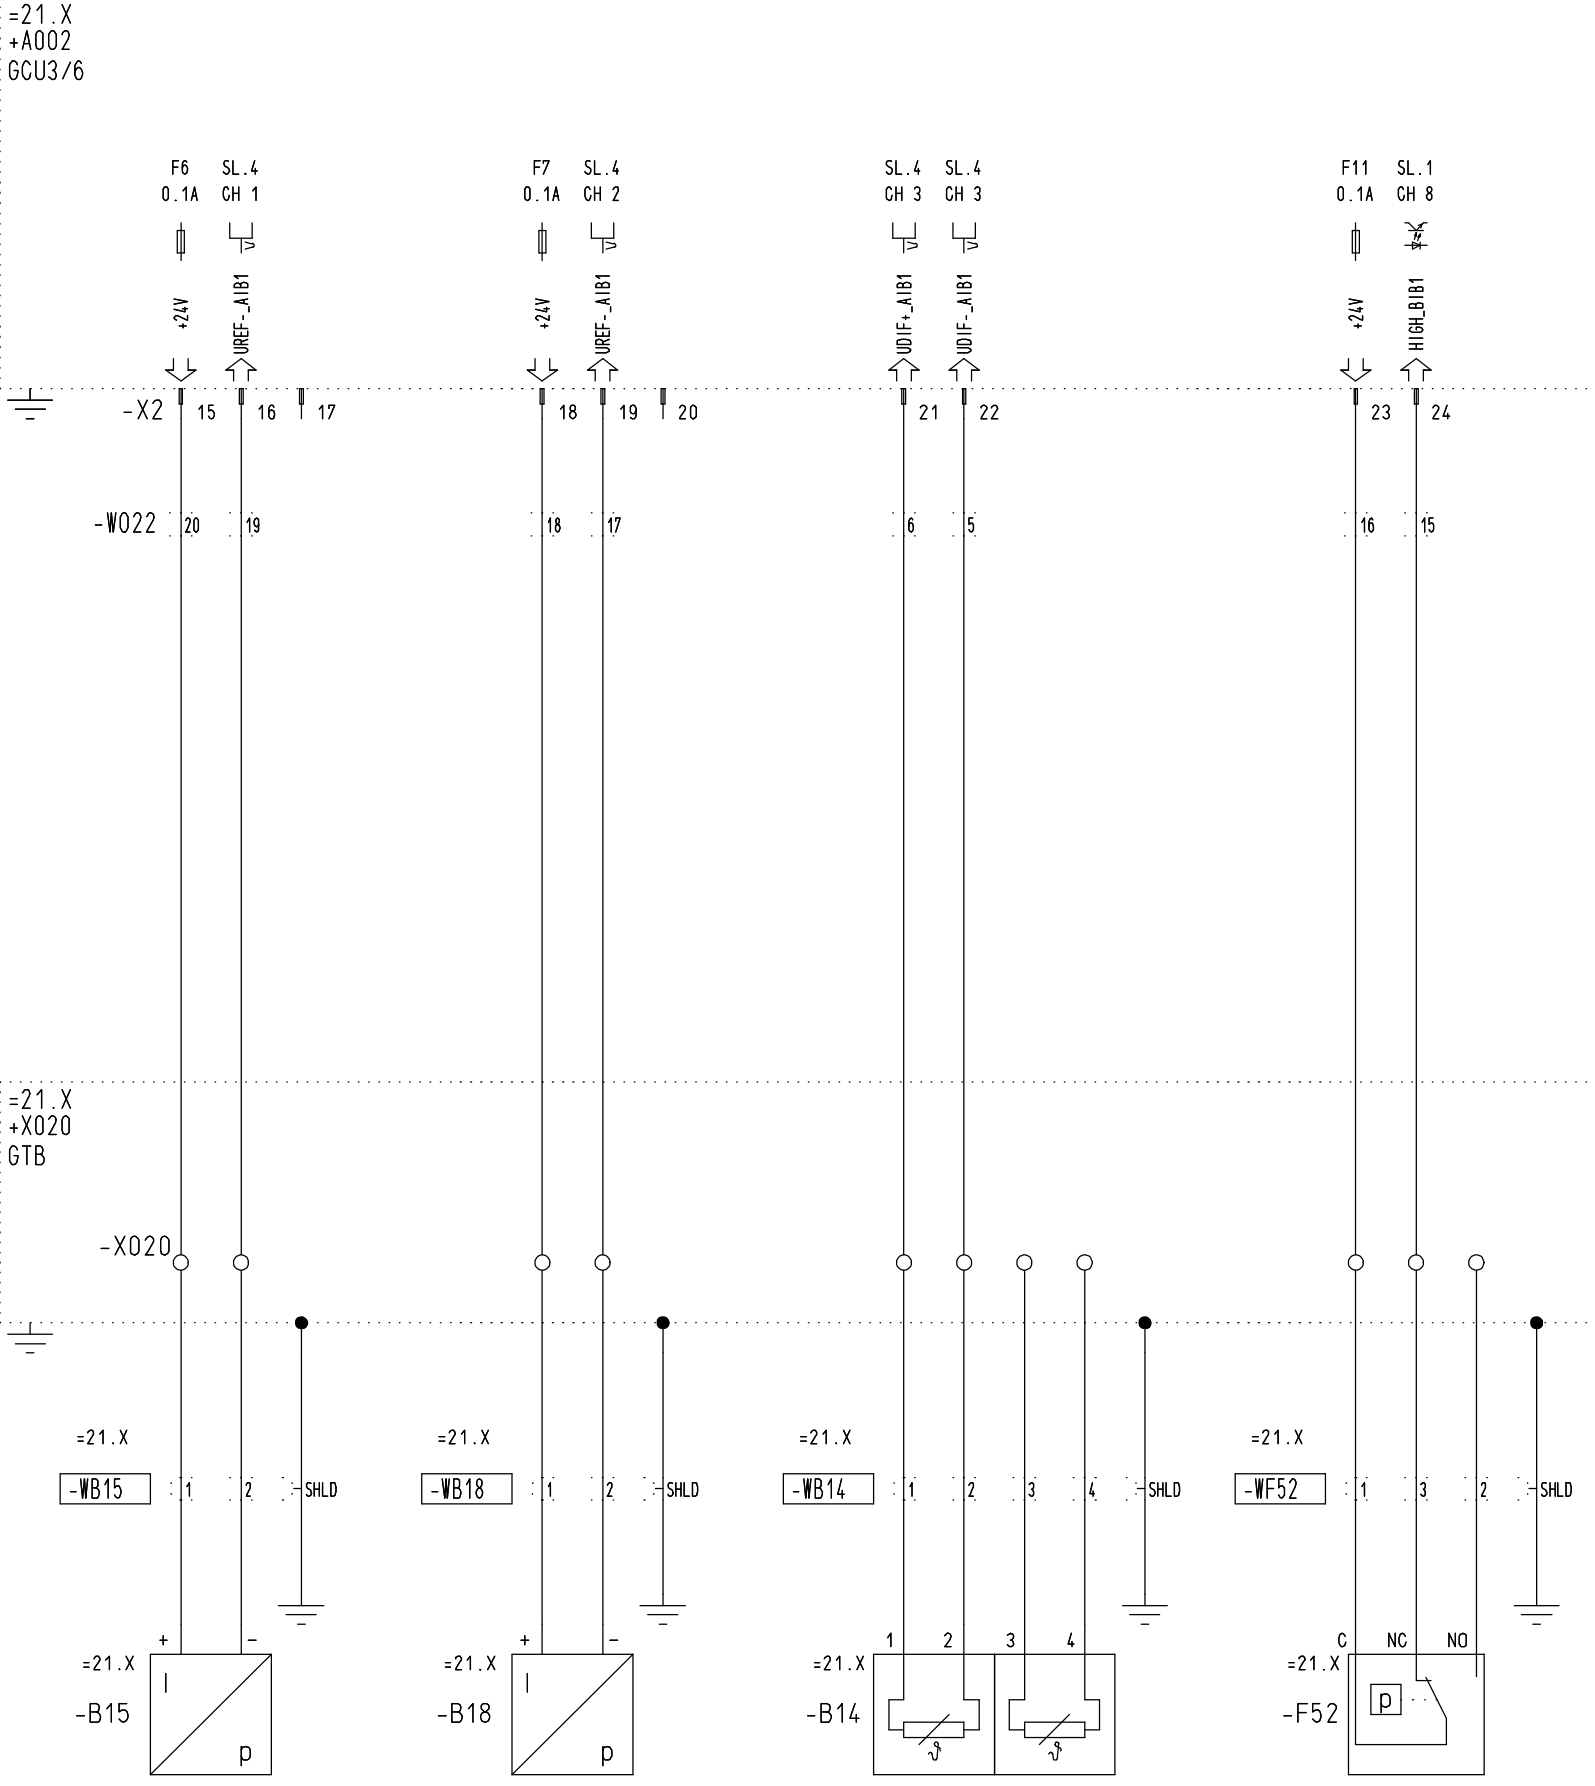


					CAD	Datum	Name	 MTU Friedrichshafen GmbH	Benennung/Title SCHEMA VERKABELUNG ANLAGENAUTOMATION WIRING DIAGRAM PLANT AUTOMATION	ZF GETRIEBE, MAXIMALUMFANG, TYP F, ERWEIT. UMFANG			Blatt Sheet 113
					Bearb.	21.02.2018	SAUTER			ZF GEARBOX, MAXIMAL SCOPE, TYPE F, EXTENDED SCOPE			
					Gepr.	21.02.2018	BOLL						
					Norm.	21.02.2018	SAUTER						
c	Rahmentexte bericht.		Freigegeb.	26.02.2018	Boll	Abt. TEA				Auftrag/ Projekt	BLUE-VIS	Zeichnungs-Nr. Drawing No.	BZ00E50000064
Buchst.	Aenderung / Revision		Auftrags-Nr.	Datum/Date	Name				Referenz-Nr./Reference-No.		-----		

Keine Änderung ohne Zustimmung der
federführenden Konstruktion.
Any alterations are subject to the
approval of the design department.

© MTU Friedrichshafen GmbH
Schutzmerk DIN 34 beachten !
Refer to protection notice DIN 34 !

013R001F
RUPLAN

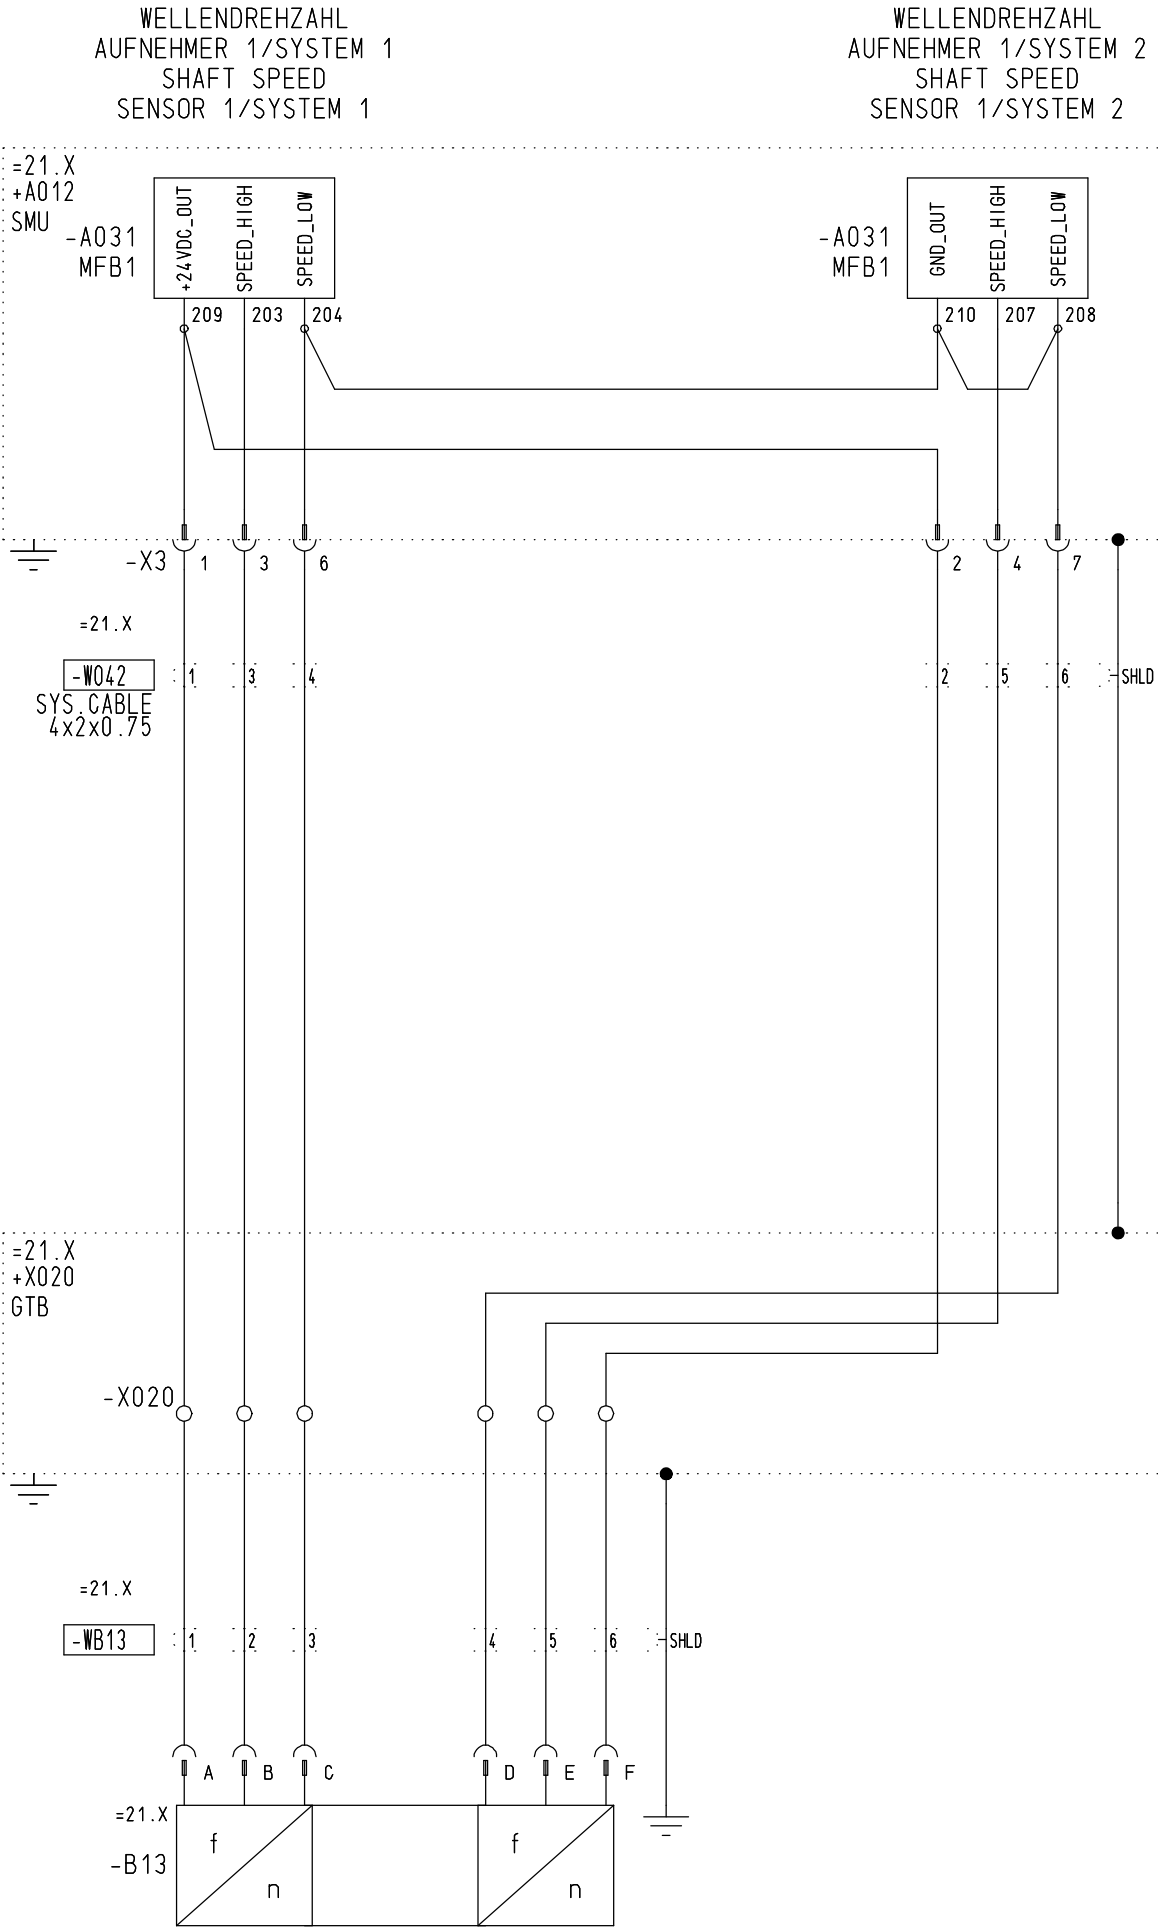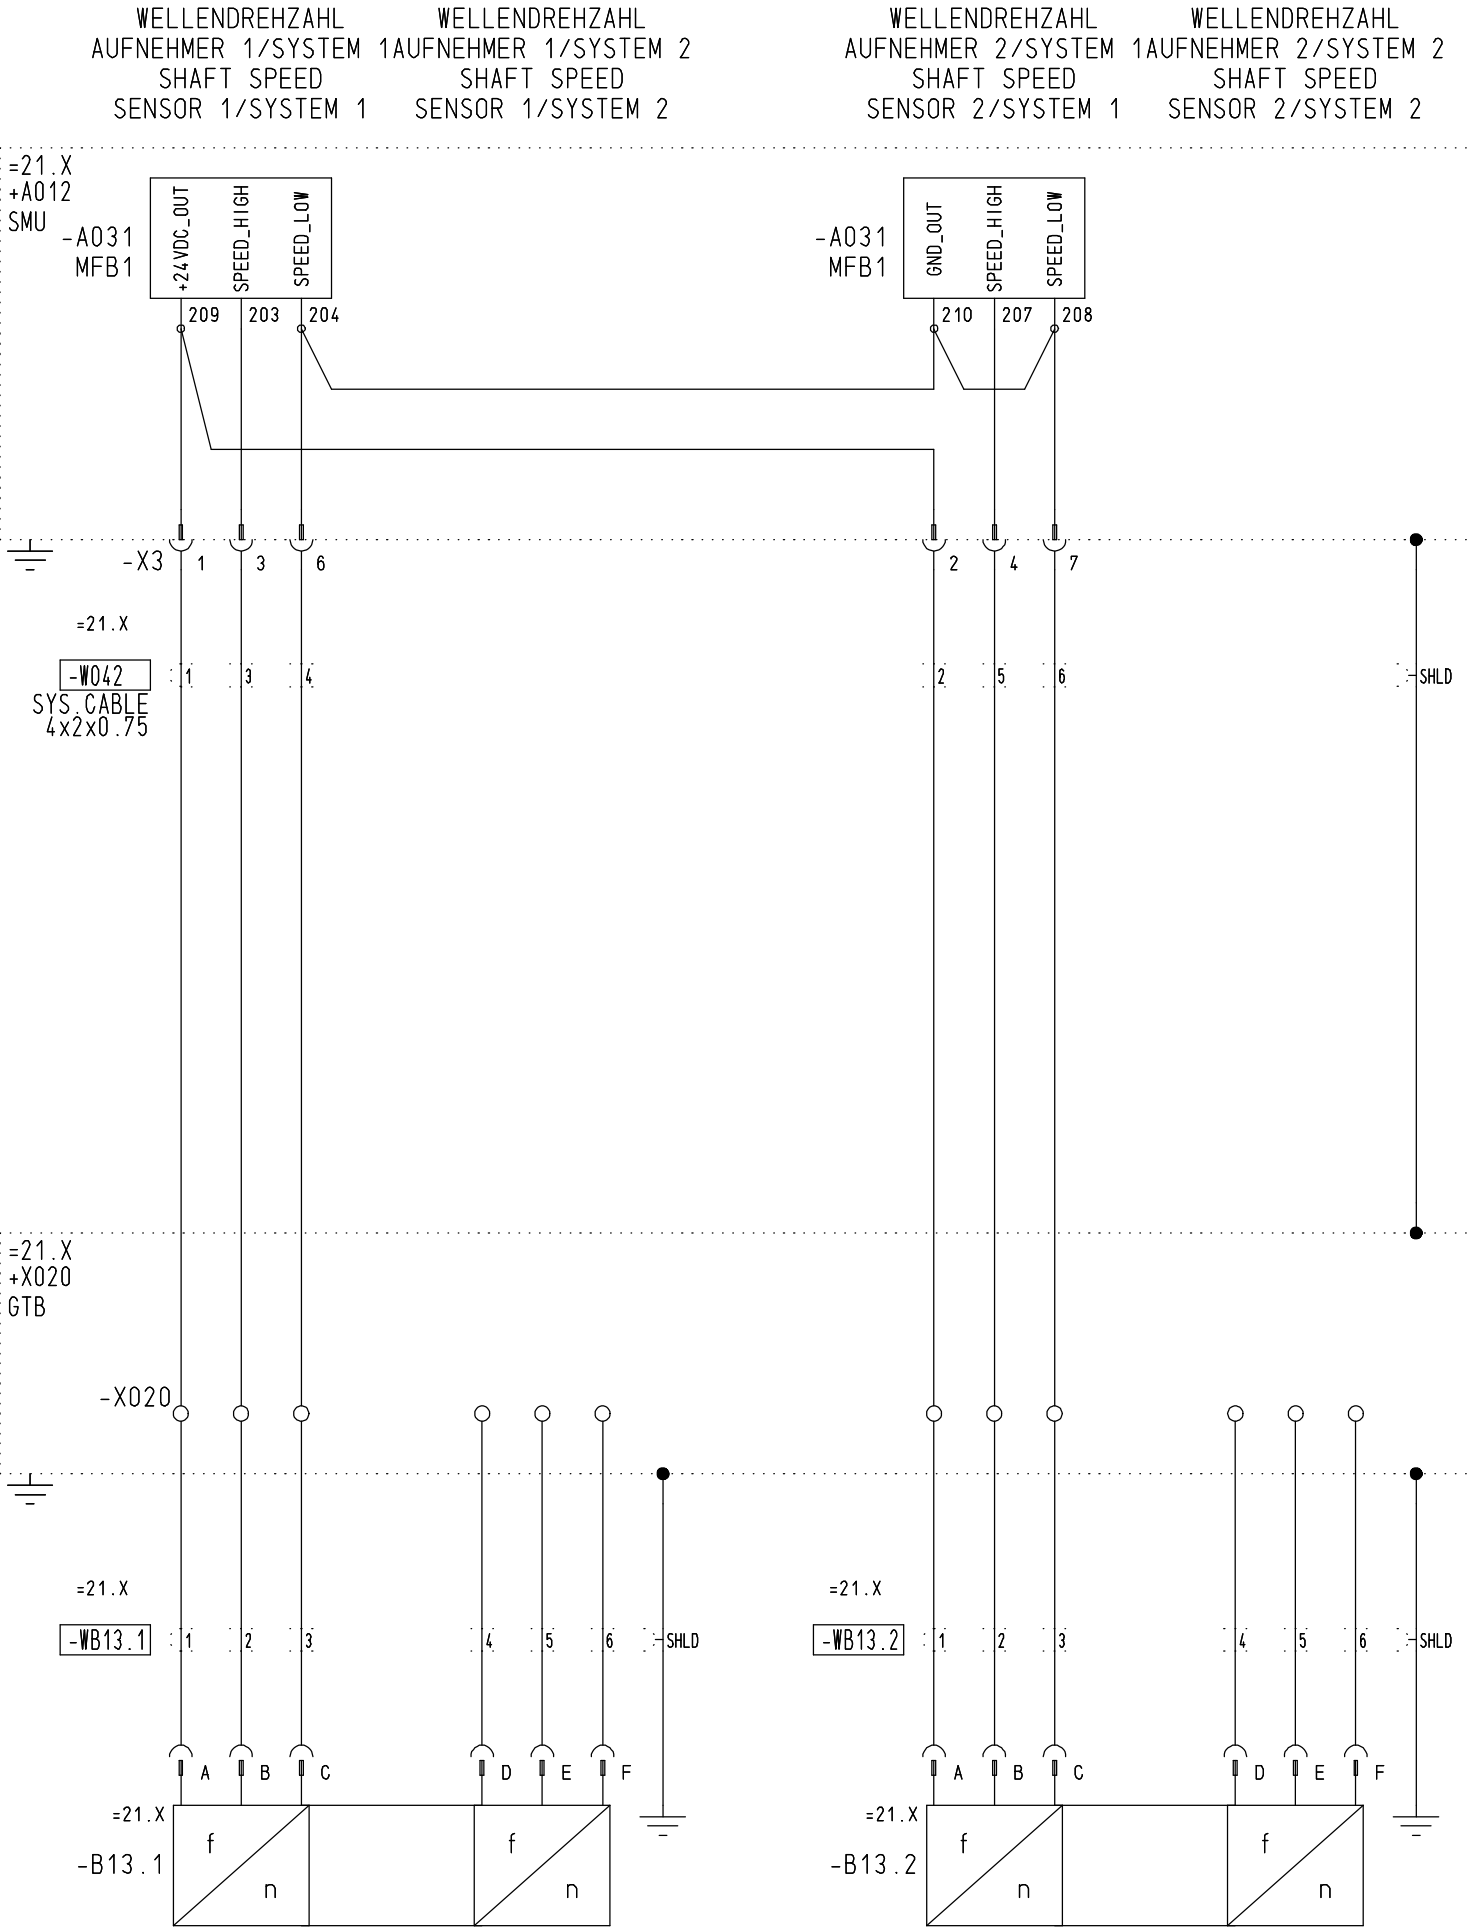

CAD	Datum	Name
Bearb.	21.02.2018	SAUTER
Gepr.	21.02.2018	BOLL
Norm.	21.02.2018	SAUTER
Abt. TEA		




MTU Friedrichshafen GmbH

Benennung/Title
SCHEMA VERKABELUNG
ANLAGENAUTOMATION
WIRING DIAGRAM
PLANT AUTOMATION

ZF GETRIEBE, MAXZFIMALUMFANG, TYP F, WELLENDREHZAHL ZF GEARBOX, MAXZFIMAL SCOPE, TYPE F, SHAFT SPEED		Blatt 115 Sheet 115
Auftrag/ Projekt	BLUE-VIS	
Zeichnungs-Nr. Drawing No. BZ00E50000064		
Referenz-Nr./Reference-No.		

Keine Änderung ohne Zustimmung der
Friedrichshafen Konstruktion.
Any alterations are subject to the
approval of the design department.


© MTU Friedrichshafen GmbH
Schutzvermerk DIN 34 beachten !
Refer to protection notice DIN 34 !

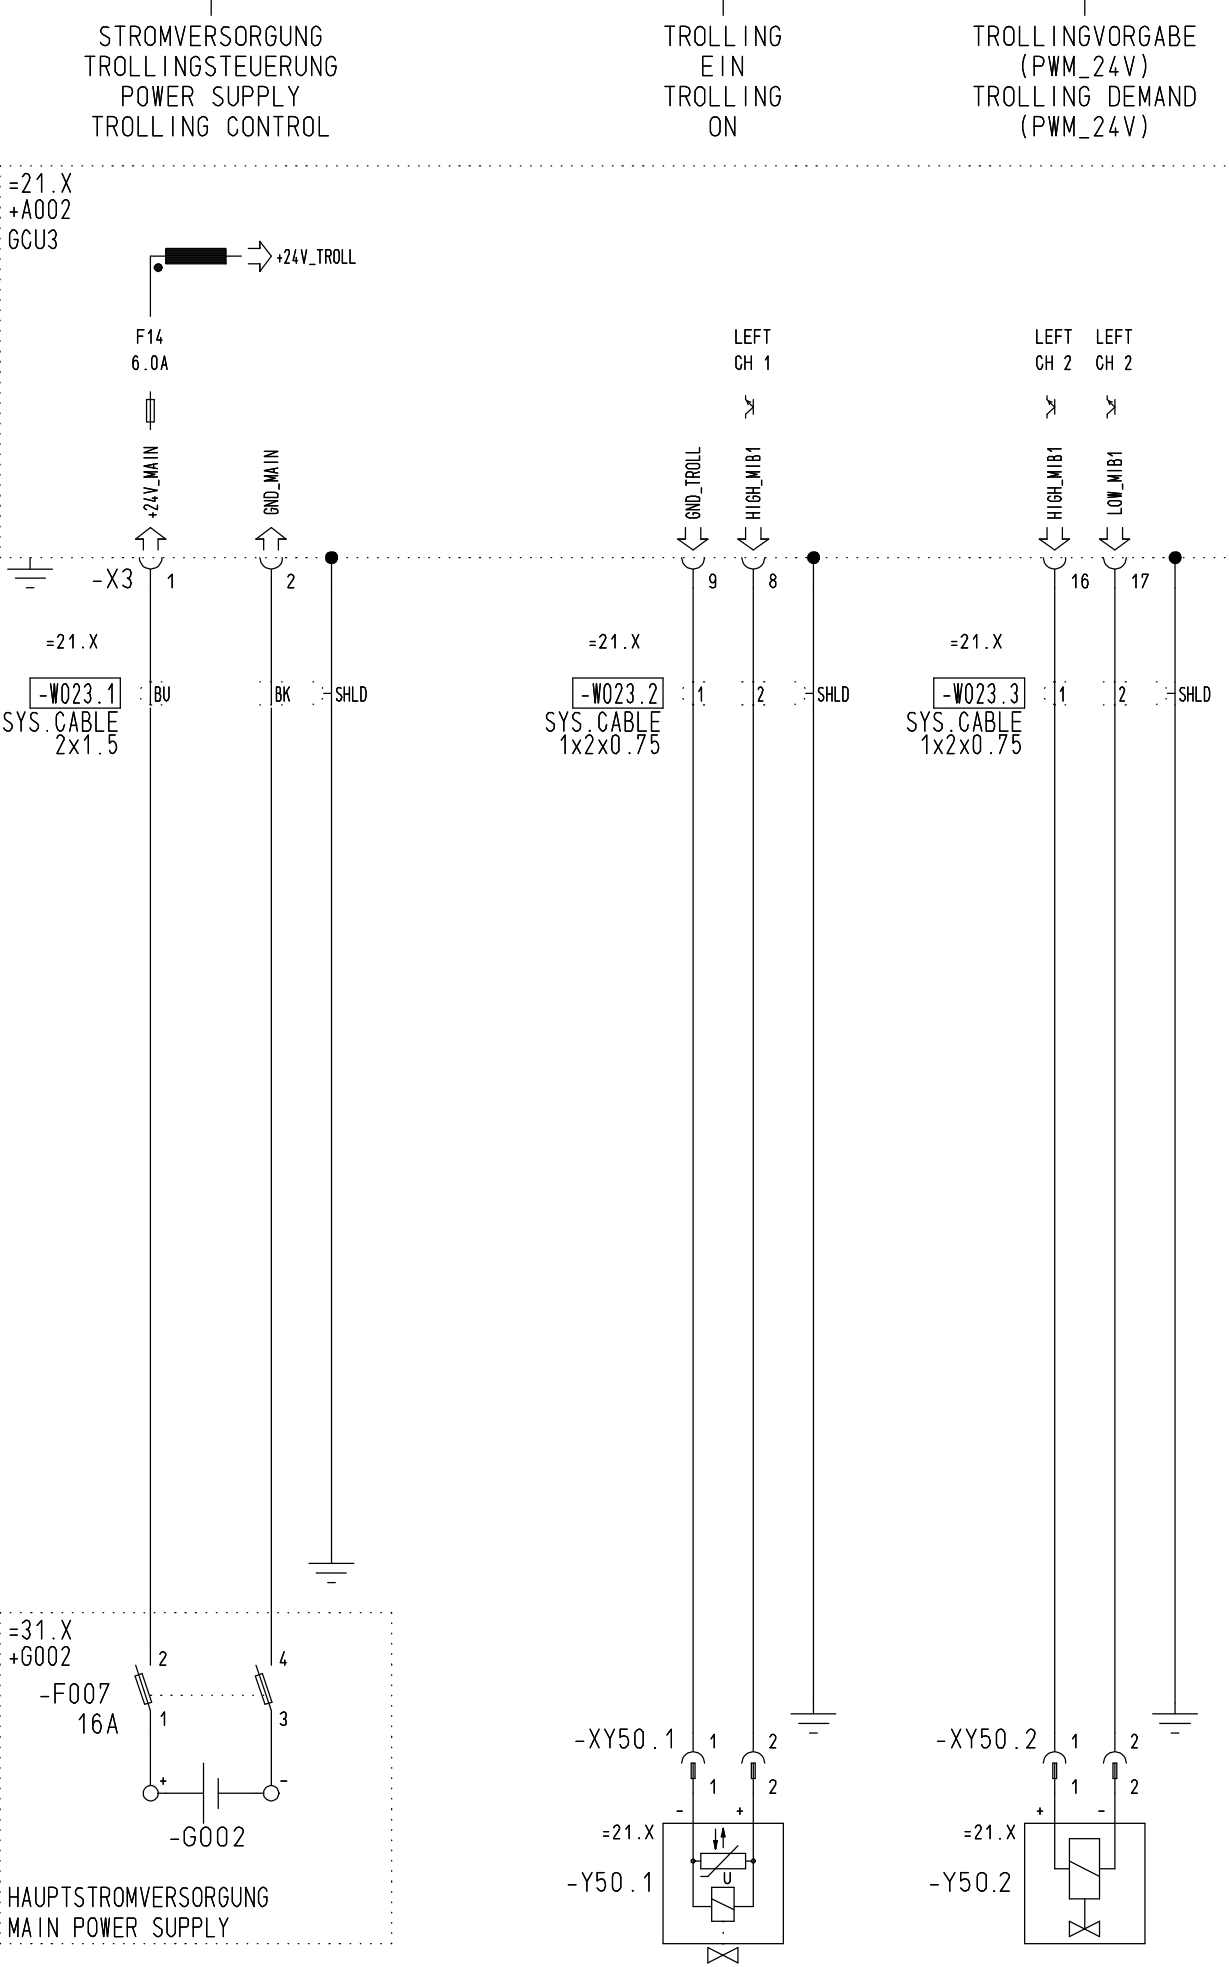

					CAD	Datum	Name	 MTU Friedrichshafen GmbH	Benennung/Title SCHEMA VERKABELUNG ANLAGENAUTOMATION WIRING DIAGRAM PLANT AUTOMATION	ZF GETRIEBE, TROLLINGSTEUERUNG ELEKTRISCH (PWM_24V)					
					Bearb.	21.02.2018	SAUTER			ZF GEARBOX, TROLLING CONTROL ELECTRICAL (PWM_24V)					
					Gepr.	21.02.2018	BOLL								
					Norm.	21.02.2018	SAUTER								
c	Rahmentexte bericht.		Freigegeb.	26.02.2018	Boll					Auftrag/ Projekt	BLUE-VIS	Zeichnungs-Nr. Drawing No.	BZ00E50000064	Blatt Sheet	117
Buchst.	Änderung / Revision		Auftrags-Nr.	Datum/Date	Name	Abt. TEA				Referenz-Nr./Reference-No.		-----			

Keine Änderung ohne Zustimmung der
federführenden Konstruktion.
Any alterations are subject to the
approval of the design department.

© MTU Friedrichshafen GmbH
Schutzvermerk DIN 34 beachten !
Refer to protection notice DIN 34 !

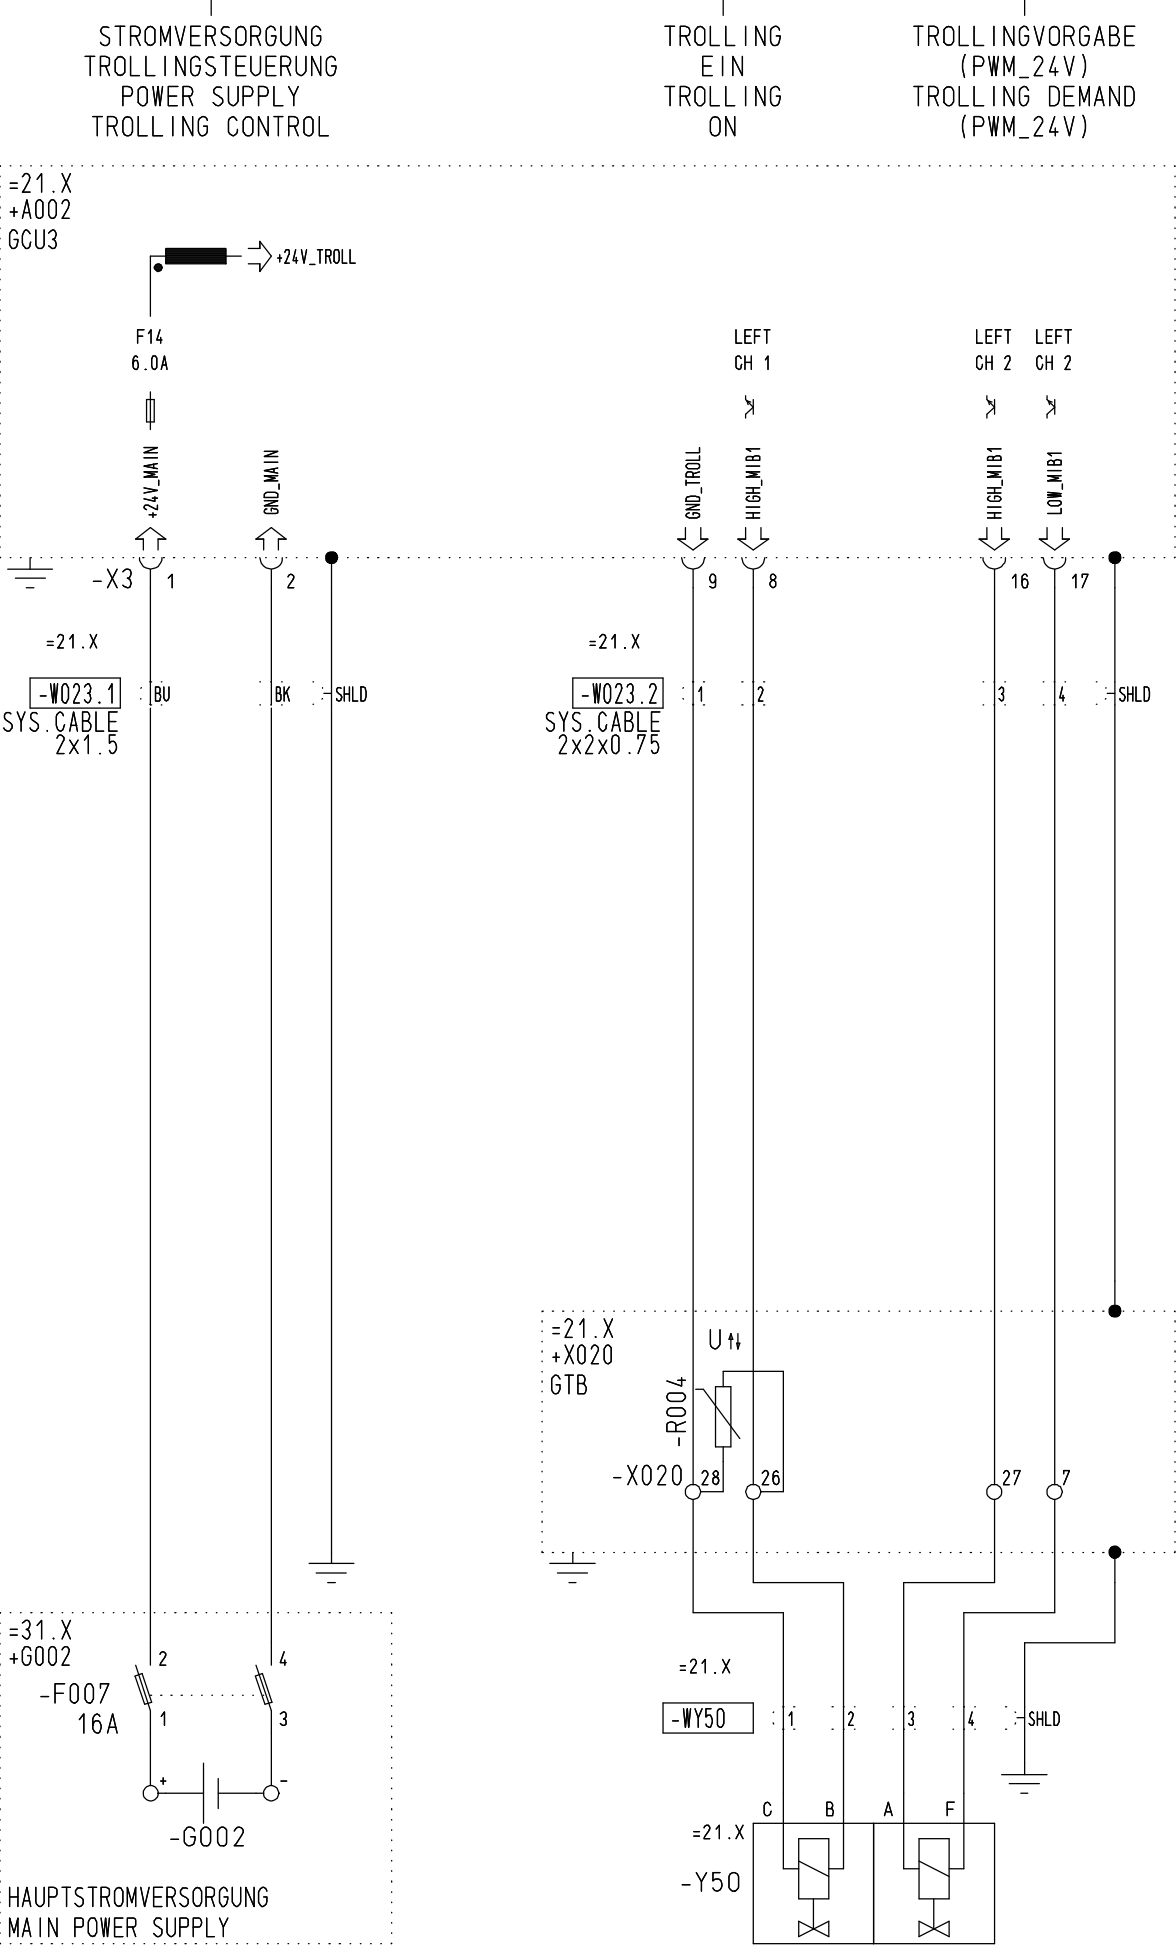

					CAD	Datum	Name
					Bearb.	21.02.2018	SAUTER
					Gepr.	21.02.2018	BOLL
c	Rahmentexte bericht.	Freigegeb.	26.02.2018	Boll	Norm.	21.02.2018	SAUTER
Buchst.	Aenderung / Revision	Auftrags-Nr.	Datum/Date	Name	Abt. TEA		



MTU Friedrichshafen GmbH

Benennung/Title
SCHEMA VERKABELUNG
ANLAGENAUTOMATION
WIRING DIAGRAM
PLANT AUTOMATION

ZF GETRIEBE, TROLLINGSTEUERUNG ELEKTRISCH (PWM_24V)		ZF GEARBOX, TROLLING CONTROL ELECTRICAL (PWM_24V)	
Auftrag/Projekt		Zeichnungs-Nr. / Drawing No.	
BLUE-VIS		BZ00E50000064	
Referenz-Nr./Reference-No.		-----	
Blatt 118		Sheet 118	

Keine Änderung ohne Zustimmung der
federführenden Konstruktion.
Any alterations are subject to the
approval of the design department.

© MTU Friedrichshafen GmbH
Schutzvermerk DIN 34 beachten !
Refer to protection notice DIN 34 !

					CAD	Datum	Name
					Bearb.	21.02.2018	SAUTER
					Gepr.	21.02.2018	BOLL
					Norm.	21.02.2018	SAUTER
c	Rahmentexte bericht.	Freigegeb.	26.02.2018	Boll	Abt. TEA		
Buchst.	Änderung / Revision	Auftrags-Nr.	Datum/Date	Name			



MTU Friedrichshafen GmbH

Benennung/Title
SCHEMA VERKABELUNG
ANLAGENAUTOMATION
WIRING DIAGRAM
PLANT AUTOMATION


ZF GETRIEBE, TROLLINGSTEUERUNG MECH./ELEKTR. (PWM_12V)
ZF GEARBOX, TROLLING CONTROL MECH./ELECTR. (PWM_12V)

Auftrag/Projekt BLUE-VIS
Zeichnungs-Nr. BZ00E50000064
Drawing No.


Blatt 119
Sheet


Keine Änderung ohne Zustimmung der
federführenden Konstruktion.
Any alterations are subject to the
approval of the design department.


© MTU Friedrichshafen GmbH
Schutzvermerk DIN 34 beachten !
Refer to protection notice DIN 34 !

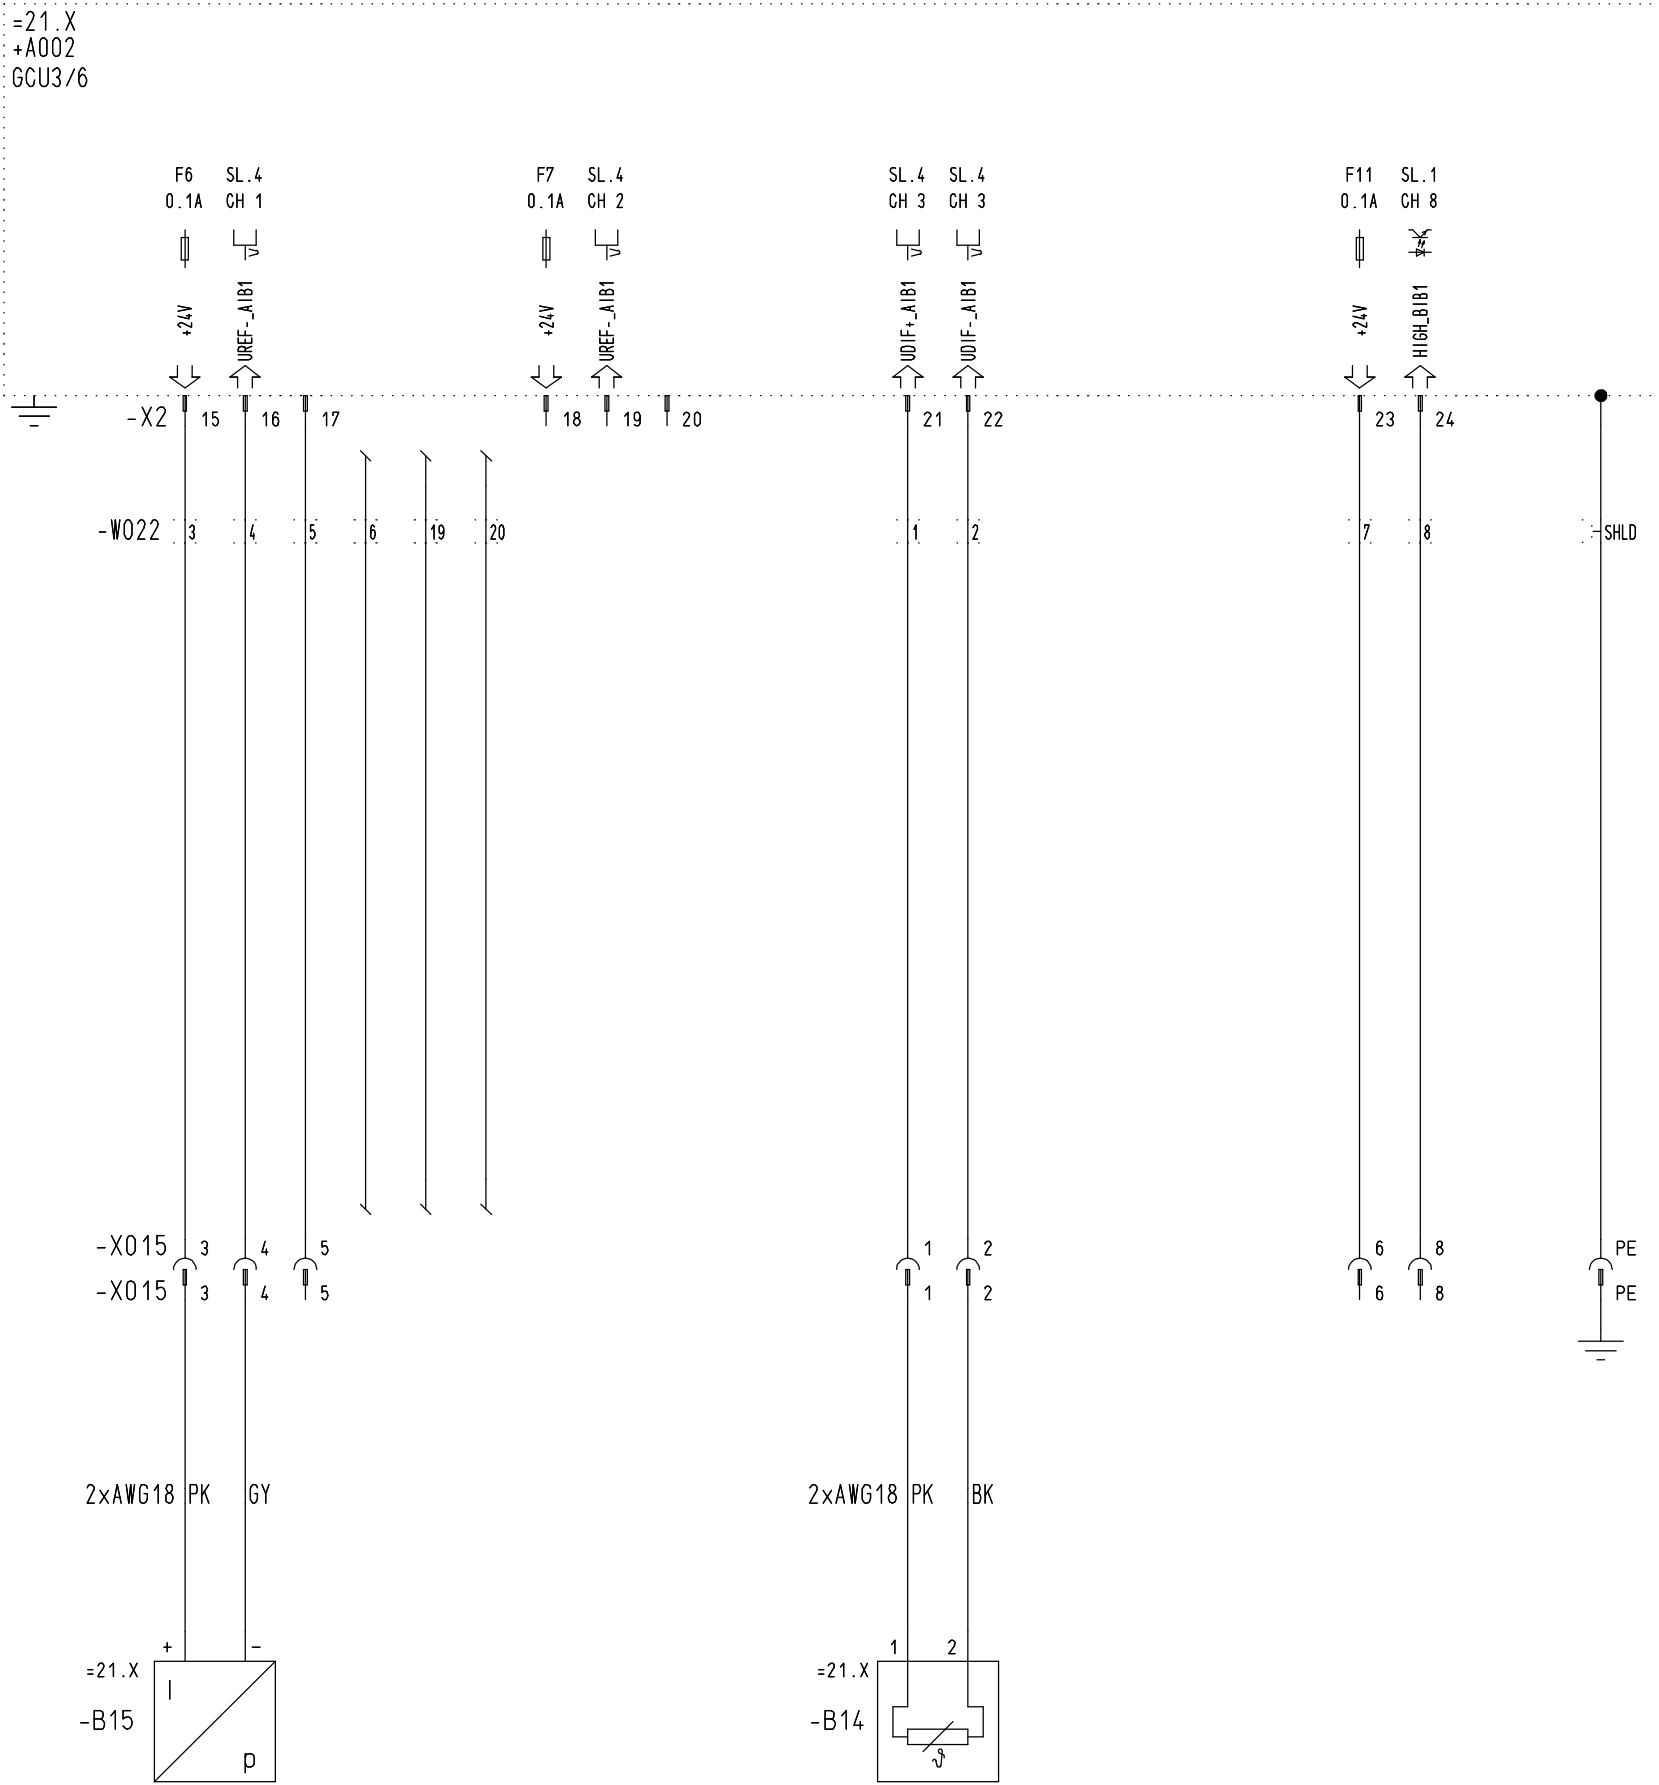

					CAD	Datum	Name	 MTU Friedrichshafen GmbH	Benennung/Title SCHEMA VERKABELUNG ANLAGENAUTOMATION WIRING DIAGRAM PLANT AUTOMATION	TWIN DISC GETRIEBE, MIT WENDETEIL, TYP D(GR.1), GRUNDUMFANG					
					Bearb.	21.02.2018	SAUTER			TWIN DISC GEARBOX, WITH REVERSING, TYPE D(GR.1), BASIC SCOPE					
					Gepr.	21.02.2018	BOLL								
					Norm.	21.02.2018	SAUTER								
c	Rahmentexte bericht.	Freigegeb.	26.02.2018	Boll						Auftrag/ Projekt	BLUE-VIS	Zeichnungs-Nr. Drawing No.	BZ00E50000064	Blatt Sheet	123
Buchst.	Aenderung / Revision	Auftrags-Nr.	Datum/Date	Name	Abt. TEA					Referenz-Nr./Reference-No.		-----			

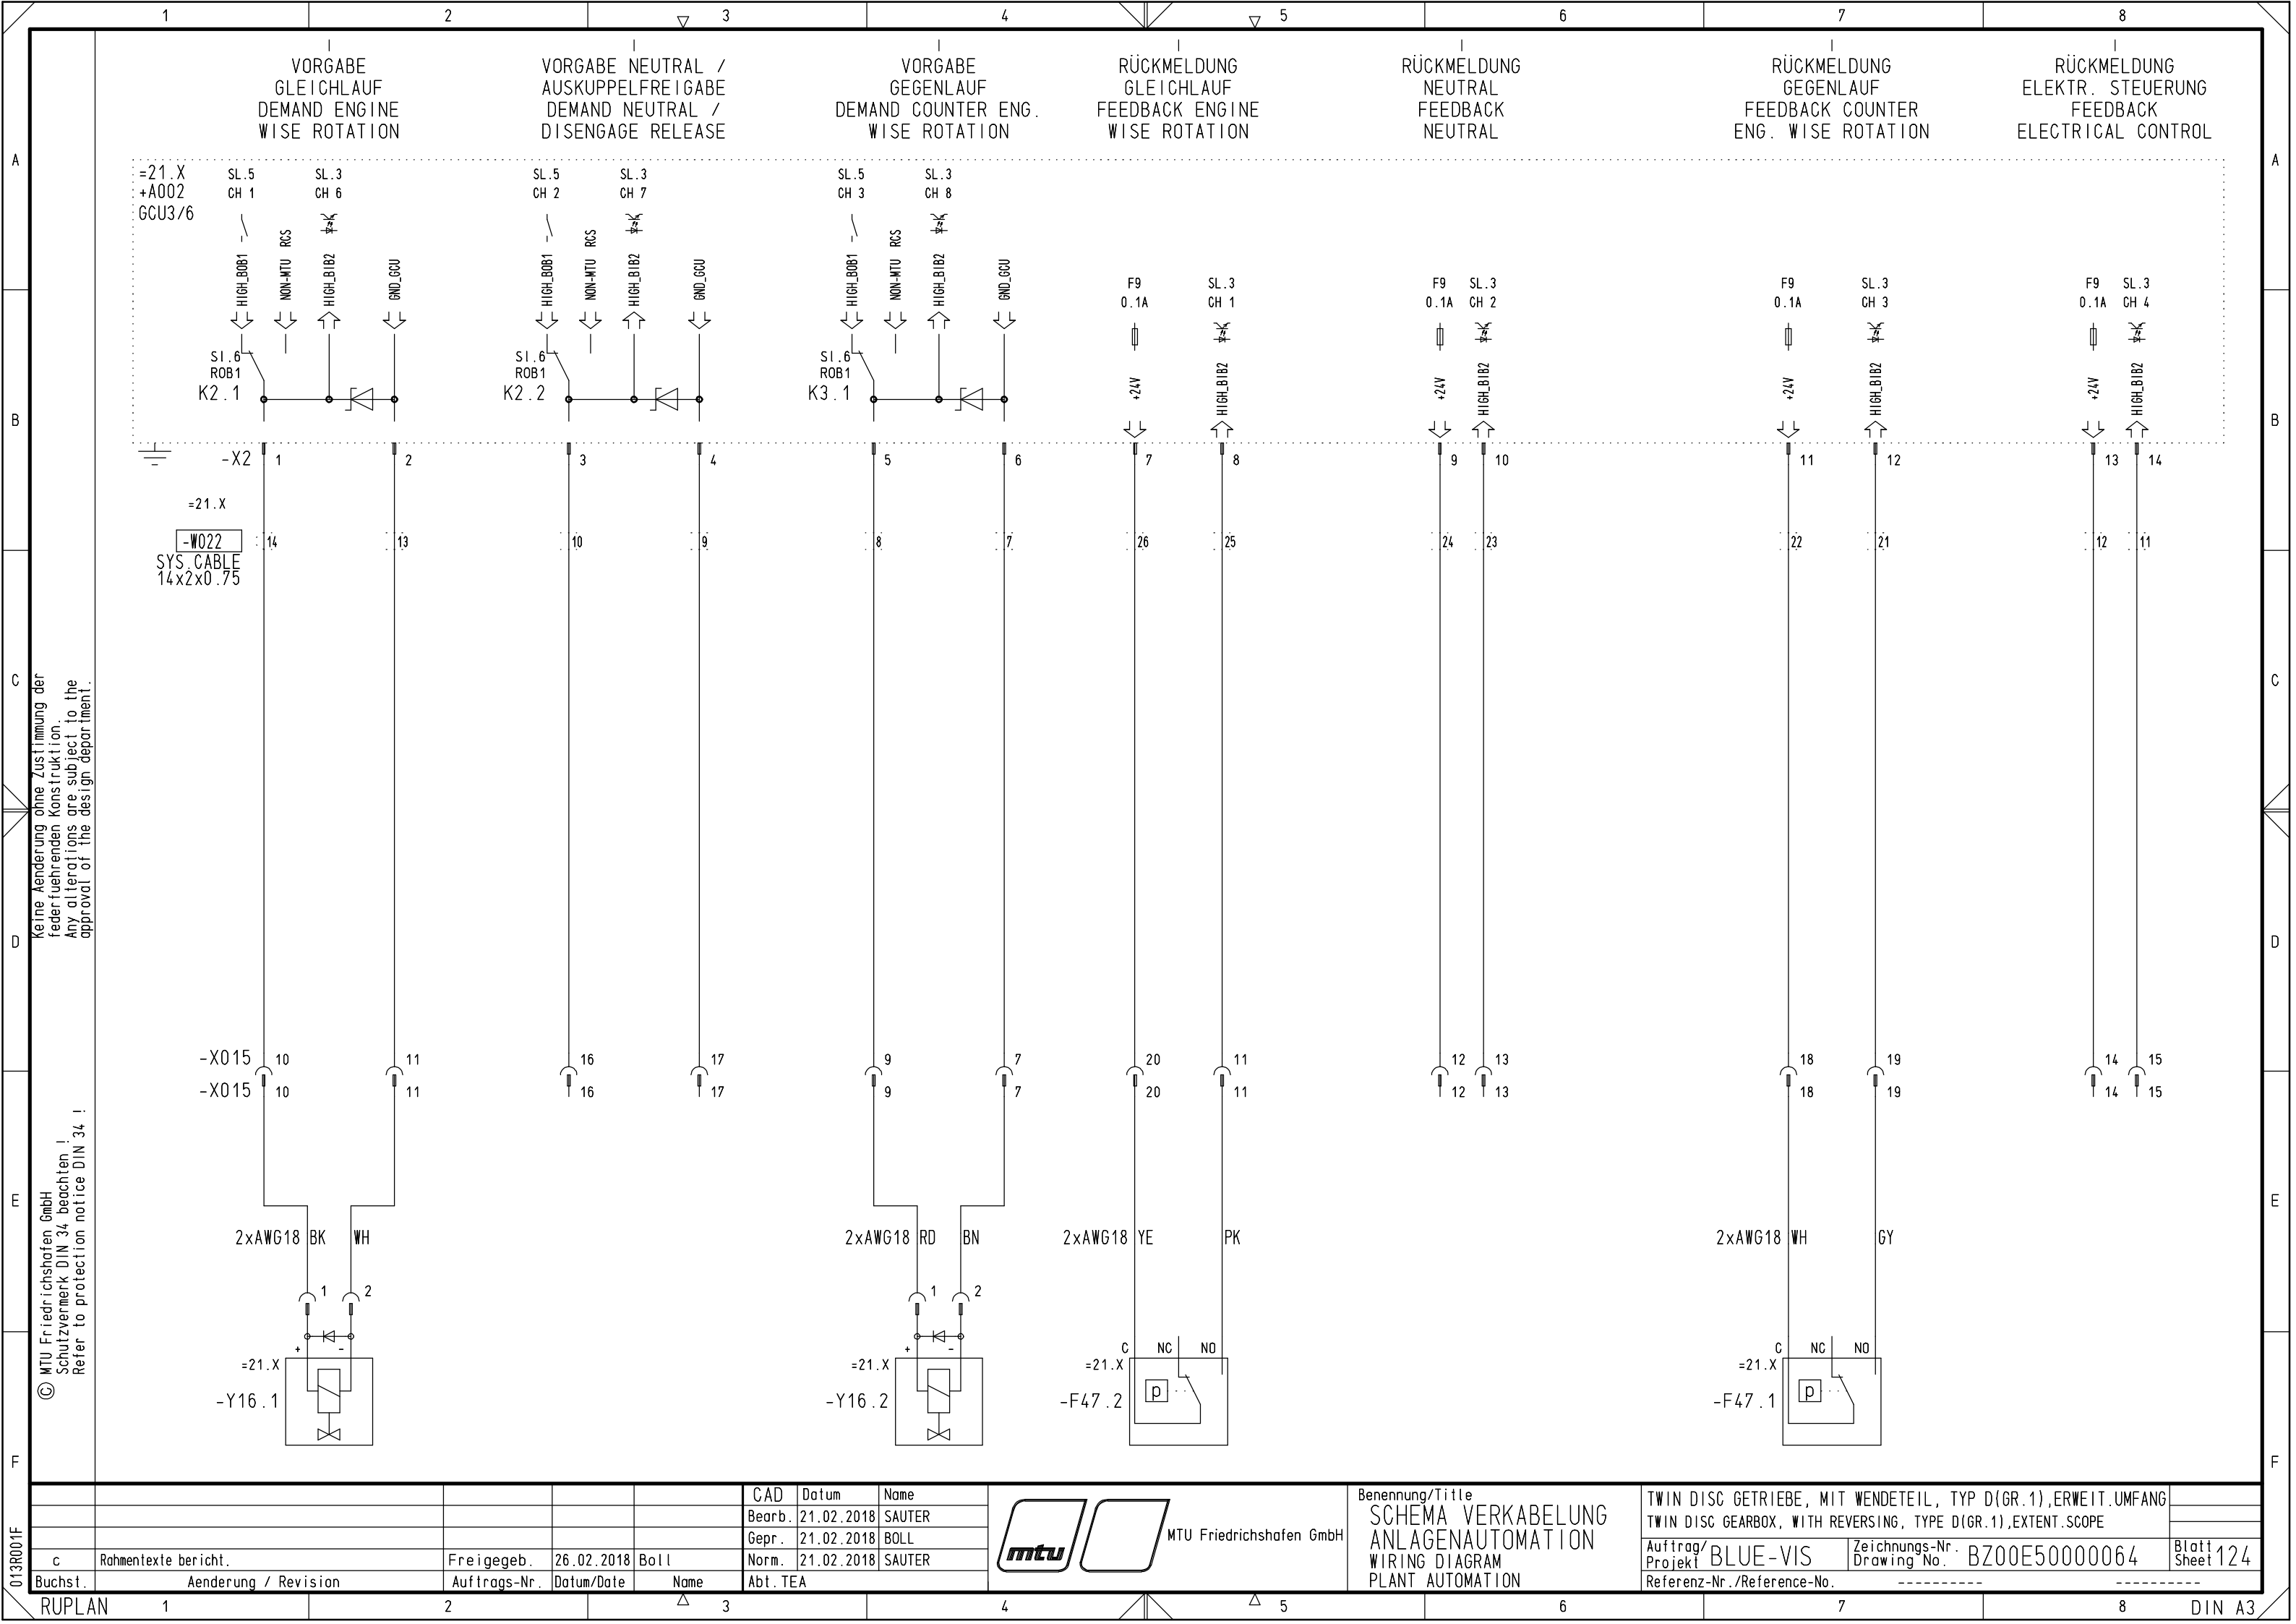


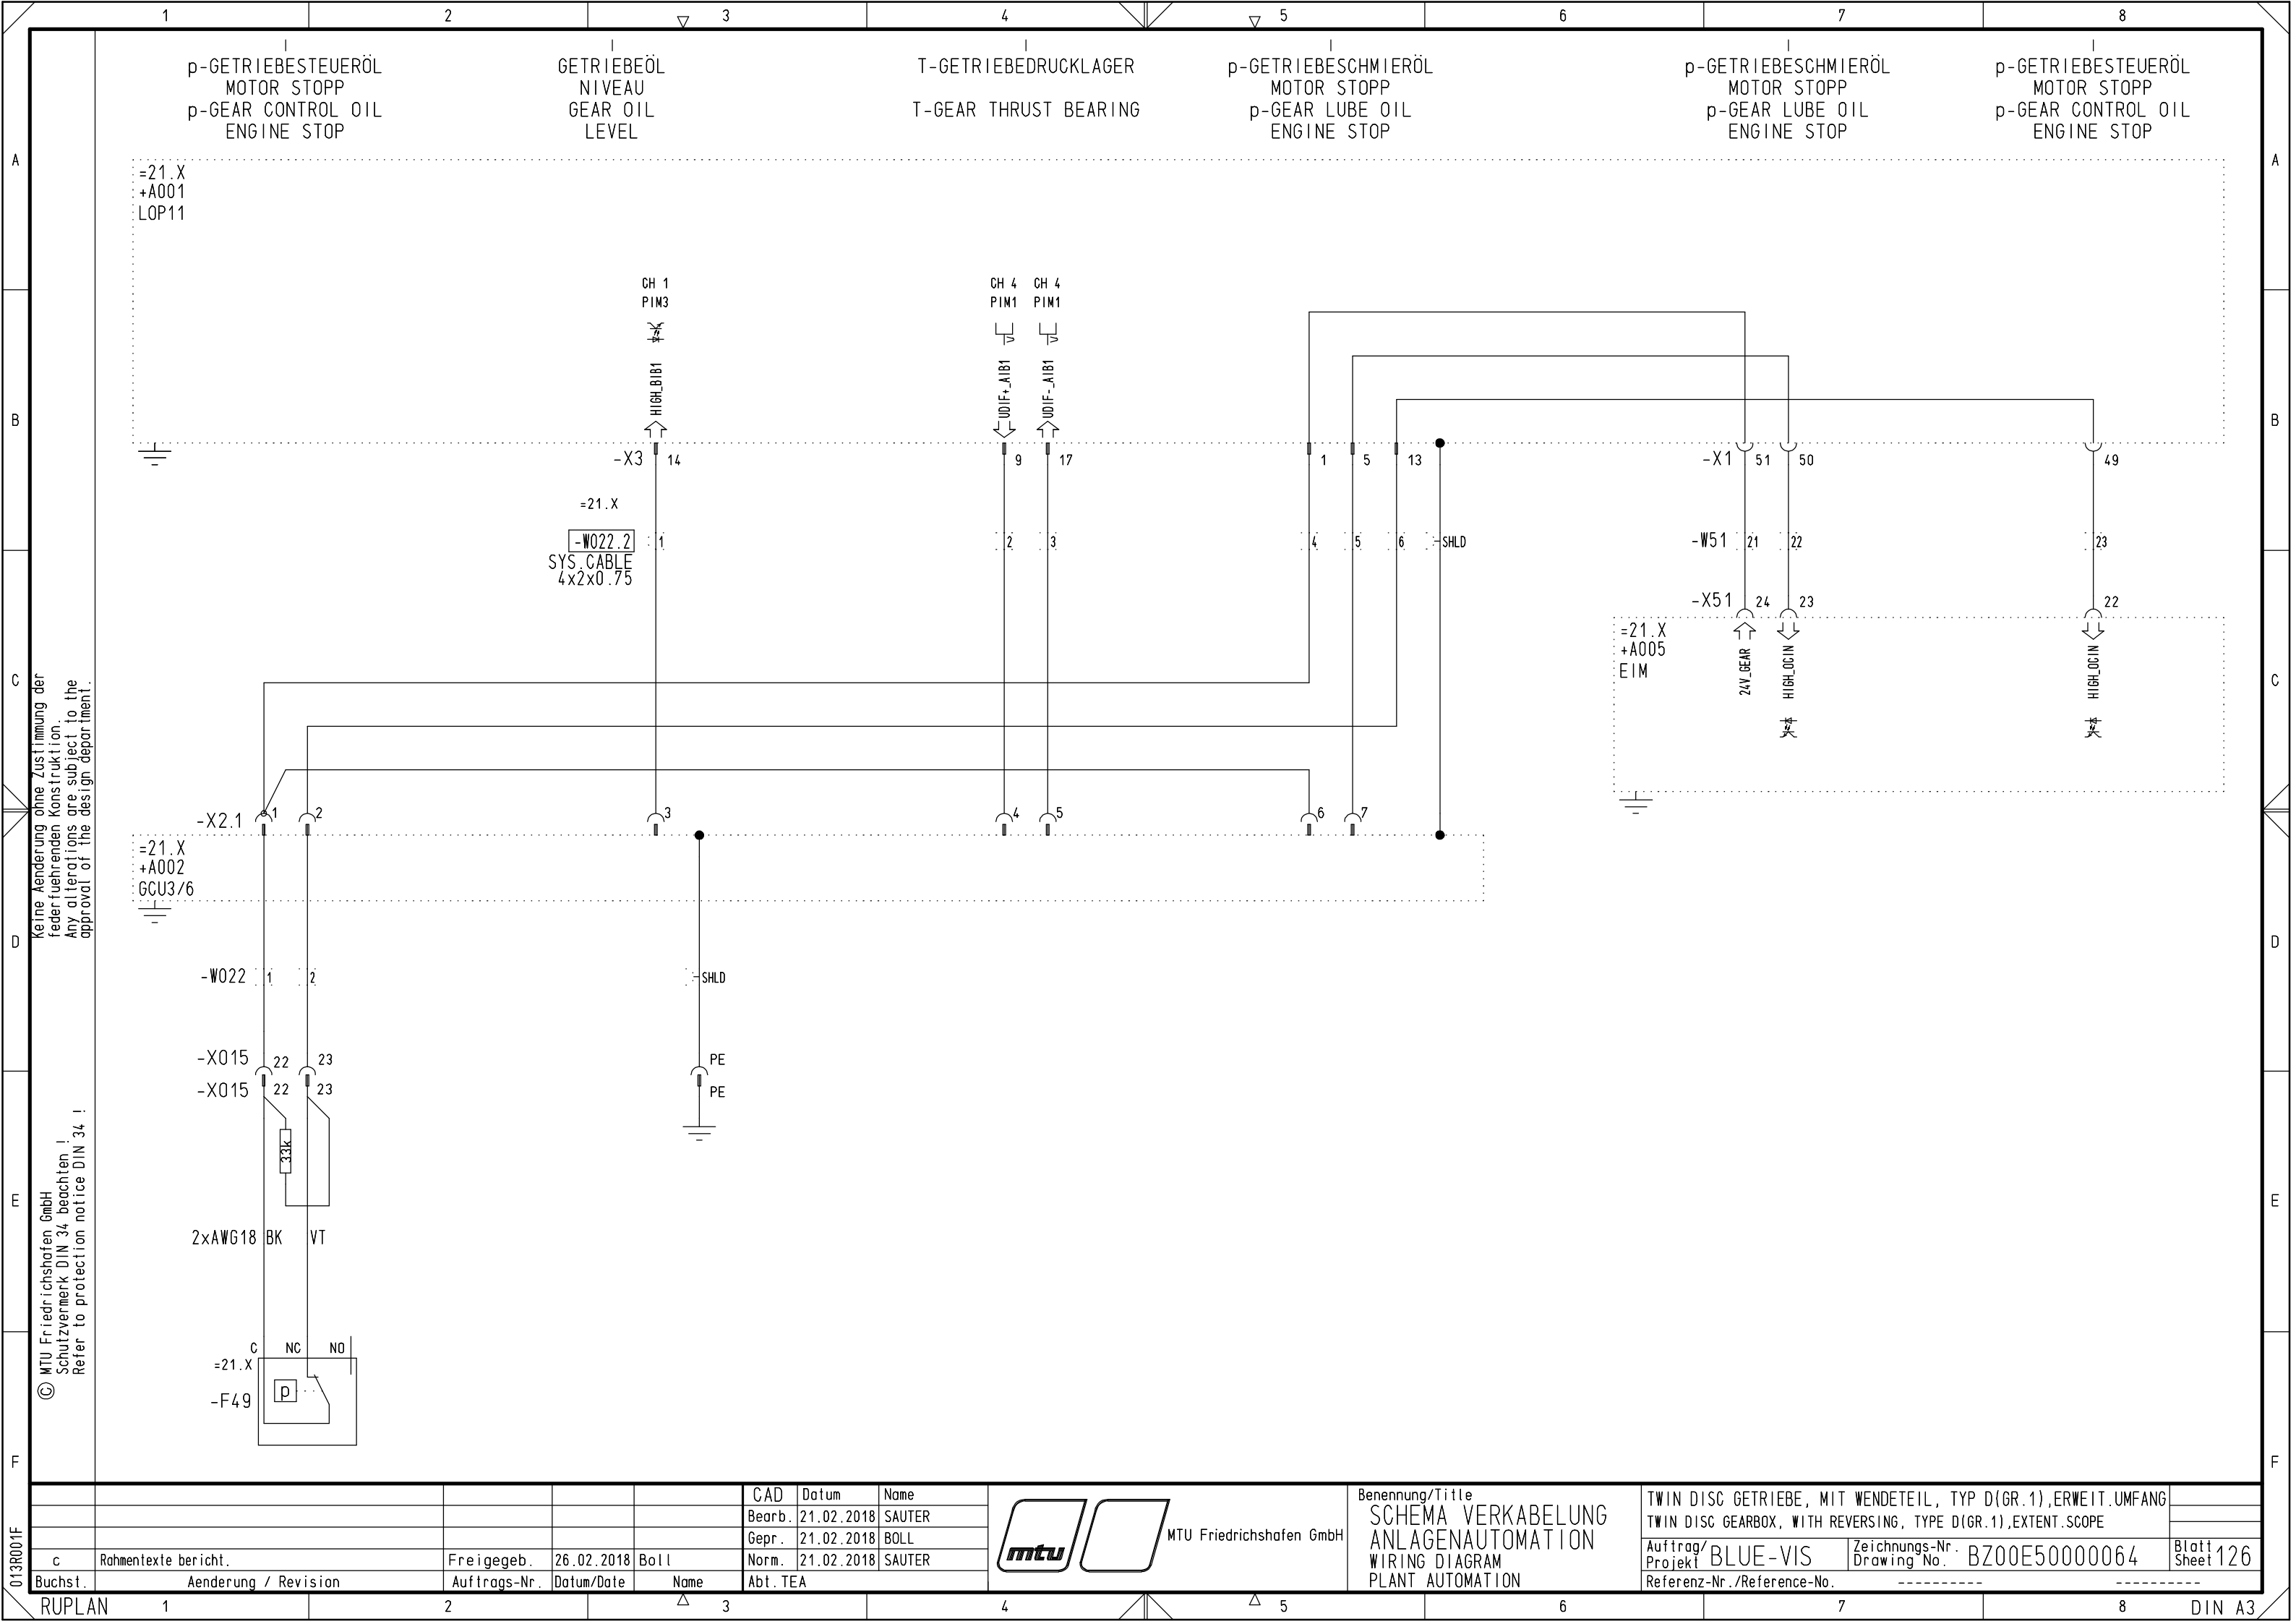

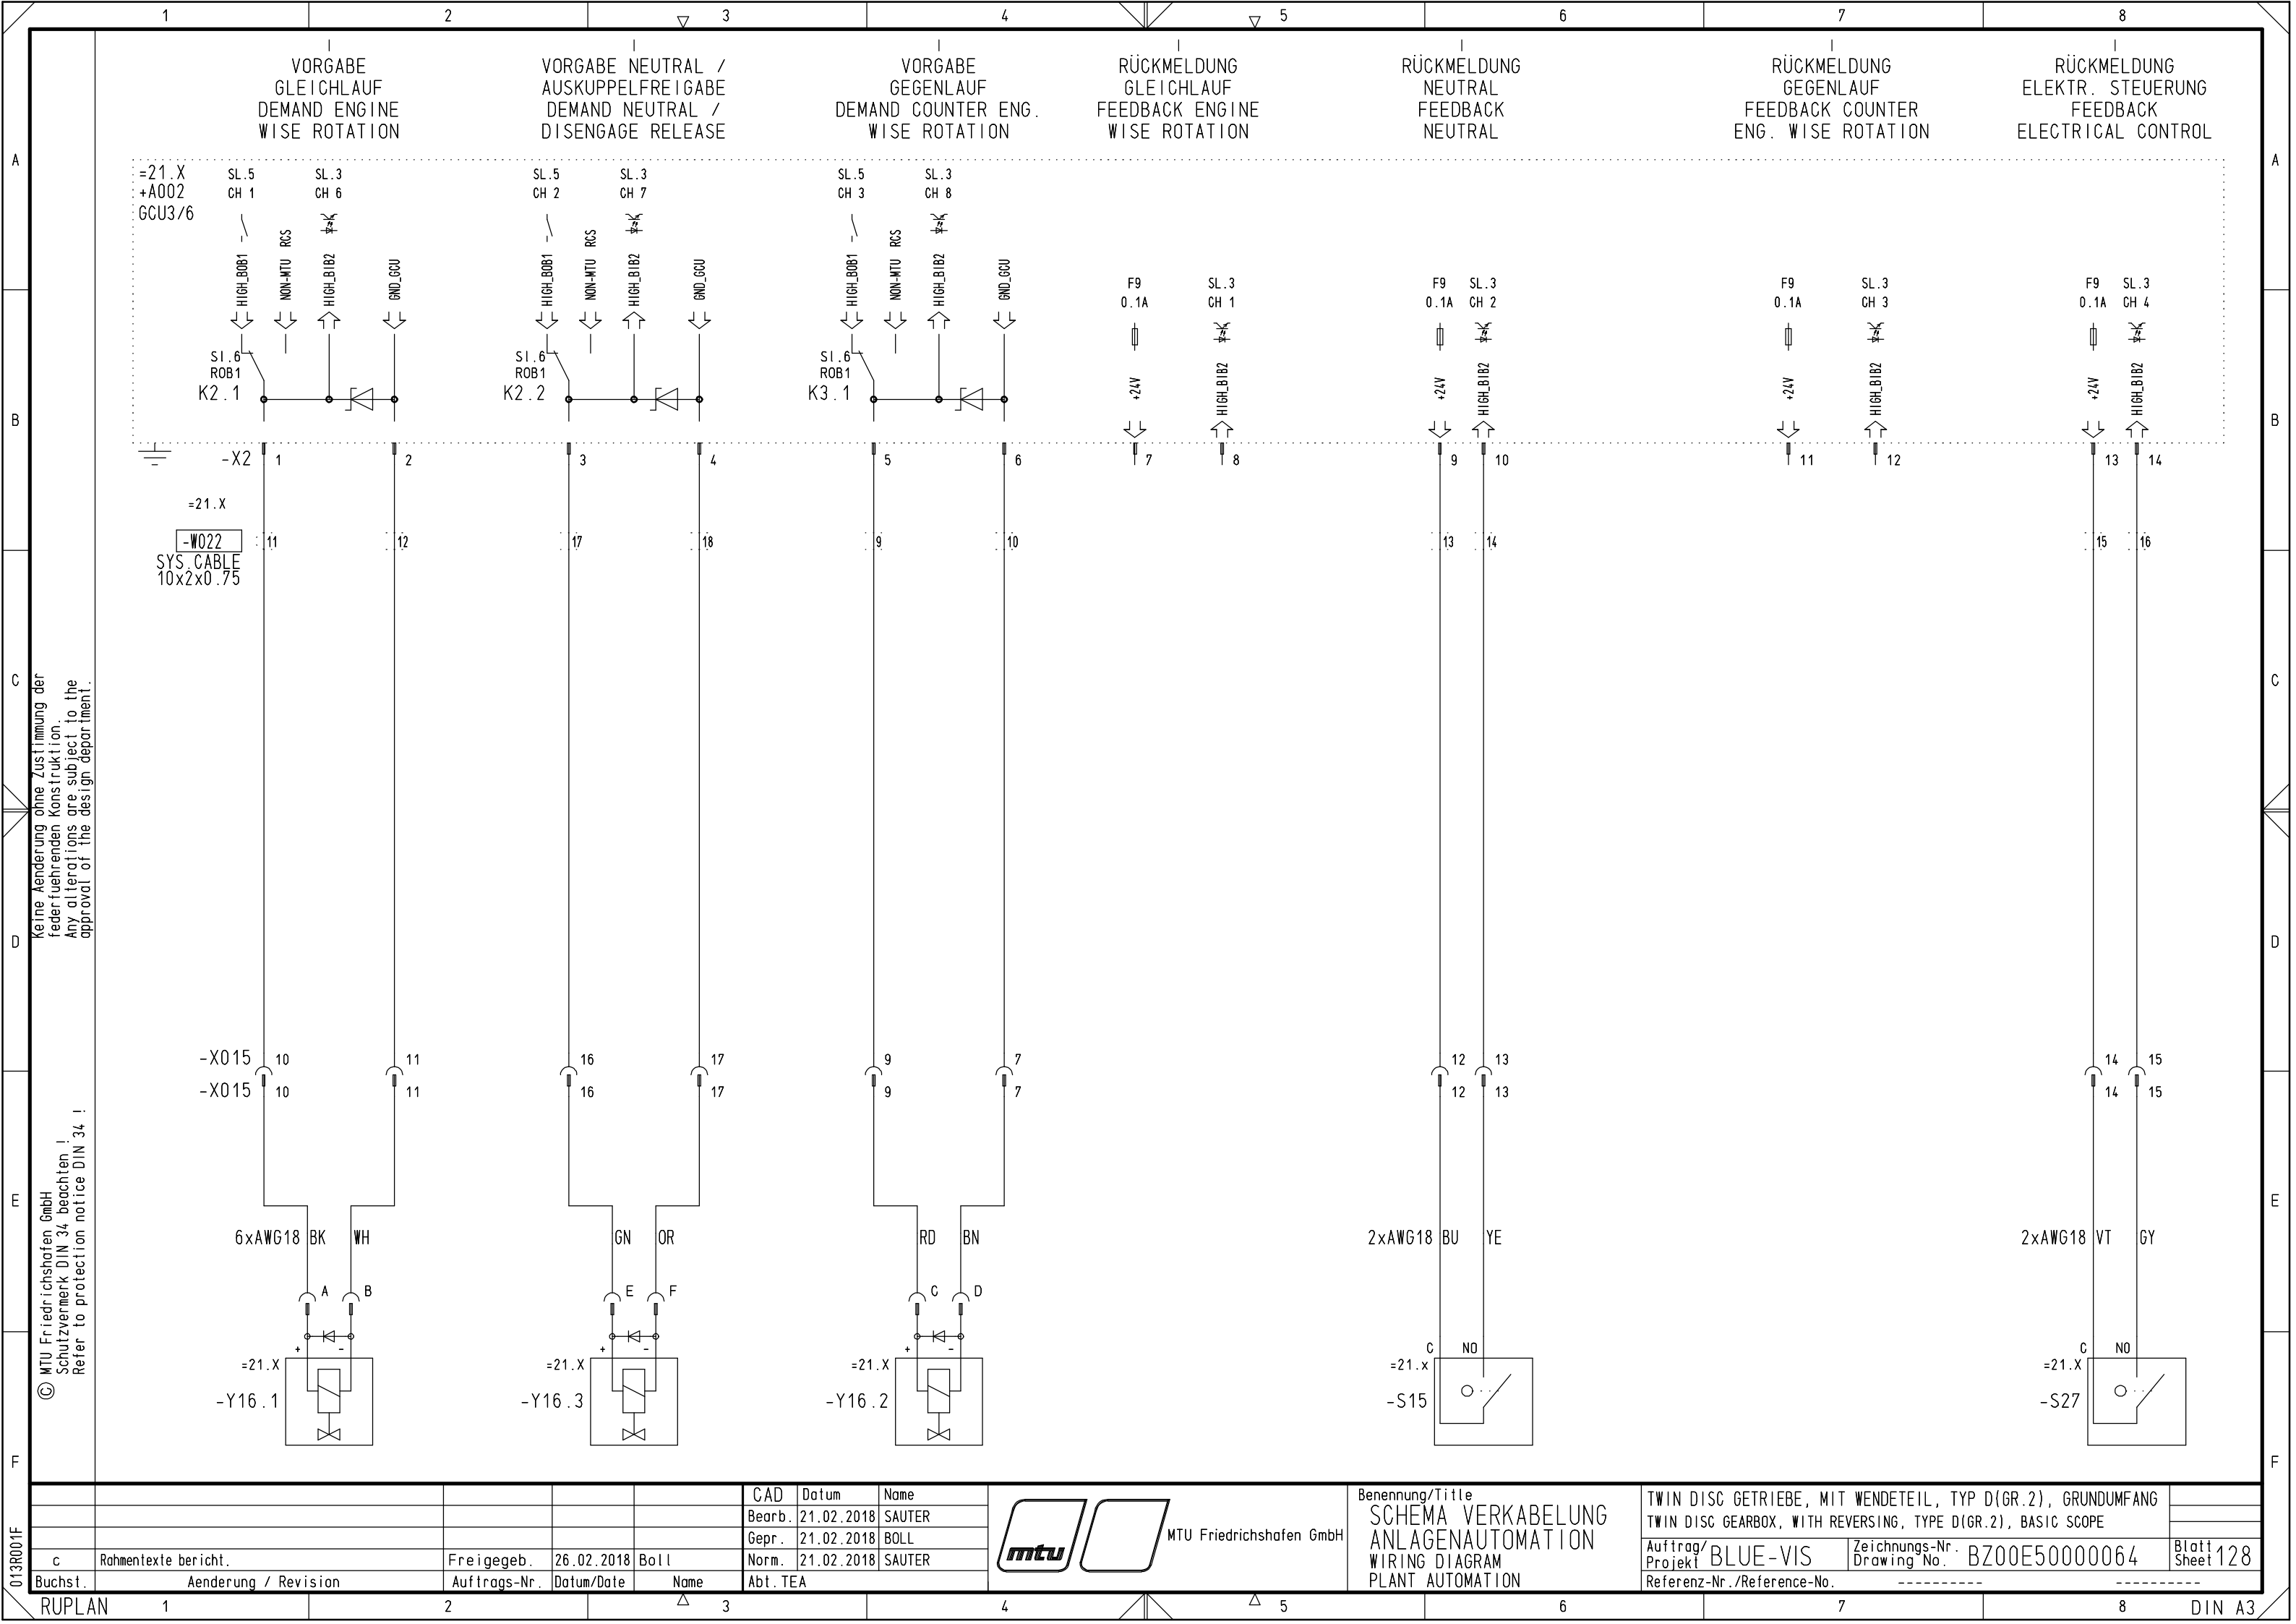

Keine Änderung ohne Zustimmung der
federführenden Konstruktion.
Any alterations are subject to the
approval of the design department.

© MTU Friedrichshafen GmbH
Schutzvermerk DIN 34 beachten !
Refer to protection notice DIN 34 !

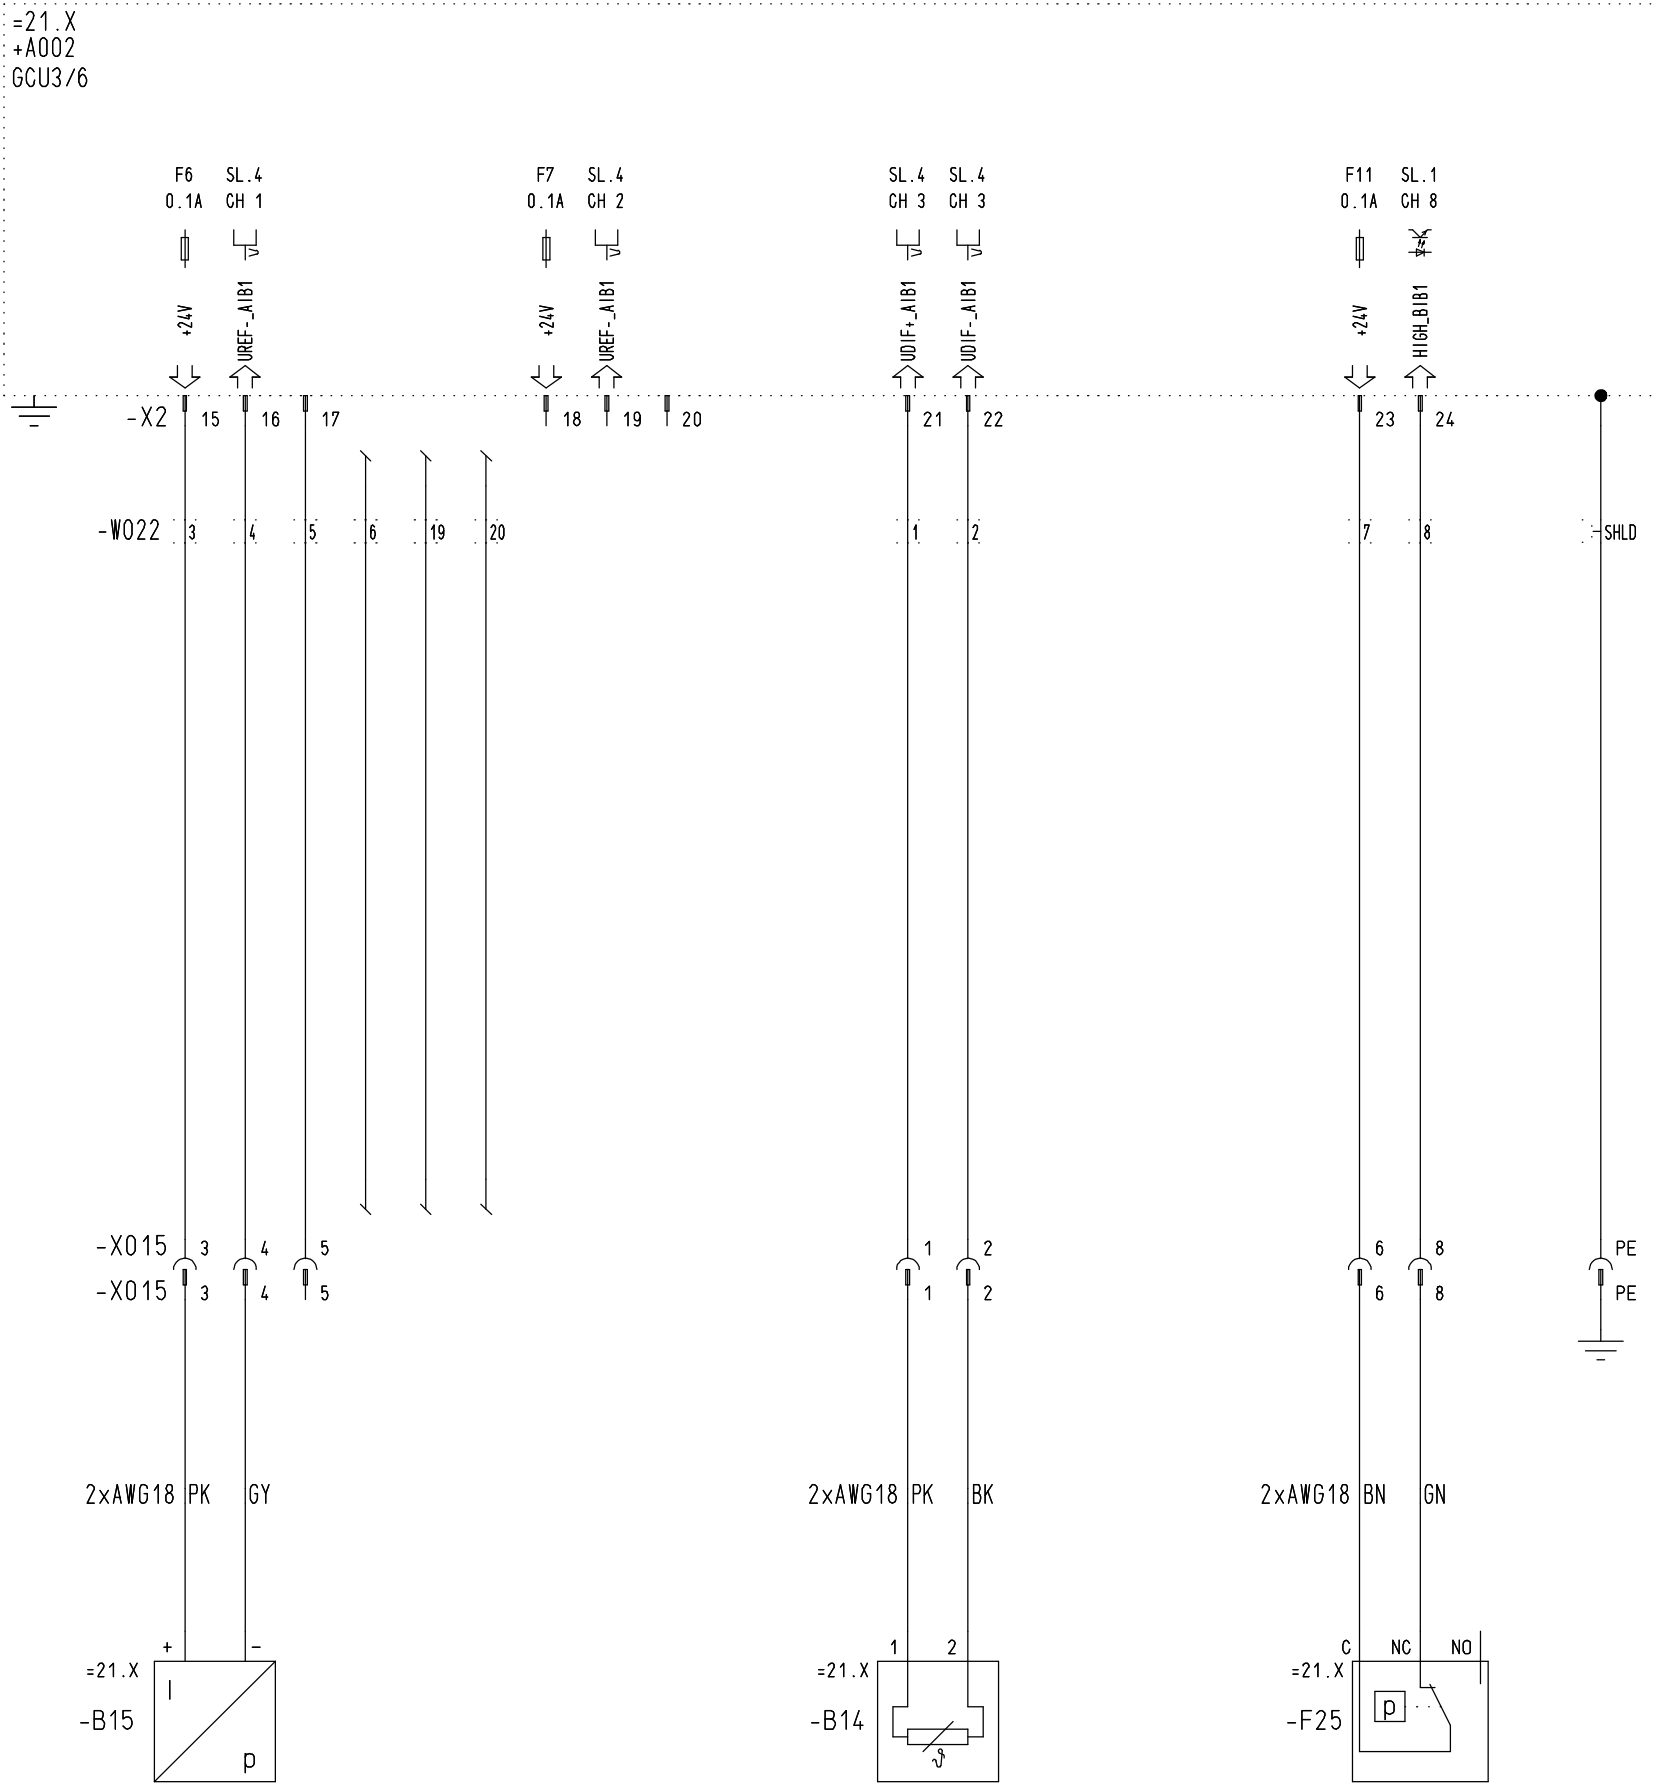

					CAD	Datum	Name
					Bearb.	21.02.2018	SAUTER
					Gepr.	21.02.2018	BOLL
					Norm.	21.02.2018	SAUTER
Buchst.	Aenderung / Revision	Auftrags-Nr.	Datum/Date	Name	Abt. TEA		





MTU Friedrichshafen GmbH

Benennung/Title
SCHEMA VERKABELUNG
ANLAGENAUTOMATION
WIRING DIAGRAM
PLANT AUTOMATION

TWIN DISC GETRIEBE, MIT WENDETEIL, TYP D(GR.2), GRUNDUMFANG
TWIN DISC GEARBOX, WITH REVERSING, TYPE D(GR.2), BASIC SCOPE
Auftrag/Projekt BLUE-VIS
Zeichnungs-Nr. BZ00E50000064
Referenz-Nr./Reference-No. -----

Blatt 129
Sheet

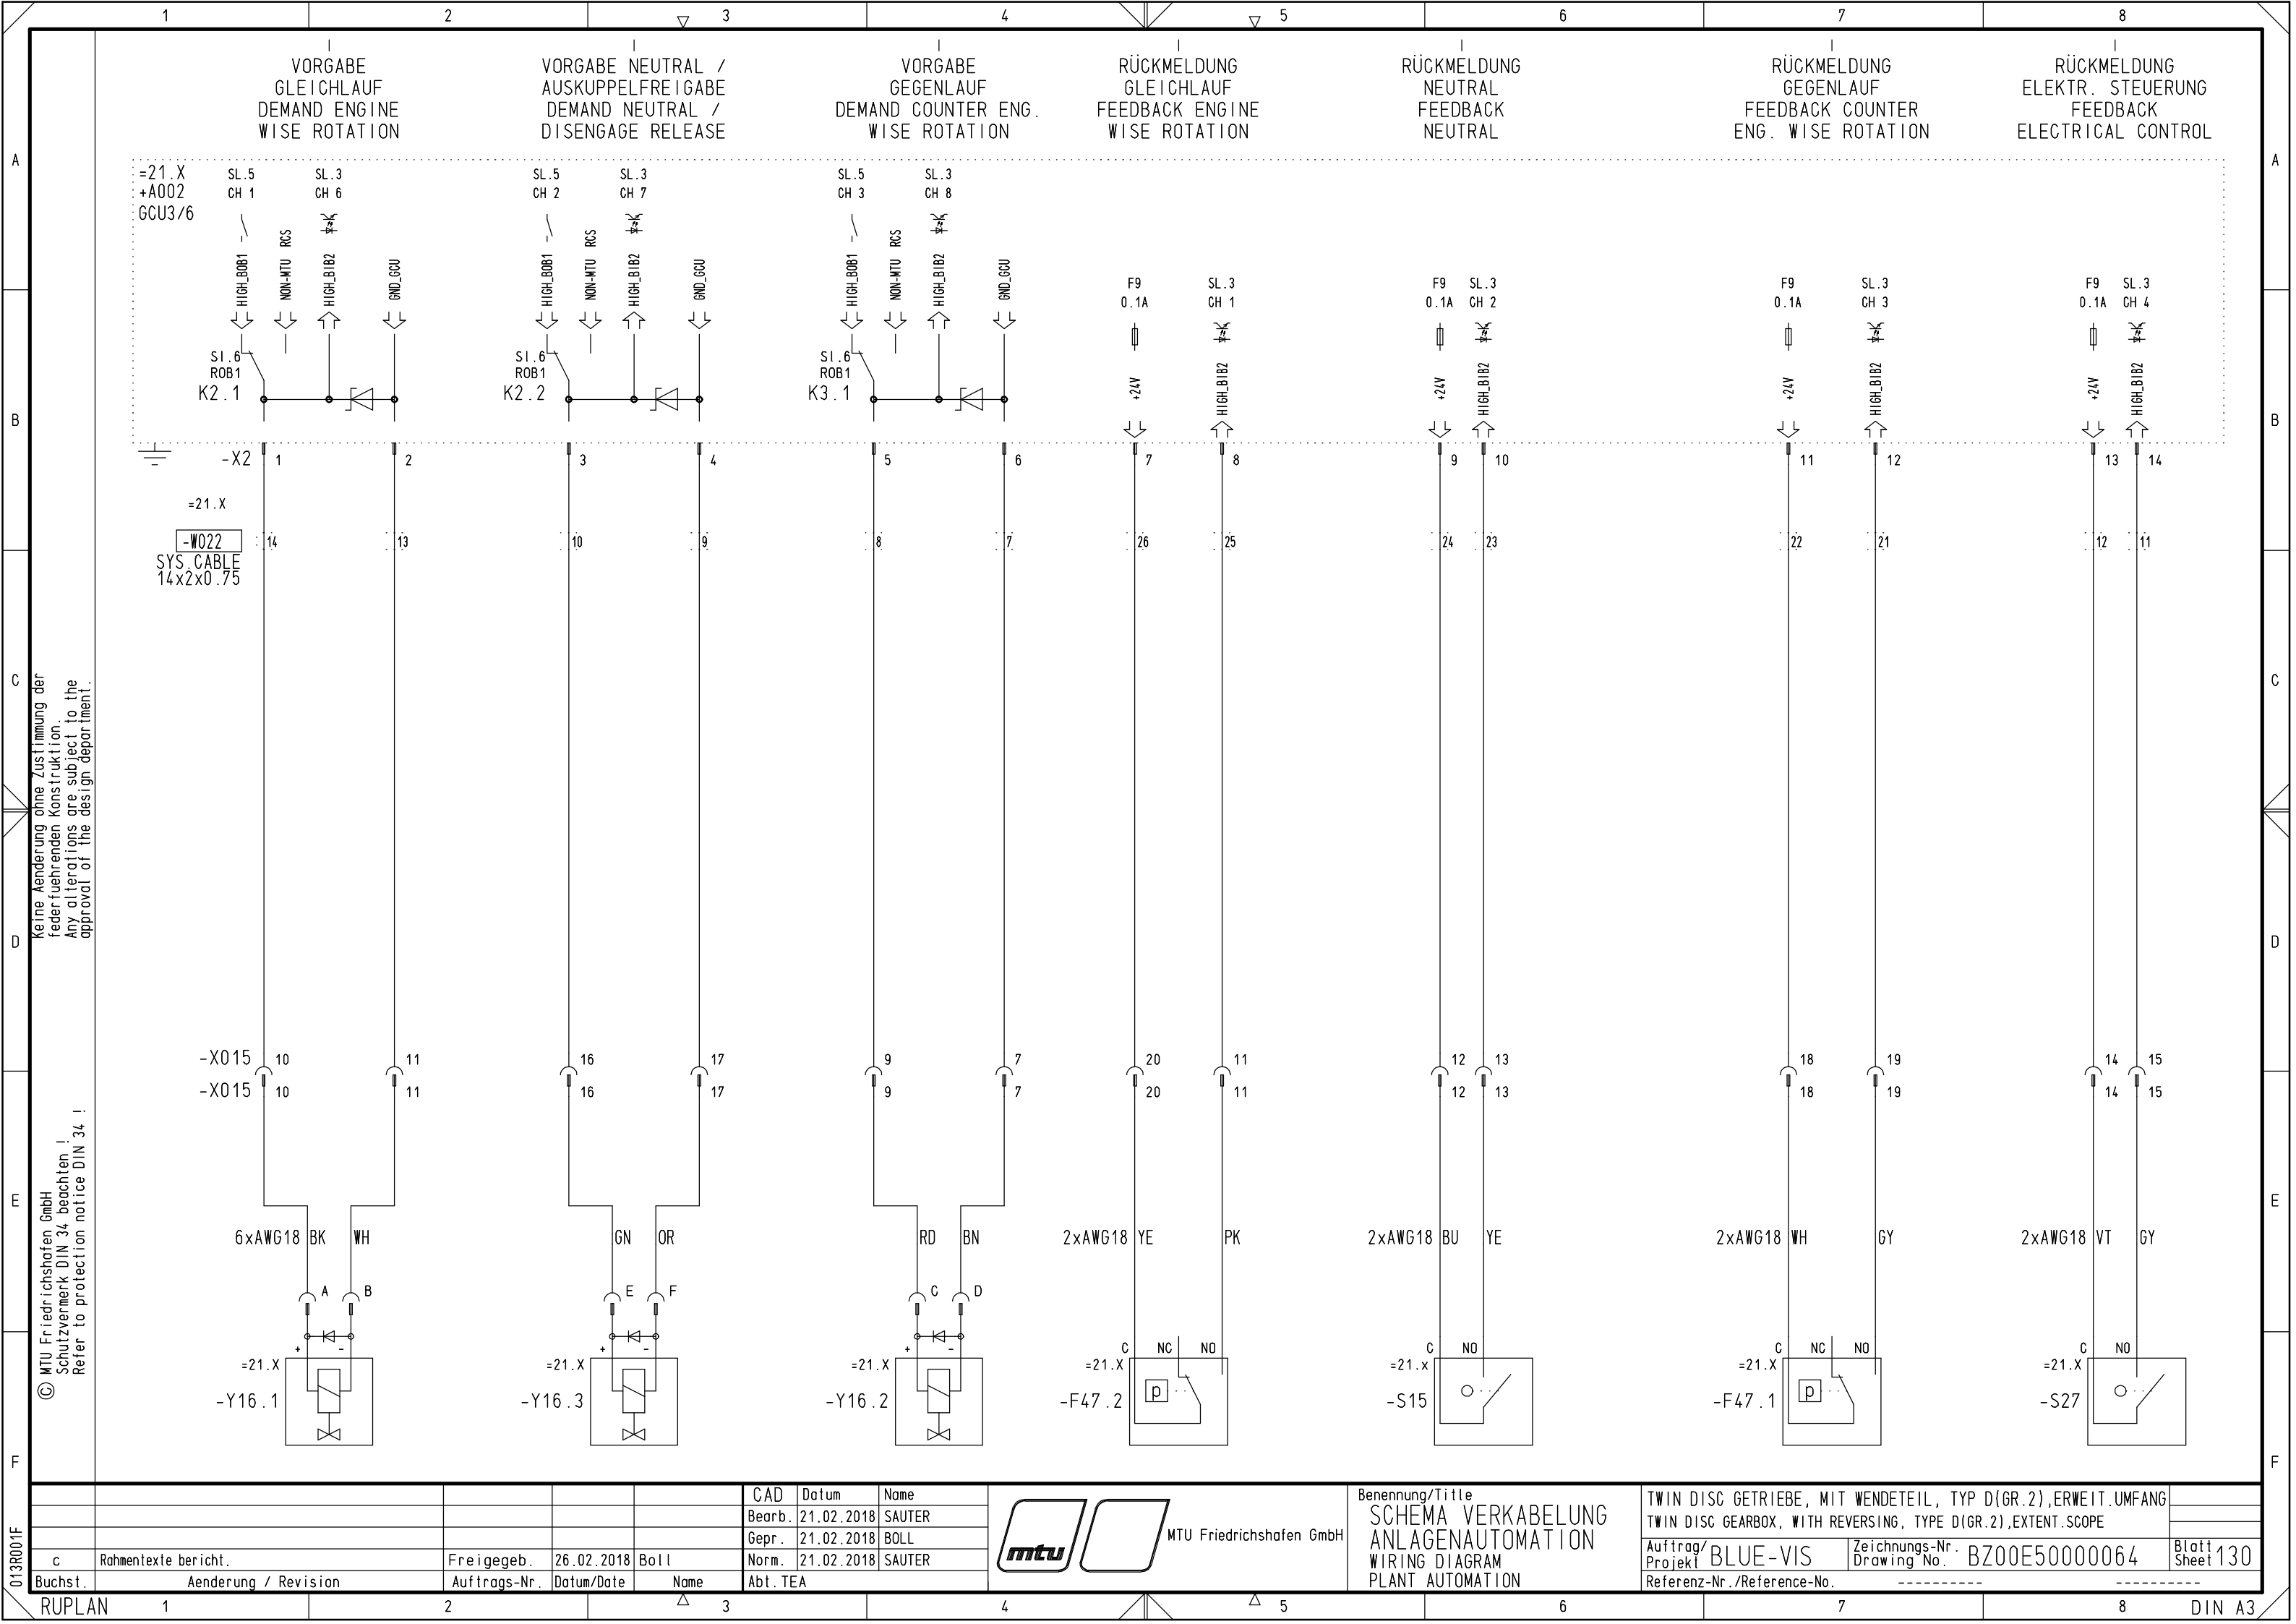

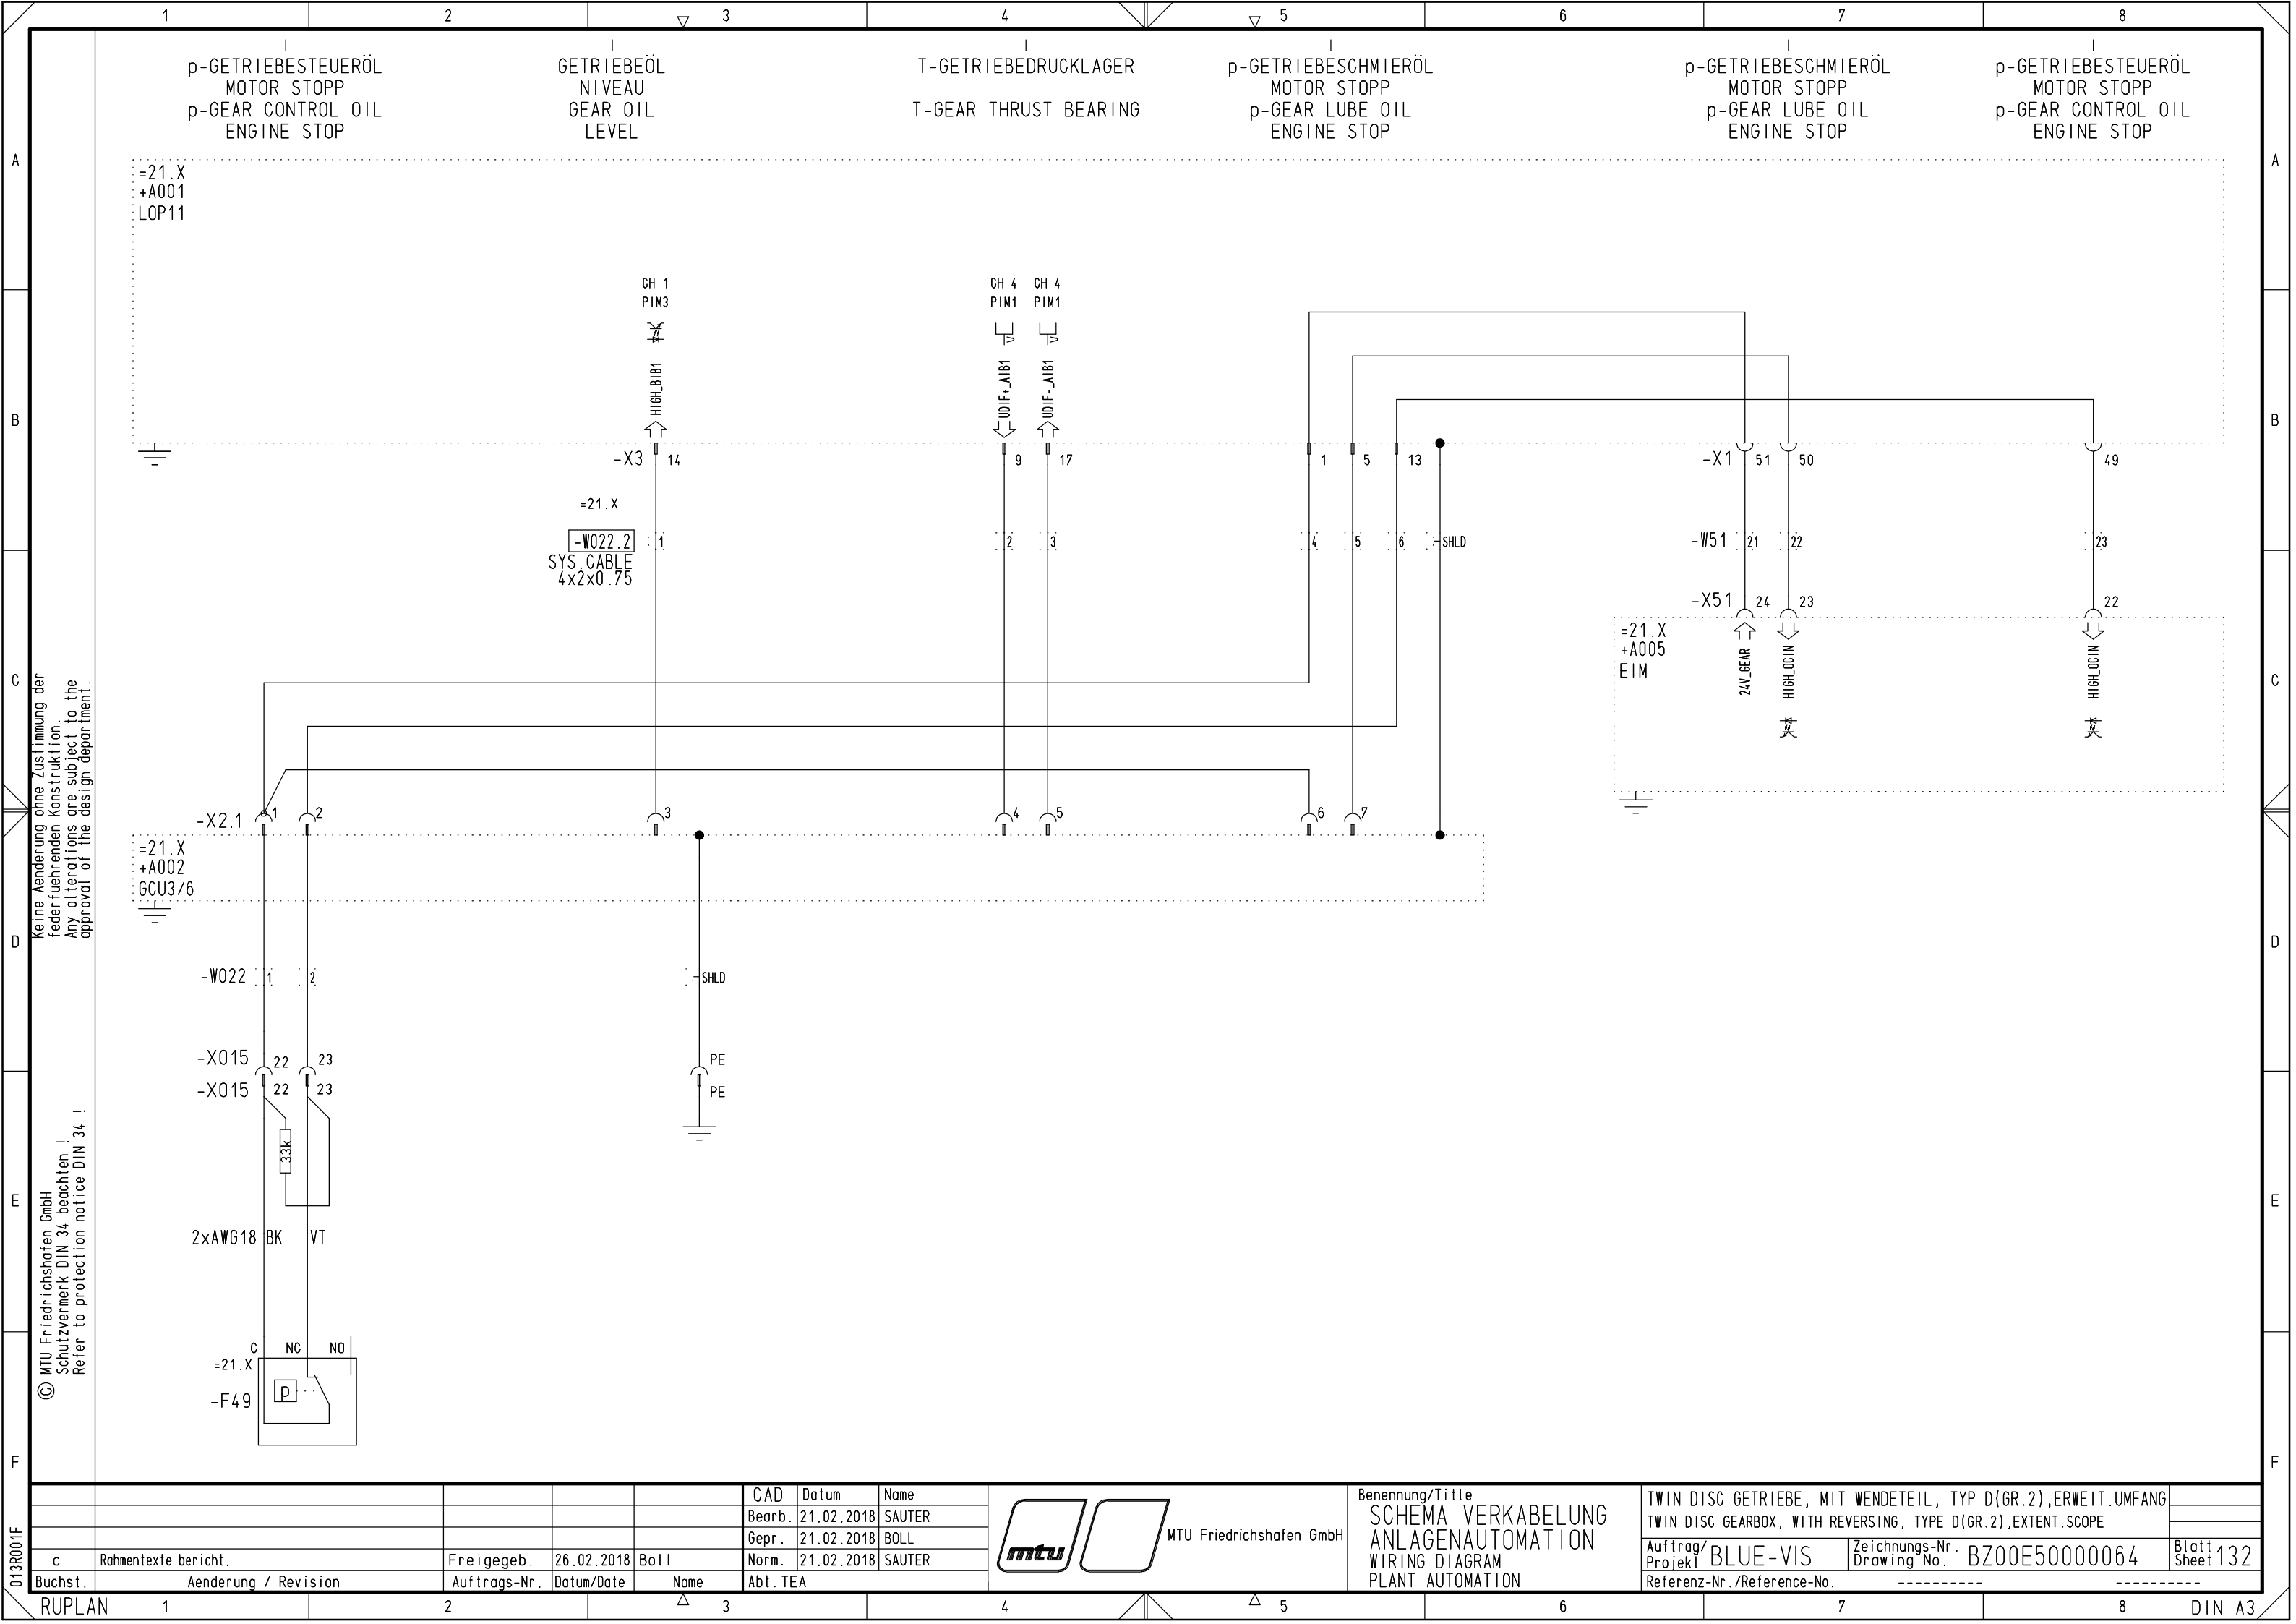

1

2

3

4

5

6

7

8

A

B

C

D

E

F

HINWEIS

PRINZIP-SCHALTPLAN FÜR UNBEKANNTES
TWIN DISK GETRIEBE

NUR ZUR INFORMATION

NOTE

GENERAL CIRCUIT DIAGRAM FOR UNKNOWN
TWIN DISK GEARBOX

FOR INFORMATION ONLY

Keine Änderung ohne Zustimmung der
federführenden Konstruktion.
Any alterations are subject to the
approval of the design department.

© MTU Friedrichshafen GmbH
Schutzmerk DIN 34 beachten !
Refer to protection notice DIN 34 !

					CAD	Datum	Name	 MTU Friedrichshafen GmbH	Benennung/Title SCHEMA VERKABELUNG ANLAGENAUTOMATION WIRING DIAGRAM PLANT AUTOMATION	TWIN DISK GETRIEBE, MAXIMALUMFANG, TYP F, HINWEISE TWIN DISK GEARBOX, MAXIMAL SCOPE, TYPE F, INSTRUCTIONS	Auftrag/ Projekt BLUE-VIS	Zeichnungs-Nr. Drawing No. BZ00E50000064	Blatt Sheet 133
					Bearb.	21.02.2018	SAUTER						
					Gepr.	21.02.2018	BOLL						
c	Rahmentexte bericht.	Freigegeb.	26.02.2018	Boll	Norm.	21.02.2018	SAUTER						
Buchst.	Änderung / Revision	Auftrags-Nr.	Datum/Date	Name	Abt. TEA								

RUPLAN

1

2

3

4


5

6

7


8

DIN A3

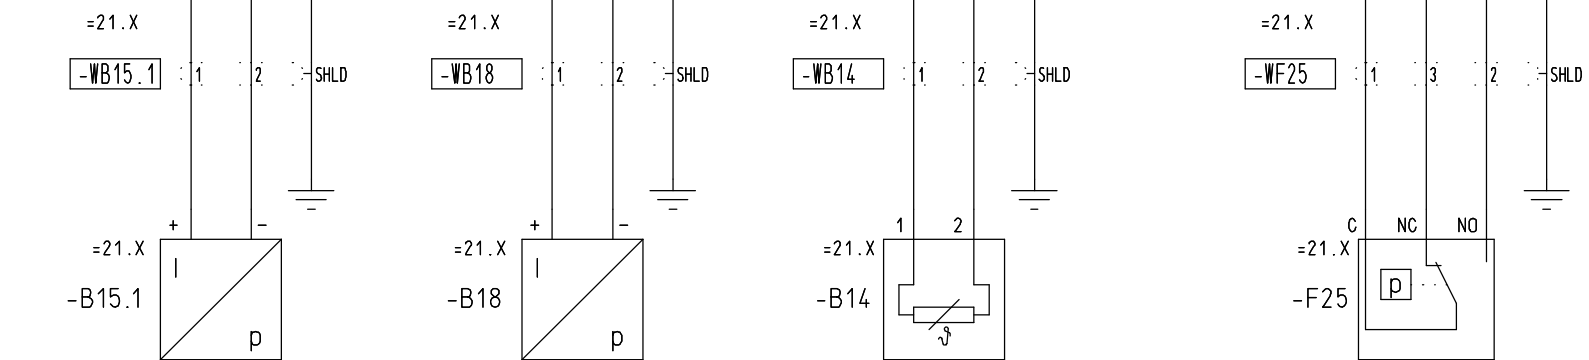

MTU Friedrichshafen GmbH
Schutzvermerk DIN 34 beachten !
Refer to protection notice DIN 34 !





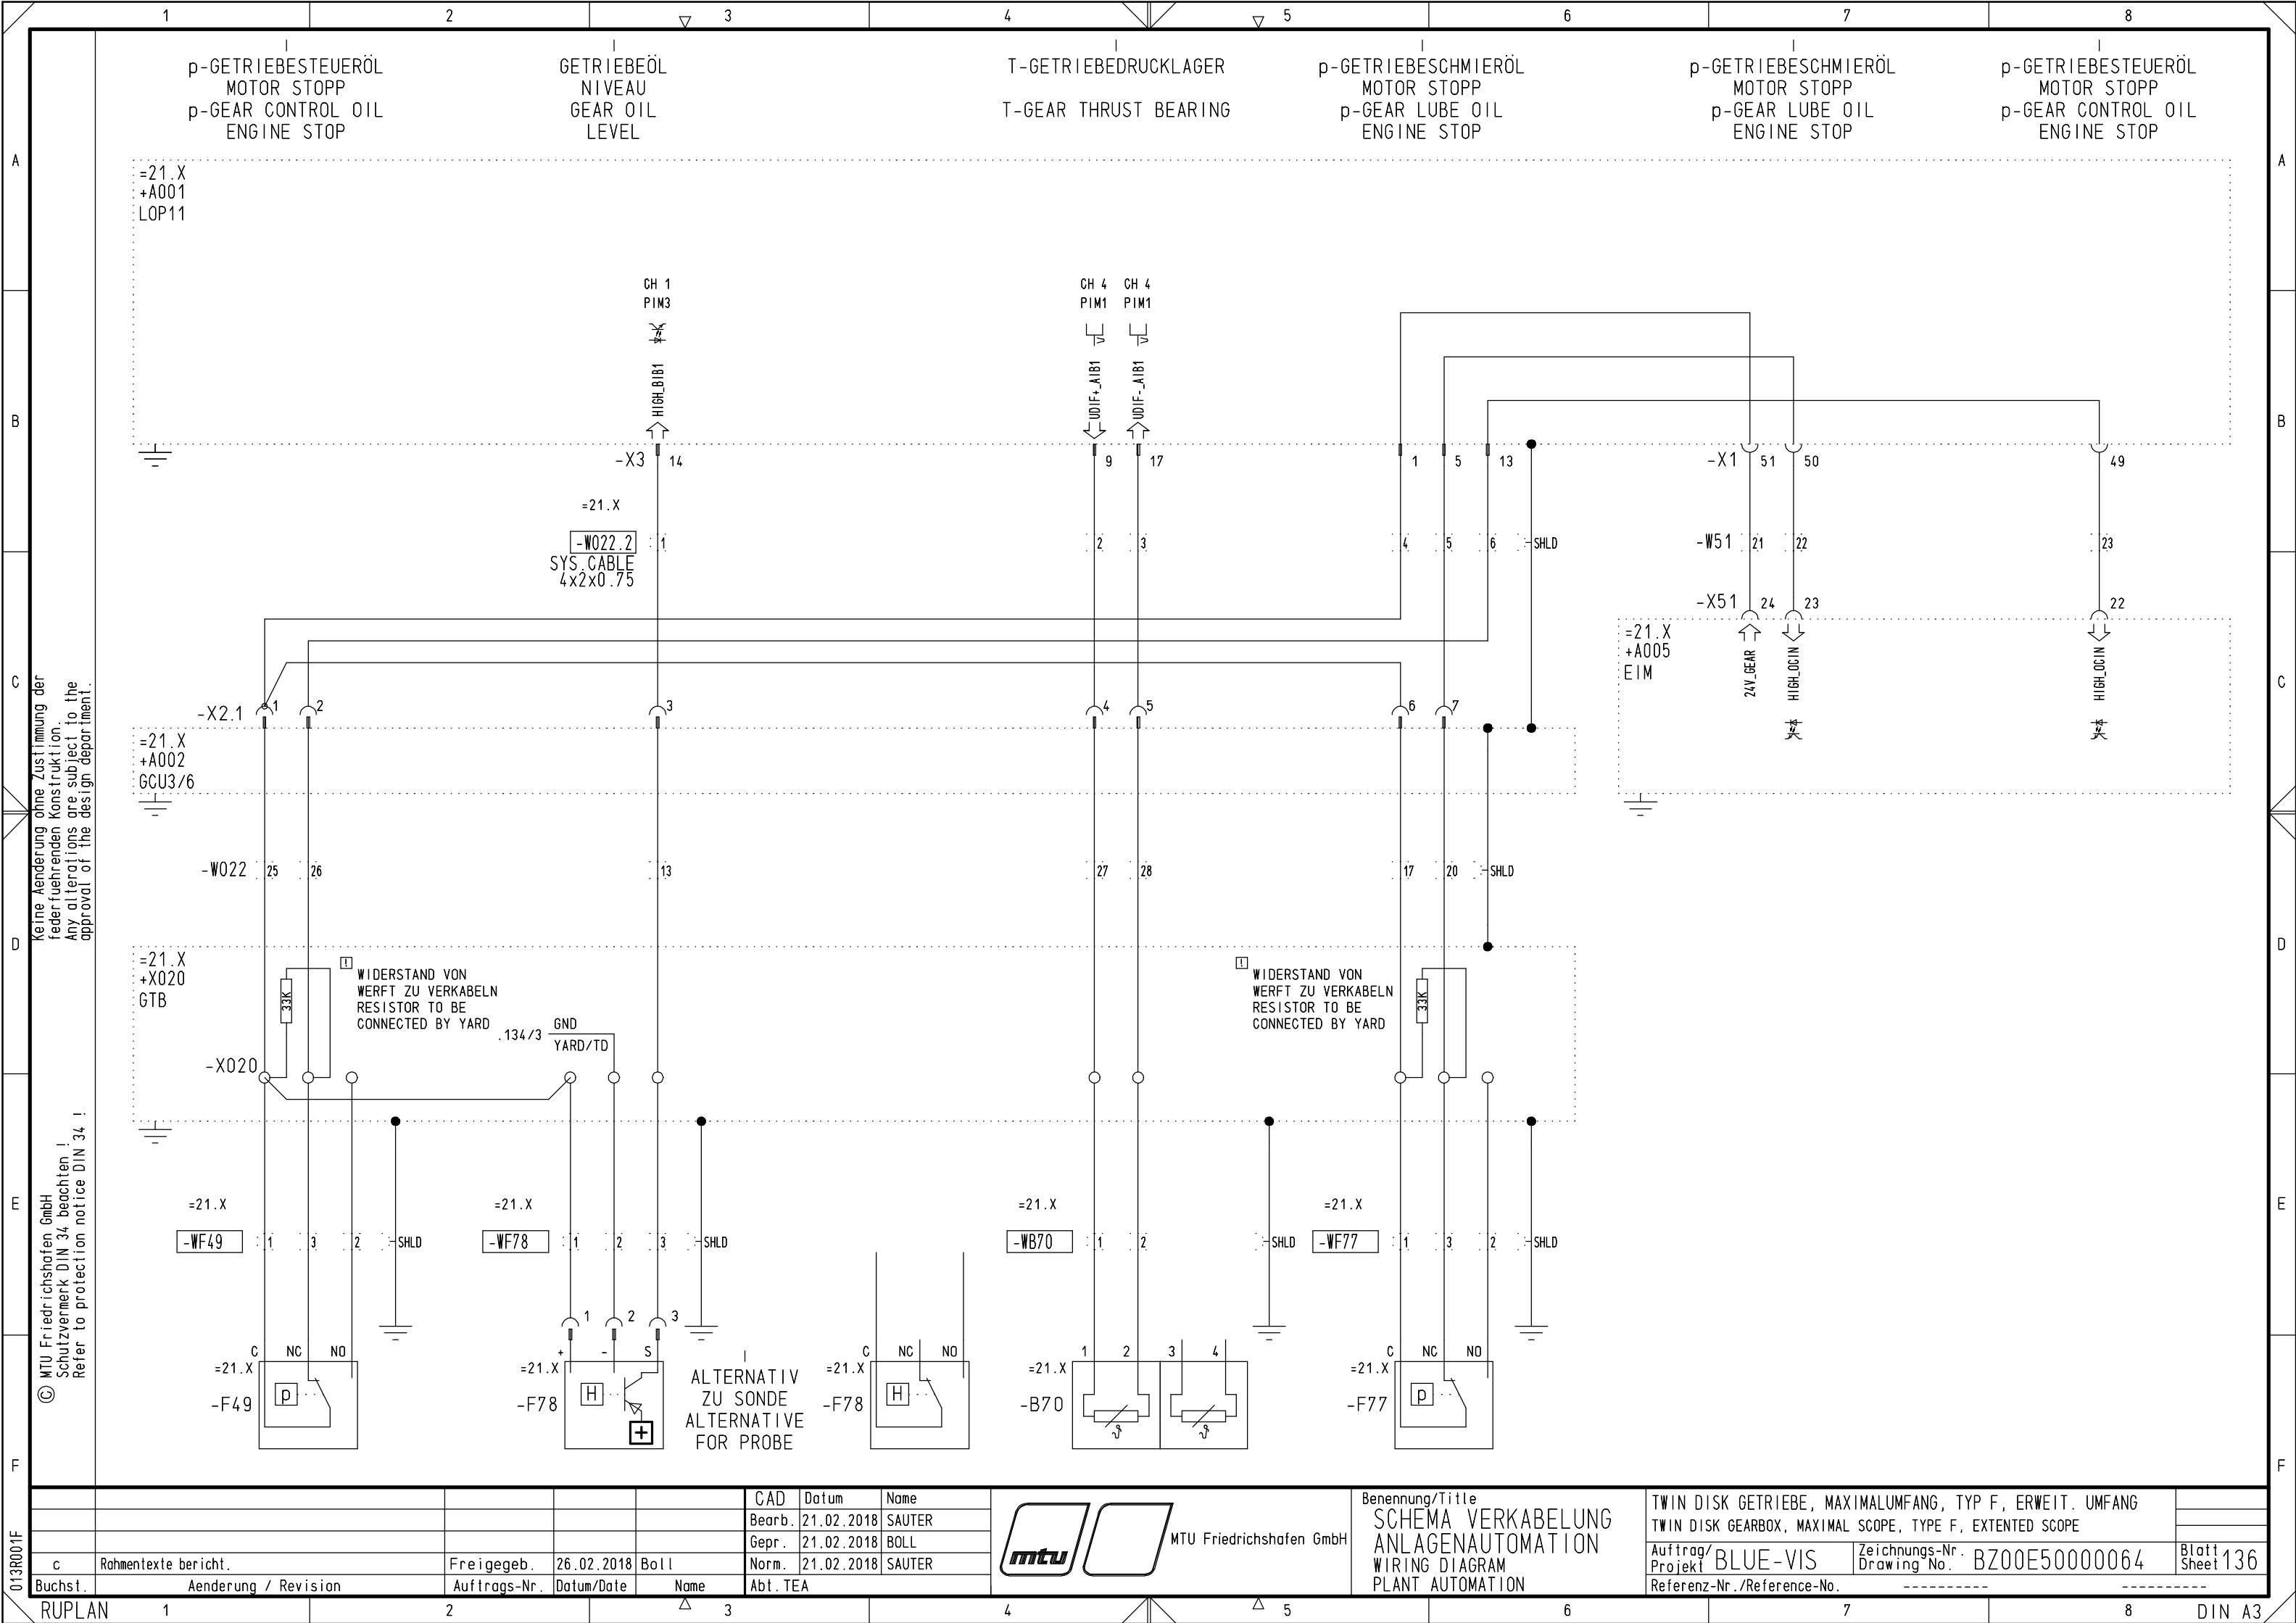

Keine Änderung ohne Zustimmung der
Federführenden Konstruktion.
Any alterations are subject to the
approval of the design department.

© MTU Friedrichshafen GmbH
Schutzmerk DIN 34 beachten !
Refer to protection notice DIN 34 !

013R001F
RUPLAN

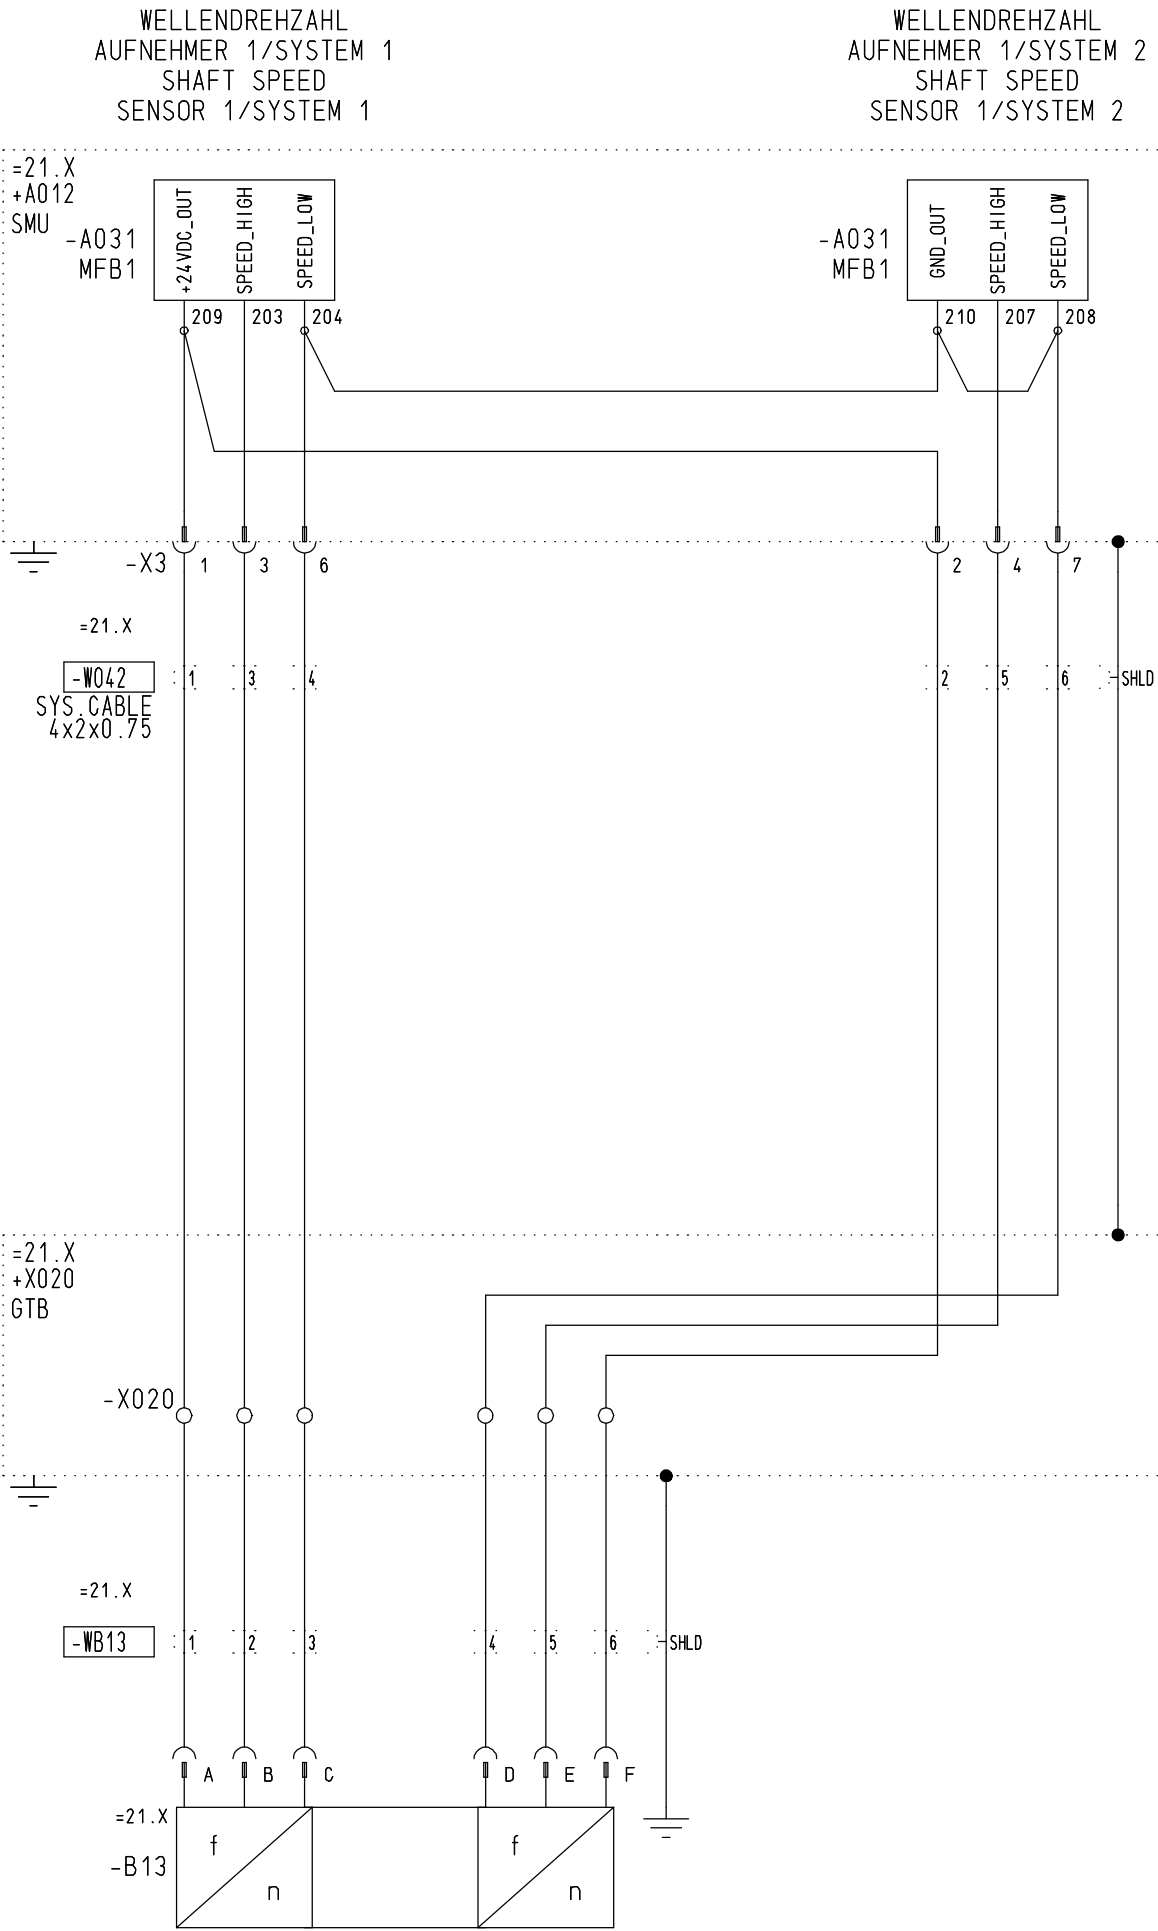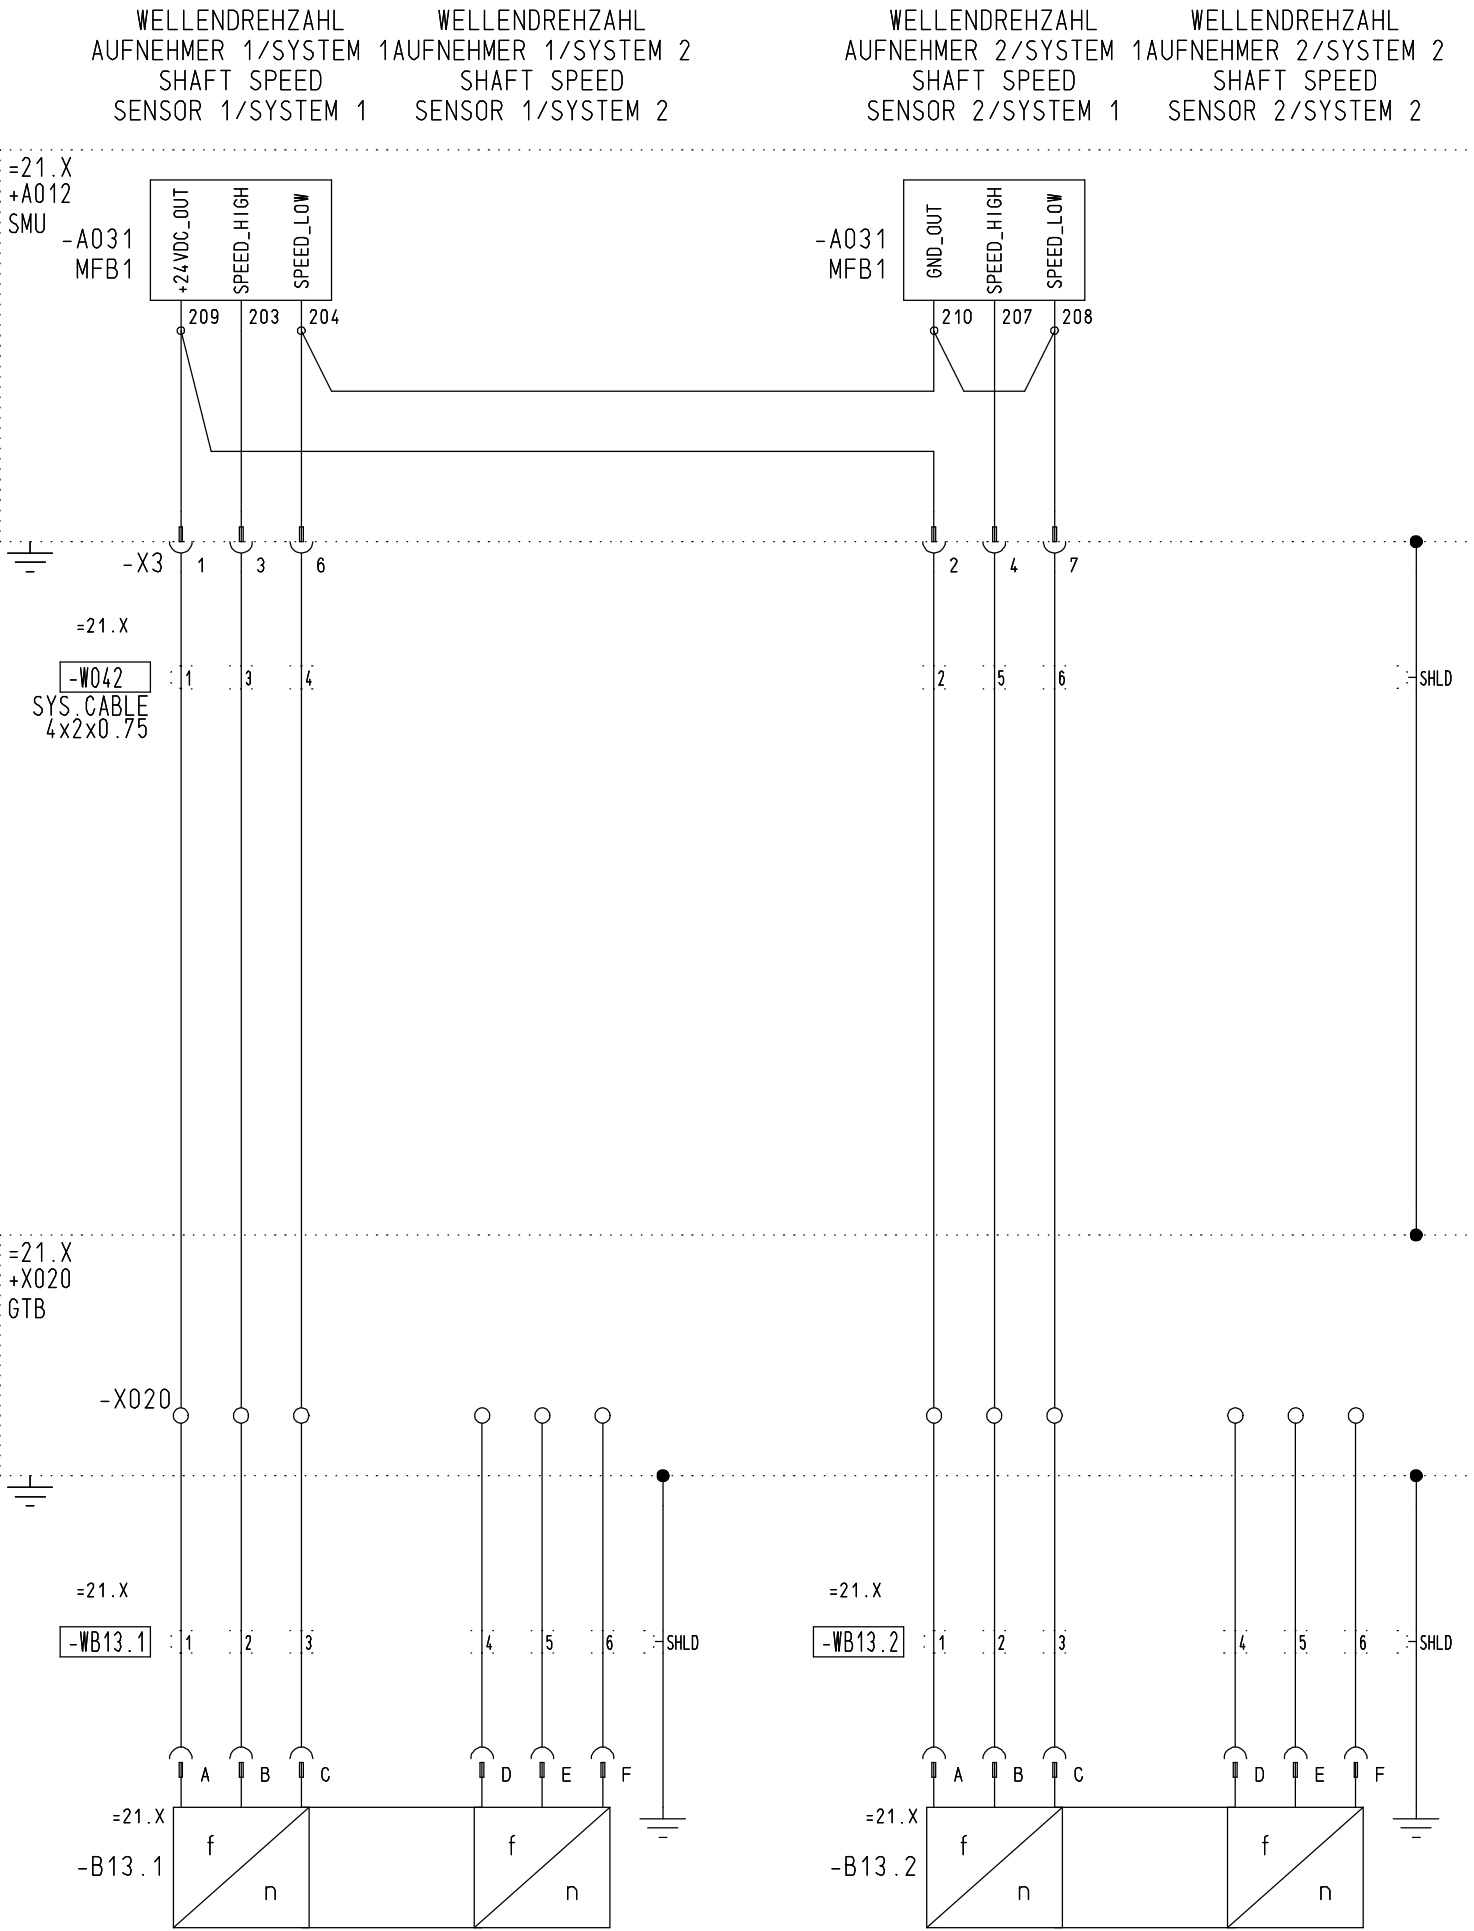

CAD	Datum	Name
Bearb.	21.02.2018	SAUTER
Gepr.	21.02.2018	BOLL
Norm.	21.02.2018	SAUTER
Abt. TEA		



MTU Friedrichshafen GmbH

Benennung/Title
SCHEMA VERKABELUNG
ANLAGENAUTOMATION
WIRING DIAGRAM
PLANT AUTOMATION

TWIN DISK GETRIEBE, MAXIMALUMFANG, TYP F, WELLENDREHZAHL
TWIN DISK GEARBOX, MAXIMAL SCOPE, TYPE F, SHAFT SPEED
Auftrag/
Projekt BLUE-VIS
Referenz-Nr./Reference-No. -----


Zeichnungs-Nr.
Drawing No. BZ00E50000064

Blatt
Sheet 137


DIN A3

Keine Änderung ohne Zustimmung der
federführenden Konstruktion.
Any alterations are subject to the
approval of the design department.

© MTU Friedrichshafen GmbH
Schutzvermerk DIN 34 beachten !
Refer to protection notice DIN 34 !

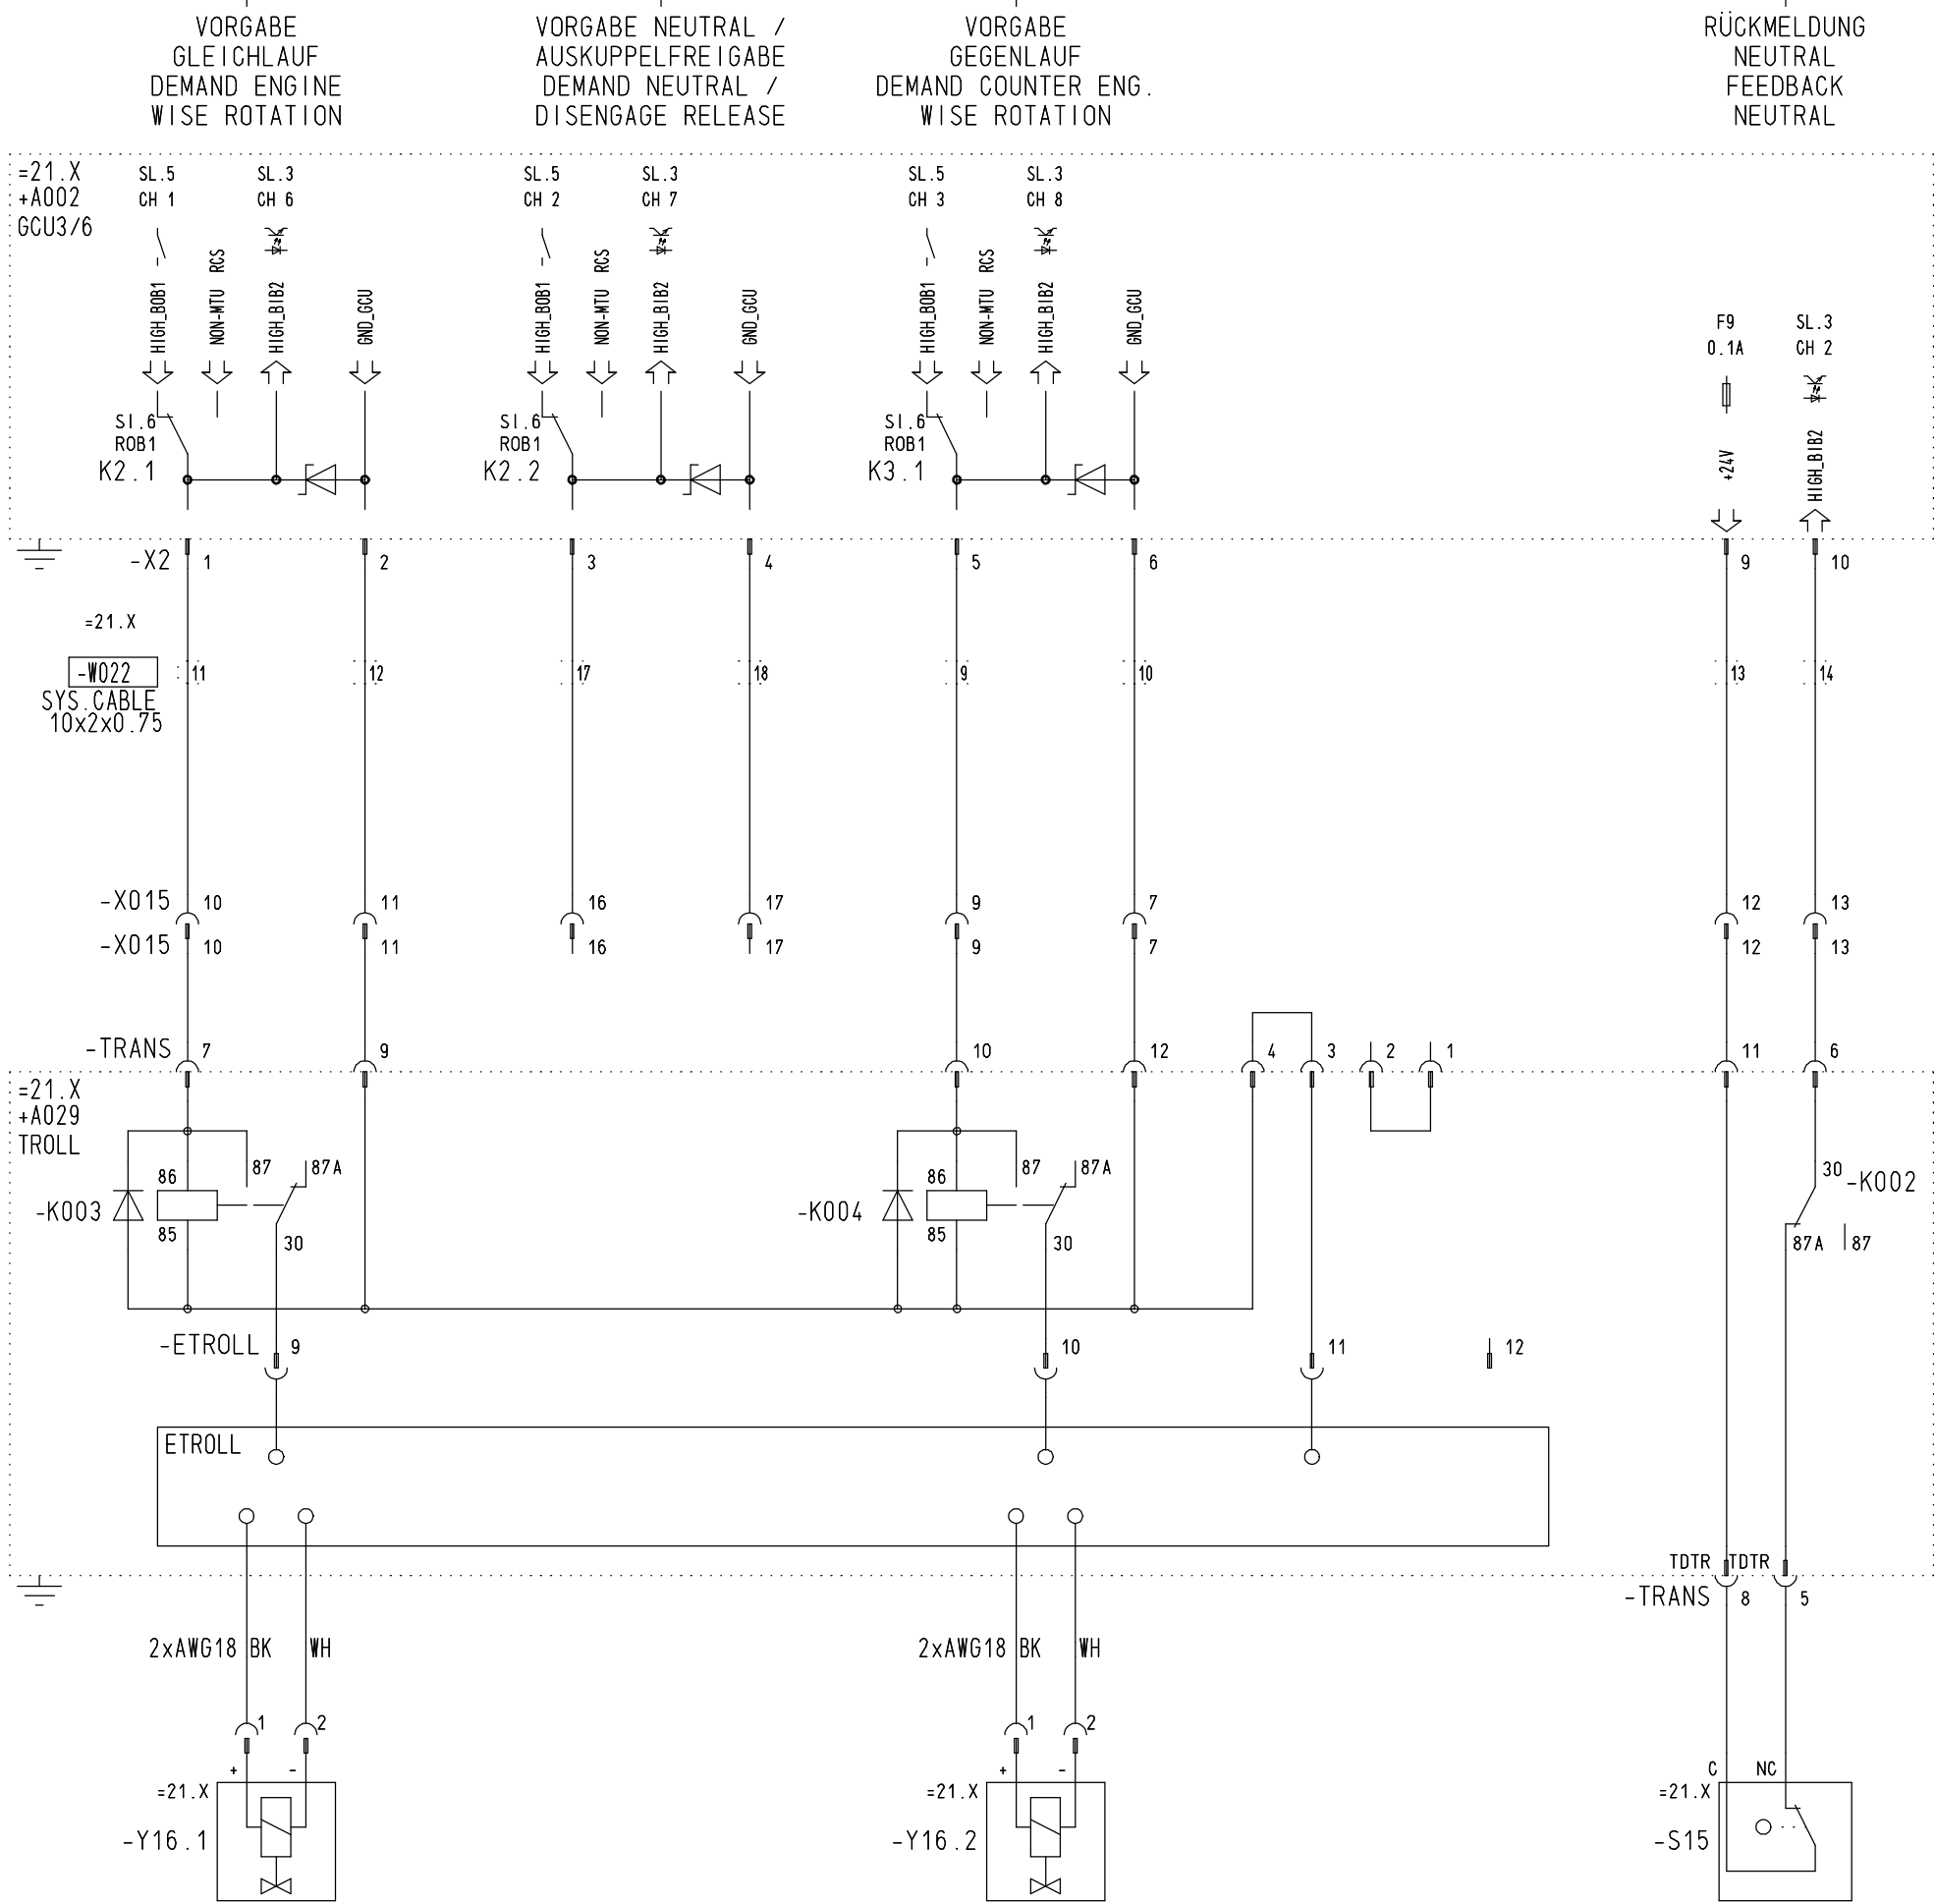


					CAD	Datum	Name	 MTU Friedrichshafen GmbH	Benennung/Title SCHEMA VERKABELUNG ANLAGENAUTOMATION WIRING DIAGRAM PLANT AUTOMATION	TWIN DISK GETRIEBE, TROLLINGSTEUERUNG E-TROLL					
					Bearb.	21.02.2018	SAUTER			TWIN DISK GEARBOX, TROLLING CONTROL E-TROLL					
					Gepr.	21.02.2018	BOLL								
					Norm.	21.02.2018	SAUTER								
c	Rahmentexte bericht.		Freigegeb.	26.02.2018	Boll					Auftrag/ Projekt	BLUE-VIS	Zeichnungs-Nr. Drawing No.	BZ00E50000064	Blatt Sheet	138
Buchst.	Aenderung / Revision		Auftrags-Nr.	Datum/Date	Name	Abt. TEA				Referenz-Nr./Reference-No. -----					

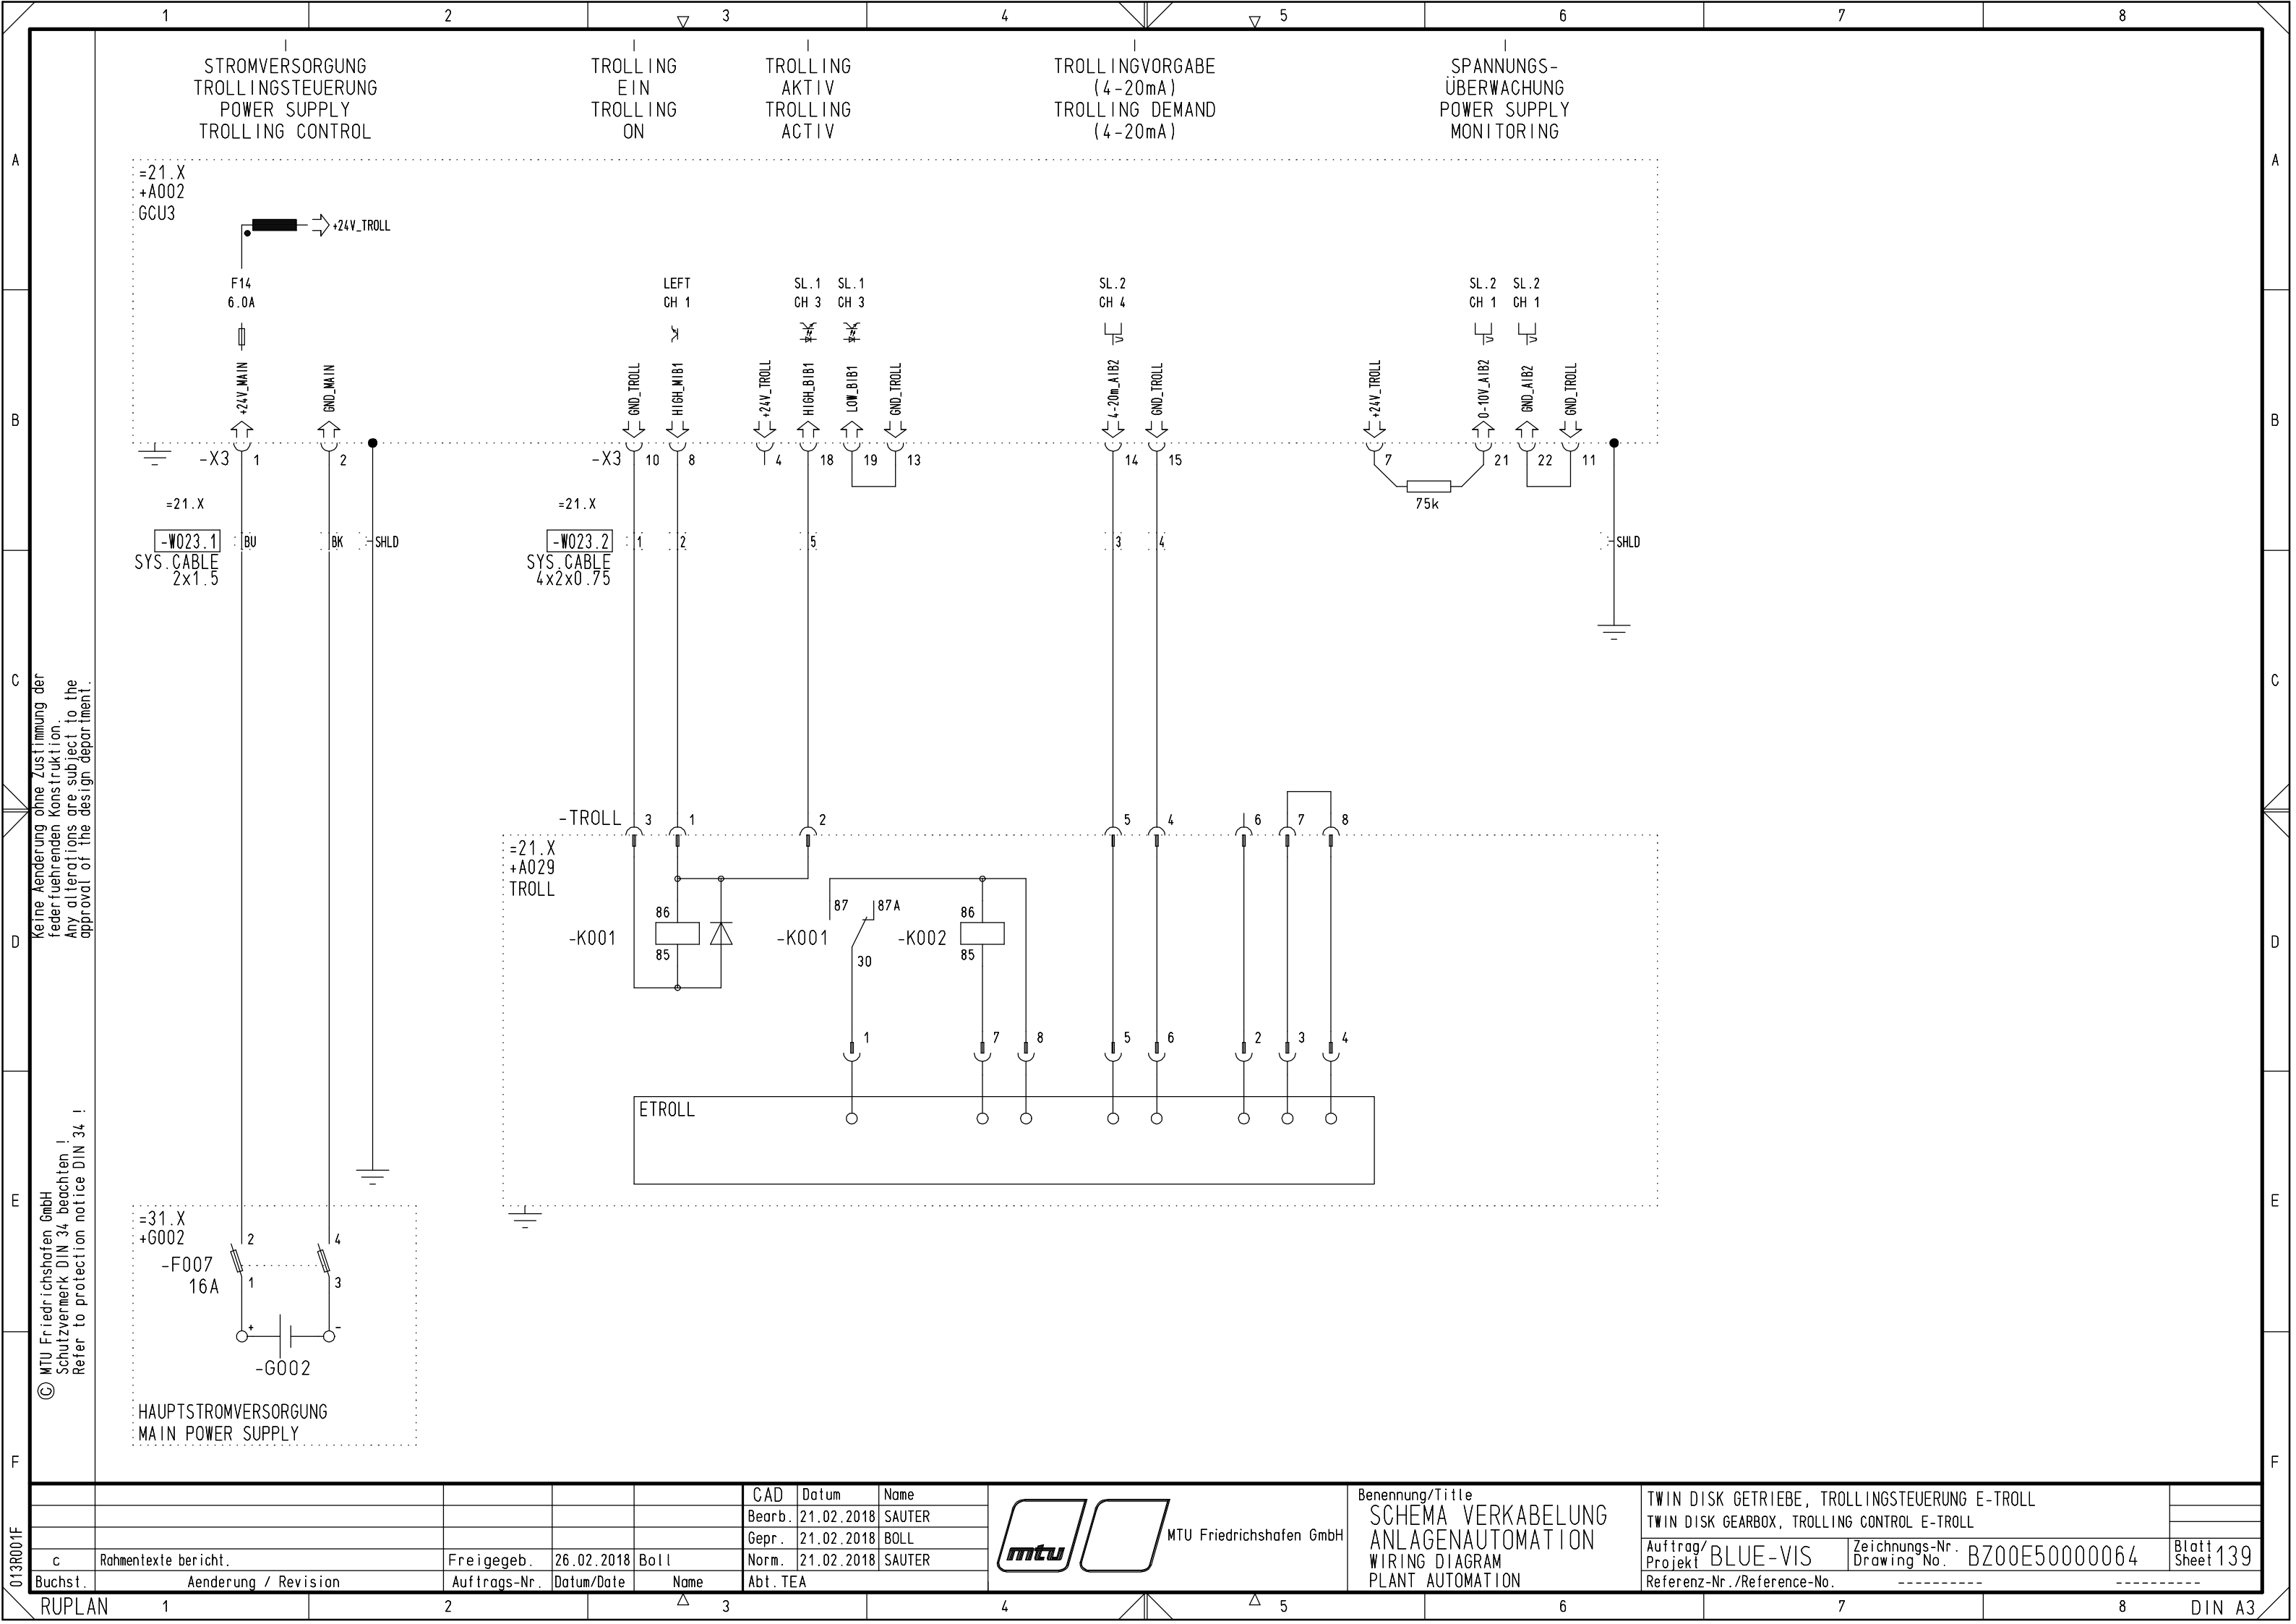

Keine Änderung ohne Zustimmung der
federführenden Konstruktion.
Any alterations are subject to the
approval of the design department.

© MTU Friedrichshafen GmbH
Schutzvermerk DIN 34 beachten !
Refer to protection notice DIN 34 !

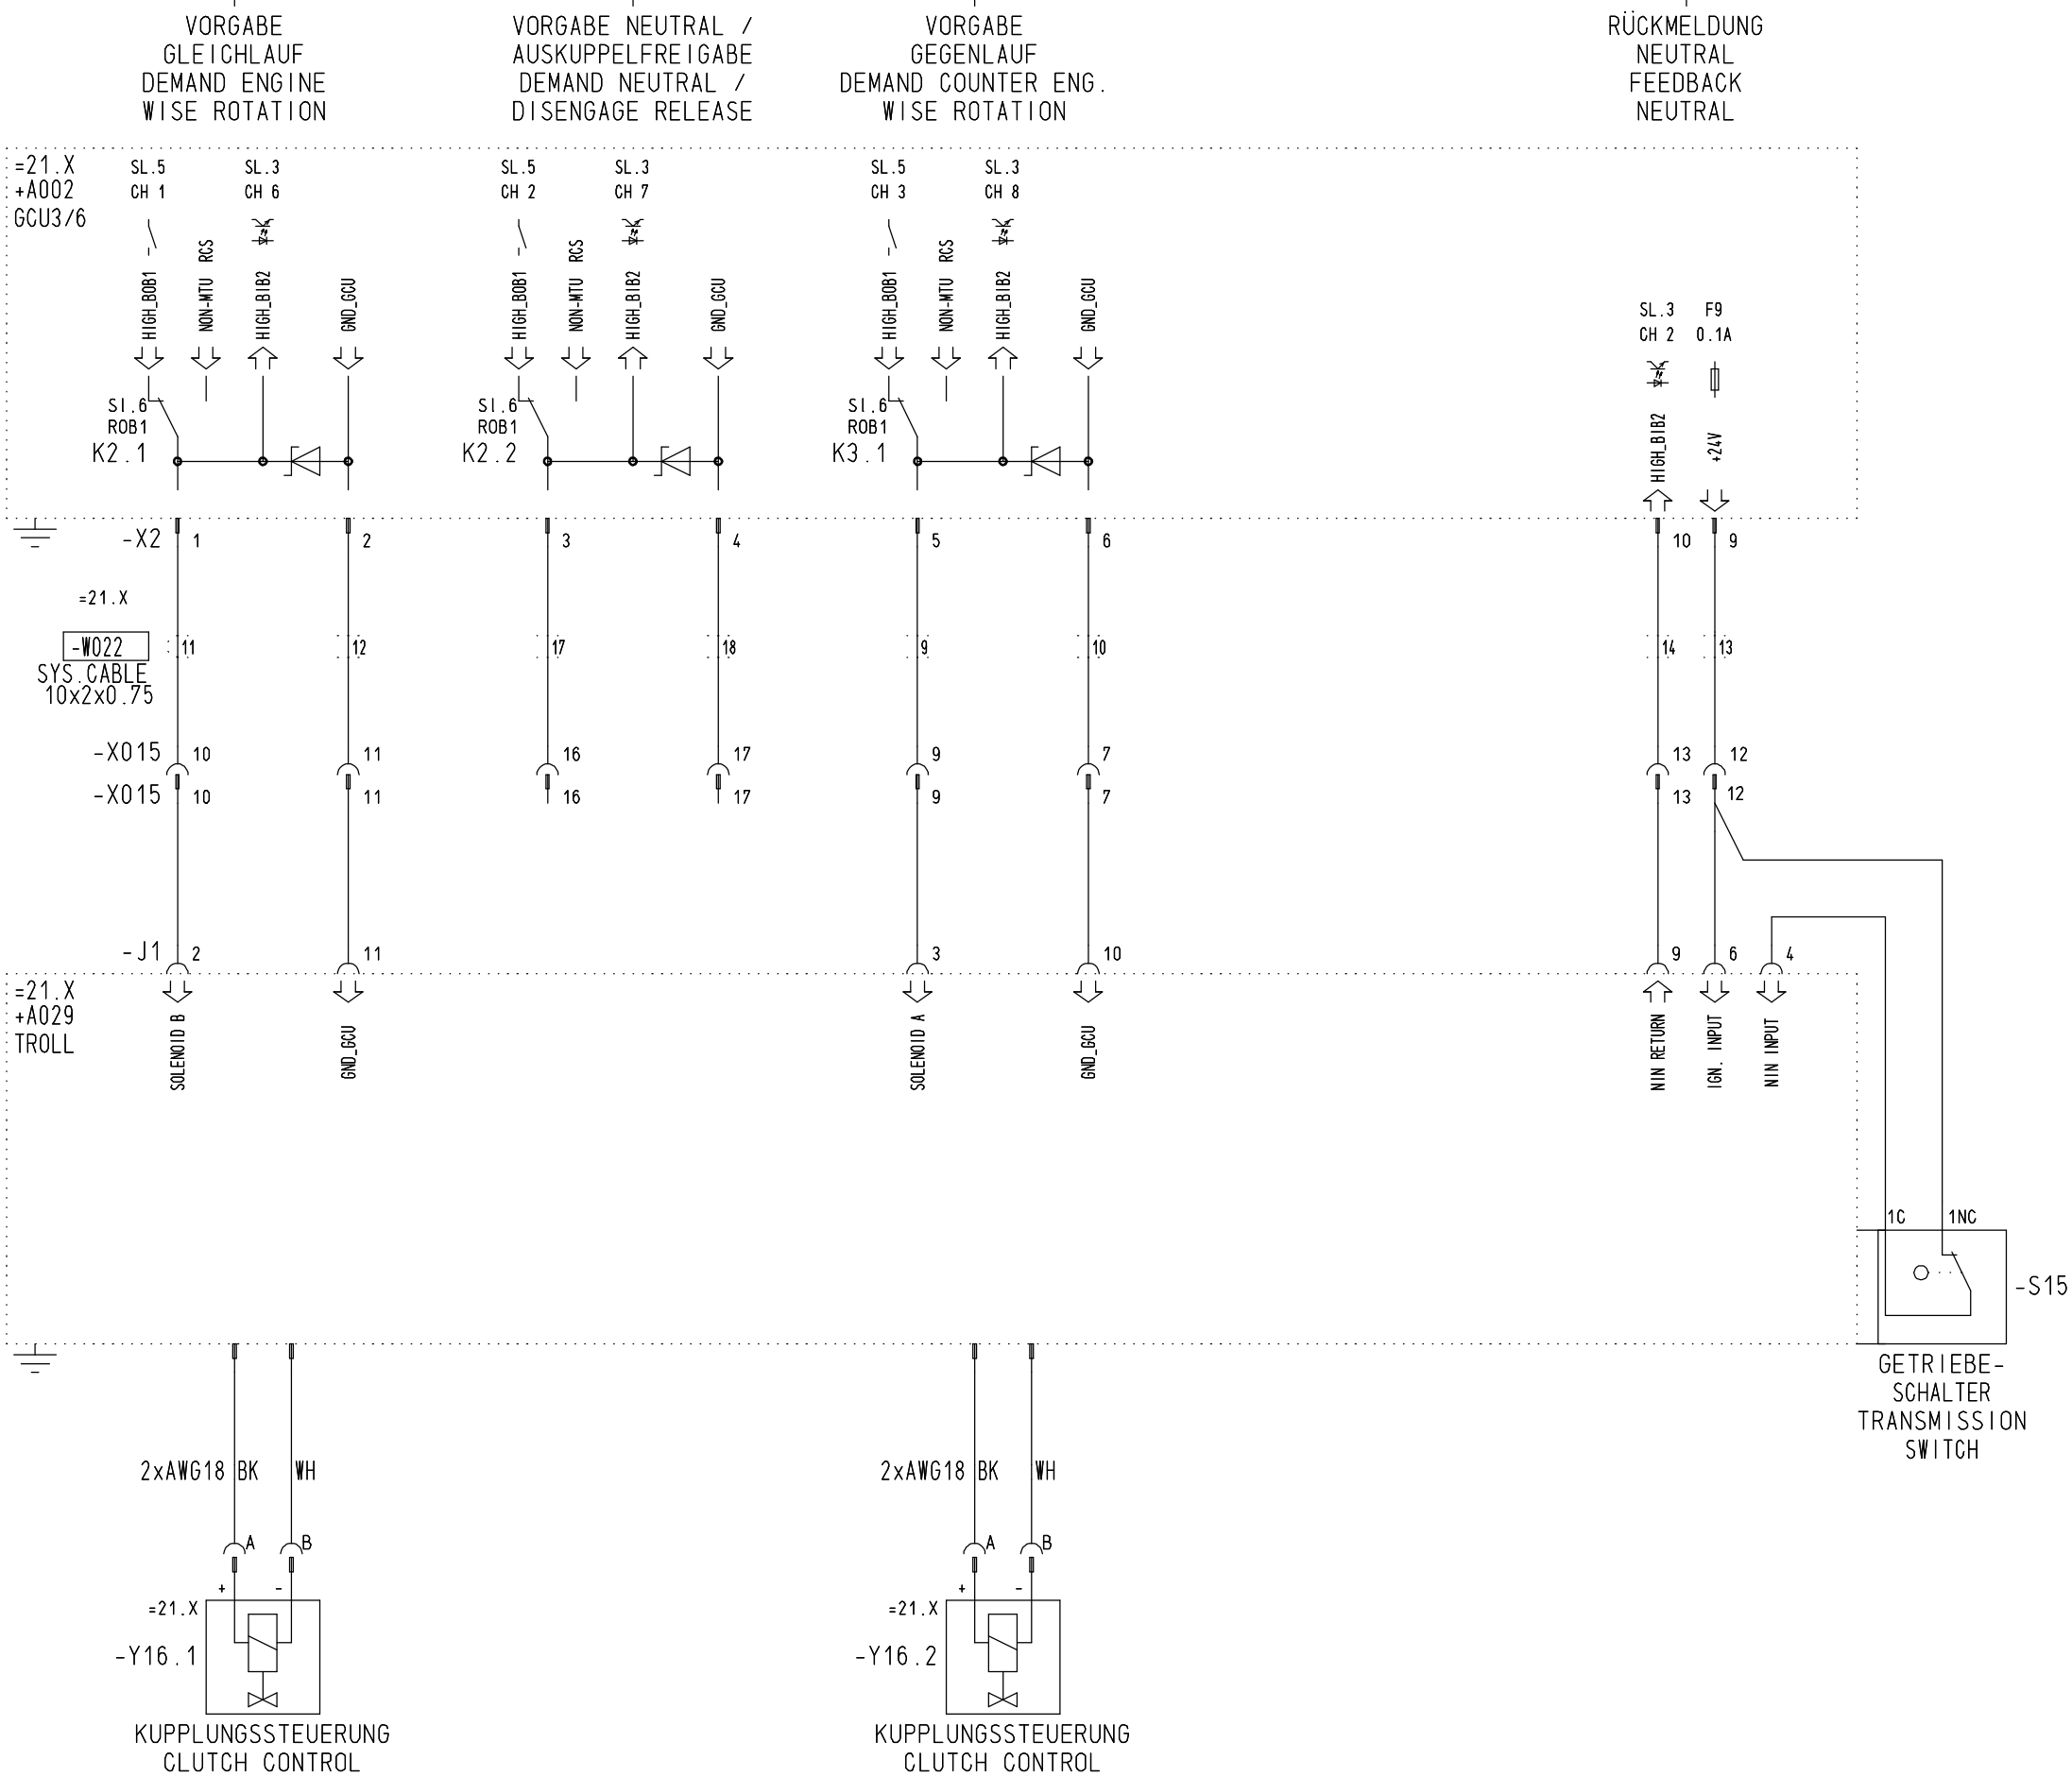

					CAD	Datum	Name
					Bearb.	21.02.2018	SAUTER
					Gepr.	21.02.2018	BOLL
					Norm.	21.02.2018	SAUTER
c	Rahmentexte bericht.	Freigegeb.	26.02.2018	Boll	Abt. TEA		
Buchst.	Aenderung / Revision	Auftrags-Nr.	Datum/Date	Name			



MTU Friedrichshafen GmbH

Benennung/Title
SCHEMA VERKABELUNG
ANLAGENAUTOMATION
WIRING DIAGRAM
PLANT AUTOMATION

TWIN DISK GETRIEBE, TROLLINGSTEUERUNG E-TROLL (EC050)
TWIN DISK GEARBOX, TROLLING CONTROL E-TROLL (EC050)


Auftrag/Projekt BLUE-VIS
Zeichnungs-Nr. BZ00E50000064
Drawing No.

Referenz-Nr./Reference-No. Blatt 140
Sheet

Keine Änderung ohne Zustimmung der
federführenden Konstruktion.
Any alterations are subject to the
approval of the design department.

© MTU Friedrichshafen GmbH
Schutzvermerk DIN 34 beachten !
Refer to protection notice DIN 34 !

013R001F

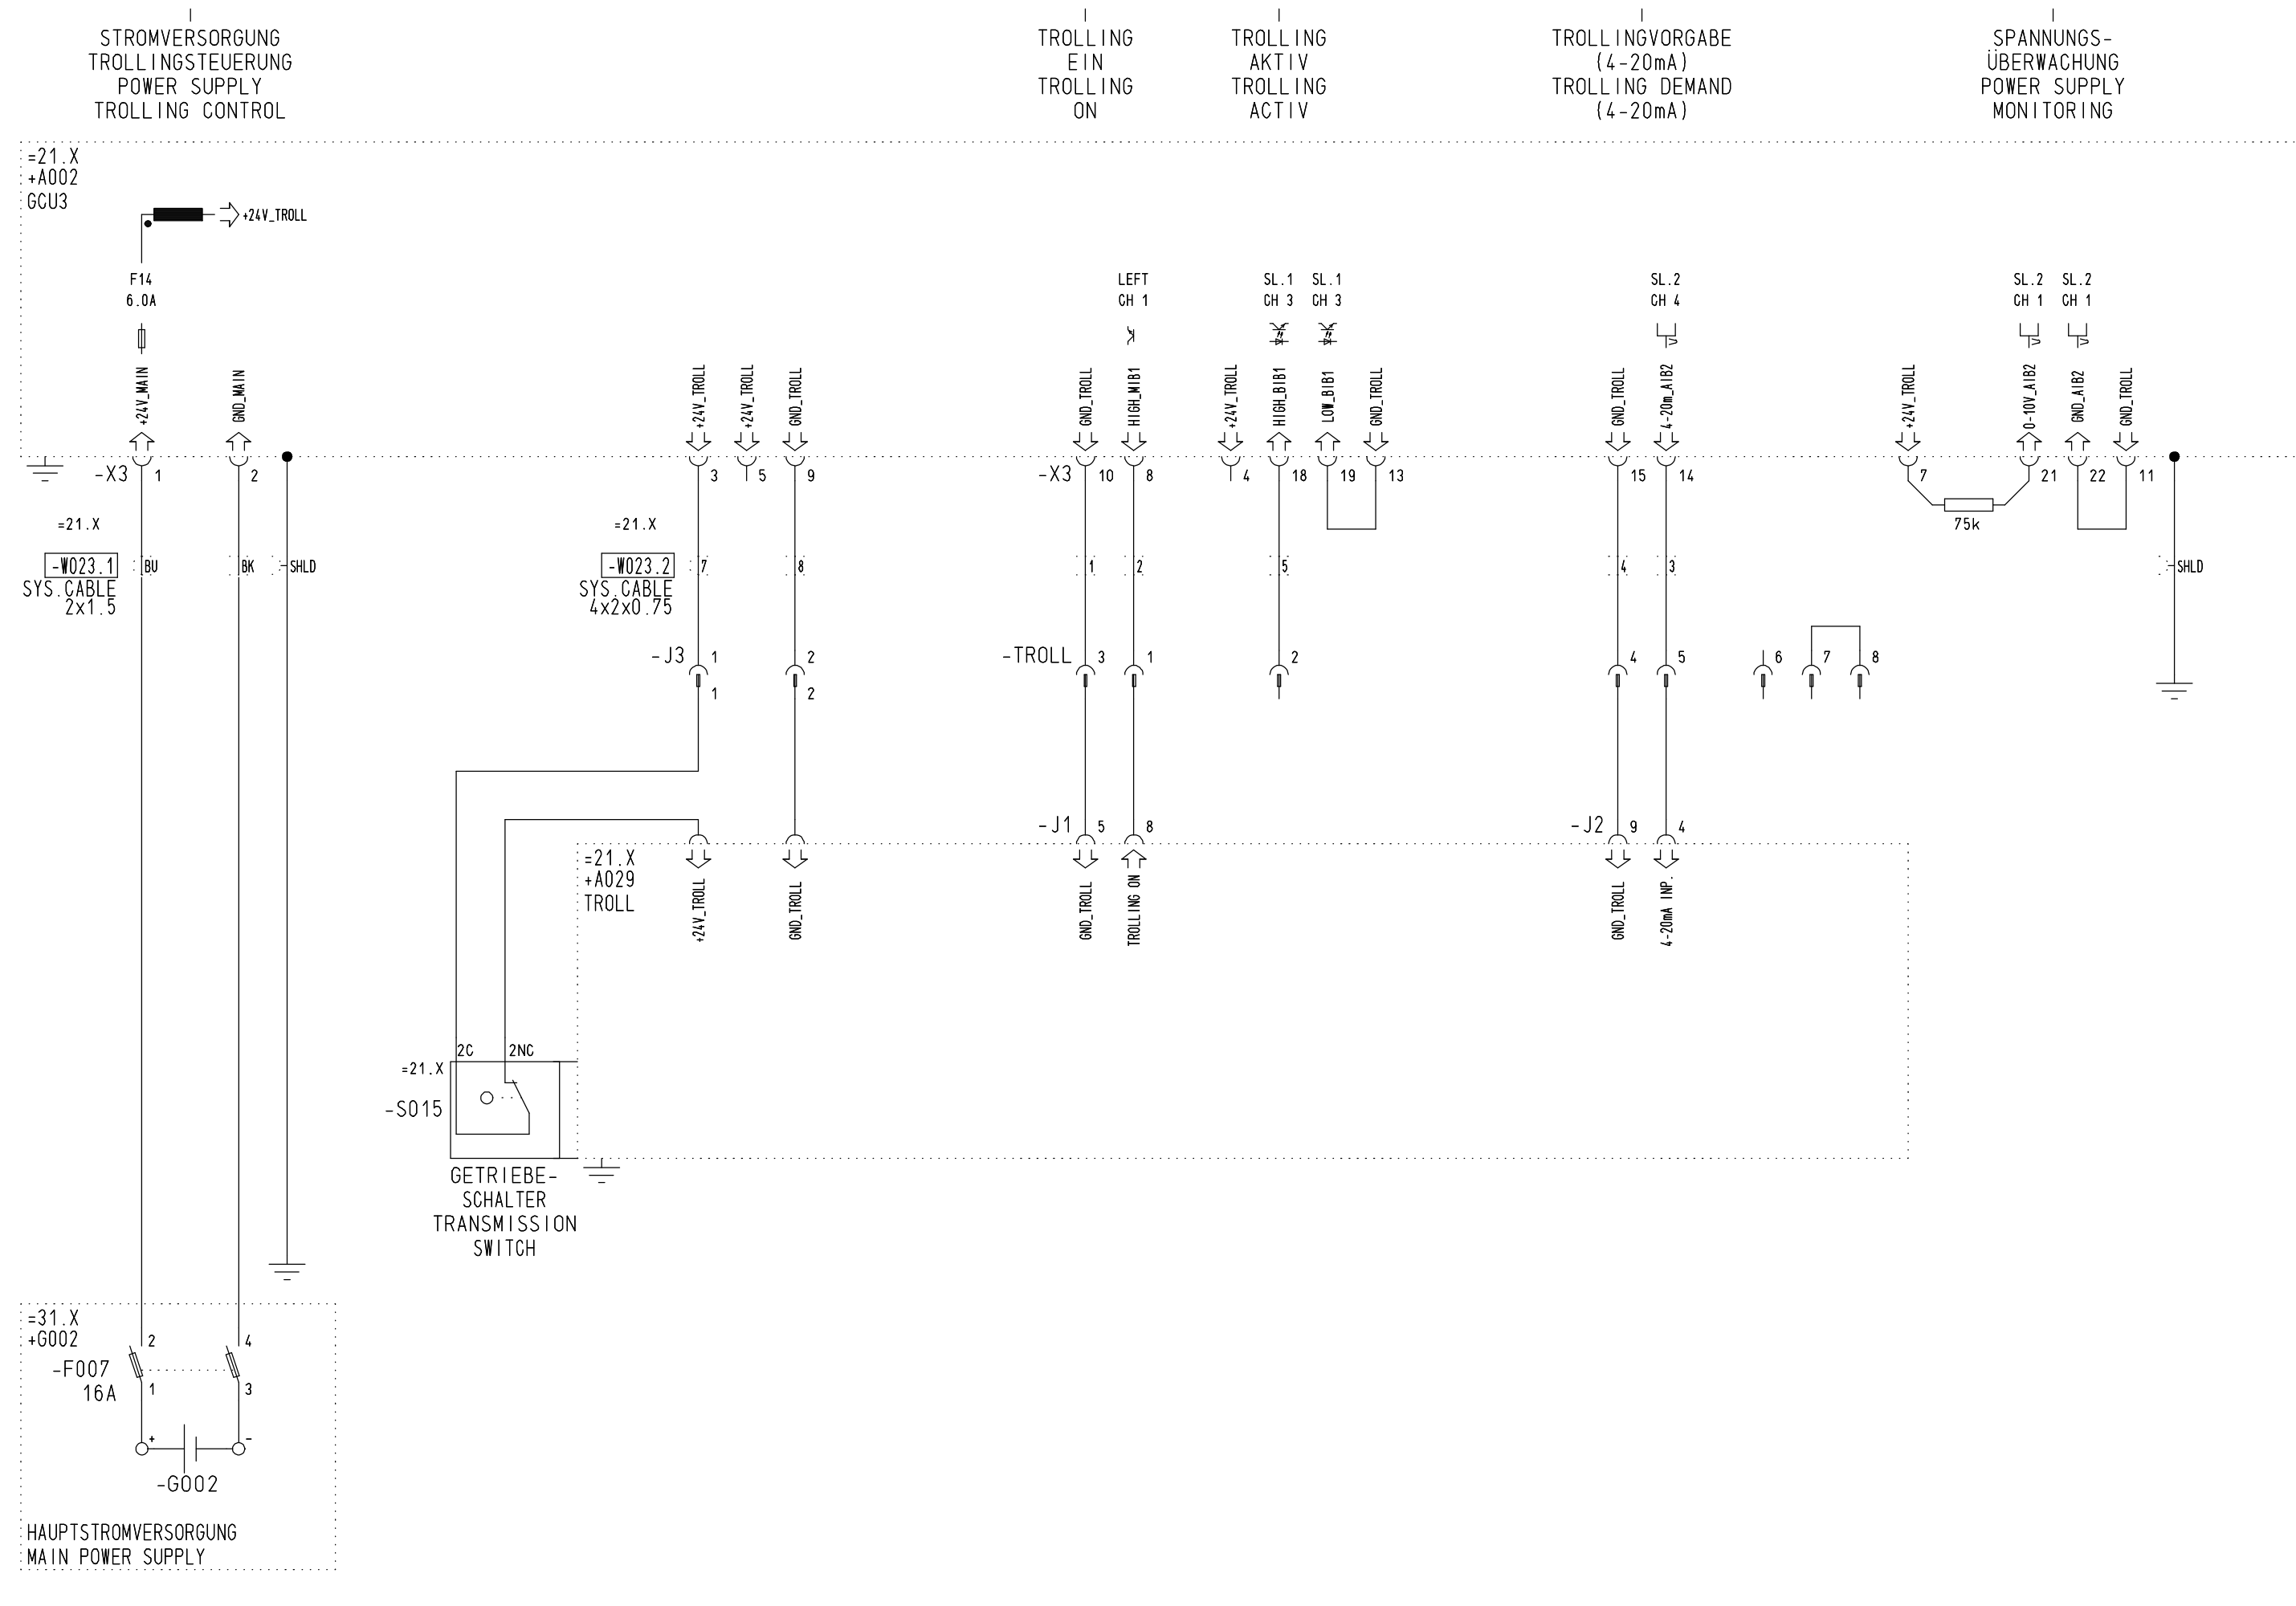

CAD			Datum	Name	Benennung/Title			TWIN DISK GETRIEBE, TROLLINGSTEUERUNG E-TROLL (EC050)		
Bearb.			21.02.2018	SAUTER	SCHEMA VERKABELUNG			TWIN DISK GEARBOX, TROLLING CONTROL E-TROLL (EC050)		
Gepr.			21.02.2018	BOLL	ANLAGENAUTOMATION					
Norm.			21.02.2018	SAUTER	WIRING DIAGRAM					
Abt. TEA					PLANT AUTOMATION					
Auftrags-Nr.			Datum/Date	Name	Auftrag/Projekt			Zeichnungs-Nr. / Drawing No.		
Freigegeb.			26.02.2018	Boll	BLUE-VIS			BZ00E50000064		
Aenderung / Revision					Referenz-Nr. / Reference-No.					

[illegible]

Keine Änderung ohne Zustimmung der
federführenden Konstruktion.
Any alterations are subject to the
approval of the design department.

© MTU Friedrichshafen GmbH
Schutzmerk DIN 34 beachten !
Refer to protection notice DIN 34 !

					CAD	Datum	Name
					Bearb.	21.02.2018	SAUTER
					Gepr.	21.02.2018	BOLL
					Norm.	21.02.2018	SAUTER
c	Rahmentexte bericht.	Freigegeb.	26.02.2018	Boll	Abt. TEA		
Buchst.	Aenderung / Revision	Auftrags-Nr.	Datum/Date	Name			



MTU Friedrichshafen GmbH

Benennung/Title
SCHEMA VERKABELUNG
ANLAGENAUTOMATION
WIRING DIAGRAM
PLANT AUTOMATION

REINTJES GETRIEBE, MIT WENDETEIL, TYP C, GRUNDUMFANG
REINTJES GEARBOX, WITH REVERSING, TYPE C, BASIC SCOPE

Auftrag/
Projekt BLUE-VIS
Zeichnungs-Nr.
Drawing No. BZ00E50000064

Blatt
Sheet 144

Keine Änderung ohne Zustimmung der
federführenden Konstruktion.
Any alterations are subject to the
approval of the design department.

© MTU Friedrichshafen GmbH
Schutzvermerk DIN 34 beachten !
Refer to protection notice DIN 34 !

					CAD	Datum	Name
					Bearb.	21.02.2018	SAUTER
					Gepr.	21.02.2018	BOLL
					Norm.	21.02.2018	SAUTER
c	Rahmentexte bericht.	Freigegeb.	26.02.2018	Boll	Abt. TEA		
Buchst.	Aenderung / Revision	Auftrags-Nr.	Datum/Date	Name			



MTU Friedrichshafen GmbH


Benennung/Title
SCHEMA VERKABELUNG
ANLAGENAUTOMATION
WIRING DIAGRAM
PLANT AUTOMATION

REINTJES GETRIEBE, MIT WENDETEIL, TYP C, ERWEIT. UMFANG REINTJES GEARBOX, WITH REVERSING, TYPE C, EXTENDED SCOPE			
Auftrag/ Projekt	BLUE-VIS	Zeichnungs-Nr. Drawing No.	BZ00E50000064
Referenz-Nr./Reference-No.	-----		
			Blatt Sheet 146

Keine Änderung ohne Zustimmung der
federführenden Konstruktion.
Any alterations are subject to the
approval of the design department.

© MTU Friedrichshafen GmbH
Schutzvermerk DIN 34 beachten !
Refer to protection notice DIN 34 !

013R001F

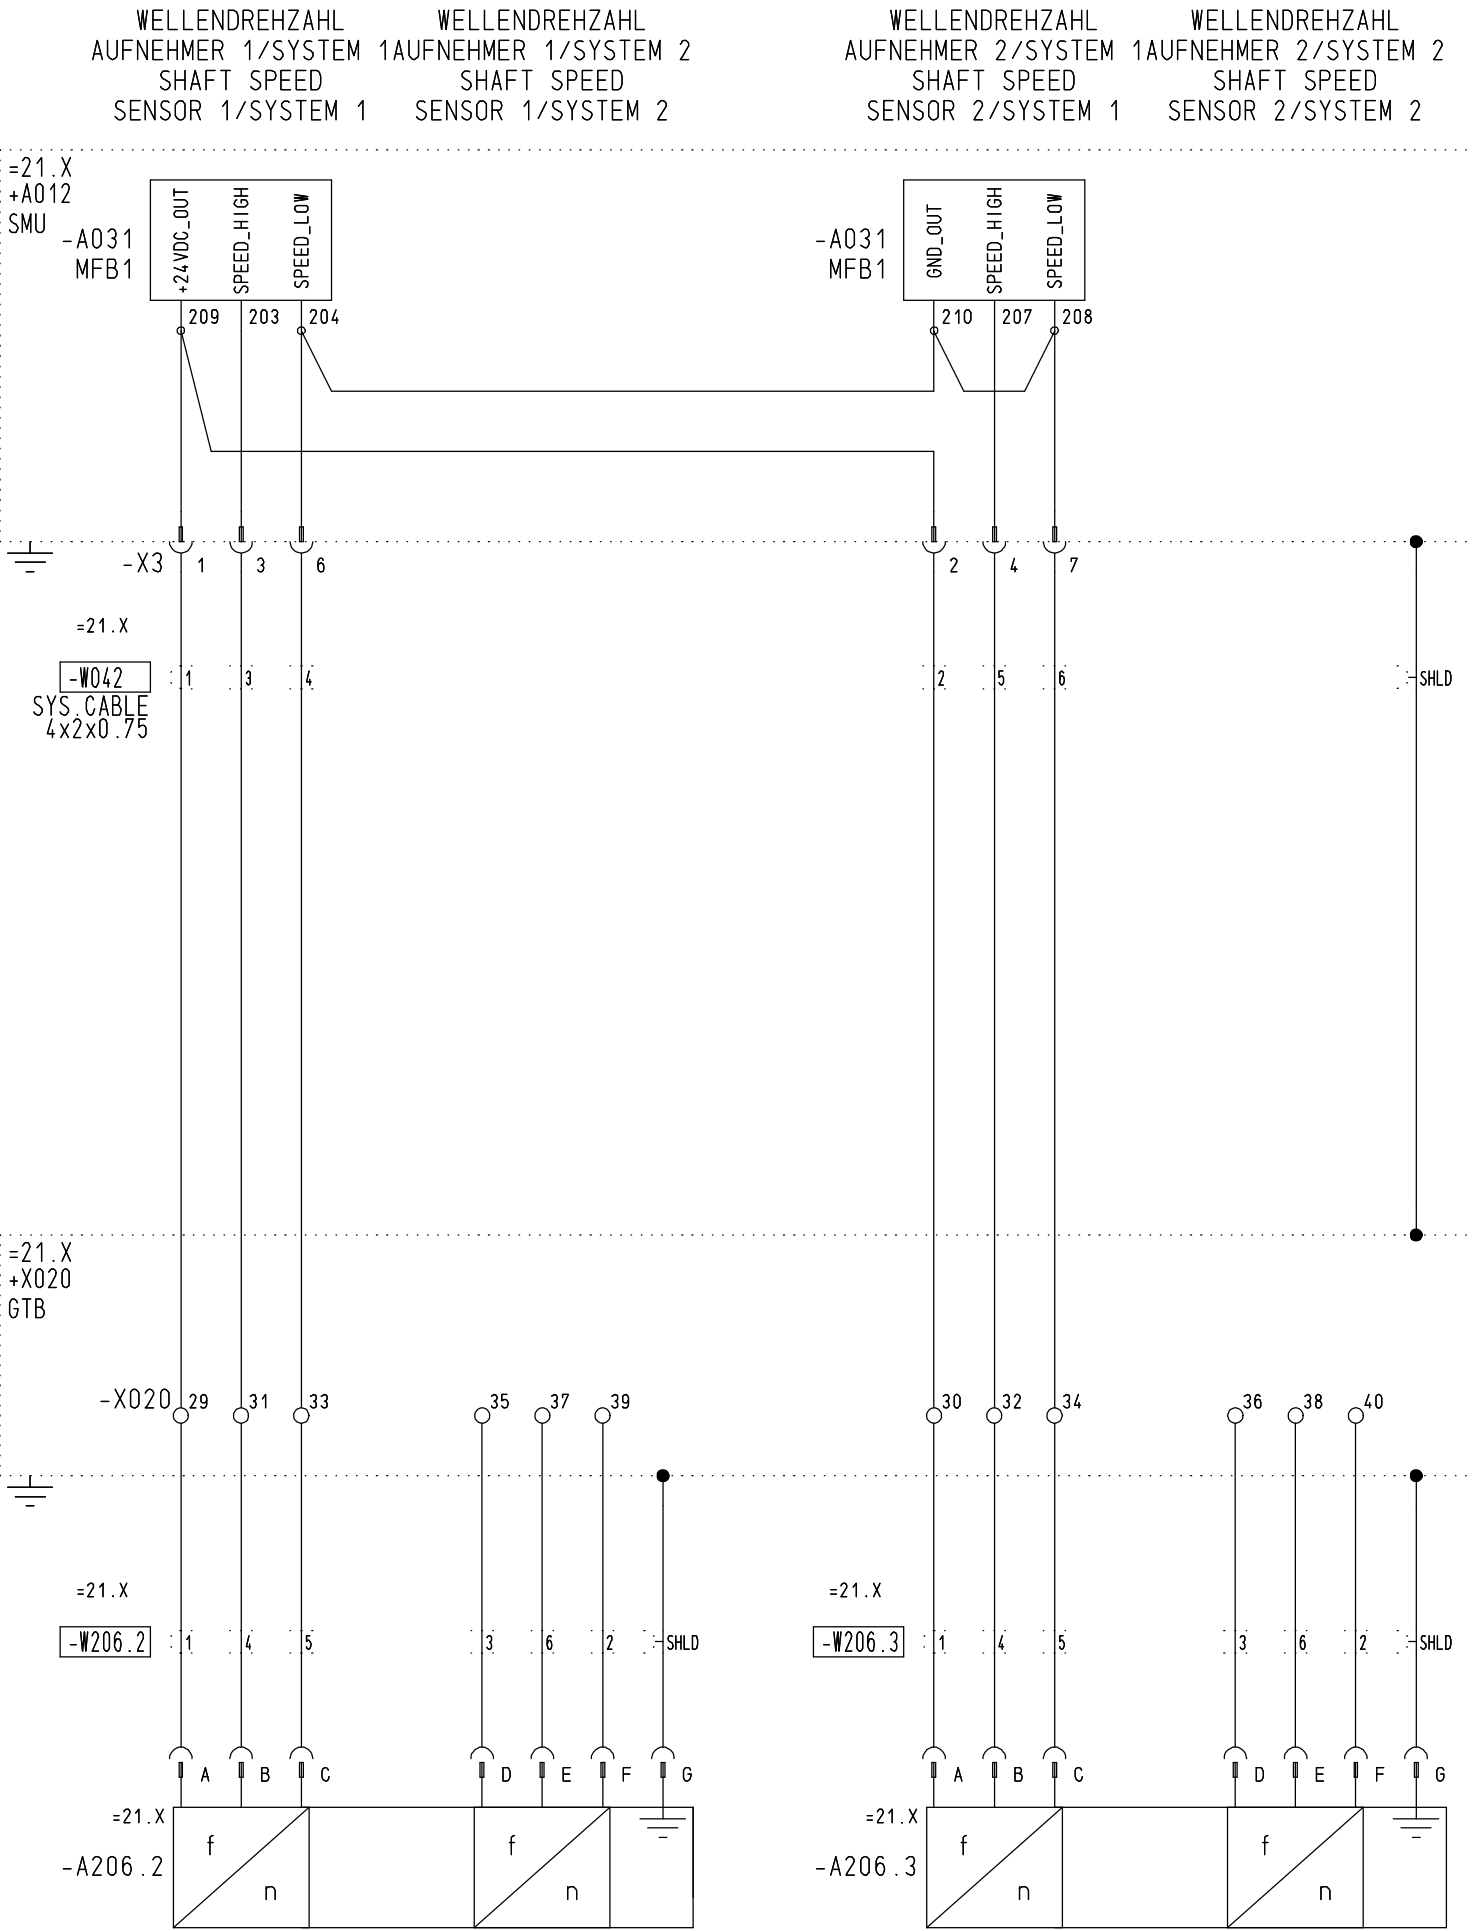

					CAD	Datum	Name
					Bearb.	21.02.2018	SAUTER
					Gepr.	21.02.2018	BOLL
c	Rahmentexte bericht.	Freigegeb.	26.02.2018	Boll	Norm.	21.02.2018	SAUTER
Buchst.	Aenderung / Revision	Auftrags-Nr.	Datum/Date	Name	Abt. TEA		



MTU Friedrichshafen GmbH

Benennung/Title
SCHEMA VERKABELUNG
ANLAGENAUTOMATION
WIRING DIAGRAM
PLANT AUTOMATION

REINTJES GETRIEBE, MIT WENDETEIL, TYP C, WELLENDREHZAHL		
REINTJES GEARBOX, WITH REVERSING, TYPE C, SHAFT SPEED		
Auftrag/ Projekt	BLUE-VIS	Zeichnungs-Nr. Drawing No.
Referenz-Nr./Reference-No.		
BZ00E50000064		Blatt Sheet
		149

GÜLTIG FÜR: VALID FOR:
VLJ 2230

MTU Friedrichshafen GmbH
Schutzvermerk DIN 34 beachten !
Refer to protection notice DIN 34 !

Keine Änderung ohne Zustimmung der
federführenden Konstruktion.
Any alterations are subject to the
approval of the design department.

© MTU Friedrichshafen GmbH
Schutzvermerk DIN 34 beachten !
Refer to protection notice DIN 34 !

					CAD	Datum	Name
					Bearb.	21.02.2018	SAUTER
					Gepr.	21.02.2018	BOLL
					Norm.	21.02.2018	SAUTER
c	Rahmentexte bericht.	Freigegeb.	26.02.2018	Boll	Abt. TEA		
Buchst.	Aenderung / Revision	Auftrags-Nr.	Datum/Date	Name			



MTU Friedrichshafen GmbH

Benennung/Title
SCHEMA VERKABELUNG
ANLAGENAUTOMATION
WIRING DIAGRAM
PLANT AUTOMATION


REINTJES GETRIEBE, OHNE WENDETEIL, TYP C, GRUNDUMFANG REINTJES GEARBOX, WITHOUT REVERSING, TYPE C, BASIC SCOPE			
Auftrag/ Projekt	BLUE-VIS	Zeichnungs-Nr. Drawing No.	BZ00E50000064
Referenz-Nr./Reference-No.	-----		
		Blatt Sheet	151

Keine Änderung ohne Zustimmung der
federführenden Konstruktion.
Any alterations are subject to the
approval of the design department.

© MTU Friedrichshafen GmbH
Schutzvermerk DIN 34 beachten !
Refer to protection notice DIN 34 !

013R001F

RUPLAN

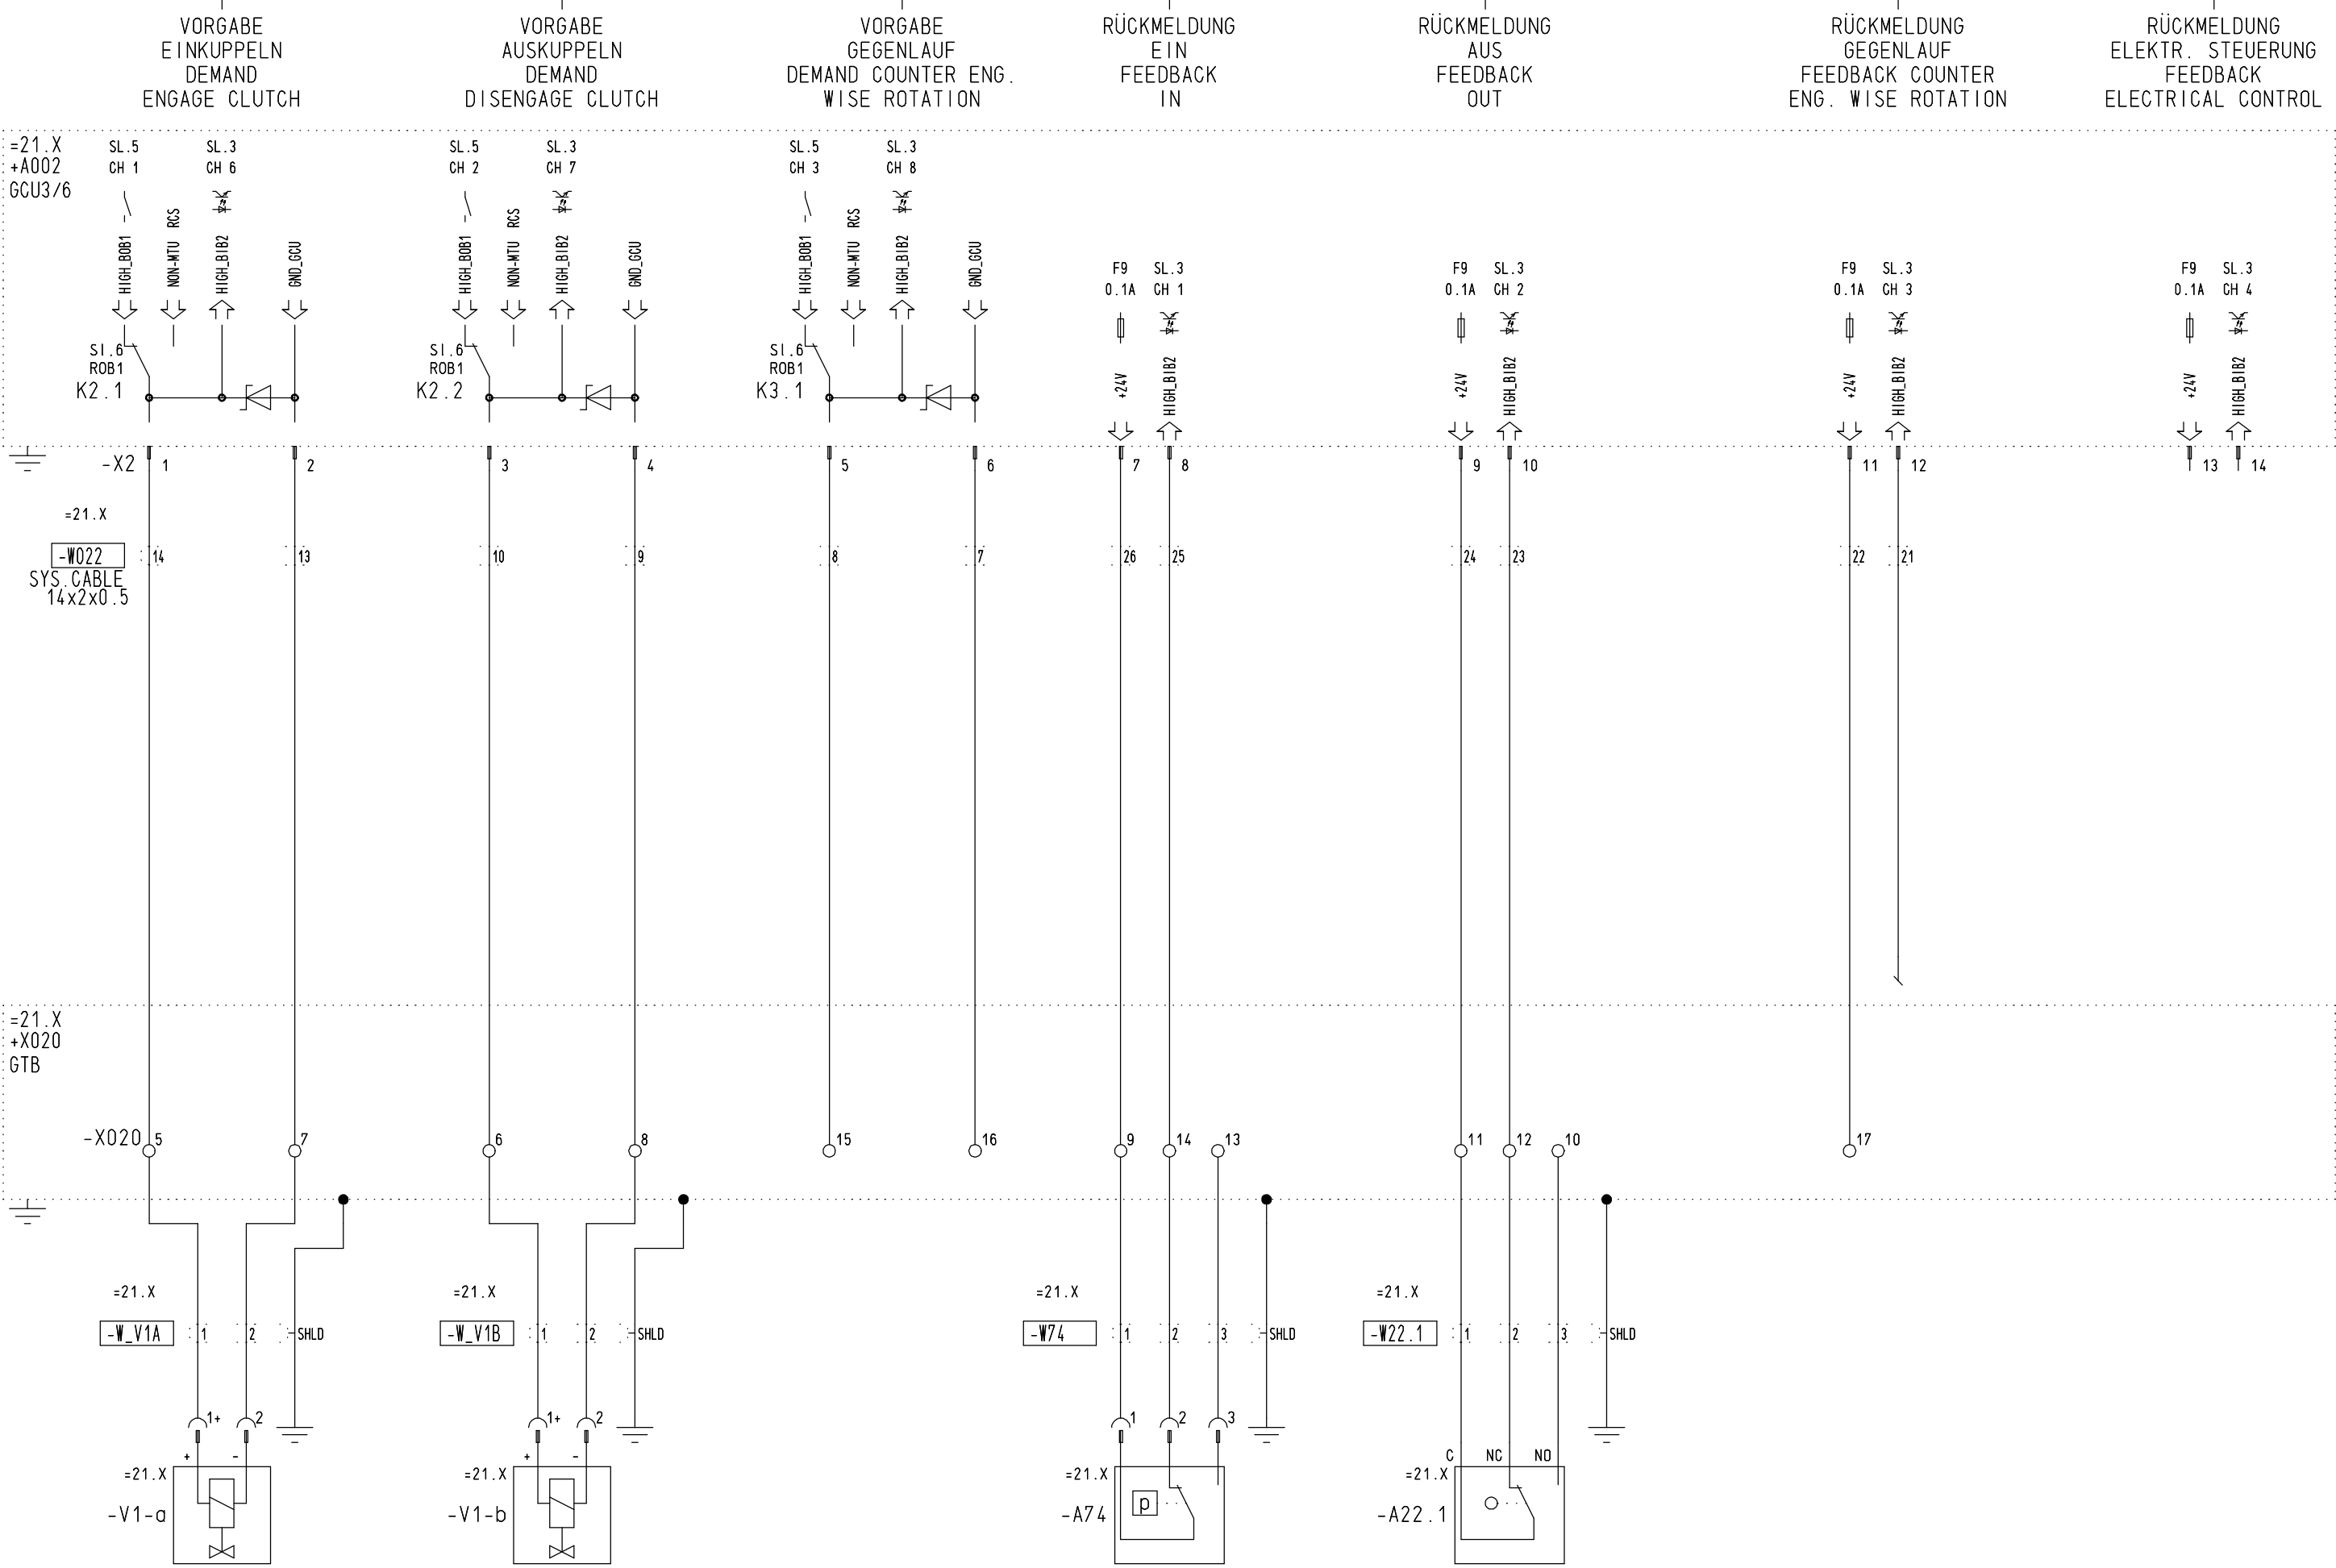

	CAD	Datum	Name
	Bearb.	21.02.2018	SAUTER
	Gepr.	21.02.2018	BOLL
	Norm.	21.02.2018	SAUTER
	Abt. TEA		





MTU Friedrichshafen GmbH

Benennung/Title
SCHEMA VERKABELUNG
ANLAGENAUTOMATION
WIRING DIAGRAM
PLANT AUTOMATION

REINTJES GETRIEBE, OHNE WENDETEIL, TYP C, ERWEIT. UMFANG REINTJES GEARBOX, WITHOUT REVERSING, TYPE C, EXTENDED SCOPE	
Auftrag/Projekt BLUE-VIS	Zeichnungs-Nr. Drawing No. BZ00E50000064
Referenz-Nr./Reference-No. -----	


DIN A3

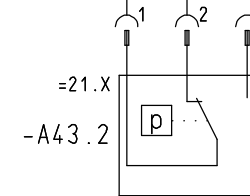 Blatt
Sheet 154

Keine Änderung ohne Zustimmung der
federführenden Konstruktion.
Any alterations are subject to the
approval of the design department.

© MTU Friedrichshafen GmbH
Schutzvermerk DIN 34 beachten !
Refer to protection notice DIN 34 !

013R001F

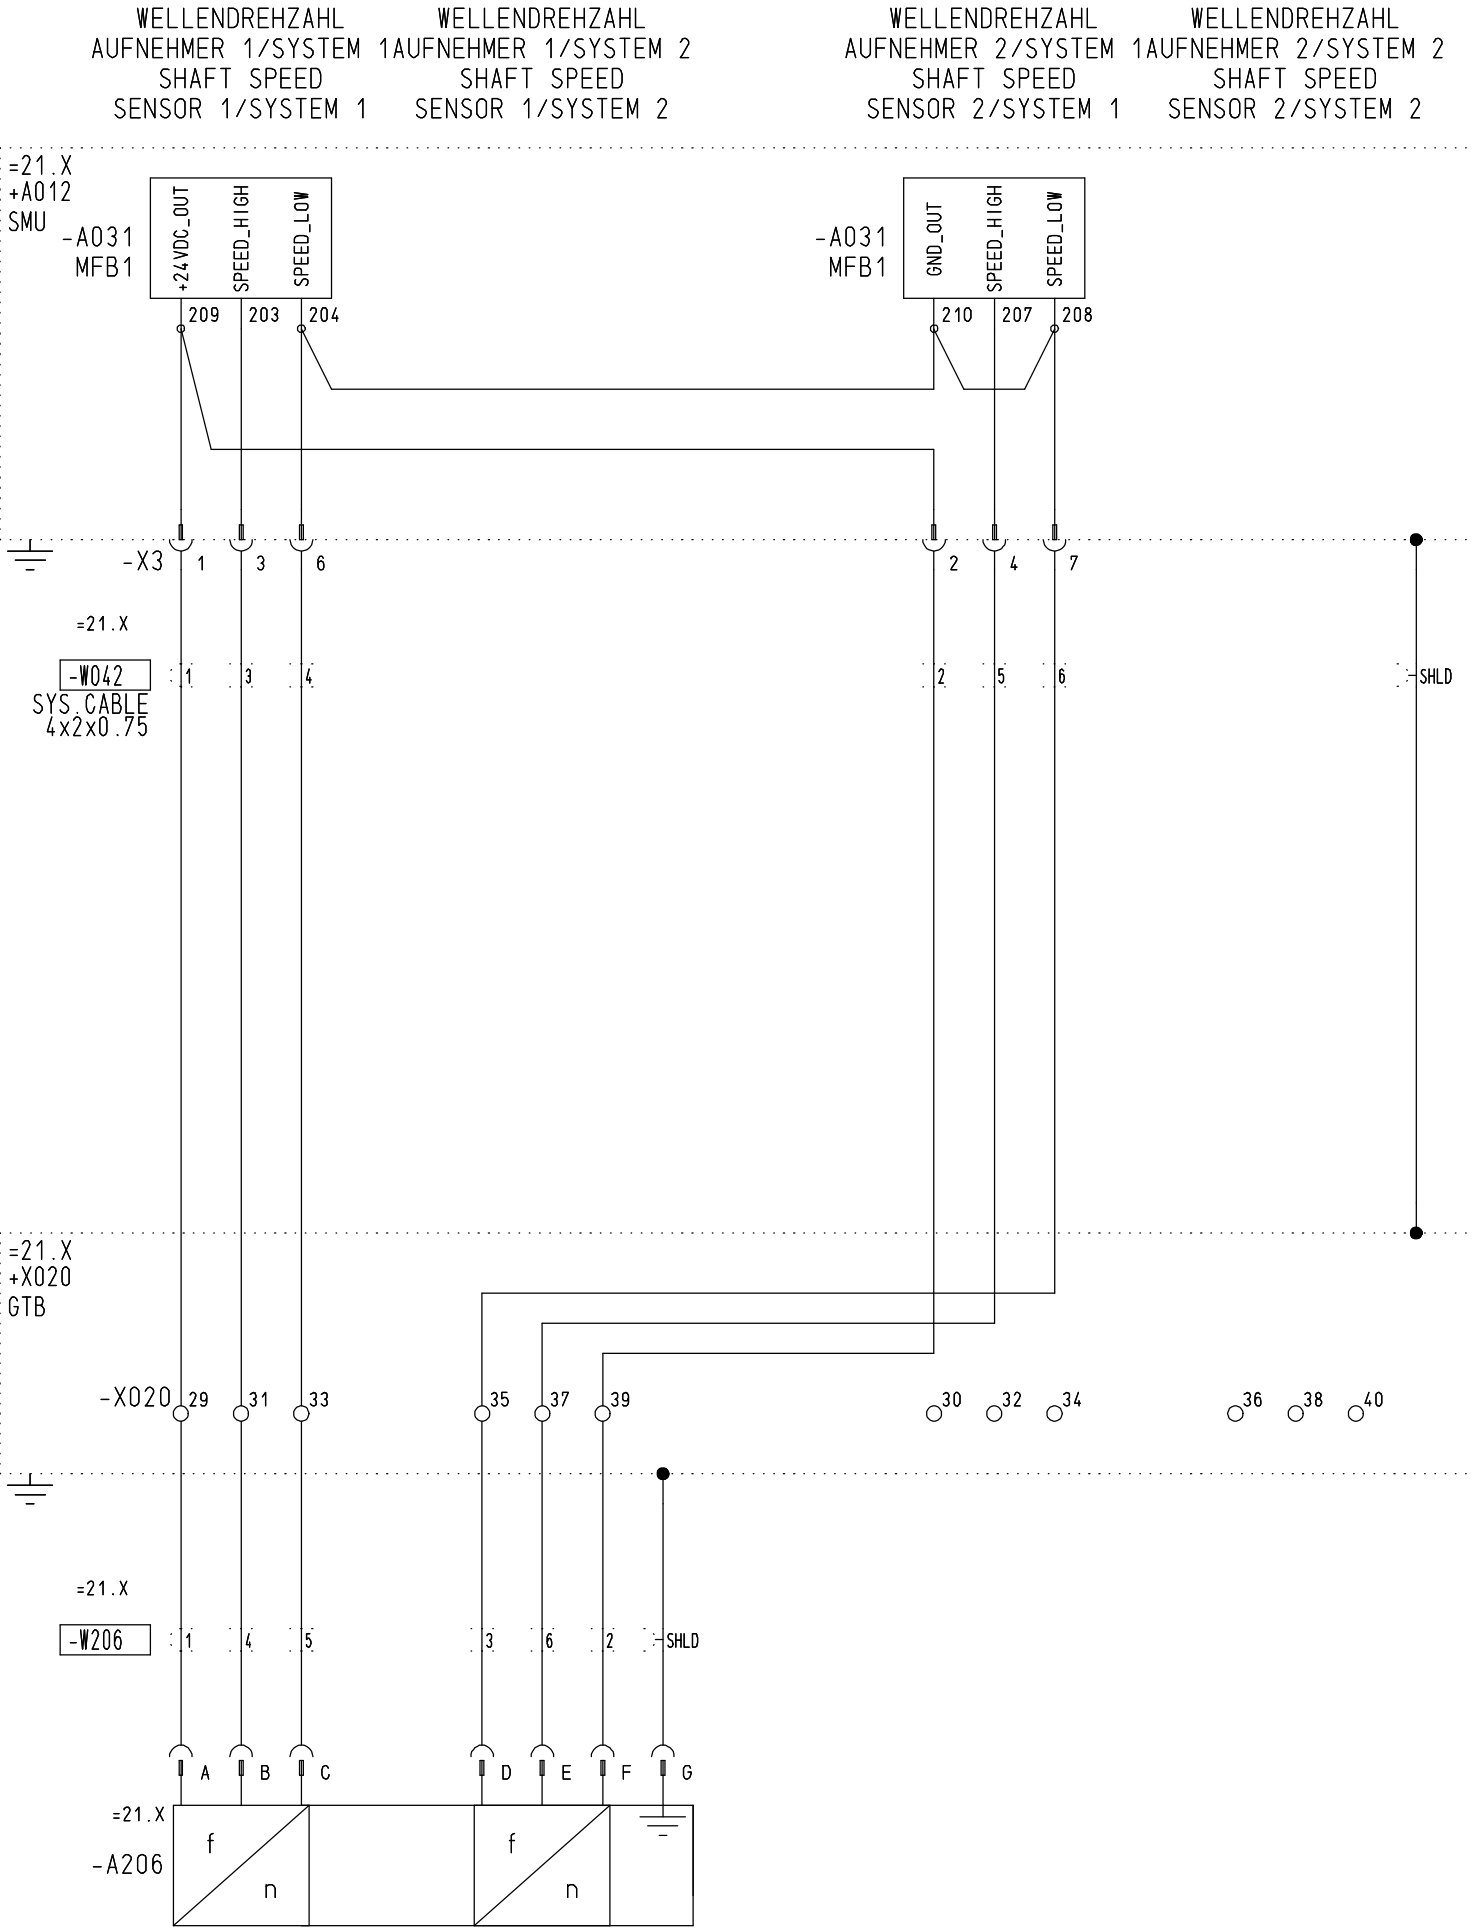

					CAD	Datum	Name	 MTU Friedrichshafen GmbH	Benennung/Title SCHEMA VERKABELUNG ANLAGENAUTOMATION WIRING DIAGRAM PLANT AUTOMATION	REINTJES GETRIEBE, OHNE WENDETEIL, TYP C, WELLENDREHZAHL					
					Bearb.	21.02.2018	SAUTER			REINTJES GEARBOX, WITHOUT REVERSING, TYPE C, SHAFT SPEED					
					Gepr.	21.02.2018	BOLL								
					Norm.	21.02.2018	SAUTER								
c	Rahmentexte bericht.	Freigegeb.	26.02.2018	Boll						Auftrag/ Projekt	BLUE-VIS	Zeichnungs-Nr. Drawing No.	BZ00E50000064	Blatt Sheet	156
Buchst.	Aenderung / Revision	Auftrags-Nr.	Datum/Date	Name	Abt. TEA					Referenz-Nr./Reference-No. -----					

1

2

3

4

5

6

7

8

A

B

C

D

E

F

HINWEIS

PRINZIP-SCHALTPLAN FÜR UNBEKANNTES
REINTJES GETRIEBE

NUR ZUR INFORMATION

NOTE

GENERAL CIRCUIT DIAGRAM FOR UNKNOWN
REINTJES GEARBOX

FOR INFORMATION ONLY

Keine Änderung ohne Zustimmung der
federführenden Konstruktion.
Any alterations are subject to the
approval of the design department.

© MTU Friedrichshafen GmbH
Schutzmerk DIN 34 beachten !
Refer to protection notice DIN 34 !

					CAD	Datum	Name	 MTU Friedrichshafen GmbH	Benennung/Title SCHEMA VERKABELUNG ANLAGENAUTOMATION WIRING DIAGRAM PLANT AUTOMATION	REINTJES GETRIEBE, MAXIMALUMFANG, TYP F, HINWEISE REINTJES GEARBOX, MAXIMAL SCOPE, TYPE F, INSTRUCTIONS	Auftrag/ Projekt BLUE-VIS	Zeichnungs-Nr. Drawing No. BZ00E50000064	Blatt Sheet 157
					Bearb.	21.02.2018	SAUTER						
					Gepr.	21.02.2018	BOLL						
c	Rahmentexte bericht.	Freigegeb.	26.02.2018	Boll	Norm.	21.02.2018	SAUTER						
Buchst.	Änderung / Revision	Auftrags-Nr.	Datum/Date	Name	Abt. TEA								

RUPLAN

1

2

3

4

5

6


7

8

DIN A3

Keine Änderung ohne Zustimmung der
federführenden Konstruktion.
Any alterations are subject to the
approval of the design department.

© MTU Friedrichshafen GmbH
Schutzvermerk DIN 34 beachten !
Refer to protection notice DIN 34 !

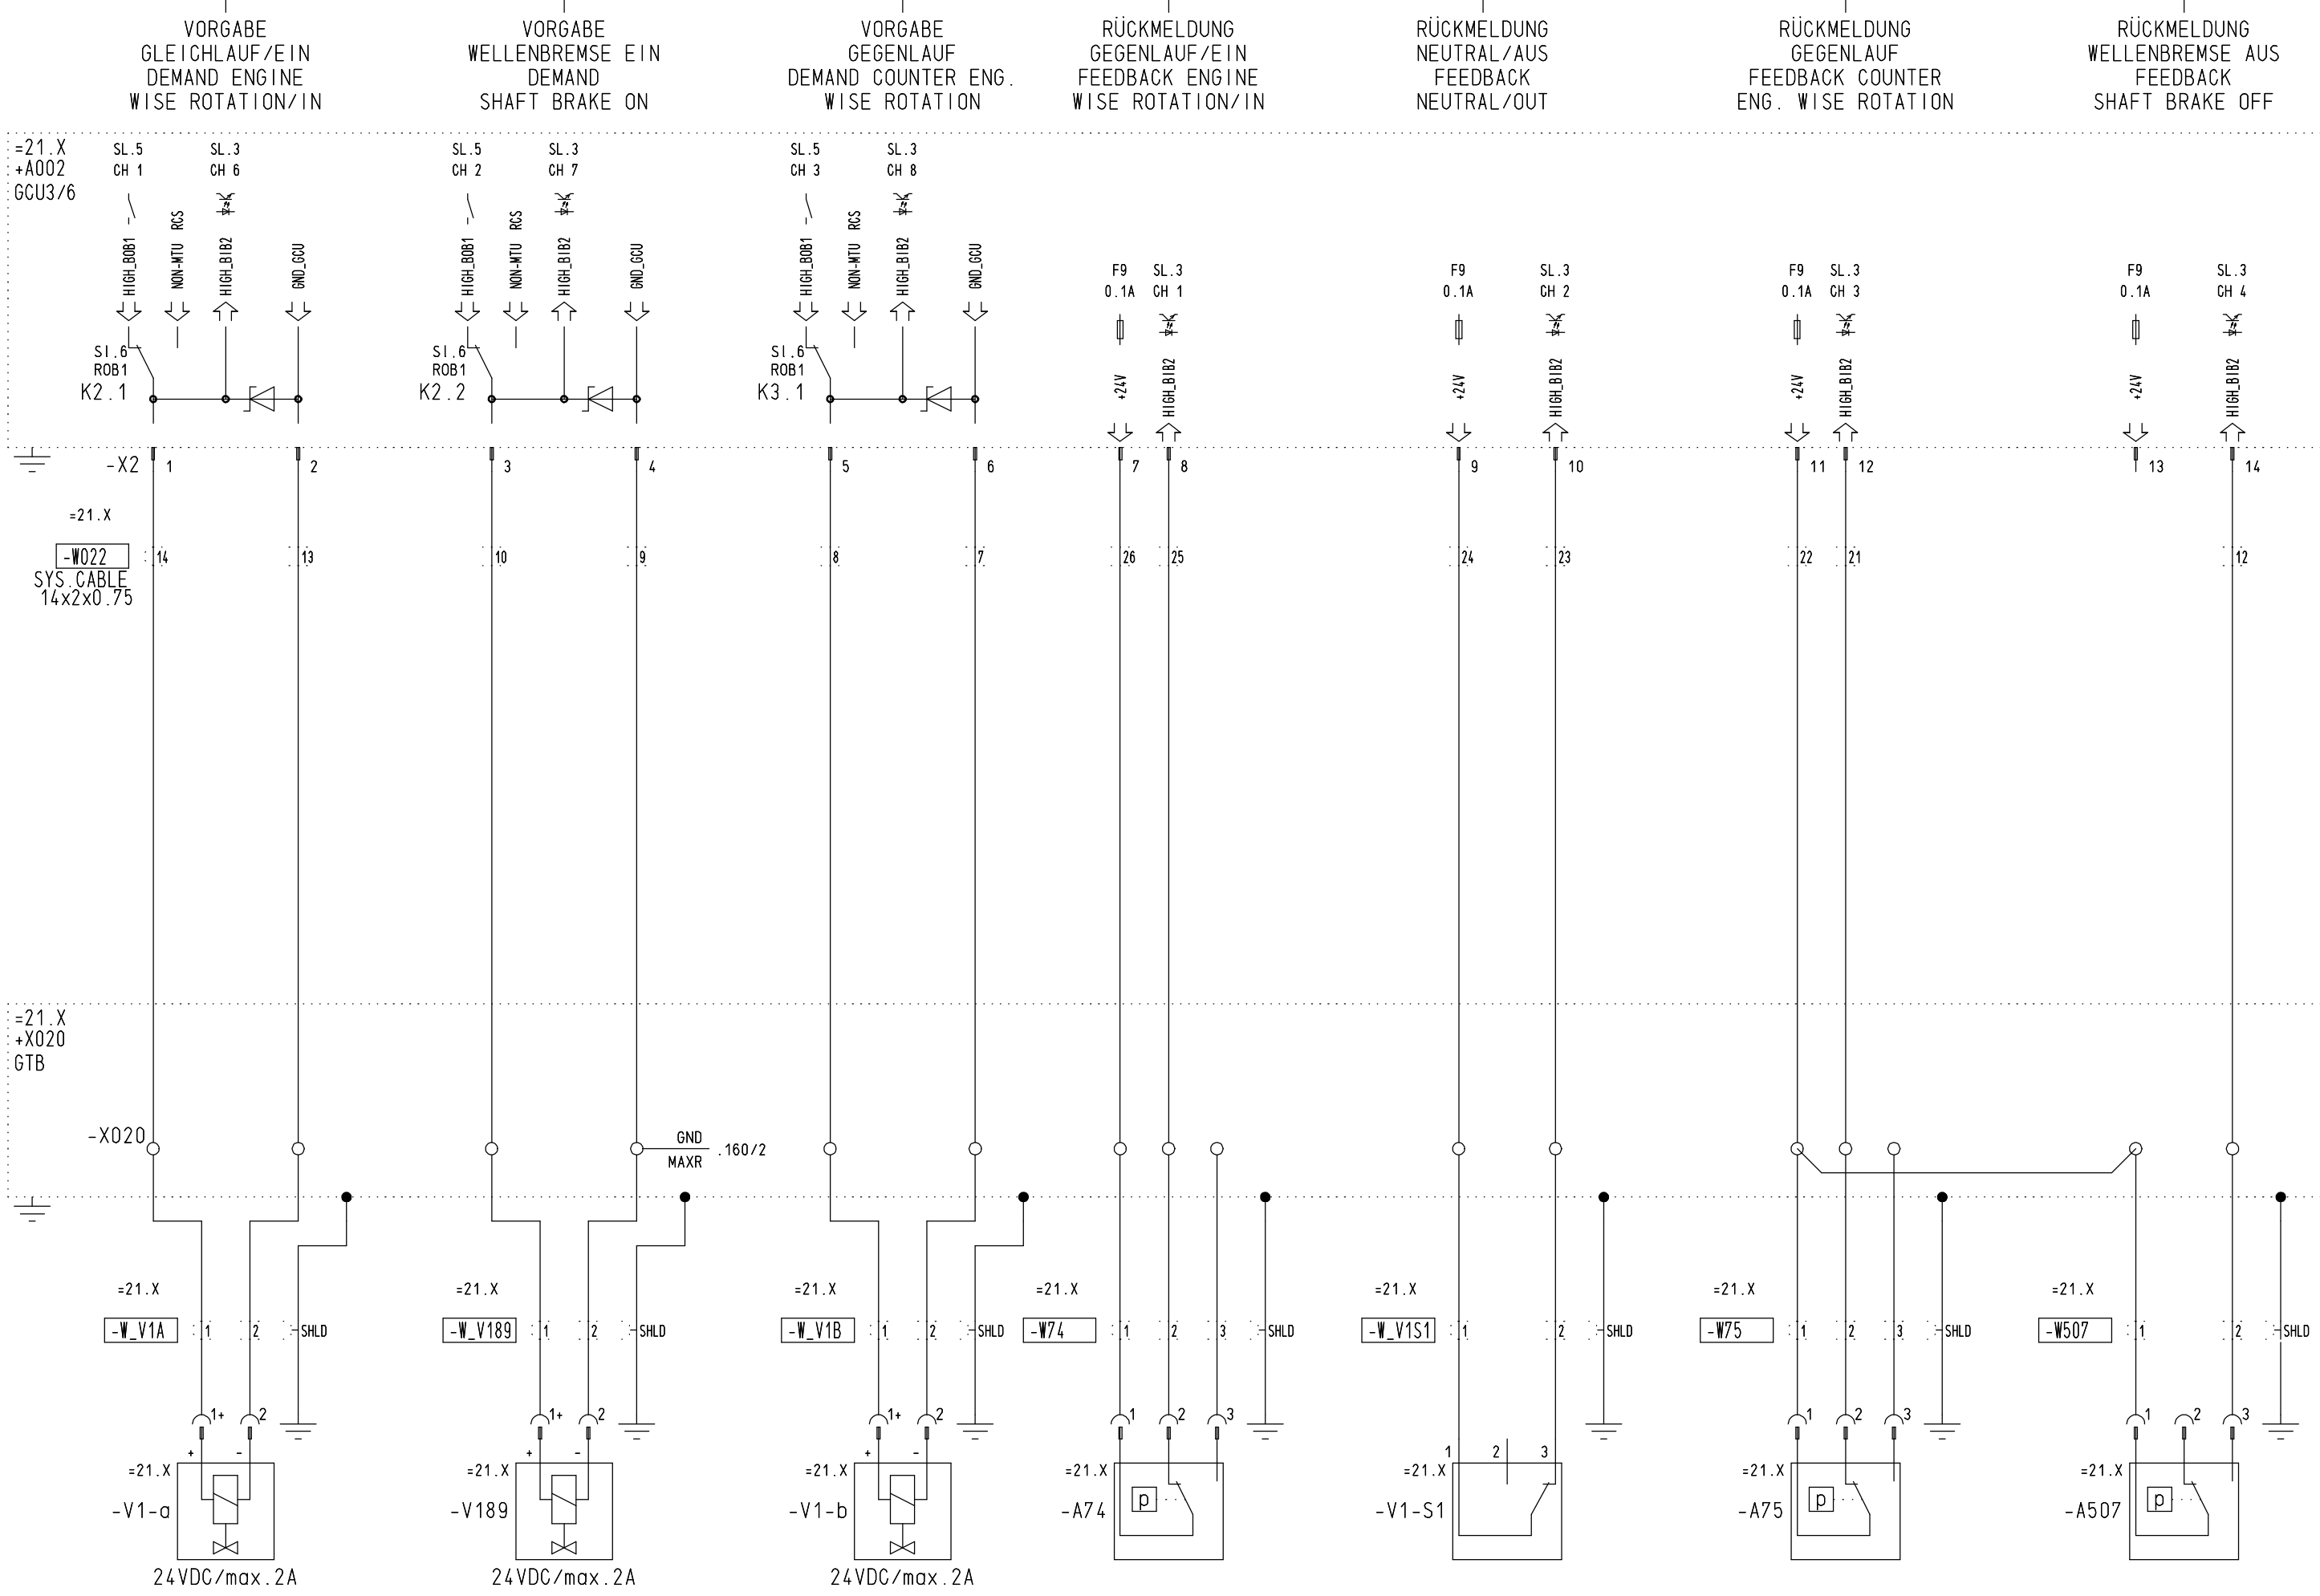

					CAD	Datum	Name	 MTU Friedrichshafen GmbH	Benennung/Title SCHEMA VERKABELUNG ANLAGENAUTOMATION WIRING DIAGRAM PLANT AUTOMATION	REINTJES GETRIEBE, MAXIMALUMFANG, TYP F, ERWEIT. UMFANG				
					Bearb.	21.02.2018	SAUTER			REINTJES GEARBOX, MAXIMAL SCOPE, TYPE F, EXTENDED SCOPE				
					Gepr.	21.02.2018	BOLL							
c	Rahmentexte bericht.		Freigegeb.	26.02.2018	Boll	Norm.	21.02.2018			SAUTER				
Buchst.	Aenderung / Revision		Auftrags-Nr.	Datum/Date	Name	Abt. TEA				Auftrag/Projekt BLUE-VIS		Zeichnungs-Nr. BZ00E50000064	Blatt 158 Sheet 158	
										Referenz-Nr./Reference-No.		-----		

 MTU Friedrichshafen GmbH

REINTJES GETRIEBE, MAXIMALUMFANG, TYP F, ERWEIT. UMFANG		
REINTJES GEARBOX, MAXIMAL SCOPE, TYPE F, EXTENDED SCOPE		
Auftrag/ Projekt	BLUE-VIS	Zeichnungs-Nr. Drawing No. BZ00E50000064
Referenz-Nr./Reference-No.		Blatt Sheet 160

