

	1	2	3	4	5	6	7	8	
A	<table><tr><td>A-Buchst. Rev. Ltr.</td><td>Datum Date</td><td>Änd.Nr. Rev.No.</td><td>Blattanzahl No. of sheets</td><td>Änderung Revision</td><td>Geänderte Seiten Modified Pages</td></tr><tr><td>-</td><td>05.03.2010</td><td>58509</td><td>21</td><td>war kZ</td><td>1-21</td></tr><tr><td>a</td><td>26.04.2012</td><td>79440</td><td>23</td><td>Verkabelung geändert</td><td>1-23</td></tr><tr><td>b</td><td>07.03.2018</td><td>Freigegeben</td><td>26</td><td>Verkabelung geändert</td><td>1, 13-26</td></tr></table>								A-Buchst. Rev. Ltr.	Datum Date	Änd.Nr. Rev.No.	Blattanzahl No. of sheets	Änderung Revision	Geänderte Seiten Modified Pages	-	05.03.2010	58509	21	war kZ	1-21	a	26.04.2012	79440	23	Verkabelung geändert	1-23	b	07.03.2018	Freigegeben	26	Verkabelung geändert	1, 13-26	A	
A-Buchst. Rev. Ltr.	Datum Date	Änd.Nr. Rev.No.	Blattanzahl No. of sheets	Änderung Revision	Geänderte Seiten Modified Pages	
-	05.03.2010	58509	21	war kZ	1-21	
a	26.04.2012	79440	23	Verkabelung geändert	1-23	
b	07.03.2018	Freigegeben	26	Verkabelung geändert	1, 13-26	
B									B	
C									C	
D									D	
E									E	
F									F	
013R001F	<table><tr><td colspan="2"></td><td colspan="2"></td><td colspan="2"></td><td colspan="2">CAD</td><td>Datum</td><td>Name</td><td rowspan="4"> MTU Friedrichshafen GmbH</td><td rowspan="4">Benennung/Title SCHEMA VERKABELUNG ANTRIEBSSTEUERUNG WIRING DIAGRAM PROPULSION CONTROL</td><td colspan="2">NULLBLATT ACTIVE SHEET RECORD</td><td></td></tr><tr><td colspan="2"></td><td colspan="2"></td><td colspan="2"></td><td colspan="2">Bearb.</td><td>05.03.2018</td><td>SAUTER</td><td></td></tr><tr><td colspan="2"></td><td colspan="2"></td><td colspan="2"></td><td colspan="2">Gepr.</td><td>05.03.2018</td><td>BOLL</td><td></td></tr><tr><td colspan="2">b</td><td colspan="2">Verkabelung geändert</td><td colspan="2">Freigegeb</td><td colspan="2">07.03.2018</td><td>Boll</td><td></td><td>Norm.</td><td>05.03.2018</td><td>SAUTER</td><td></td></tr><tr><td colspan="2">Buchst.</td><td colspan="2">Änderung / Revision</td><td colspan="2">Auftrags-Nr.</td><td colspan="2">Datum/Date</td><td colspan="2">Name</td><td colspan="2">Abt. TEA</td><td colspan="2">Auftrag/ Projekt</td><td>BLUE-VIS</td><td>Zeichnungs-Nr. Drawing No.</td><td>BZ00E50200068</td><td>Blatt Sheet</td><td>0</td></tr></table>														CAD		Datum	Name	 MTU Friedrichshafen GmbH	Benennung/Title SCHEMA VERKABELUNG ANTRIEBSSTEUERUNG WIRING DIAGRAM PROPULSION CONTROL	NULLBLATT ACTIVE SHEET RECORD									Bearb.		05.03.2018	SAUTER								Gepr.		05.03.2018	BOLL		b		Verkabelung geändert		Freigegeb		07.03.2018		Boll		Norm.	05.03.2018	SAUTER		Buchst.		Änderung / Revision		Auftrags-Nr.		Datum/Date		Name		Abt. TEA		Auftrag/ Projekt		BLUE-VIS	Zeichnungs-Nr. Drawing No.	BZ00E50200068	Blatt Sheet	0	
						CAD		Datum	Name	 MTU Friedrichshafen GmbH	Benennung/Title SCHEMA VERKABELUNG ANTRIEBSSTEUERUNG WIRING DIAGRAM PROPULSION CONTROL	NULLBLATT ACTIVE SHEET RECORD	
						Bearb.		05.03.2018	SAUTER	
						Gepr.		05.03.2018	BOLL	
b		Verkabelung geändert		Freigegeb		07.03.2018		Boll				Norm.	05.03.2018	SAUTER	
Buchst.		Änderung / Revision		Auftrags-Nr.		Datum/Date		Name		Abt. TEA		Auftrag/ Projekt		BLUE-VIS	Zeichnungs-Nr. Drawing No.	BZ00E50200068	Blatt Sheet	0	
RUPLAN		1	2	3	4	5	6	7	8	DIN A3	

Keine Änderung ohne Zustimmung der
federführenden Konstruktion.
Any alterations are subject to the
approval of the design department.

© MTU Friedrichshafen GmbH
Schutzvermerk DIN 34 beachten !
Refer to protection notice DIN 34 !

		1		2		3		4		5		6		7		8	
A 																	

DIE ADERN DER DARGESTELLTEN SCHIFFSKABEL SIND VON 1 BIS n DURCHNUMMERIERT. WERDEN SCHIFFSKABEL MIT ABWEICHENDER ADERKENNZEICHNUNG VERWENDET (Z.B. FARBKENNZEICHNUNG), SIND DIE ADERN SINNGEMÄSS ANZUSCHLIESSEN.

=21.X X	ANLAGE	DIESELMOTOR MOTOR X, MOTORRAUM
=31.X X	ANLAGE	HAUPTSTROMVERSORGUNGSANLAGE MOTOR X
=38.X X	ANLAGE	NOTSTROMVERSORGUNGSANLAGE MOTOR X
+A001	ORT	WACHSTAND LOP8 ODER LOP11
+A002	ORT	GETRIEBESTEUERUNG GCU3 ODER GCU6
+A005	ORT	MOTORMODUL EIM
+A008	ORT	ABGASKLAPPENSTEUERUNG FCU2
+A012	ORT	ÜBERWACHUNGSERWEITERUNG MEU1
+A012	ORT	WELLENDREHZAHLÜBERWACHUNG SMU1
+A020	ORT	ANTRIEBSSTEUERUNG UND -ÜBERWACHUNG PCMU
+G002	ORT	STROMVERSORGUNG
-XXXX	GERÄT	SIEHE SCHEMA SCHIFFSVERKABELUNG

THE INDIVIDUAL WIRES OF THE SHIP'S CABLES SHOWN ARE CONSECUTIVELY NUMBERED FROM 1 TO n. IF SHIP'S CABLES WITH DIFFERING WIRE IDENTIFICATIONS ARE USED (E.G. COLORED MARKINGS), THE WIRES MUST BE CONNECTED ANALOGOUSLY.

=21.X X	PLANT	ENGINE PLANT ENGINE X, ENGINE ROOM
=31.X X	PLANT	MAIN POWER SUPPLY SYSTEM ENGINE X
=38.X X	PLANT	EMERGENCY POWER SUPPLY ENGINE X
+A001	LOCATION	LOCAL OPERATING PANEL LOP8 OR LOP11
+A002	LOCATION	GEAR CONTROL UNIT GCU3 OR GCU6
+A005	LOCATION	ENGINE INTERFACE MODULE EIM
+A008	LOCATION	EXHAUST FLAP CONTROL FCU2
+A012	LOCATION	MONITORING EXTENSION UNIT MEU1
+A012	LOCATION	SHAFT SPEED MONITORING UNIT SMU1
+A020	LOCATION	PURPUSION CONTROL AND MONITORING PCMU
+G002	ORT	POWER SUPPLY
-XXXX	DEVICE	SEE SHIP WIRING DIAGRAM

DIE SCHNITTSTELLEN ZU DEN ÜBERWACHUNGS- UND STEUERUNGSSYSTEMEN (LOP, LOS, PIM4, ...) SIND DURCH SYMBOLE BESCHRIEBEN.

 SIGNALRICHTUNG: EINGANG

B1 ● STECKKARTE: BIB1

MC ——— SIGNALPEGEL: LOW(0VDC)

 SIGNALTYP: OPTOKOPPLER

CH 1 — KANALNUMMER: CHANNEL 1

SL.2 — STECKPLATZ: SLOT 2

THE INTERFACES AT THE MONITORING
AND CONTROL SYSTEMS (LOP, LOS, PIM4, ...) ARE SHOWN BY SYMBOLS.

 SIGNAL DIRECTION: INPUT


PRINTED CIRCUIT BOARD: BIB1

MC — SIGNAL LEVEL: LOW (0VDC)

 SIGNAL TYPE: OPTOCOUPLER

CH 1 CHANNEL NUMBER: CHANNEL 1

SL.2  PLUG-IN SLOT: SLOT 2

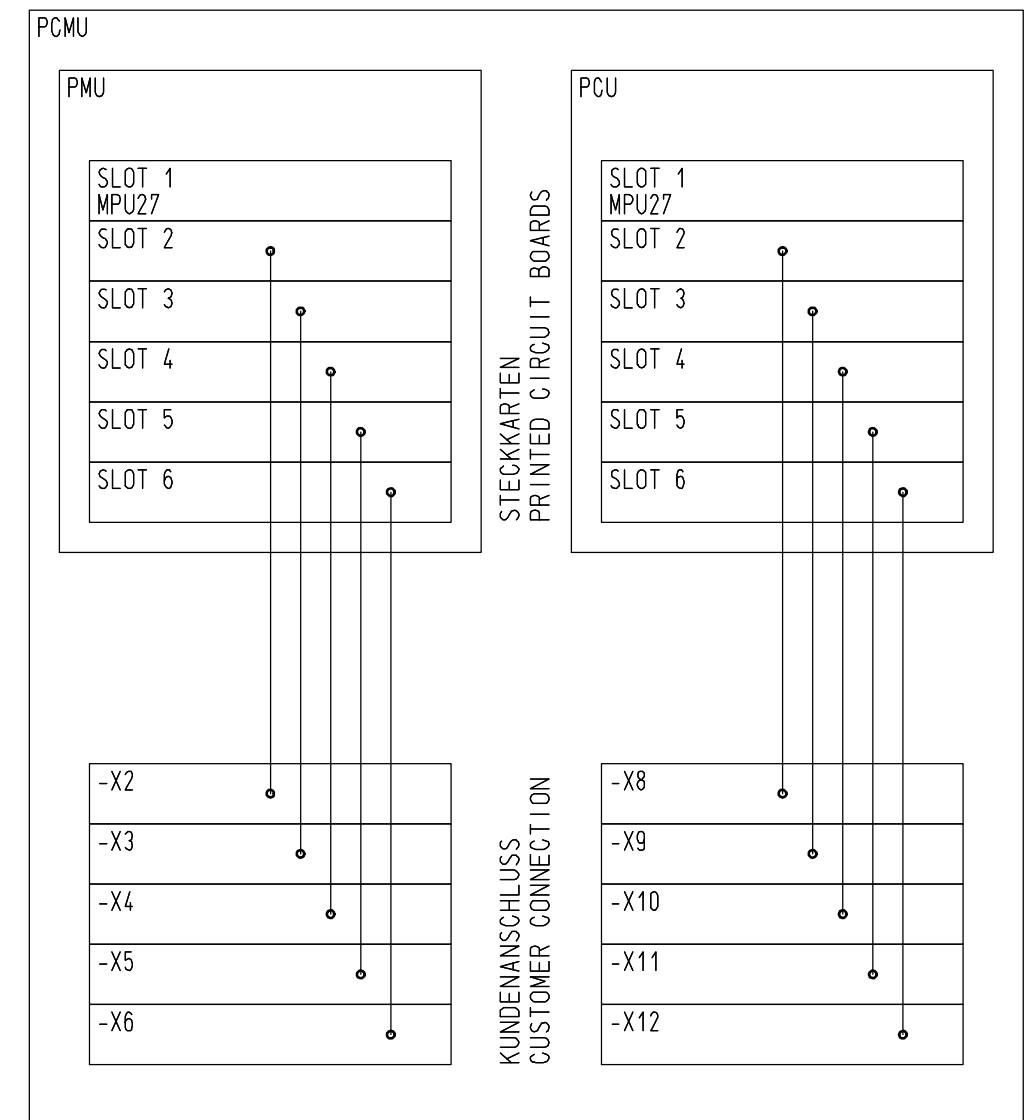

					CAD	Datum	Name
					Bearb.	05.03.2018	SAUTER
					Gepr.	05.03.2018	BOLL
b	Verkabelung geändert	Freigegeb	07.03.2018	Boll	Norm.	05.03.2018	SAUTER
Buchst.	Änderung / Revision	Auftrags-Nr.	Datum/Date	Name	Abt.	TEA	



MTU Friedrichshafen GmbH


Benennung/Title	SCHEMA VERKABELUNG ANTRIEBSSTEUERUNG WIRING DIAGRAM PROPULSION CONTROL
-----------------	---


HINWEISE INSTRUCTIONS


Auftrag/ Projekt	BLUE-VIS
Referenz-Nr./Reference-	

Zeichnungs-Nr. BZ00E50200068
Drawing No.

Blatt
Sheet 2

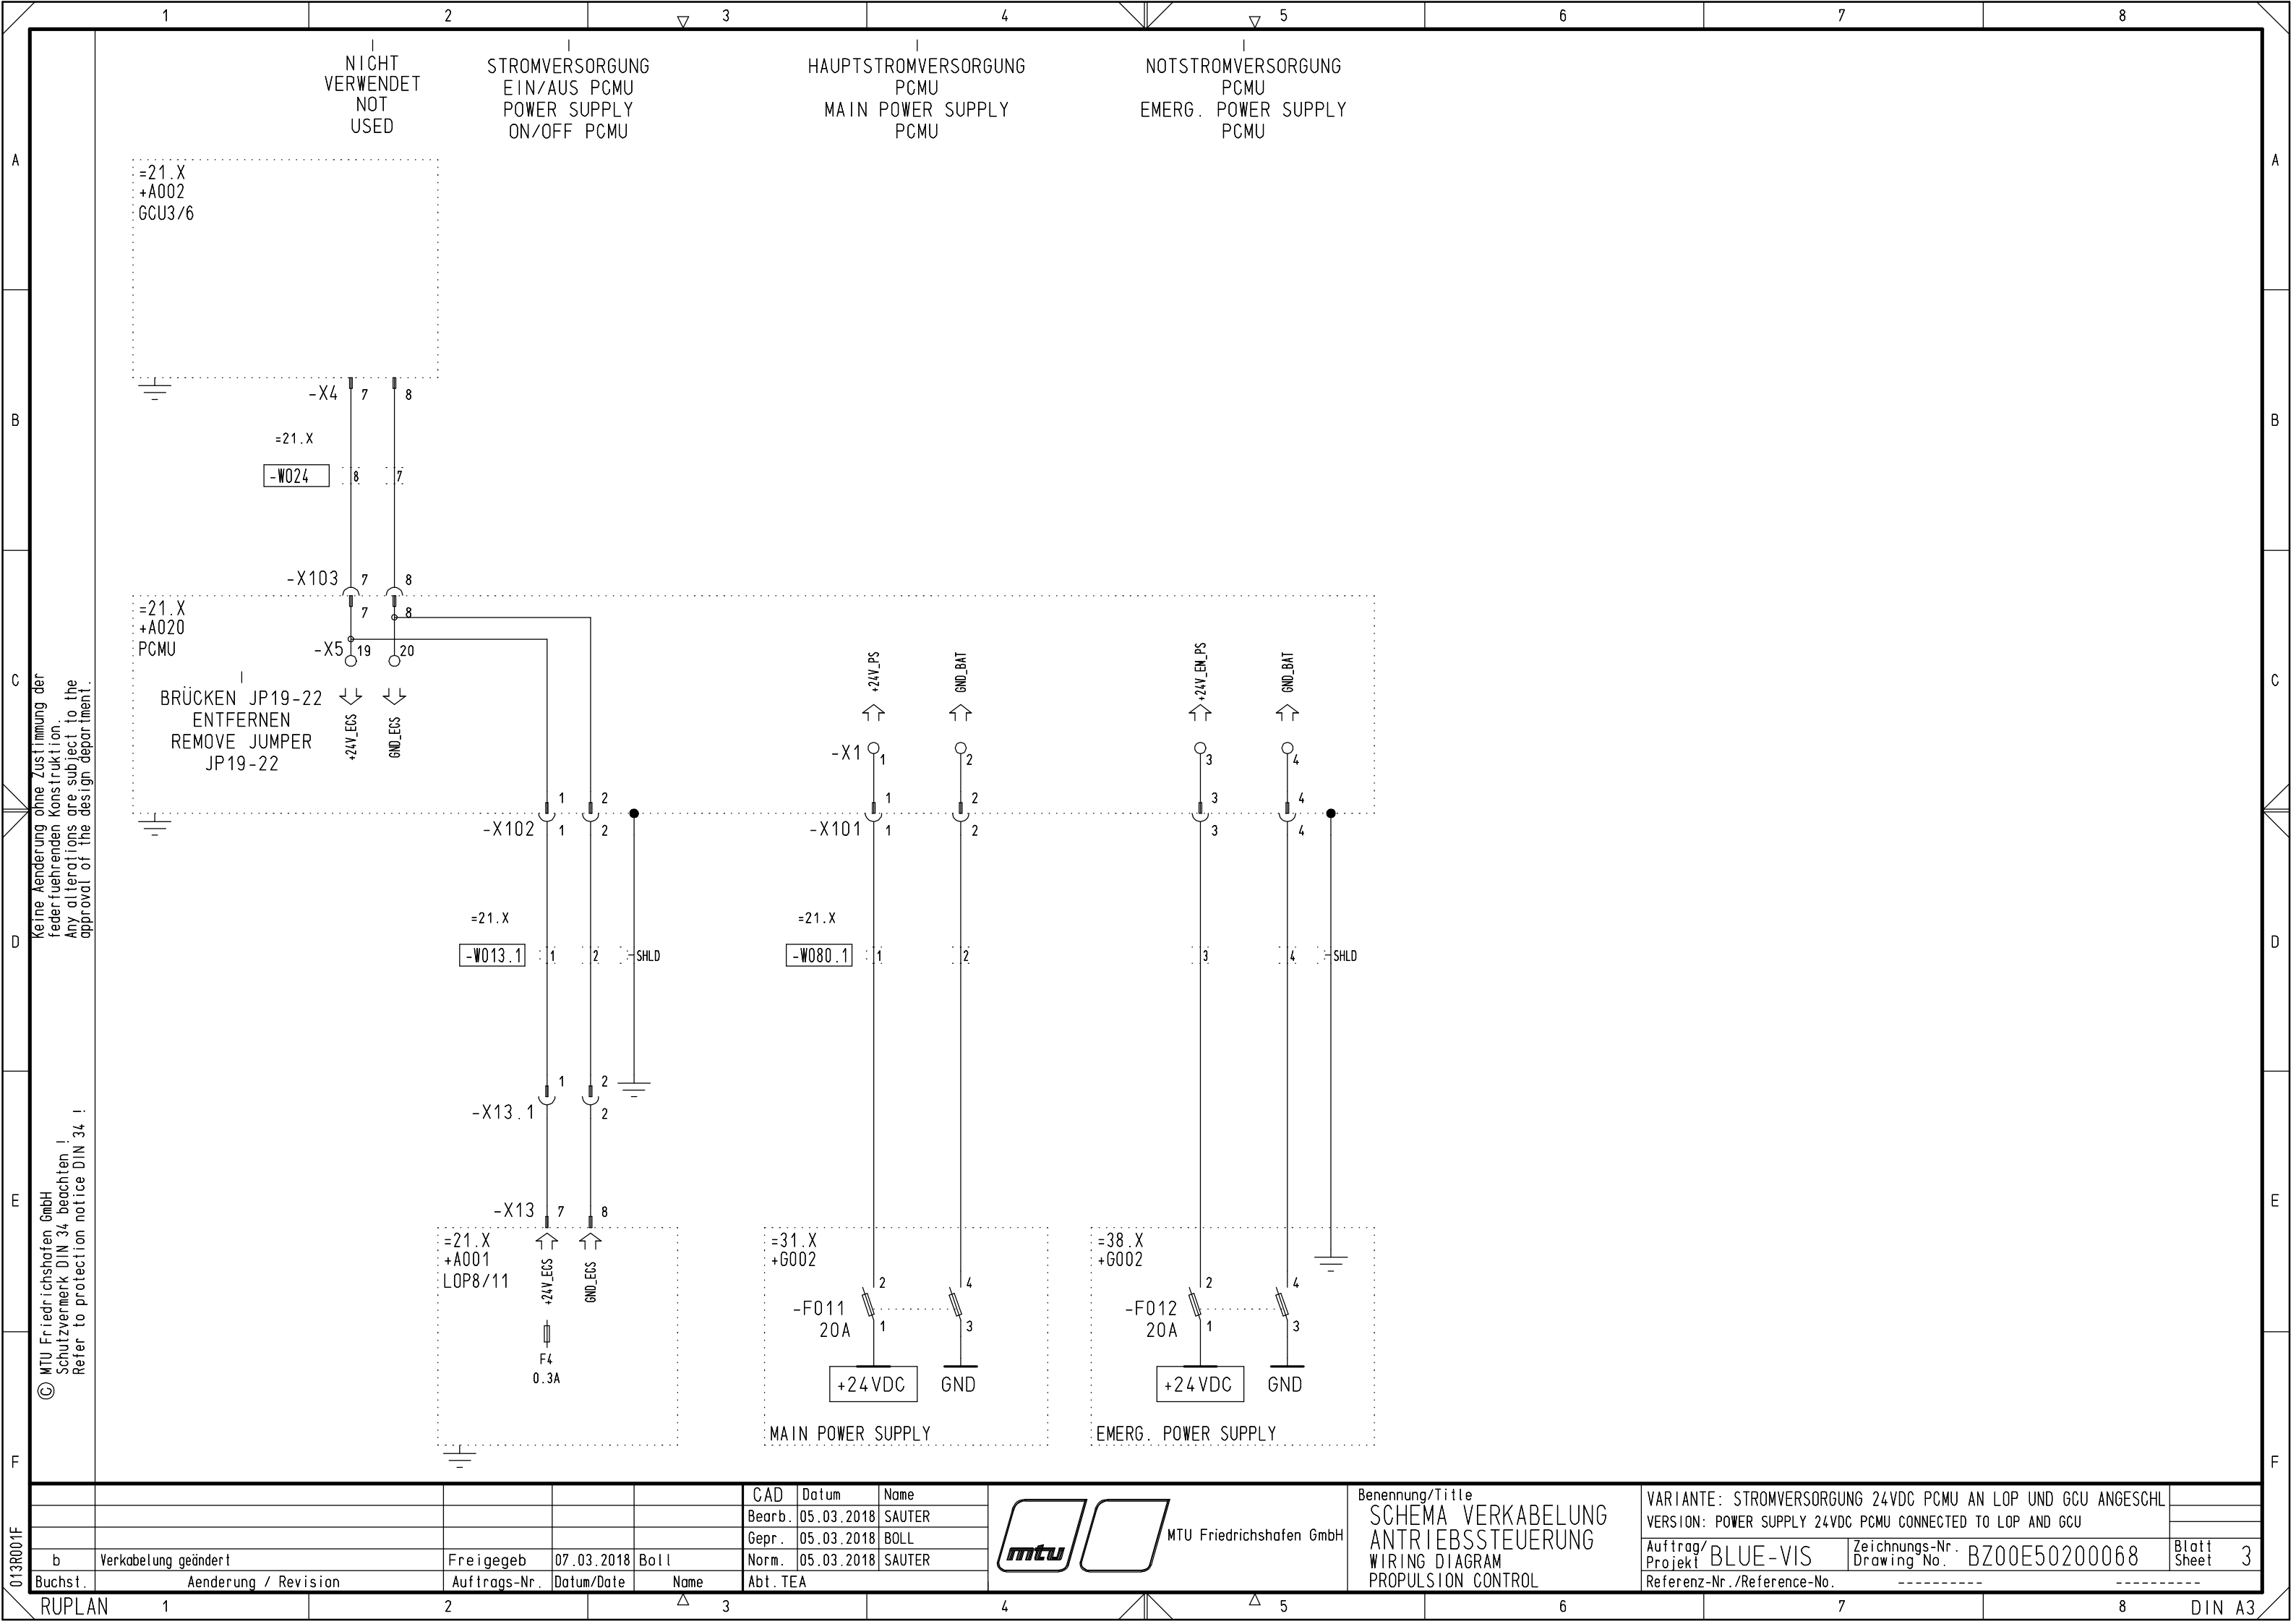


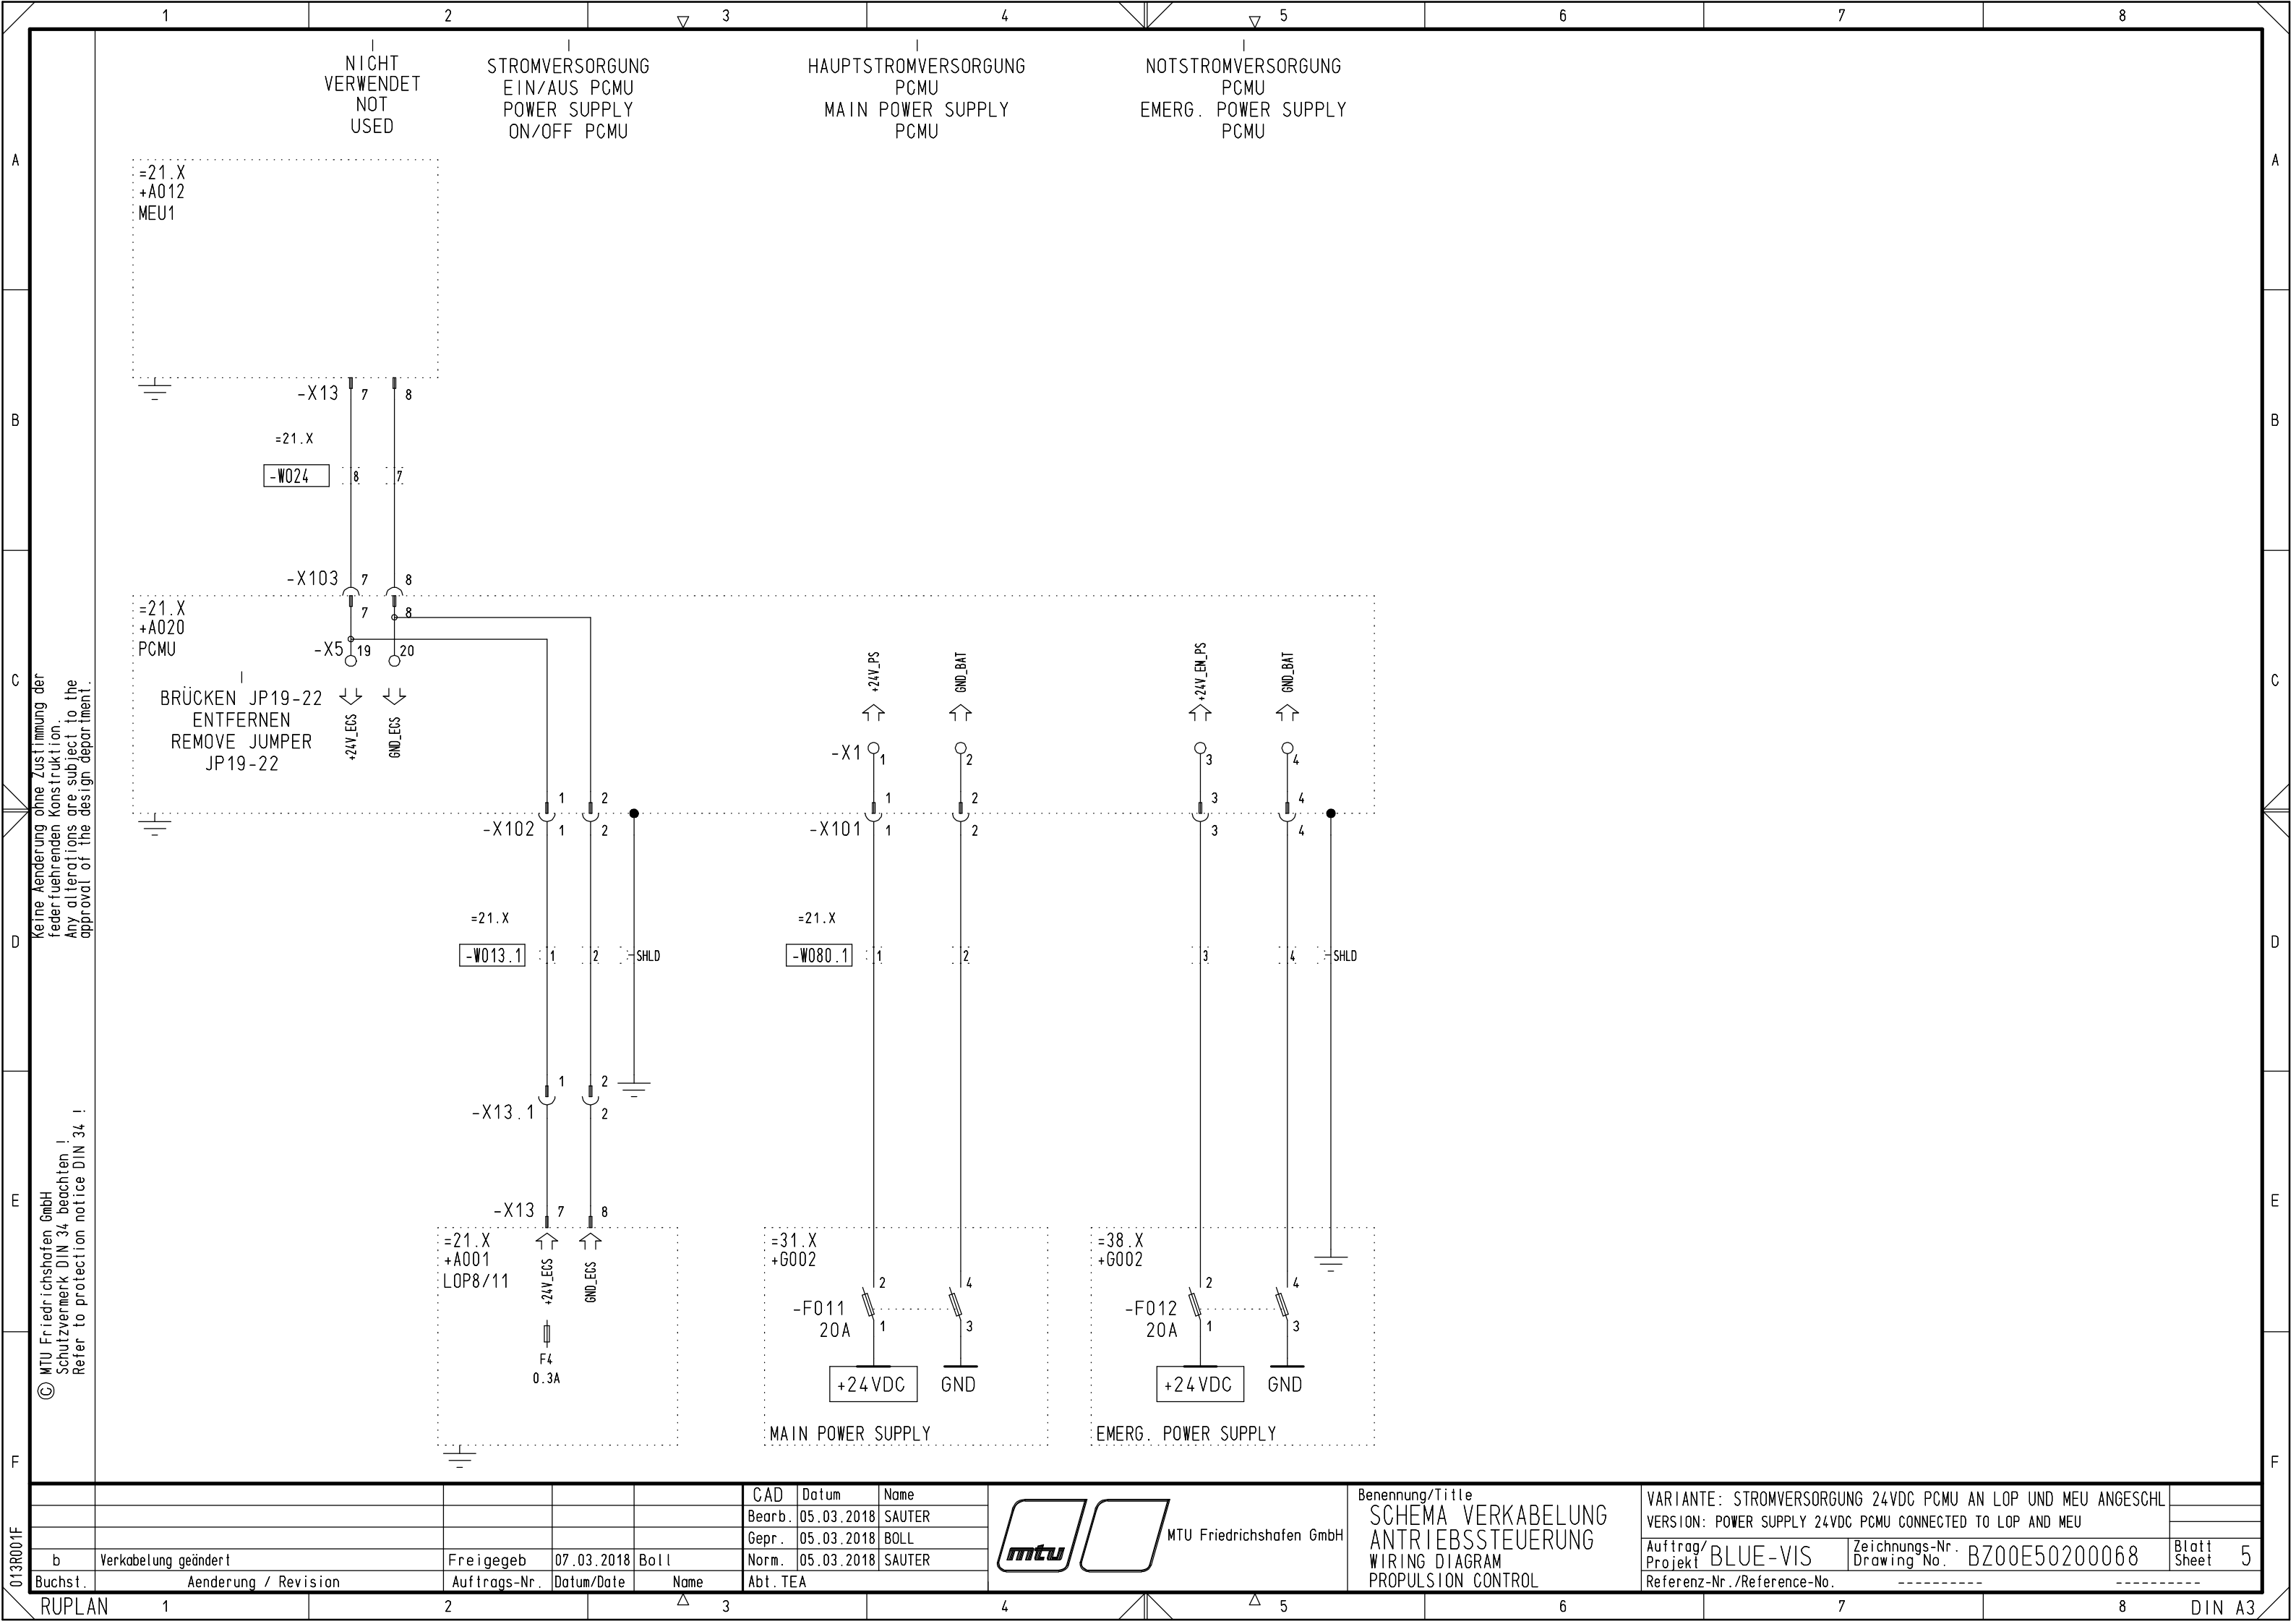

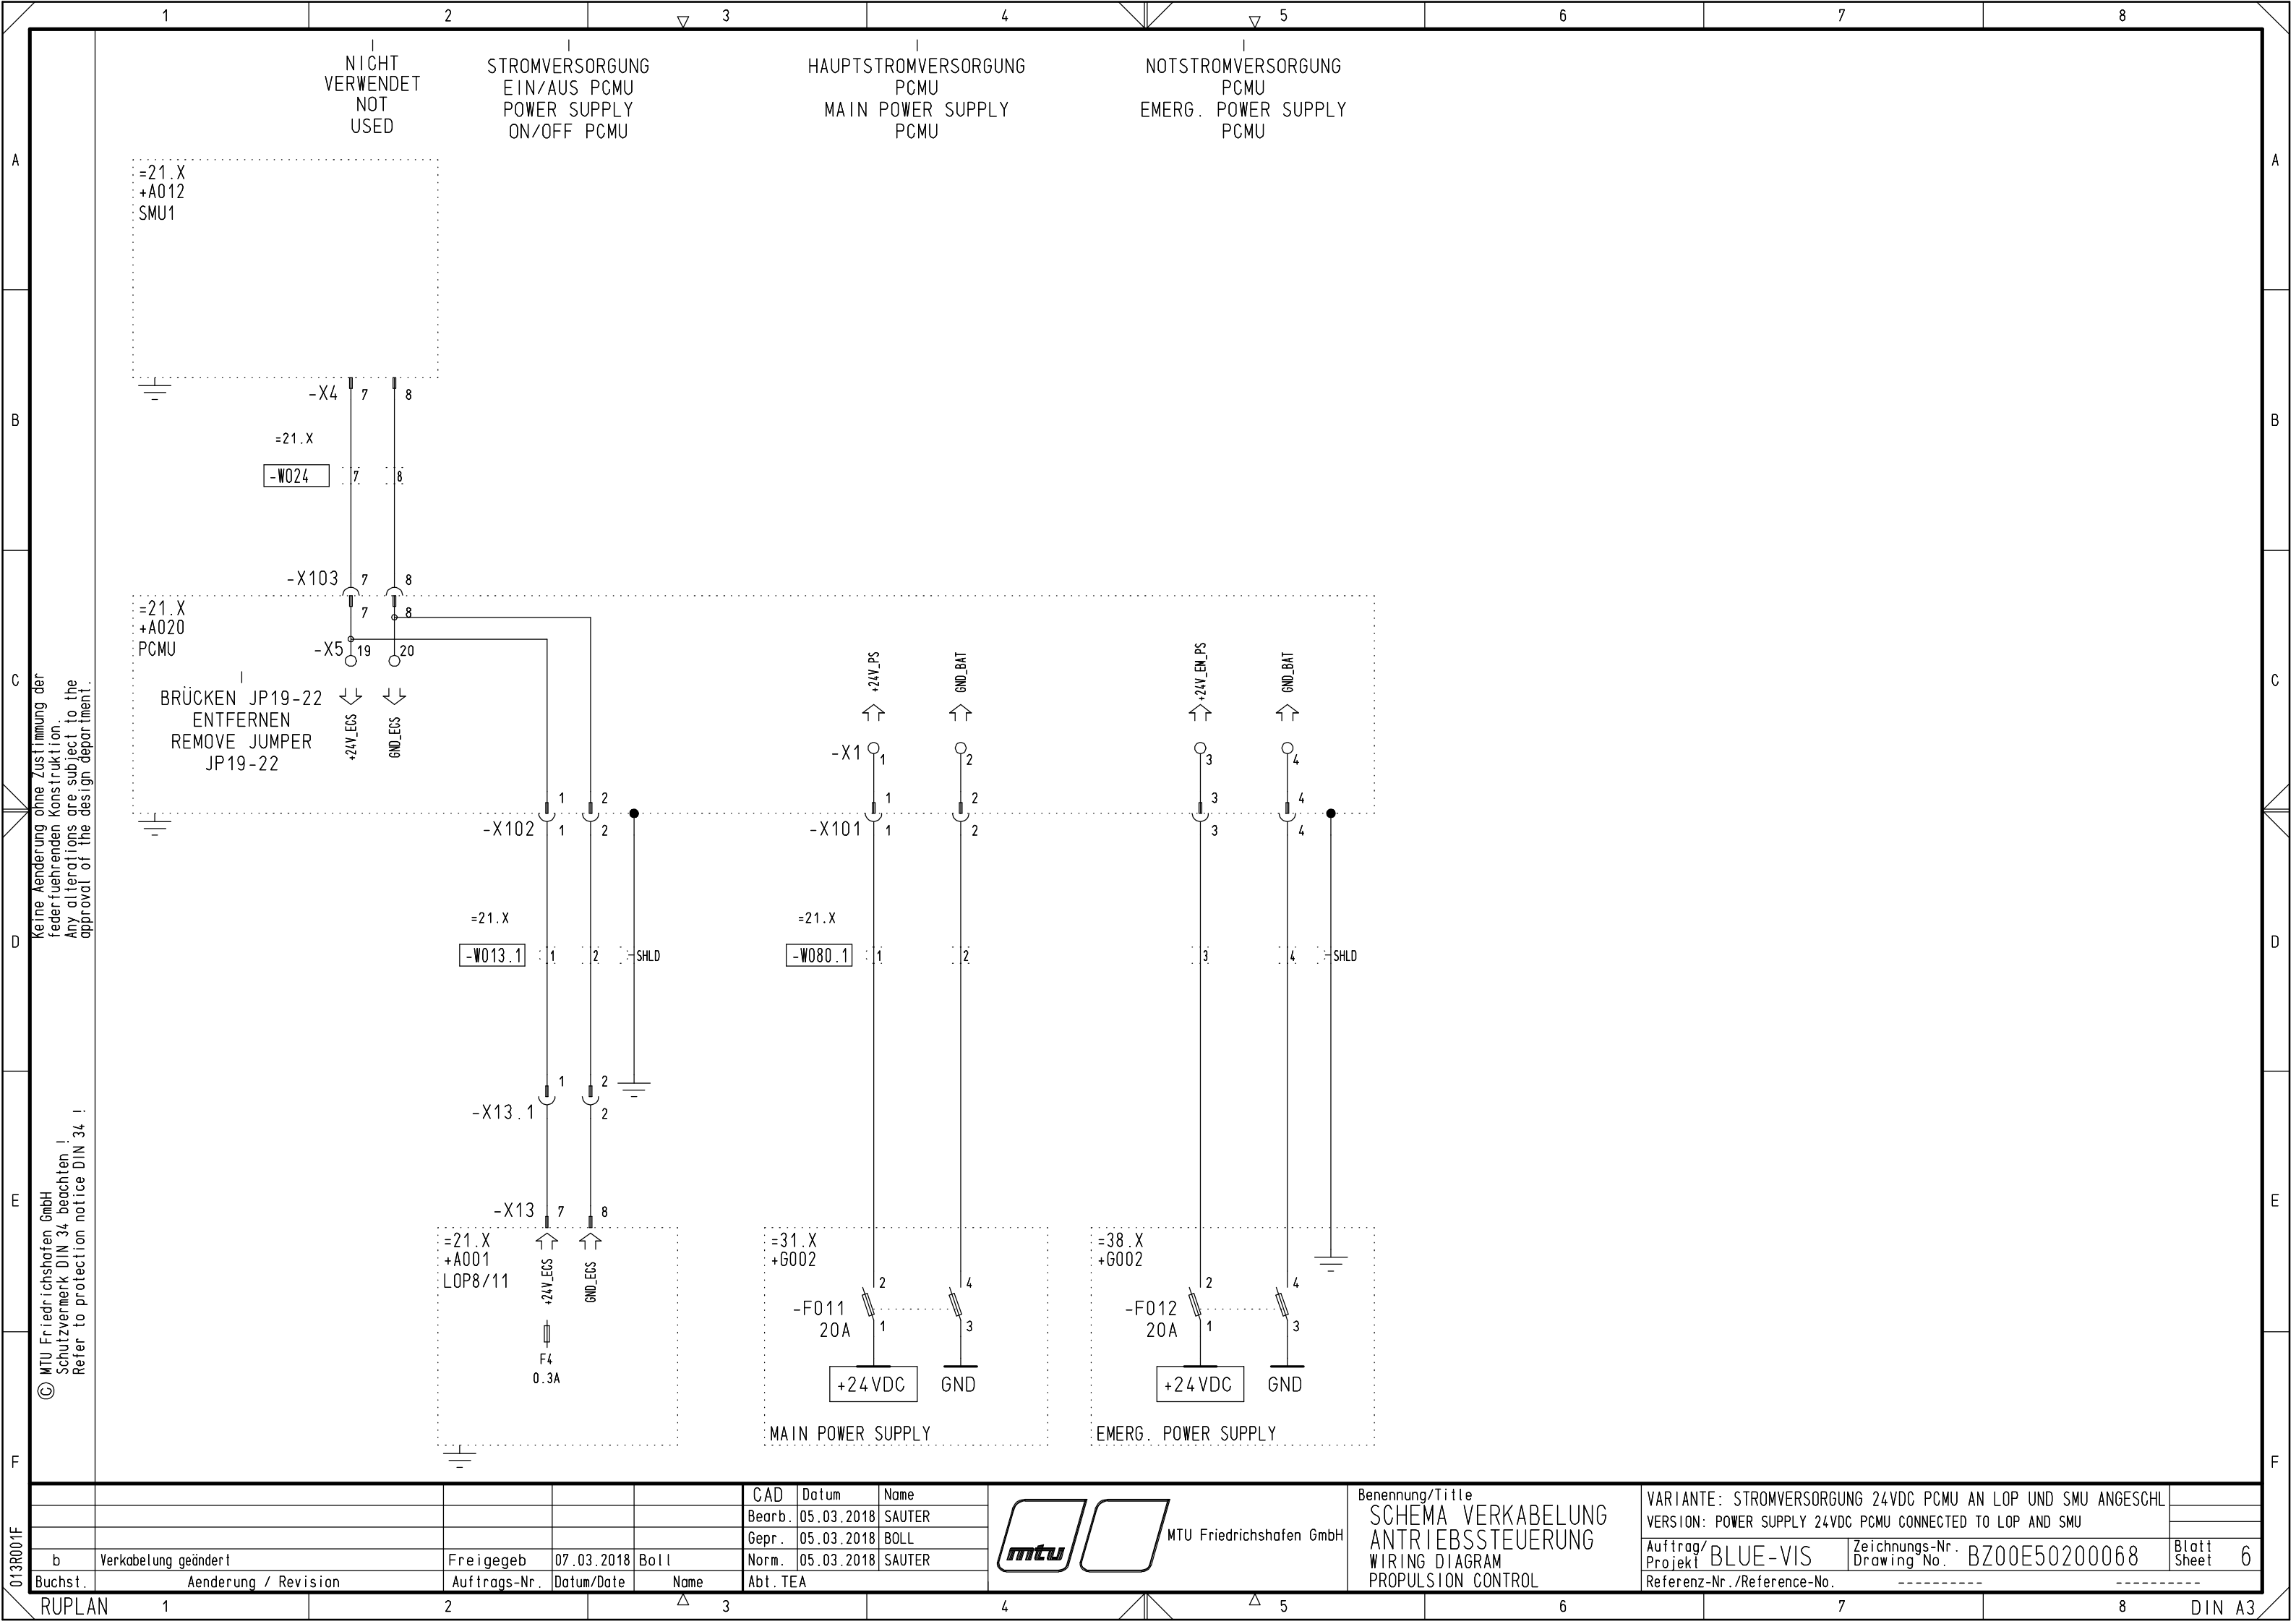

Keine Änderung ohne Zustimmung der
federführenden Konstruktion.
Any alterations are subject to the
approval of the design department.

© MTU Friedrichshafen GmbH
Schutzvermerk DIN 34 beachten !
Refer to protection notice DIN 34 !

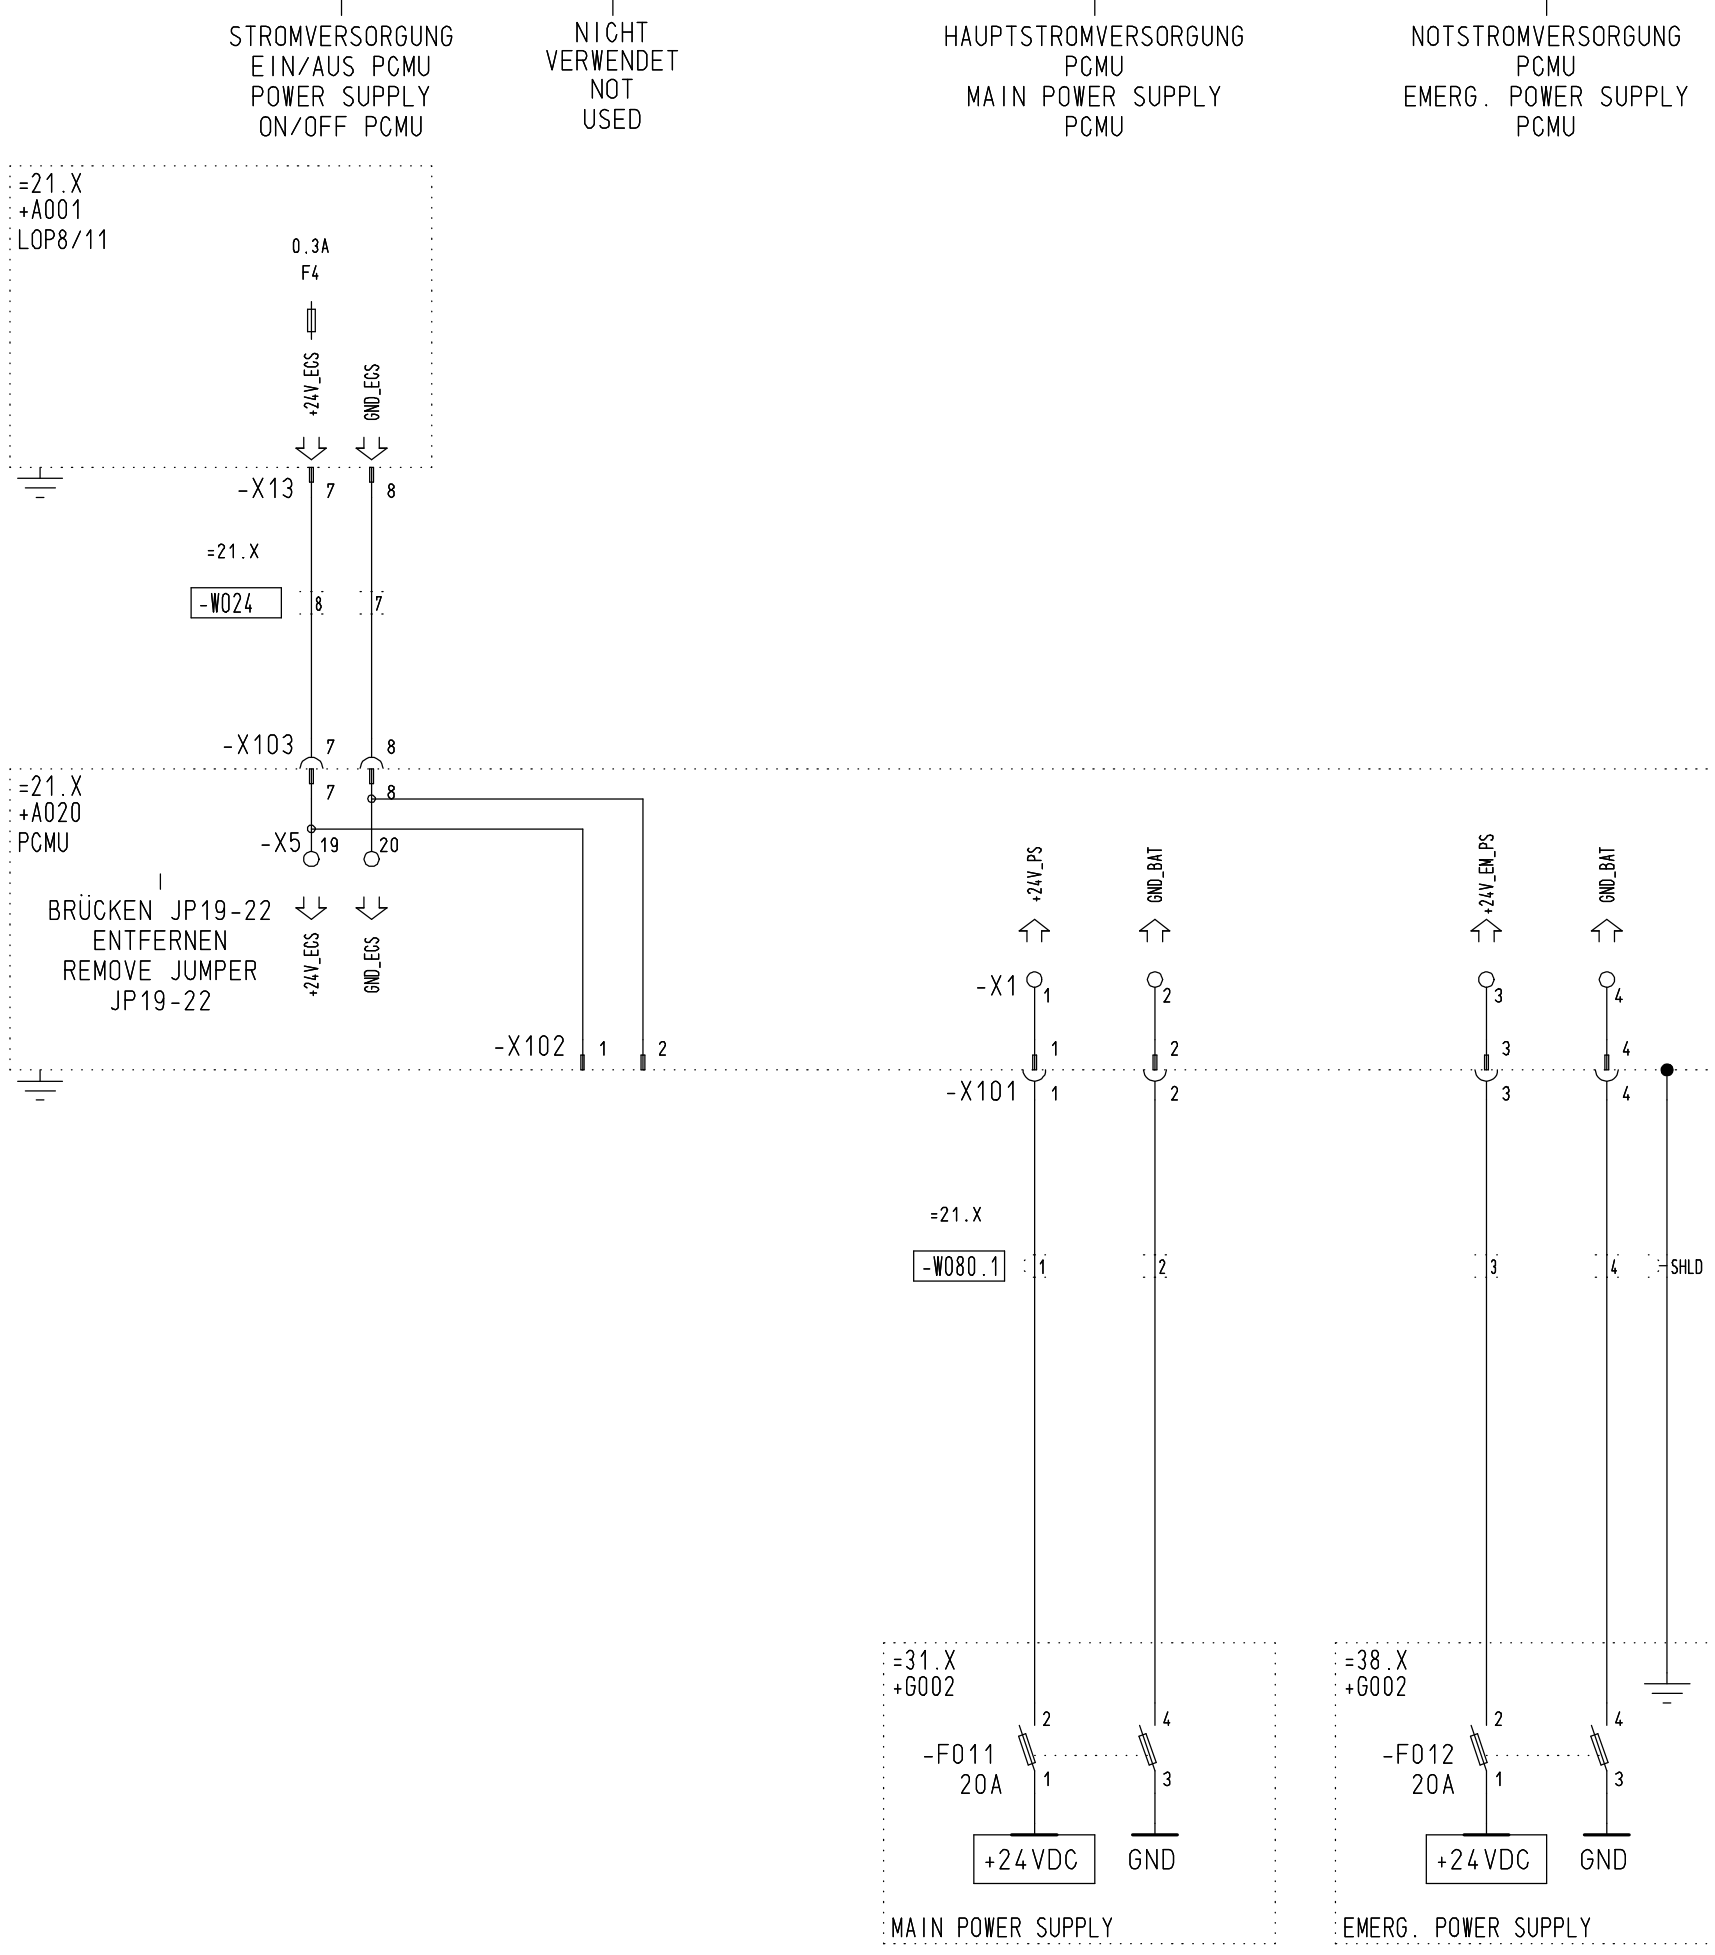

					CAD	Datum	Name	 MTU Friedrichshafen GmbH	Benennung/Title SCHEMA VERKABELUNG ANTRIEBSSTEUERUNG WIRING DIAGRAM PROPULSION CONTROL	VARIANTE: STROMVERSORGUNG 24VDC PCMU AN LOP ANGESCHLOSSEN		
					Bearb.	05.03.2018	SAUTER			VERSION: POWER SUPPLY 24VDC PCMU CONNECTED TO LOP		
					Gepr.	05.03.2018	BOLL					
b	Verkabelung geändert	Freigegeb	07.03.2018	Boll	Norm.	05.03.2018	SAUTER					Auftrag/ Projekt
Buchst.	Aenderung / Revision	Auftrags-Nr.	Datum/Date	Name	Abt. TEA					BLUE-VIS	BZ00E50200068	7
Referenz-Nr./Reference-No. -----												

Keine Änderung ohne Zustimmung der
federführenden Konstruktion.
Any alterations are subject to the
approval of the design department.

© MTU Friedrichshafen GmbH
Schutzvermerk DIN 34 beachten !
Refer to protection notice DIN 34 !


					CAD	Datum	Name
					Bearb.	05.03.2018	SAUTER
					Gepr.	05.03.2018	BOLL
b	Verkabelung geändert	Freigegeb	07.03.2018	Boll	Norm.	05.03.2018	SAUTER
Buchst.	Änderung / Revision	Auftrags-Nr.	Datum/Date	Name	Abt. TEA		



MTU Friedrichshafen GmbH

Benennung/Title
SCHEMA VERKABELUNG
ANTRIEBSSTEUERUNG
WIRING DIAGRAM
PROPULSION CONTROL

VARIANTE: FELDBUS PCMU AN GCU ANGESCHLOSSEN VERSION: FIELD BUS PCMU CONNECTED TO GCU			
Auftrag/ Projekt	BLUE-VIS	Zeichnungs-Nr. Drawing No.	BZ00E50200068
Referenz-Nr./Reference-No.		-----	
			Blatt Sheet 8

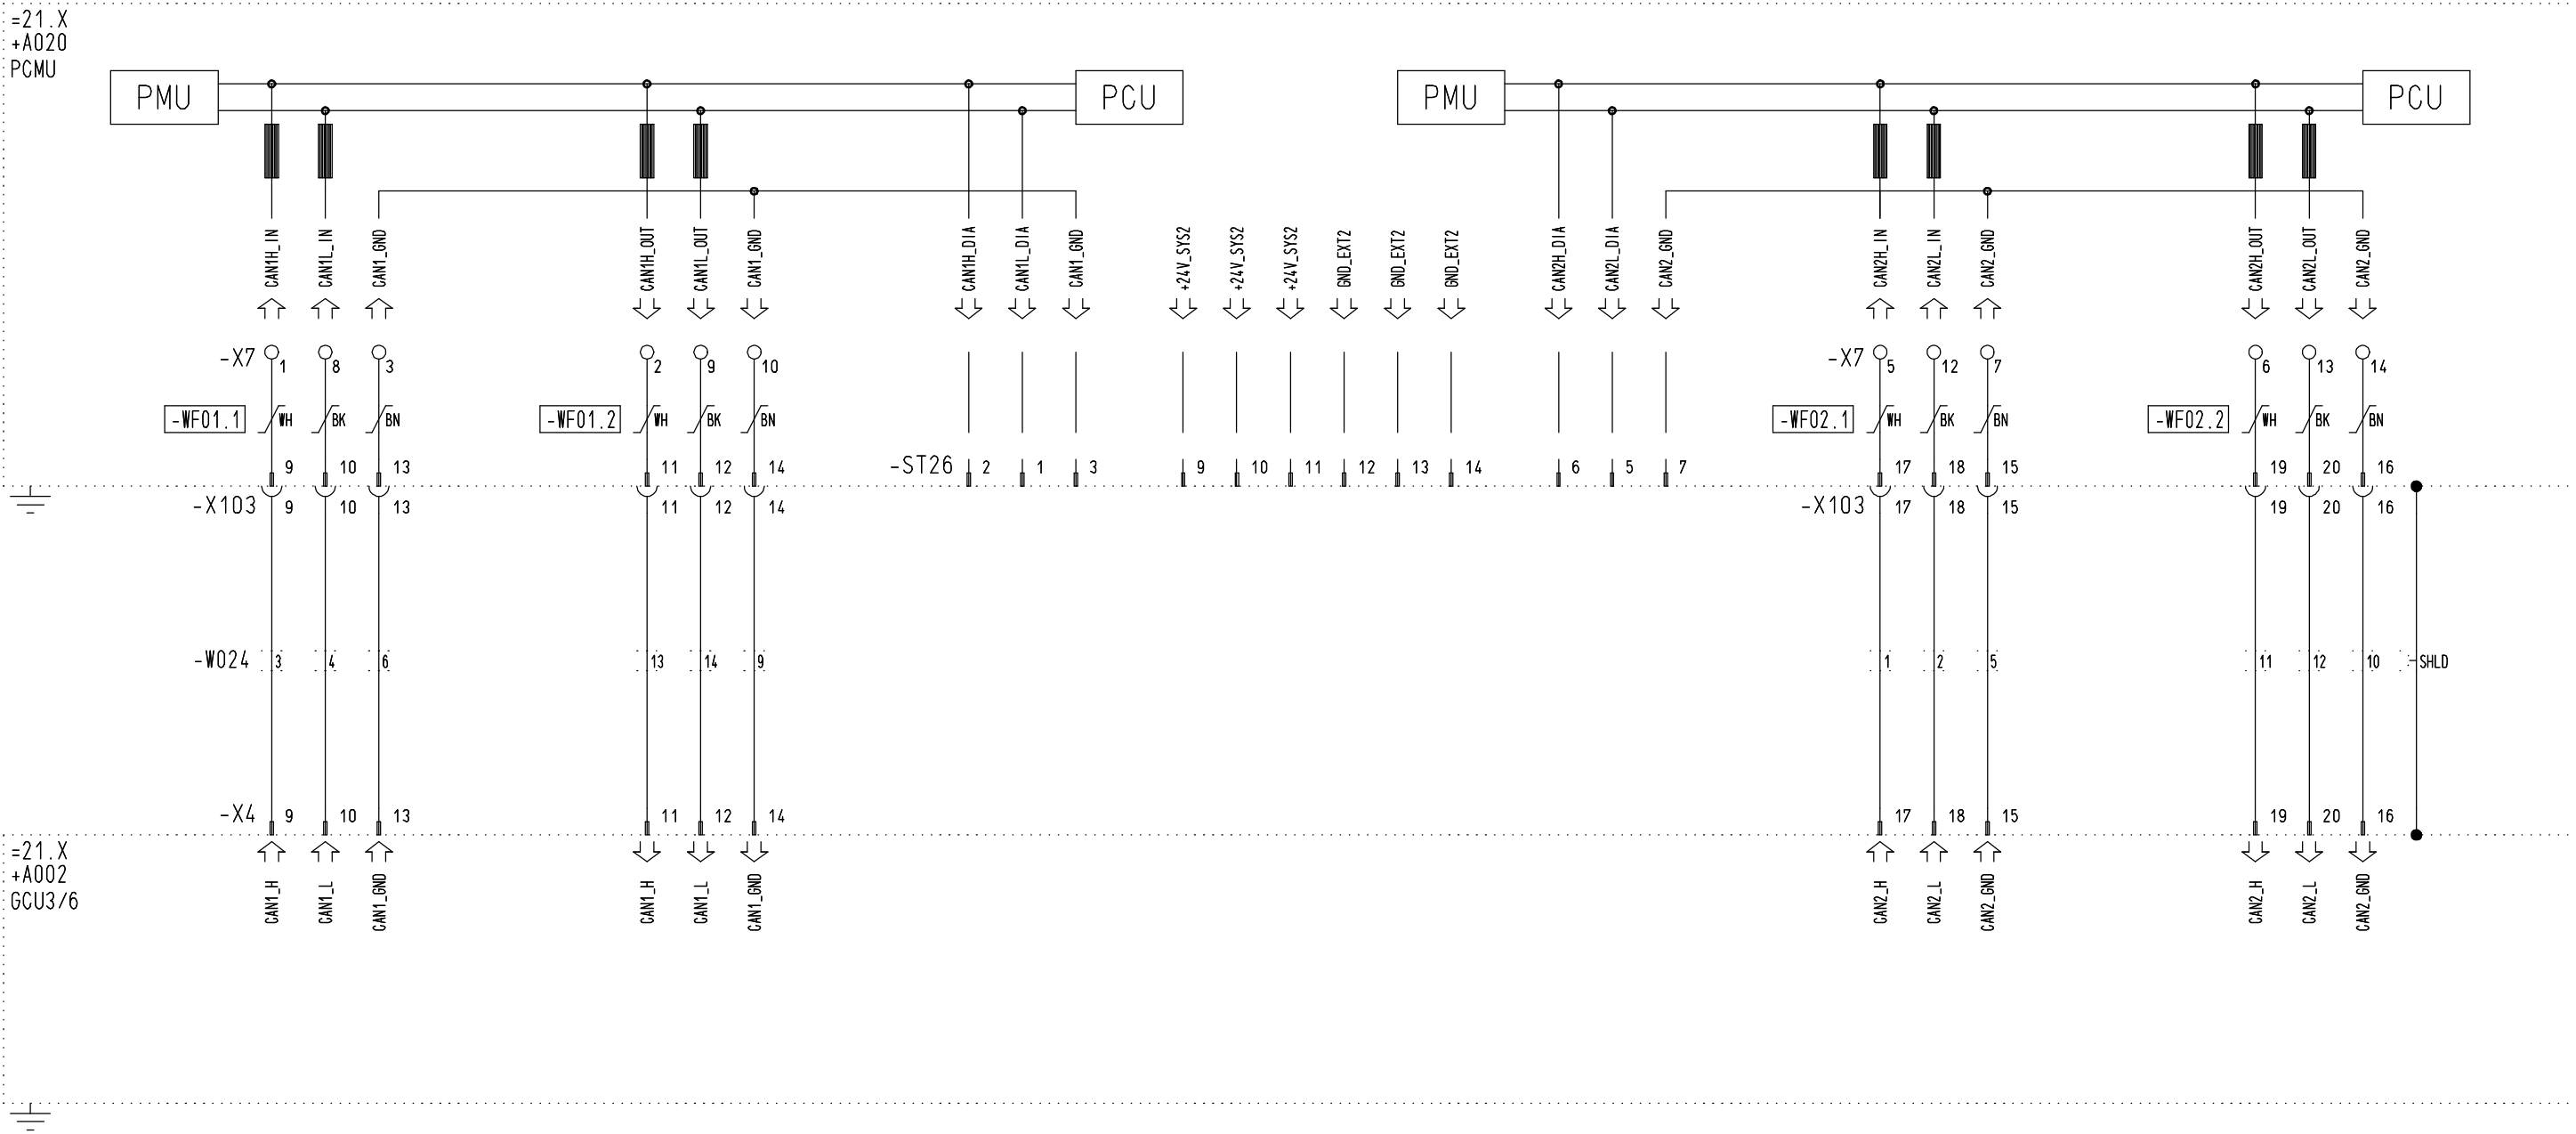

Keine Änderung ohne Zustimmung der
federführenden Konstruktion.
Any alterations are subject to the
approval of the design department.

© MTU Friedrichshafen GmbH
Schutzvermerk DIN 34 beachten !
Refer to protection notice DIN 34 !


					CAD	Datum	Name
					Bearb.	05.03.2018	SAUTER
					Gepr.	05.03.2018	BOLL
b	Verkabelung geändert	Freigegeb	07.03.2018	Boll	Norm.	05.03.2018	SAUTER
Buchst.	Änderung / Revision	Auftrags-Nr.	Datum/Date	Name	Abt. TEA		



MTU Friedrichshafen GmbH

Benennung/Title
SCHEMA VERKABELUNG
ANTRIEBSSTEUERUNG
WIRING DIAGRAM
PROPULSION CONTROL

VARIANTE: FELDBUS PCMU AN FCU ANGESCHLOSSEN VERSION: FIELD BUS PCMU CONNECTED TO FCU			
Auftrag/ Projekt	BLUE-VIS	Zeichnungs-Nr. Drawing No.	BZ00E50200068
Referenz-Nr./Reference-No.		-----	
			Blatt Sheet 9

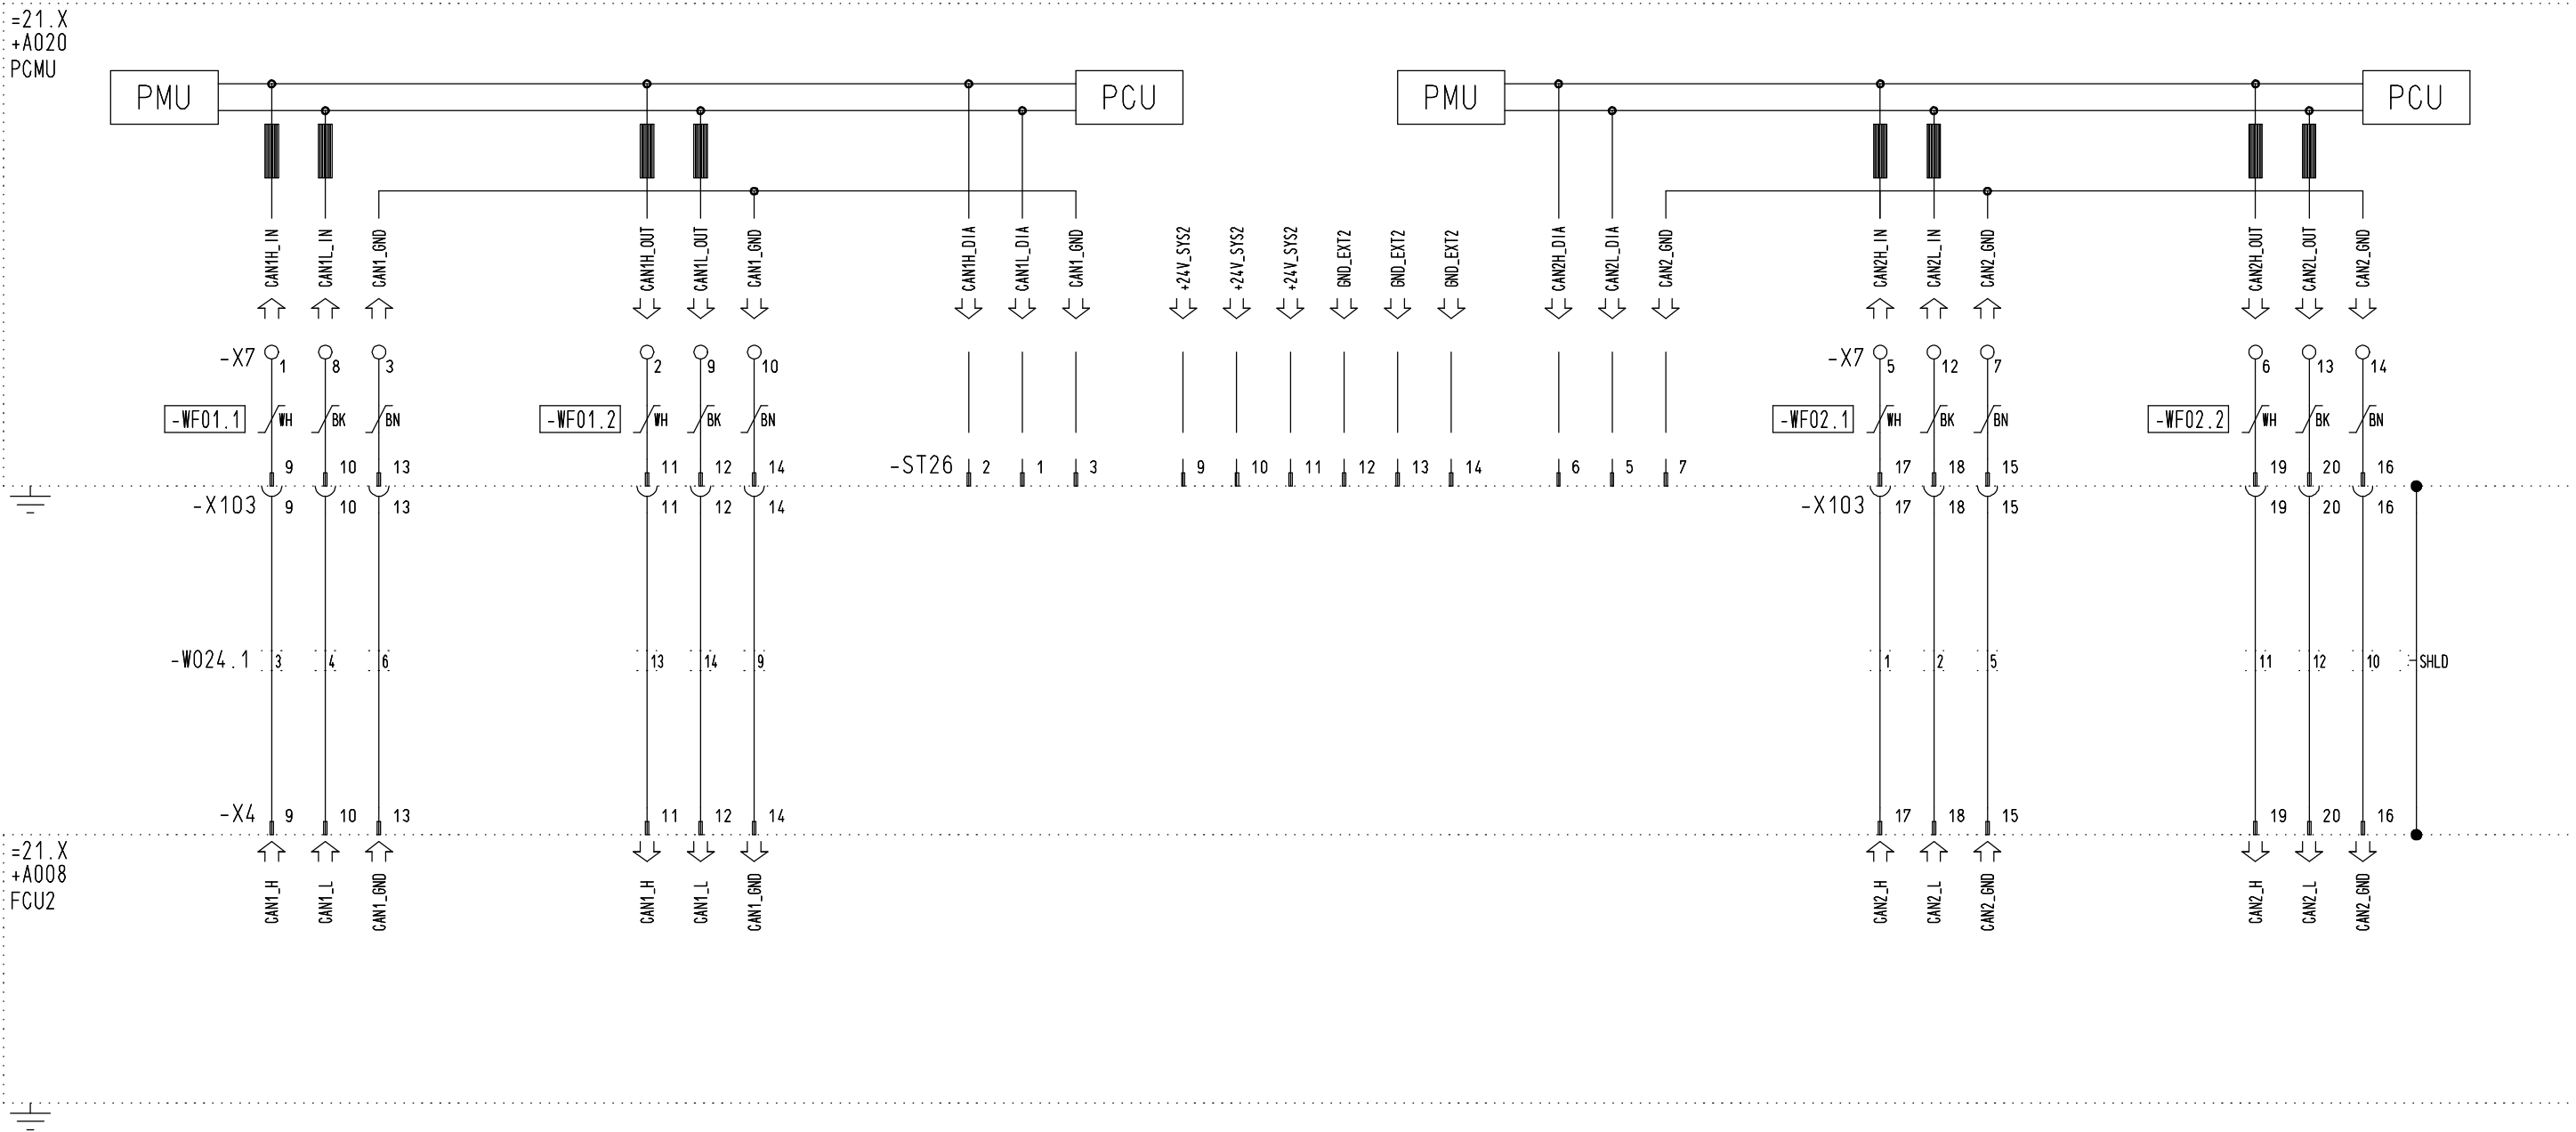

Keine Änderung ohne Zustimmung der
federführenden Konstruktion.
Any alterations are subject to the
approval of the design department.

© MTU Friedrichshafen GmbH
Schutzvermerk DIN 34 beachten !
Refer to protection notice DIN 34 !

					CAD	Datum	Name
					Bearb.	05.03.2018	SAUTER
					Gepr.	05.03.2018	BOLL
b	Verkabelung geändert	Freigegeb	07.03.2018	Boll	Norm.	05.03.2018	SAUTER
Buchst.	Änderung / Revision	Auftrags-Nr.	Datum/Date	Name	Abt. TEA		



MTU Friedrichshafen GmbH

Benennung/Title
SCHEMA VERKABELUNG
ANTRIEBSSTEUERUNG
WIRING DIAGRAM
PROPULSION CONTROL

VARIANTE: FELDBUS PCMU AN MEU ANGESCHLOSSEN
VERSION: FIELD BUS PCMU CONNECTED TO MEU

Auftrag/Projekt
BLUE-VIS
Zeichnungs-Nr.
Drawing No. BZ00E50200068

Referenz-Nr./Reference-No. -----

Blatt
Sheet 10

Keine Änderung ohne Zustimmung der
federführenden Konstruktion.
Any alterations are subject to the
approval of the design department.


© MTU Friedrichshafen GmbH
Schutzvermerk DIN 34 beachten !
Refer to protection notice DIN 34 !

					CAD	Datum	Name
					Bearb.	05.03.2018	SAUTER
					Gepr.	05.03.2018	BOLL
b	Verkabelung geändert	Freigegeb	07.03.2018	Boll	Norm.	05.03.2018	SAUTER
Buchst.	Änderung / Revision	Auftrags-Nr.	Datum/Date	Name	Abt. TEA		



Benennung/Title
SCHEMA VERKABELUNG
ANTRIEBSSTEUERUNG
WIRING DIAGRAM
PROPULSION CONTROL

VARIANTE: FELDBUS PCMU AN SMU ANGESCHLOSSEN VERSION: FIELD BUS PCMU CONNECTED TO SMU			
Auftrag/ Projekt	BLUE-VIS	Zeichnungs-Nr. Drawing No.	BZ00E50200068
Referenz-Nr./Reference-No.		-----	
Blatt Sheet		11	

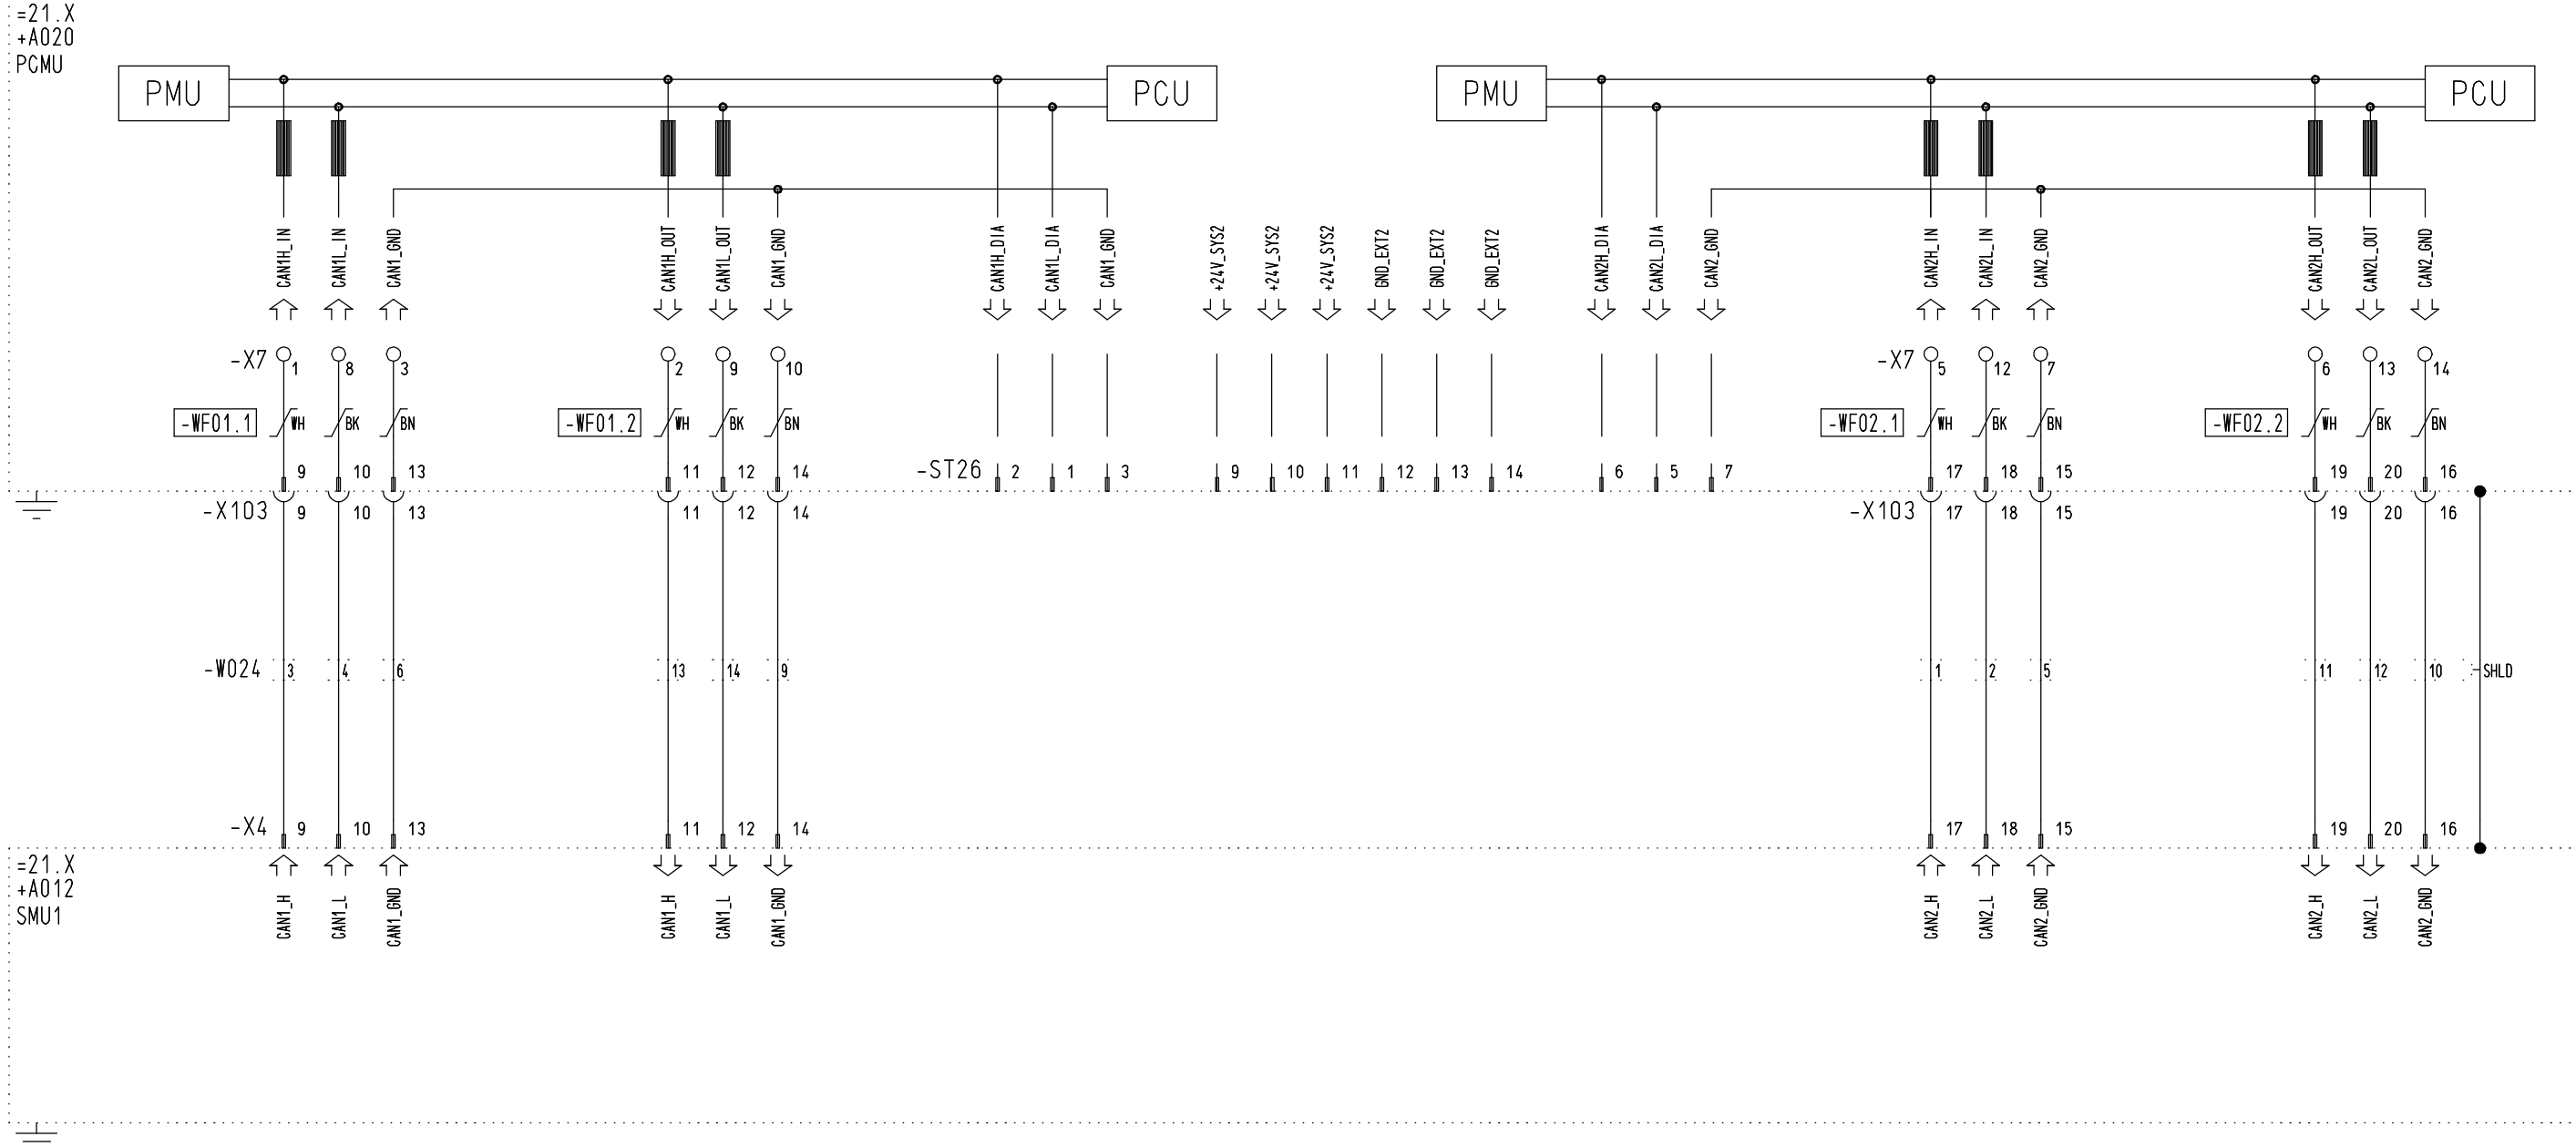

Keine Änderung ohne Zustimmung der
federführenden Konstruktion.
Any alterations are subject to the
approval of the design department.

© MTU Friedrichshafen GmbH
Schutzvermerk DIN 34 beachten !
Refer to protection notice DIN 34 !

					CAD	Datum	Name
					Bearb.	05.03.2018	SAUTER
					Gepr.	05.03.2018	BOLL
b	Verkabelung geändert	Freigegeb	07.03.2018	Boll	Norm.	05.03.2018	SAUTER
Buchst.	Änderung / Revision	Auftrags-Nr.	Datum/Date	Name	Abt. TEA		



MTU Friedrichshafen GmbH

Benennung/Title
SCHEMA VERKABELUNG
ANTRIEBSSTEUERUNG
WIRING DIAGRAM
PROPULSION CONTROL

VARIANTE: FELDBUS PCMU AN LOP ANGESCHLOSSEN
VERSION: FIELD BUS PCMU CONNECTED TO LOP

Auftrag/
Projekt BLUE-VIS Zeichnungs-Nr.
Drawing No. BZ00E50200068

Referenz-Nr./Reference-No. -----

Blatt
Sheet 12

Keine Änderung ohne Zustimmung der
federführenden Konstruktion.
Any alterations are subject to the
approval of the design department.

© MTU Friedrichshafen GmbH
Schutzvermerk DIN 34 beachten !
Refer to protection notice DIN 34 !


AKTUELL NICHT VERWENDET - GÜLTIGKEIT LIEFERUMFANGABHÄNGIG
CURRENTLY NOT USED - VALIDITY DEPENDING ON SCOPE OF SUPPLY

--	--	

Keine Änderung ohne Zustimmung der
federführenden Konstruktion.
Any alterations are subject to the
approval of the design department.

© MTU Friedrichshafen GmbH
Schutzvermerk DIN 34 beachten !
Refer to protection notice DIN 34 !

013R001F

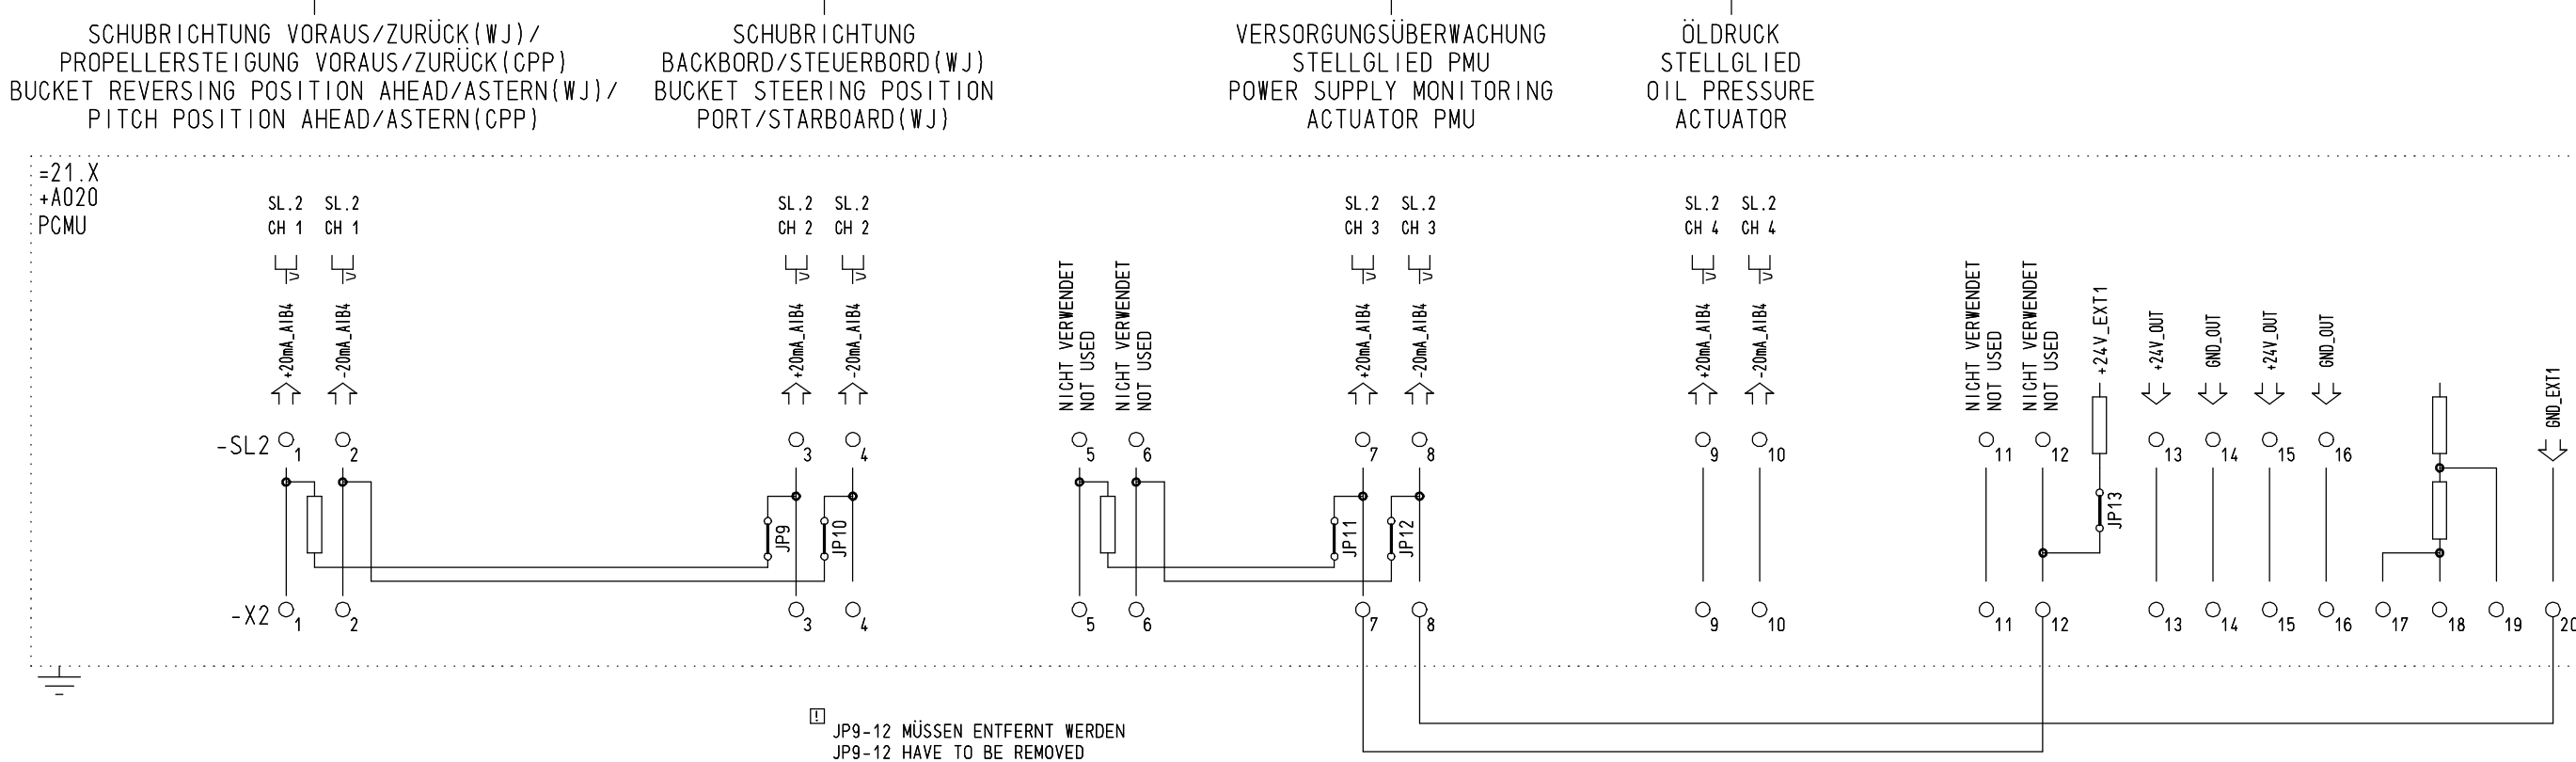

					CAD	Datum	Name
					Bearb.	05.03.2018	SAUTER
					Gepr.	05.03.2018	BOLL
					Norm.	05.03.2018	SAUTER
b	Verkabelung geändert	Freigegeb	07.03.2018	Boll	Abt. TEA		
Buchst.	Änderung / Revision	Auftrags-Nr.	Datum/Date	Name			



Benennung/Title
SCHEMA VERKABELUNG
ANTRIEBSSTEUERUNG
WIRING DIAGRAM
PROPULSION CONTROL

PMU: STECKER -X2, STECKPLATZ 2 (AIB4)	
PMU: PLUG -X2, SLOT 2 (AIB4)	
Auftrag/Projekt BLUE-VIS	Zeichnungs-Nr. Drawing No. BZ00E50200068
Referenz-Nr./Reference-No.	-----
	Blatt Sheet 14

Keine Änderung ohne Zustimmung der
federführenden Konstruktion.
Any alterations are subject to the
approval of the design department.

© MTU Friedrichshafen GmbH
Schutzvermerk DIN 34 beachten !
Refer to protection notice DIN 34 !


					CAD	Datum	Name
					Bearb.	05.03.2018	SAUTER
					Gepr.	05.03.2018	BOLL
b	Verkabelung geändert	Freigegeb	07.03.2018	Boll	Norm.	05.03.2018	SAUTER
Buchst.	Änderung / Revision	Auftrags-Nr.	Datum/Date	Name	Abt. TEA		



MTU Friedrichshafen GmbH

Benennung/Title
SCHEMA VERKABELUNG
ANTRIEBSSTEUERUNG
WIRING DIAGRAM
PROPULSION CONTROL

PMU: STECKER -X3, STECKPLATZ 3 (INB2)	
PMU: PLUG -X3, SLOT 3 (INB2)	
Auftrag/ Projekt	Zeichnungs-Nr. Drawing No.
BLUE-VIS	BZ00E50200068
Referenz-Nr./Reference-No.	-----
	Blatt Sheet 15

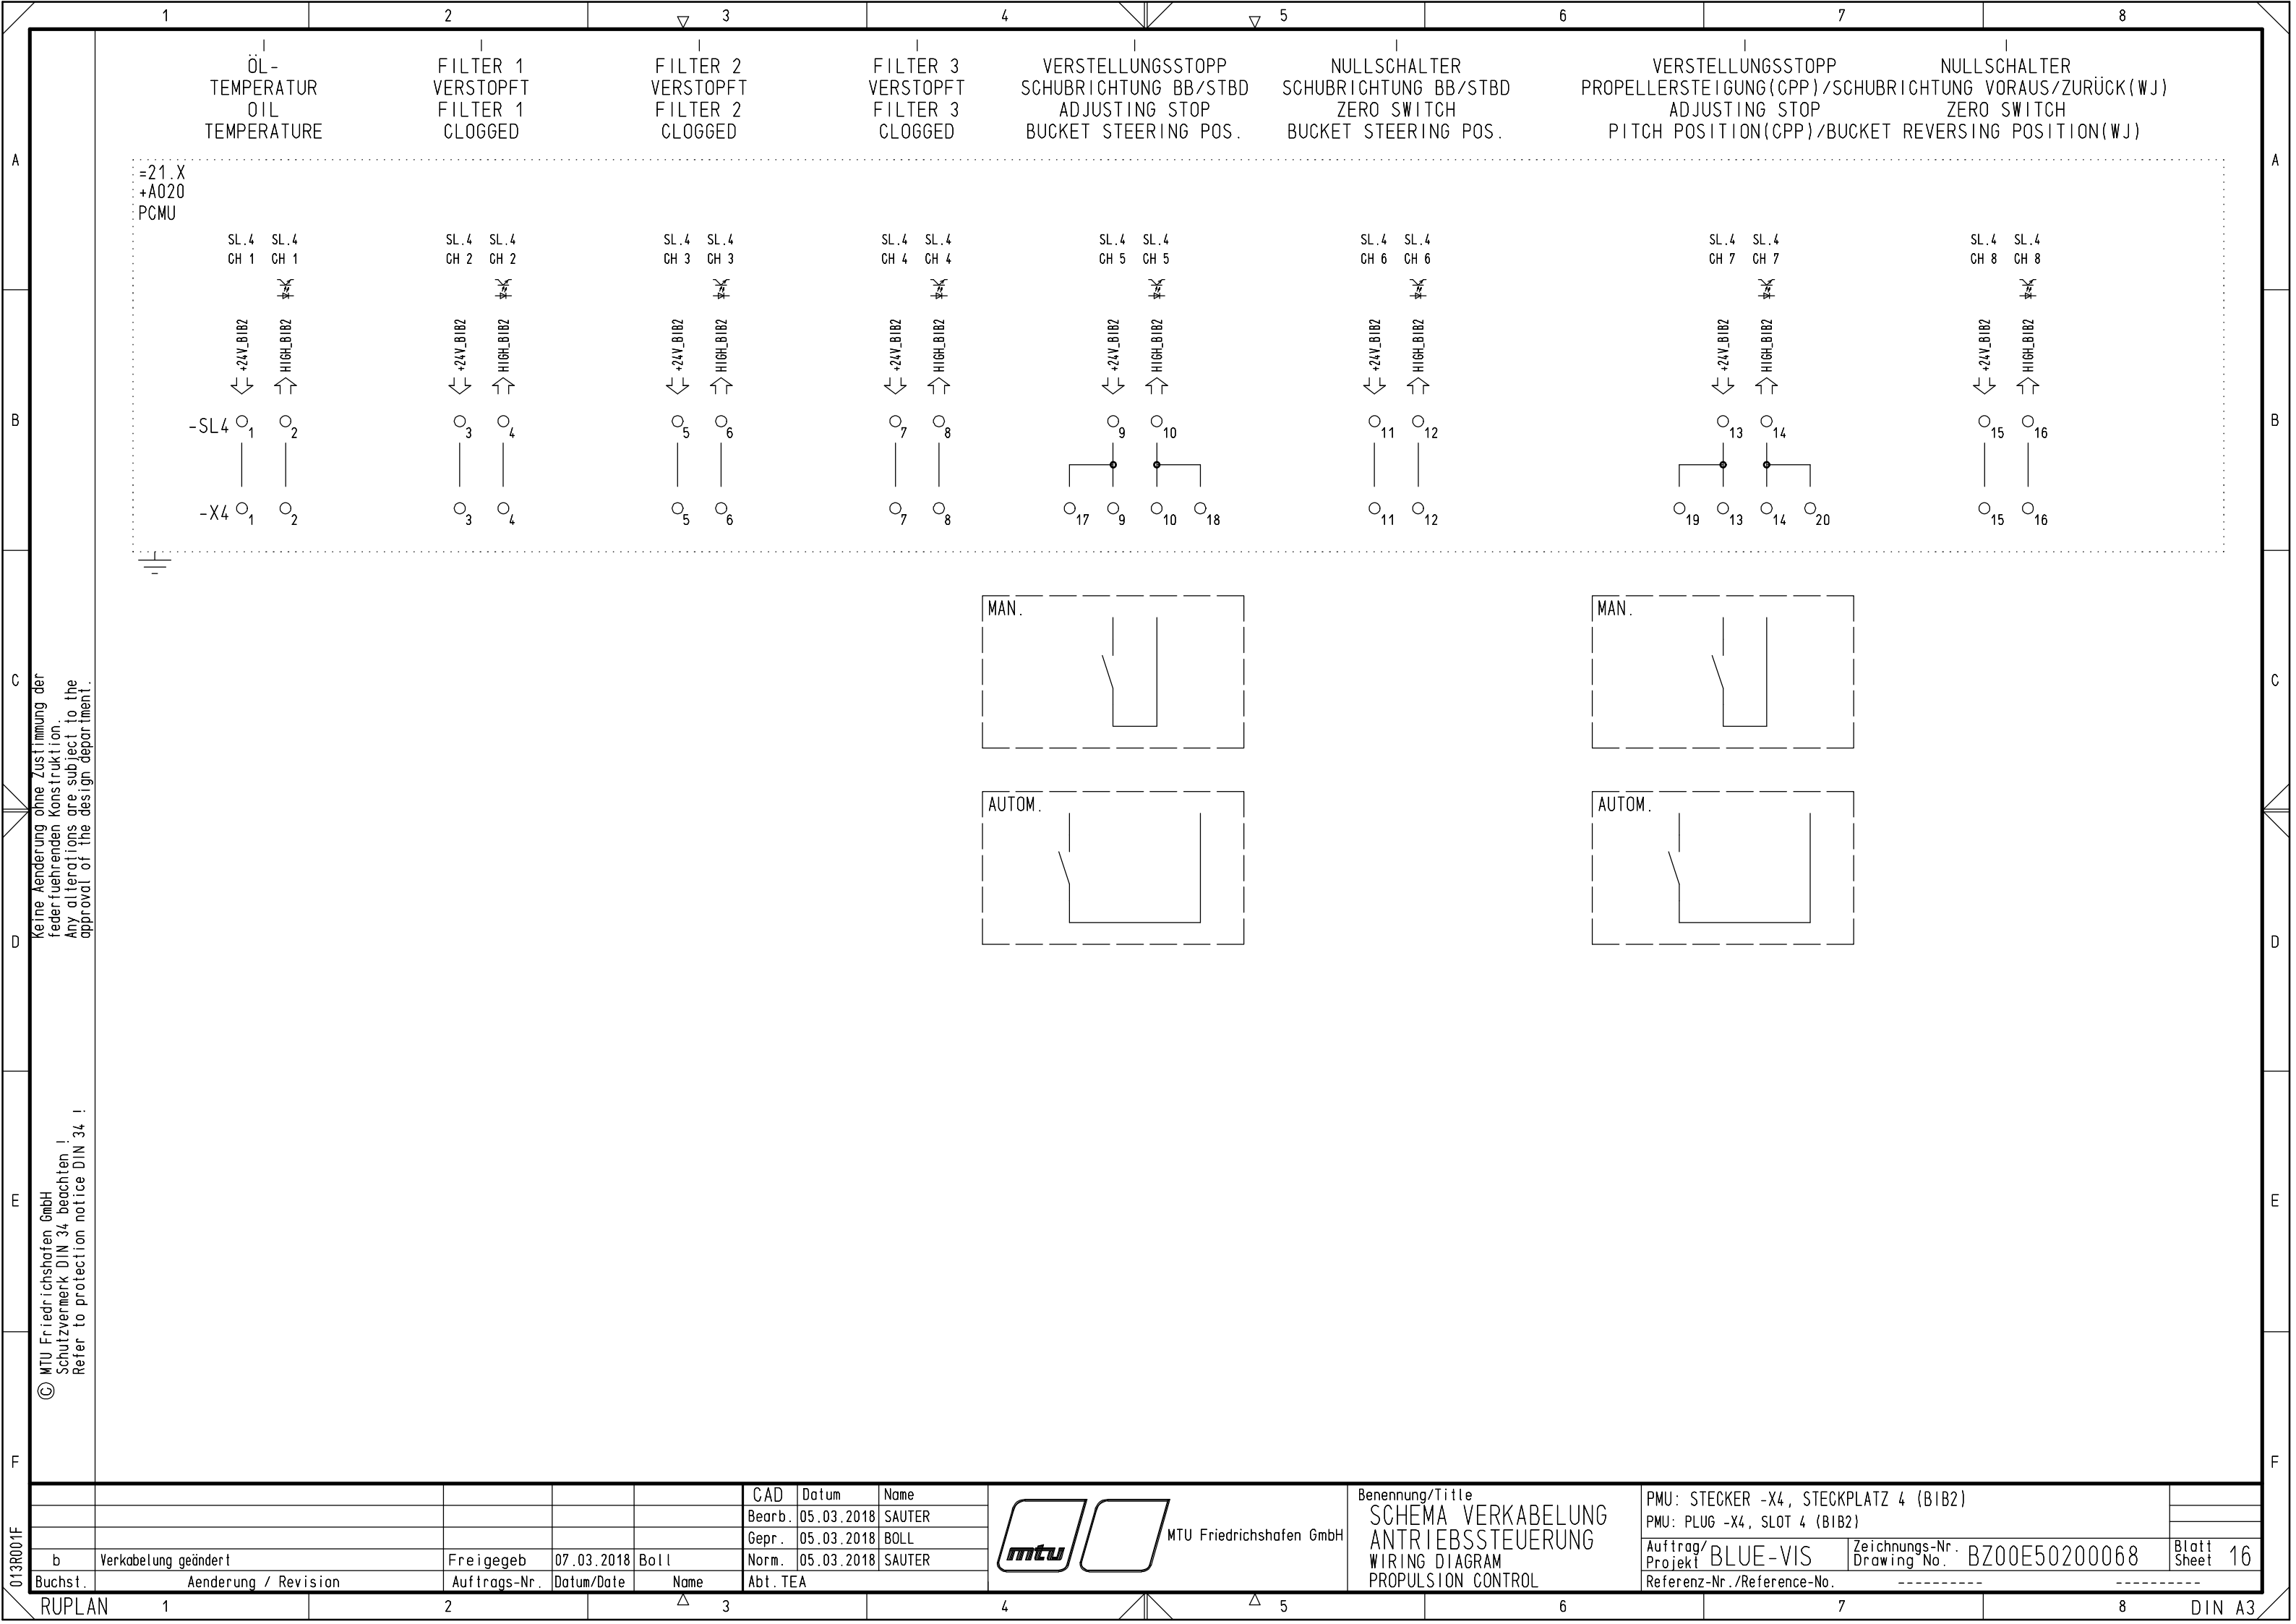

Keine Änderung ohne Zustimmung der
federführenden Konstruktion.
Any alterations are subject to the
approval of the design department.

© MTU Friedrichshafen GmbH
Schutzvermerk DIN 34 beachten !
Refer to protection notice DIN 34 !

					CAD	Datum	Name	 MTU Friedrichshafen GmbH	Benennung/Title SCHEMA VERKABELUNG ANTRIEBSSTEUERUNG WIRING DIAGRAM PROPULSION CONTROL	PMU: STECKER -X4, STECKPLATZ 4 (BIB2)					
					Bearb.	05.03.2018	SAUTER			PMU: PLUG -X4, SLOT 4 (BIB2)					
					Gepr.	05.03.2018	BOLL								
					Norm.	05.03.2018	SAUTER								
b	Verkabelung geändert	Freigegeb	07.03.2018	Boll						Auftrag/ Projekt	BLUE-VIS	Zeichnungs-Nr. Drawing No.	BZ00E50200068	Blatt Sheet	16
Buchst.	Aenderung / Revision	Auftrags-Nr.	Datum/Date	Name	Abt. TEA					Referenz-Nr./Reference-No.	-----		-----		

Keine Änderung ohne Zustimmung der
federführenden Konstruktion.
Any alterations are subject to the
approval of the design department.

© MTU Friedrichshafen GmbH
Schutzvermerk DIN 34 beachten !
Refer to protection notice DIN 34 !

					CAD	Datum	Name
					Bearb.	05.03.2018	SAUTER
					Gepr.	05.03.2018	BOLL
b	Verkabelung geändert	Freigegeb	07.03.2018	Boll	Norm.	05.03.2018	SAUTER
Buchst.	Änderung / Revision	Auftrags-Nr.	Datum/Date	Name	Abt. TEA		




MTU Friedrichshafen GmbH

Benennung/Title
SCHEMA VERKABELUNG
ANTRIEBSSTEUERUNG
WIRING DIAGRAM
PROPULSION CONTROL

PMU: STECKER -X5, STECKPLATZ 5 (BIB2)	
PMU: PLUG -X5, SLOT 5 (BIB2)	
Auftrag/ Projekt	Zeichnungs-Nr. Drawing No.
BLUE-VIS	BZ00E50200068
Referenz-Nr./Reference-No.	-----
	Blatt Sheet
	17

ANSTEUERUNG
STELLGLIEDER, VENTILE
CONTROL OF
ACTUATORS, VALVES

=21.X
+A020
PGMU

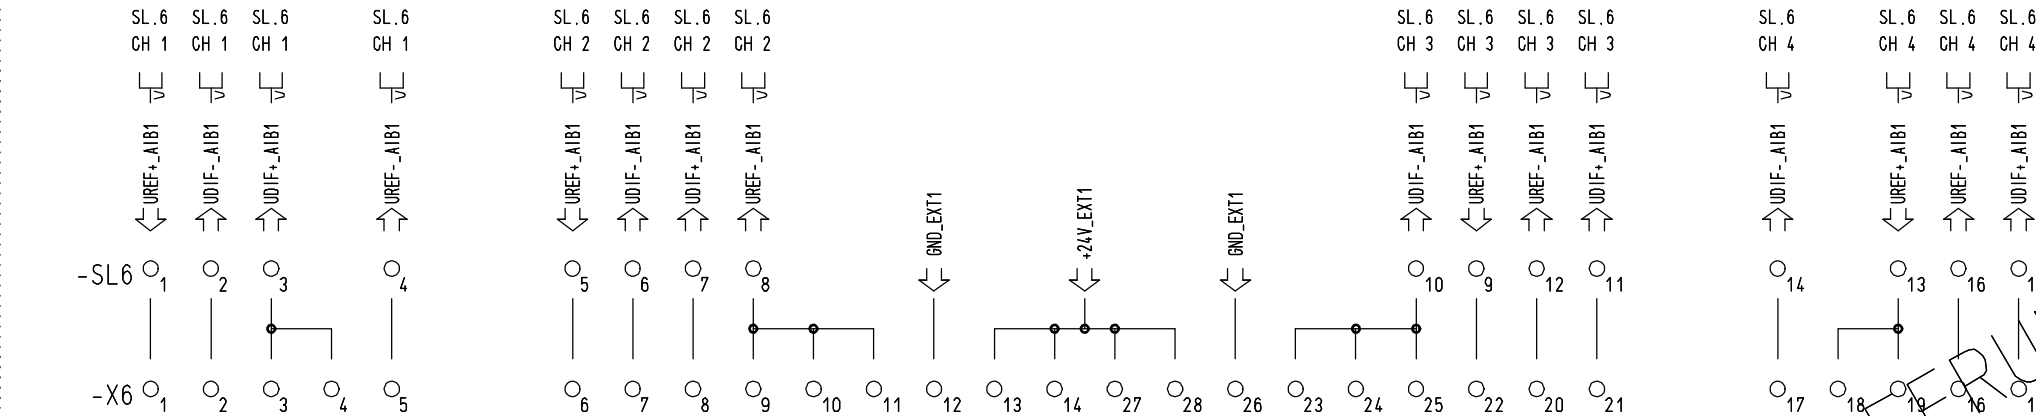

AKTUELL NICHT VERWENDET - GÜLTIGKEIT LIEFERUMFANGABHÄNGIG
CURRENTLY NOT USED - VALIDITY DEPENDING ON SCOPE OF SUPPLY

Keine Änderung ohne Zustimmung der
federführenden Konstruktion.
Any alterations are subject to the
approval of the design department.

© MTU Friedrichshafen GmbH
Schutzvermerk DIN 34 beachten!
Refer to protection notice DIN 34!

					CAD	Datum	Name
					Bearb.	05.03.2018	SAUTER
					Gepr.	05.03.2018	BOLL
					Norm.	05.03.2018	SAUTER
b	Verkabelung geändert	Freigegeb	07.03.2018	Boll	Abt. TEA		
Buchst.	Änderung / Revision	Auftrags-Nr.	Datum/Date	Name			




MTU Friedrichshafen GmbH

Benennung/Title
SCHEMA VERKABELUNG
ANTRIEBSSTEUERUNG
WIRING DIAGRAM
PROPULSION CONTROL

PMU: STECKER -X6, STECKPLATZ 6 (AIB1)	
PMU: PLUG -X6, SLOT 6 (AIB1)	
Auftrag/Projekt BLUE-VIS	Zeichnungs-Nr. BZ00E50200068
Referenz-Nr./Reference-No.	Blatt Sheet 18

ANSTEUERUNG
STELLGLIEDER, VENTILE
CONTROL OF
ACTUATORS, VALVES

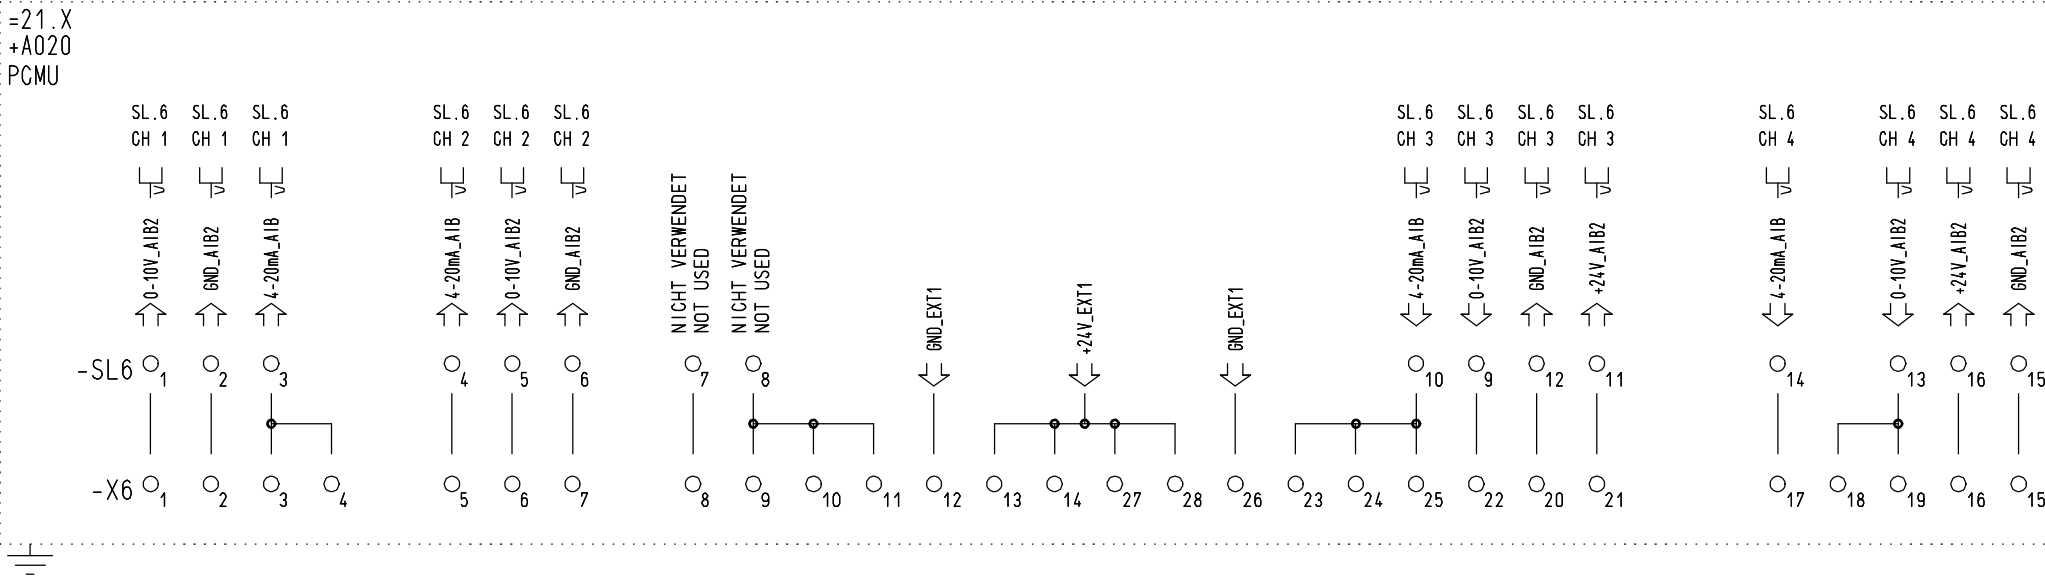

Keine Änderung ohne Zustimmung der
federführenden Konstruktion.
Any alterations are subject to the
approval of the design department.

© MTU Friedrichshafen GmbH
Schutzvermerk DIN 34 beachten !
Refer to protection notice DIN 34 !

						CAD	Datum	Name
						Bearb.	05.03.2018	SAUTER
						Gepr.	05.03.2018	BOLL
						Norm.	05.03.2018	SAUTER
b	Verkabelung geändert	Freigegeb	07.03.2018	Boll		Abt. TEA		
Buchst.	Aenderung / Revision	Auftrags-Nr.	Datum/Date	Name				



Benennung/Title
SCHEMA VERKABELUNG
ANTRIEBSSTEUERUNG
WIRING DIAGRAM
PROPULSION CONTROL

PMU: STECKER -X6, STECKPLATZ 6 (AIB2)			
PMU: PLUG -X6, SLOT 6 (AIB2)			
Auftrag/ Projekt	BLUE-VIS	Zeichnungs-Nr. Drawing No.	BZ00E50200068
Referenz-Nr./Reference-No.		-----	
		Blatt Sheet	19

=21.X
+A020
PCMU

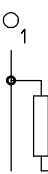
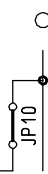
SL.2 CH 1	SL.2 CH 1	SL.2 CH 1	SL.2 CH 1
			
↓ UREF+_AIB1	↑ UDF+_AIB1	↑ UDF+_AIB1	↑ UREF+_AIB1
			

Diagram showing pins 13, 15, 14, and 16. Above the pins are labels: SL 2 CH 4, SL 2 CH 4, SL 2 CH 4, and SL 2 CH 4. Below the pins are labels: UREF_AIB1, UDF_AIB1, UDF_AIB1, and UREF_AIB1. To the right of the pins is a label: PCU_24V. To the far right is a label: END EXT2.

☒ BINÄRSIGNAL
☐ BINARY SIGNAL

ANALOG SIGNAL
ANALOG SIGNAL

1 (4-20mA)

[illegible]

keine Änderung ohne Zustimmung der
eroderführenden Konstruktion.
any alterations are subject to the
approval of the design department.

© MTU Friedrichshafen GmbH
Schutzvermerk DIN 34 beachten !
Refer to protection notice DIN 34 !

					CAD	Datum	Name
					Bearb.	05.03.2018	SAUTER
					Gepr.	05.03.2018	BOLL
b	Verkabelung geändert	Freigegeb	07.03.2018	Boll	Norm.	05.03.2018	SAUTER
Buchst.	Änderung / Revision	Auftrags-Nr.	Datum/Date	Name	Abt.	TEA	



MTU Friedrichshafen GmbH

	Benennung/Title
H	SCHEMA VERKABELUNG ANTRIEBSSTEUERUNG WIRING DIAGRAM PROPULSION CONTROL

PCU: STECKER -X8, STECKPLATZ 2 (AIB1)
PCU: PLUG -X8, SLOT 2 (AIB1)

Auftrag/ Projekt	BLUE-VIS	Zeichnungs-Nr. Drawing No.	BZ00E50200068
---------------------	----------	-------------------------------	---------------

Blatt	20
Sheet	

RUPLAN

1

2

—

L

5


3

DIN A3

Keine Änderung ohne Zustimmung der
federführenden Konstruktion.
Any alterations are subject to the
approval of the design department.

© MTU Friedrichshafen GmbH
Schutzvermerk DIN 34 beachten !
Refer to protection notice DIN 34 !

013R001F

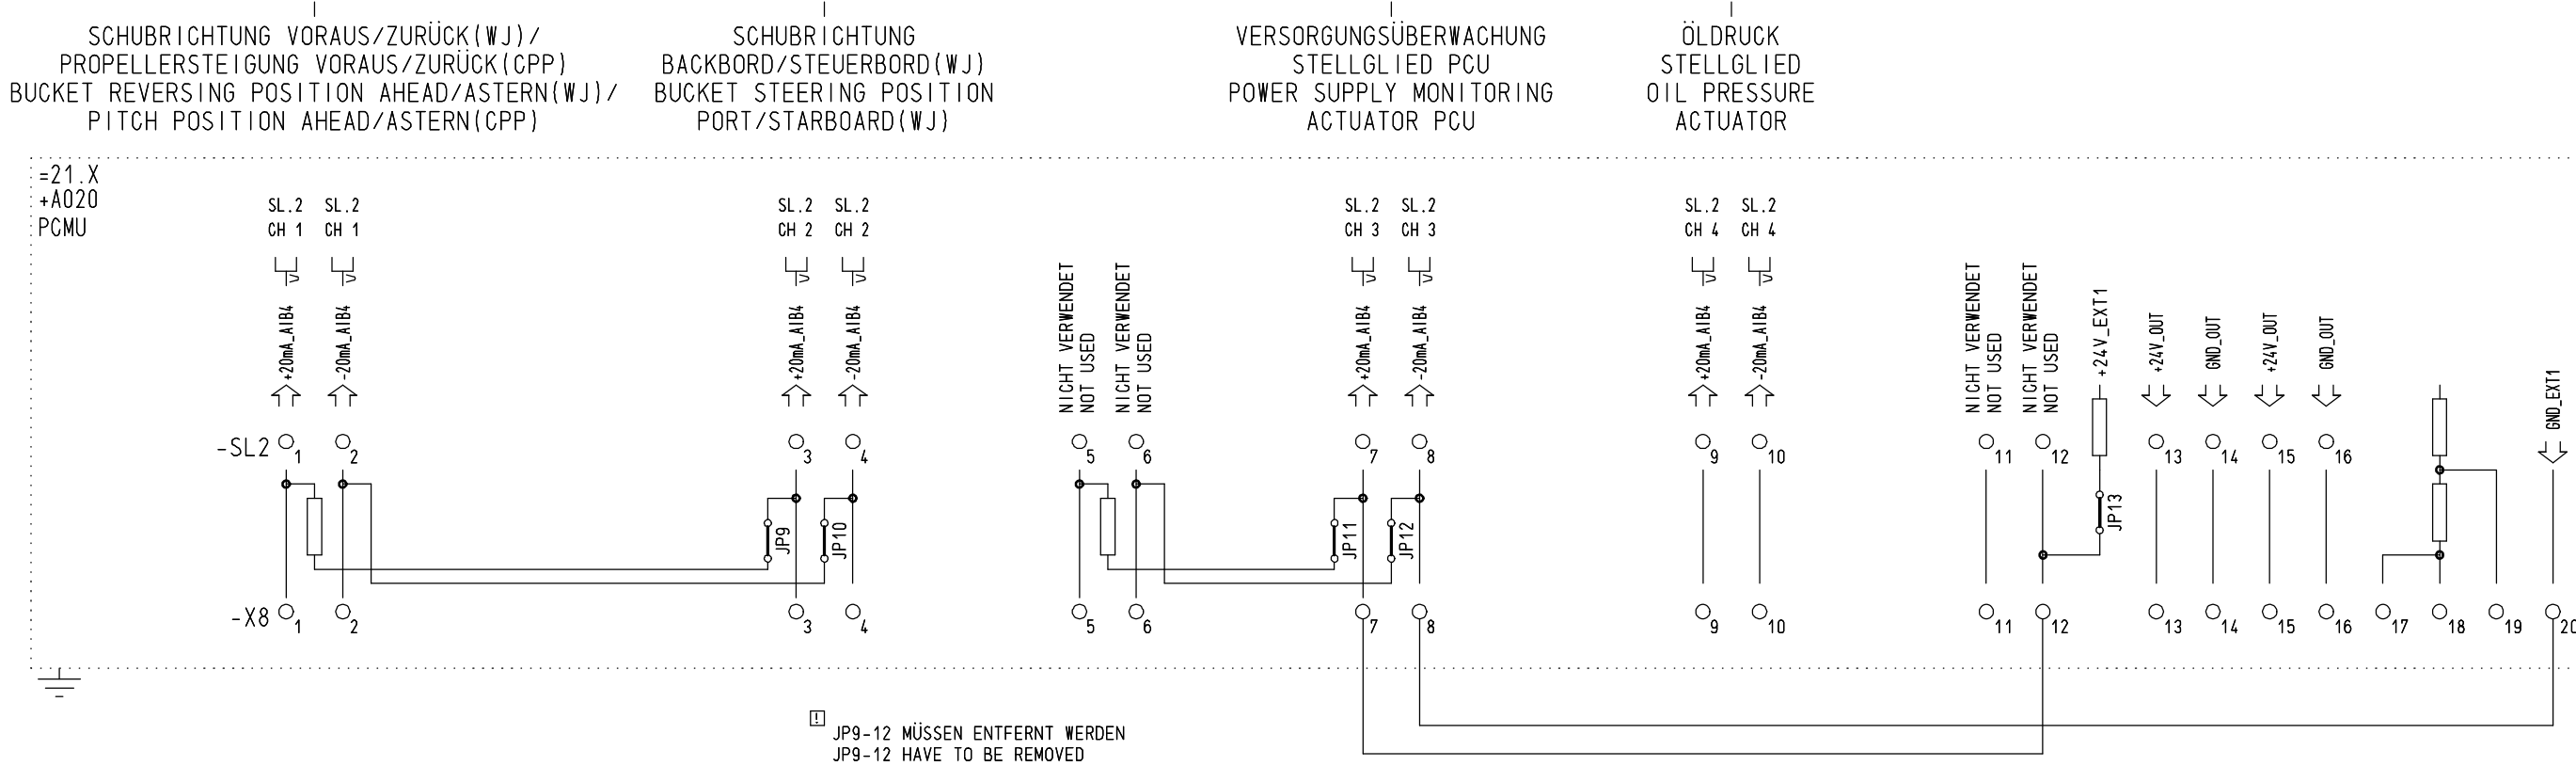

					CAD	Datum	Name
					Bearb.	05.03.2018	SAUTER
					Gepr.	05.03.2018	BOLL
					Norm.	05.03.2018	SAUTER
b	Verkabelung geändert	Freigegeb	07.03.2018	Boll	Abt. TEA		
Buchst.	Änderung / Revision	Auftrags-Nr.	Datum/Date	Name			





Benennung/Title
SCHEMA VERKABELUNG
ANTRIEBSSTEUERUNG
WIRING DIAGRAM
PROPULSION CONTROL

PCU: STECKER -X8, STECKPLATZ 2 (AIB4)	
PCU: PLUG -X8, SLOT 2 (AIB4)	
Auftrag/Projekt BLUE-VIS	Zeichnungs-Nr. Drawing No. BZ00E50200068
Referenz-Nr./Reference-No.	-----
	Blatt Sheet 21


Keine Änderung ohne Zustimmung der
federführenden Konstruktion.
Any alterations are subject to the
approval of the design department.

© MTU Friedrichshafen GmbH
Schutzvermerk DIN 34 beachten !
Refer to protection notice DIN 34 !

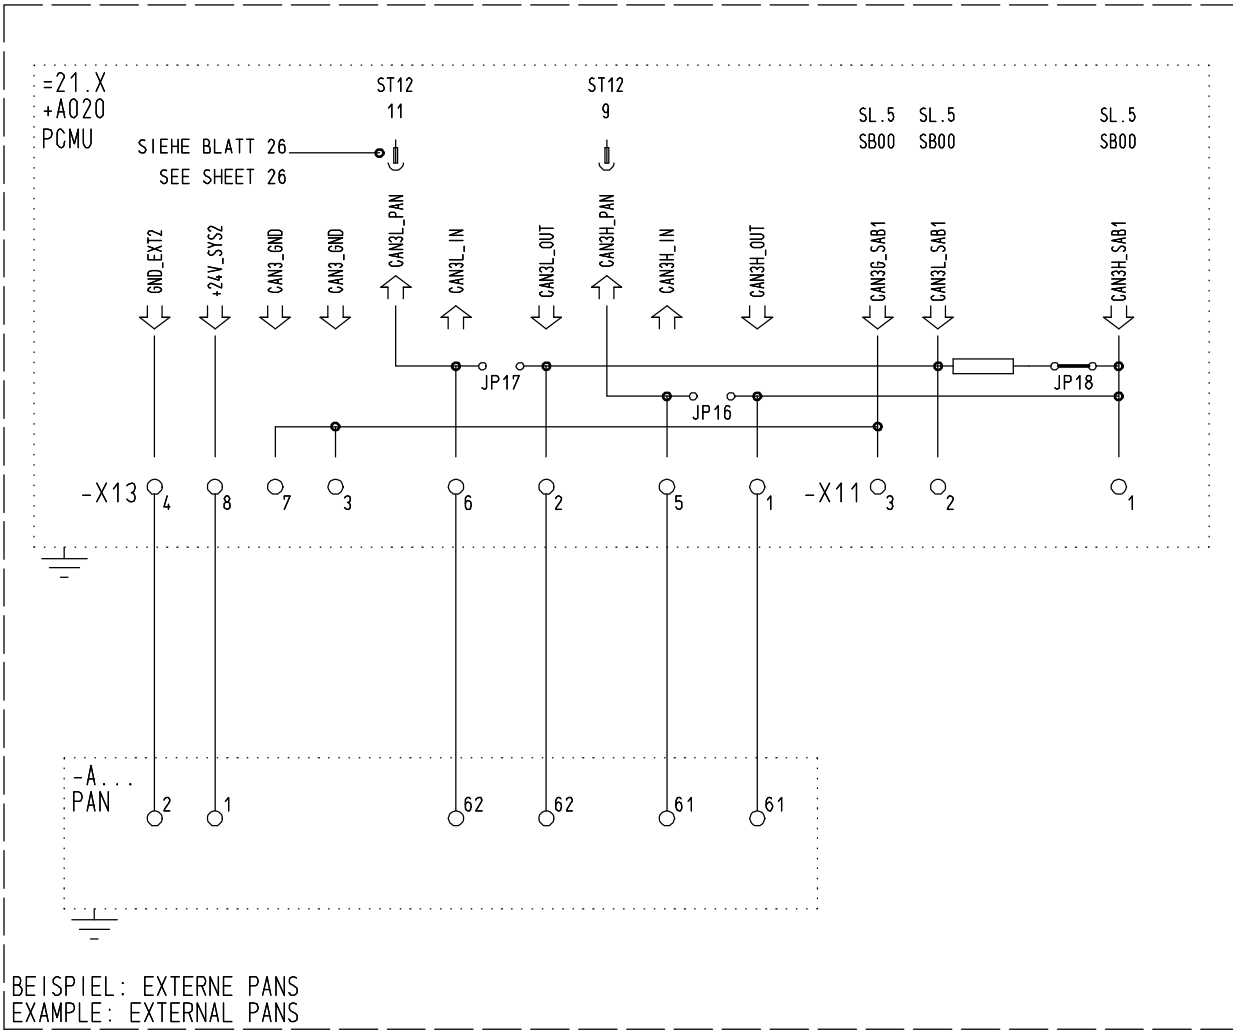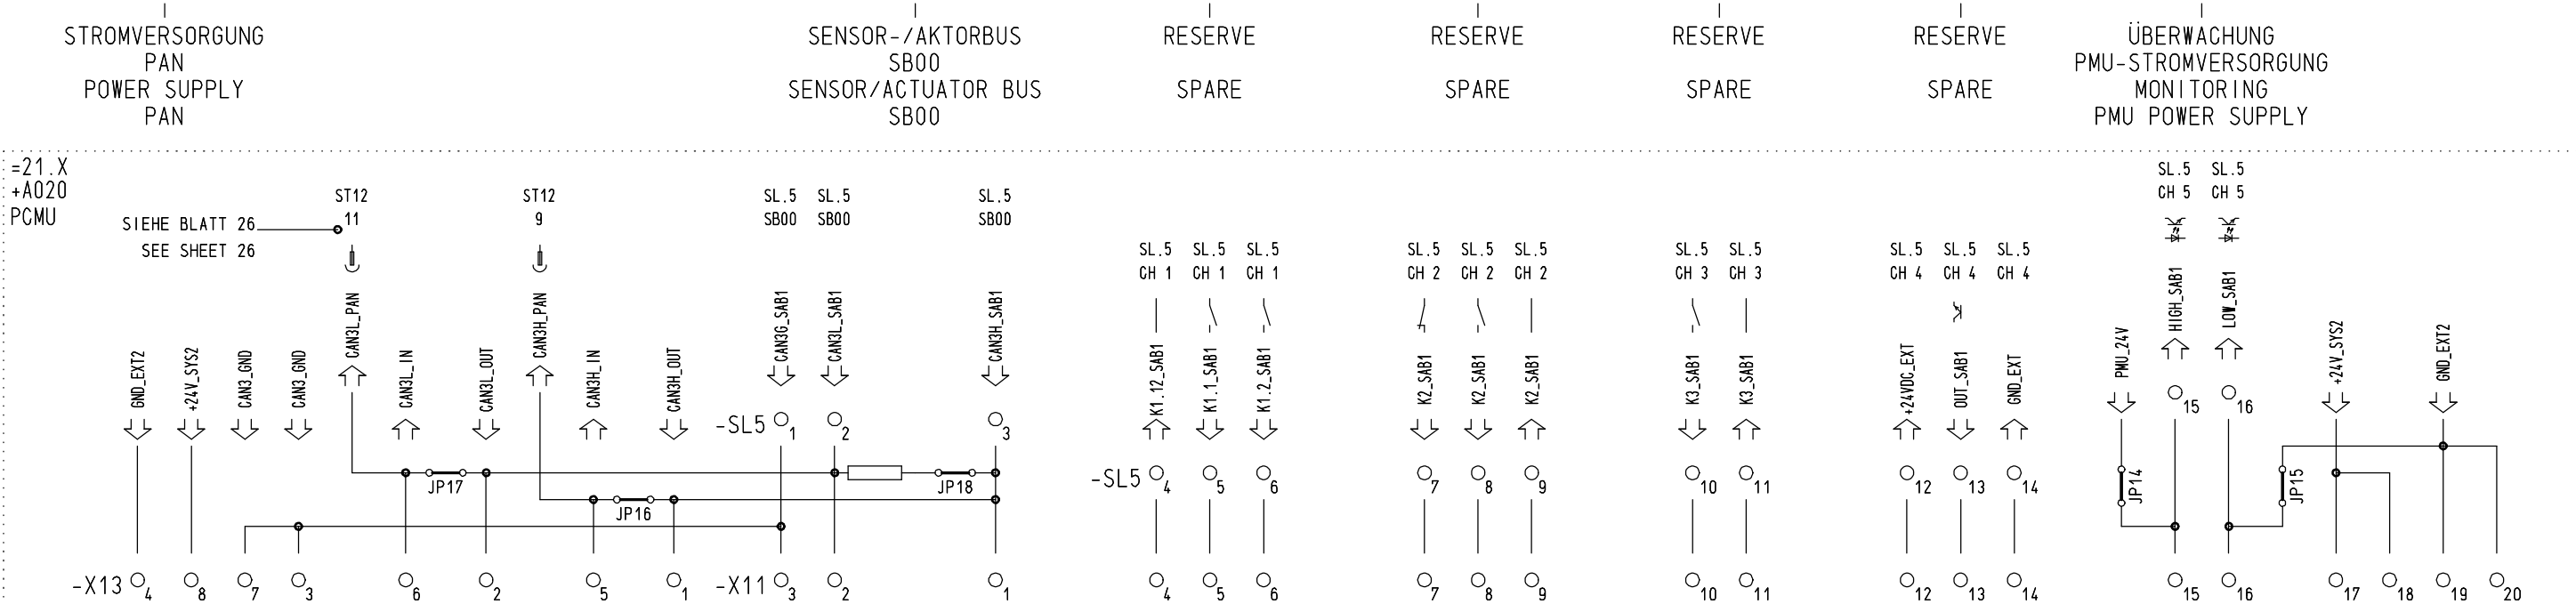

					CAD	Datum	Name	 MTU Friedrichshafen GmbH	Benennung/Title SCHEMA VERKABELUNG ANTRIEBSSTEUERUNG WIRING DIAGRAM PROPULSION CONTROL	PCU: STECKER -X11, STECKPLATZ 5 (SAB1)			
					Bearb.	05.03.2018	SAUTER			PCU: PLUG -X11, SLOT 5 (SAB1)			
					Gepr.	05.03.2018	BOLL						
					Norm.	05.03.2018	SAUTER						
b	Verkabelung geändert		Freigegeb	07.03.2018	Boll					Auftrag/ Projekt BLUE-VIS		Zeichnungs-Nr. Drawing No. BZ00E50200068	Blatt Sheet 24
Buchst.	Änderung / Revision		Auftrags-Nr.	Datum/Date	Name	Abt. TEA				Referenz-Nr./Reference-No.		-----	-----

ANSTEUERUNG
STELLGLIEDER, VENTILE
CONTROL OF
ACTUATORS, VALVES

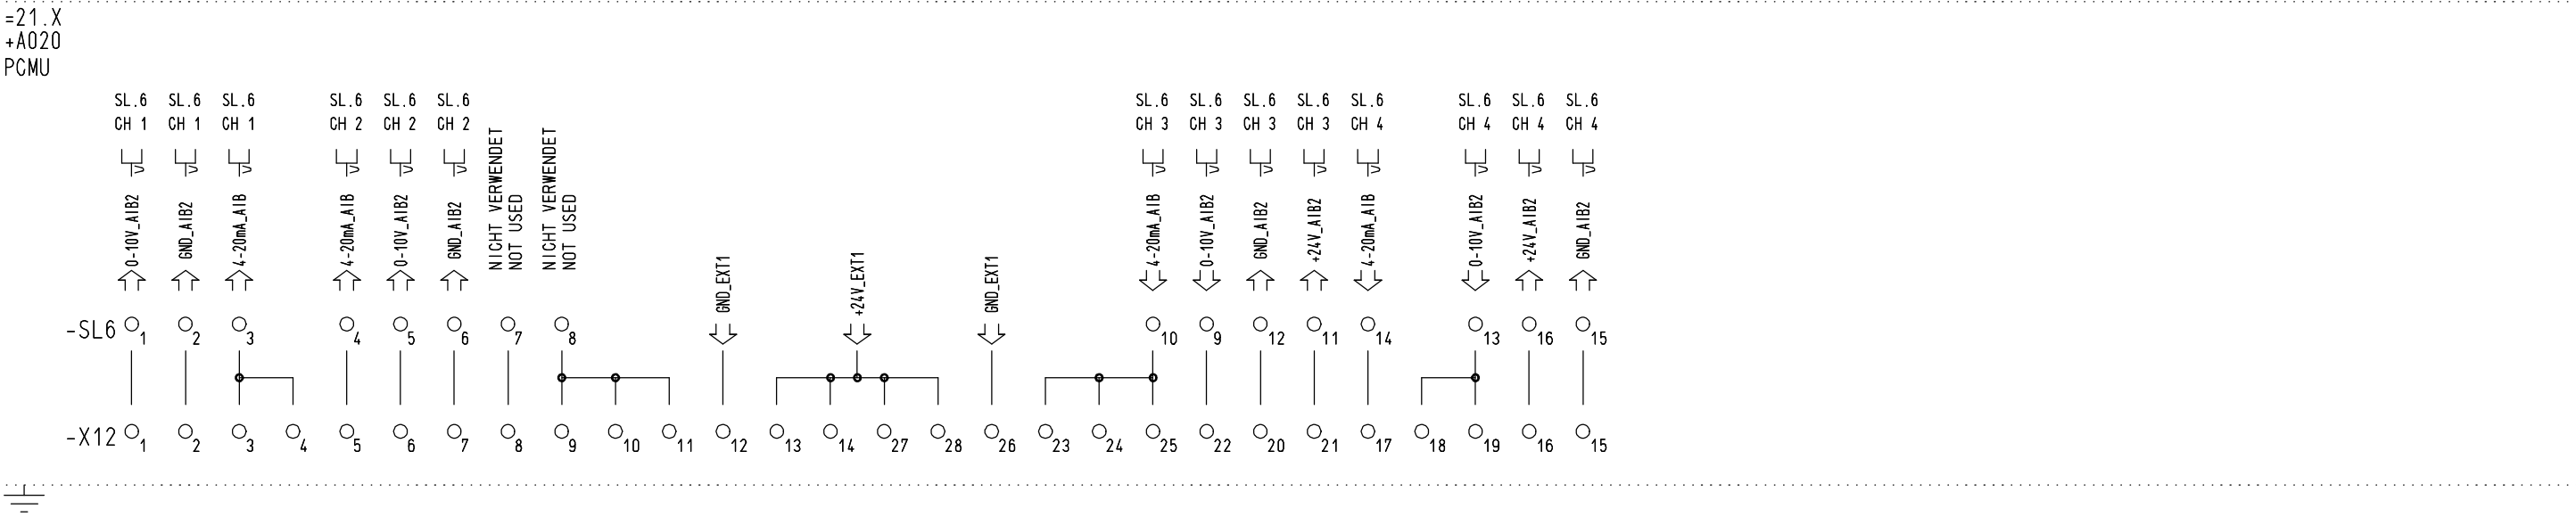

Keine Änderung ohne Zustimmung der
federführenden Konstruktion.
Any alterations are subject to the
approval of the design department.

© MTU Friedrichshafen GmbH
Schutzvermerk DIN 34 beachten !
Refer to protection notice DIN 34 !

					CAD	Datum	Name
					Bearb.	05.03.2018	SAUTER
					Gepr.	05.03.2018	BOLL
					Norm.	05.03.2018	SAUTER
b	Verkabelung geändert	Freigegeb	07.03.2018	Boll	Abt. TEA		
Buchst.	Aenderung / Revision	Auftrags-Nr.	Datum/Date	Name			



Benennung/Title
SCHEMA VERKABELUNG
ANTRIEBSSTEUERUNG
WIRING DIAGRAM
PROPULSION CONTROL

PCU: STECKER -X12, STECKPLATZ 6 (AIB2)	
PCU: PLUG -X12, SLOT 6 (AIB2)	
Auftrag/Projekt BLUE-VIS	Zeichnungs-Nr. BZ00E50200068
Referenz-Nr./Reference-No.	-----
	Blatt 25

